



Общество с ограниченной ответственностью
«Архитектурная лаборатория «АК и партнеры»
Свидетельство СРО НП «Гильдия архитекторов и проектировщиков»
от 14.02.2017 № 1096-2017-7726730507-П-3

**КАПИТАЛЬНЫЙ РЕМОНТ ГОСУДАРСТВЕННОГО БЮДЖЕТНОГО
ОБЩЕОБРАЗОВАТЕЛЬНОГО УЧРЕЖДЕНИЯ ГОРОДА МОСКВЫ
«ШКОЛА № 1282 «СОКОЛЬНИКИ»
ПО АДРЕСУ: Г. МОСКВА, УЛ. БАРБОЛИНА, Д. 1, КОРП. 1**

РЕЗУЛЬТАТЫ ИНЖЕНЕРНЫХ ИЗЫСКАНИЙ.

**Книга 1. Техническое заключение по результатам обследования строительных
конструкций и инженерных систем, обмерные чертежи по Объекту:
Капитальный ремонт Государственного бюджетного общеобразовательного учреждения
города Москвы «Школа № 1282 «Сокольники»
по адресу: г. Москва, ул. Барболина, д.1, корп. 1**

696/П-24-АНО/ТЗК
Часть 2 из 3

Изм.	№ док.	Подп.	Дата

Подрядчик

ООО «АрхЛАБ «АК и партнеры»

**Москва 2024
Шифр 24-108**



Общество с ограниченной ответственностью
«Архитектурная лаборатория «АК и партнеры»
Свидетельство СРО НП «Гильдия архитекторов и проектировщиков»
от 14.02.2017 № 1096-2017-7726730507-П-3

КАПИТАЛЬНЫЙ РЕМОНТ ГОСУДАРСТВЕННОГО БЮДЖЕТНОГО
ОБЩЕОБРАЗОВАТЕЛЬНОГО УЧРЕЖДЕНИЯ ГОРОДА МОСКВЫ
«ШКОЛА № 1282 «СОКОЛЬНИКИ»
ПО АДРЕСУ: Г. МОСКВА, УЛ. БАРБОЛИНА, Д. 1, КОРП. 1

РЕЗУЛЬТАТЫ ИНЖЕНЕРНЫХ ИЗЫСКАНИЙ.

Книга 1. Техническое заключение по результатам обследования строительных
конструкций и инженерных систем, обмерные чертежи по Объекту:
Капитальный ремонт Государственного бюджетного общеобразовательного учреждения
города Москвы «Школа № 1282 «Сокольники»
по адресу: г. Москва, ул. Барболина, д.1, корп. 1

696/П-24-АНО/ТЗК

Часть 2 из 3

Генеральный директор
ООО «АрхЛАБ «АК и партнеры»

Главный инженер проекта



Жукова Т.В.

Мелихов А.И.

Москва 2024

Шифр 24-108

Свидетельство Ассоциация СРО «ЦЕНТРСТРОЙПРОЕКТ» от 01.03.2024 № СРО-П-029-25092009
Свидетельство СРО АС «ИНЖГЕОТЕХ» от 28.05.2024 № СРО-И-012-24122009

Заказчик: ООО «Архитектурная
лаборатория «АК и партнеры»
Договор: АК-6/24-(24-108)-суб1 от 22.08.2024 г.

**Капитальный ремонт Государственного бюджетного
общеобразовательного учреждения города Москвы
«Школа № 1282 «Сокольники»
по адресу: г. Москва, ул. Барболина, д. 1, корп. 1**

Результаты инженерных изысканий.

**Книга 1. Техническое заключение по результатам обследования
строительных конструкций и инженерных систем,
обмерные чертежи по Объекту:
Капитальный ремонт Государственного бюджетного
общеобразовательного учреждения города Москвы
«Школа № 1282 «Сокольники»
по адресу: г. Москва, ул. Барболина, д. 1, корп.1**

696/П-24-АНО/ТЗК

Часть 2 из 3

Изм.	№ док.	Подп.	Дата

Москва 2024



Свидетельство Ассоциация СРО «ЦЕНТРСТРОЙПРОЕКТ» от 01.03.2024 № СРО-П-029-25092009
Свидетельство СРО АС «ИНЖГЕОТЕХ» от 28.05.2024 № СРО-И-012-24122009

Заказчик: ООО «Архитектурная
лаборатория «АК и партнеры»
Договор: АК-6/24-(24-108)-суб1 от 22.08.2024 г.

**Капитальный ремонт Государственного бюджетного
общеобразовательного учреждения города Москвы
«Школа № 1282 «Сокольники»
по адресу: г. Москва, ул. Барболина, д. 1, корп. 1**

Результаты инженерных изысканий.

**Книга 1. Техническое заключение по результатам обследования
строительных конструкций и инженерных систем,
обмерные чертежи по Объекту:
Капитальный ремонт Государственного бюджетного
общеобразовательного учреждения города Москвы
«Школа № 1282 «Сокольники»
по адресу: г. Москва, ул. Барболина, д. 1, корп.1**

696/П-24-АНО/ТЗК

Часть 2 из 3

Исполнительный директор

Д. В. Мирошниченко

Руководитель проекта

Д. В. Мирошниченко



Москва 2024





ARCANA
— PROJECT COMPANY —

Общество с ограниченной ответственностью «АРКАНА»
ИНН 9715487170 КПП 771501001 ОГРН 1247700457366



arcana-project@yandex.ru



+7 (910) 534-33-80



www.arcana-project.ru



127410, РФ, г. Москва, вн. тер. г. Муниципальный
округ Алтуфьевский, ш. Алтуфьевское, д. 79А,
стр. 3, помещ. 21/3/2

ТЕХНИЧЕСКОЕ ЗАКЛЮЧЕНИЕ
по результатам обследования строительных конструкций и
инженерных систем, обмерные чертежи по Объекту:
Капитальный ремонт Государственного бюджетного
общеобразовательного учреждения города Москвы «Школа
№ 1282 «Сокольники» по адресу:
г. Москва, ул. Барболина, д.1, корпус 1.

696/П-24-АНО/ТЗК

Часть 2 из 3


Москва 2024 г.

ТЕХНИЧЕСКОЕ ЗАКЛЮЧЕНИЕ
по результатам обследования строительных конструкций и
инженерных систем, обмерные чертежи по Объекту:
Капитальный ремонт Государственного бюджетного
общеобразовательного учреждения города Москвы «Школа
№ 1282 «Сокольники» по адресу:
г. Москва, ул. Барболина, д.1, корпус 1.

696/П-24-АНО/ТЗК

УТВЕРЖДАЮ

Генеральный директор

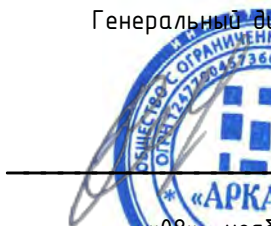

/Е.Ю. Степанова
«08» ноября 2024 г.



Москва 2024 г.

Ведомость чертежей		
Лист	Наименование	Примечание
1	Ведомость чертежей	
2	План подвала	
3	План 1-го этажа	
4	План 2-го этажа	
5	План 3-го этажа	
6	План 4-го этажа	
7	План чердачного пространства	
8	План кровли	
9	Фасады в осях 1-12 и Ж-А*	
10	Фасады в осях Ж-А по оси 10 и Г-Ж по оси 6	
11	Фасады в осях 12-1 и А*-Ж	
12	Фасады в осях Г-Ж по оси 7 и А-Ж по оси 3	
13	План перекрытия подвала	
14	План перекрытия 1-го этажа	
15	План перекрытия 2-го этажа	
16	План перекрытия 3-го этажа	
17	План перекрытия 4-го этажа	
18	План балок под стойки стропильной системы	
19	Схема расположения конструкций покрытия	
20	Разрезы 1-1, 2-2 и 3-3	


Формат А4

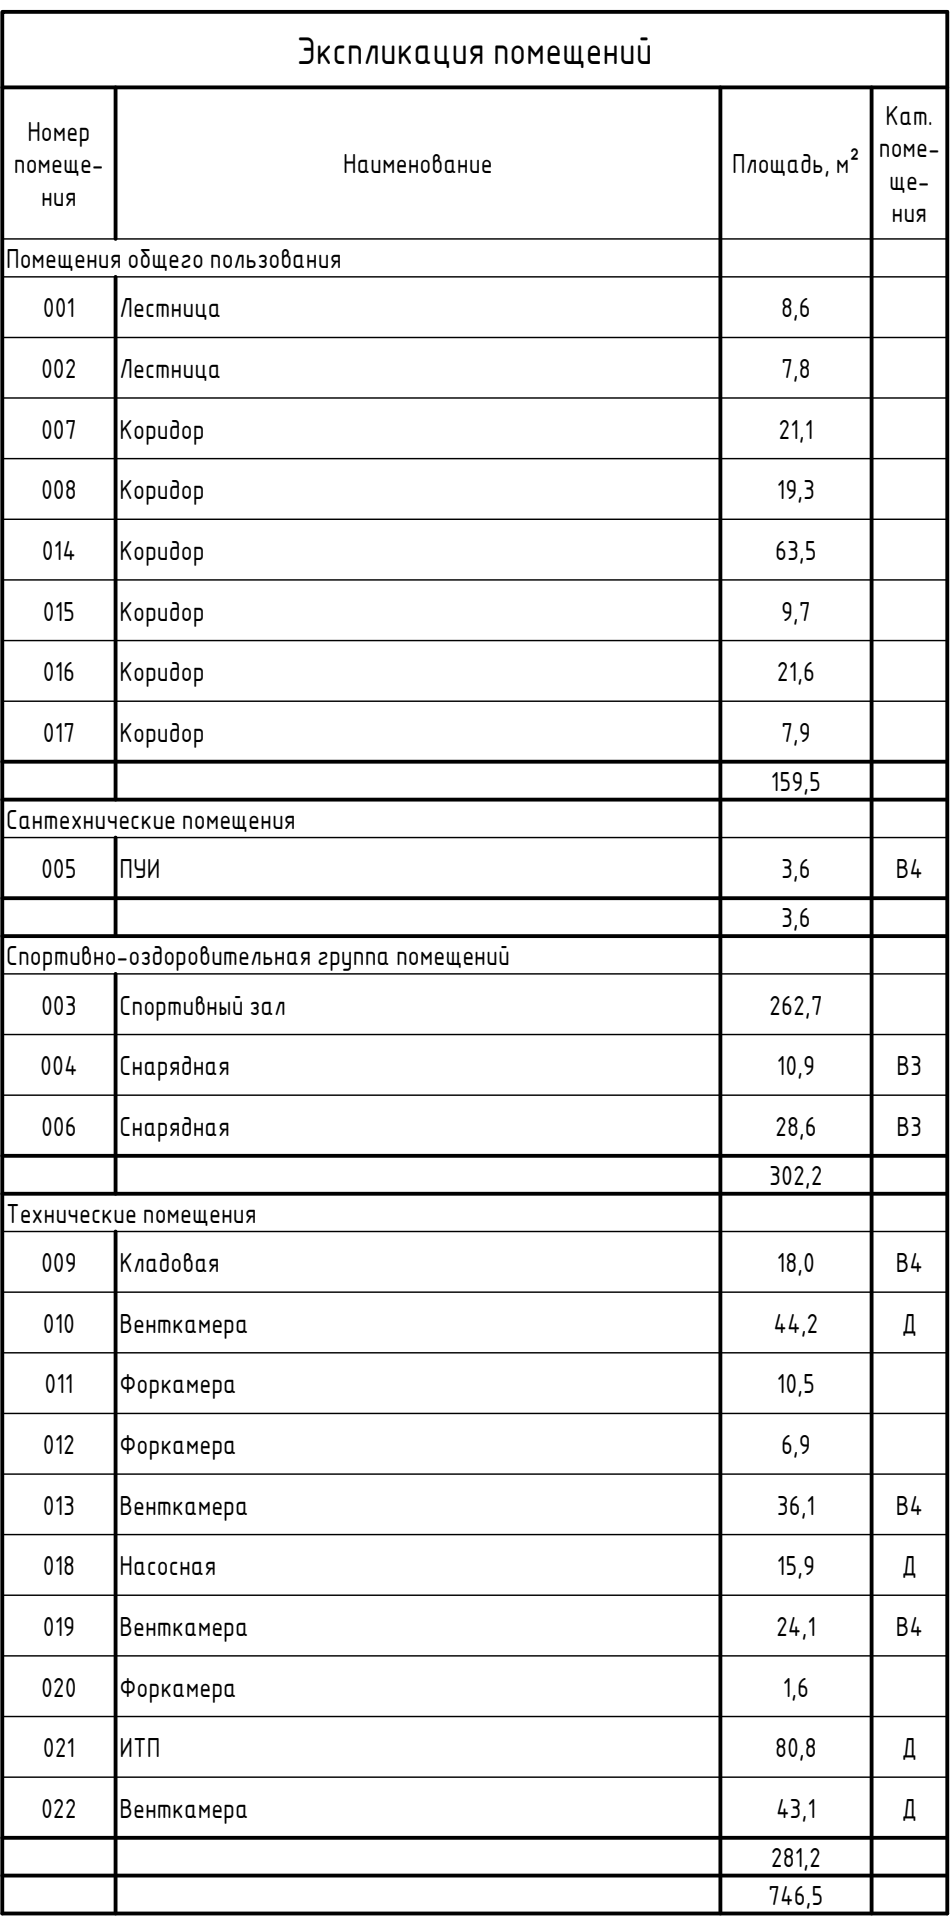[illegible]

²


Экспликация помещений 1-20 этажа				
Номер помещения	Назначение	Площадь, м²	Кат. помещения	
Административные помещения				
103	Капота охраны (с диспетчерским пунктом)	16,2		
165	Кабинет с рабочим пространством для учителей/начальника и вивача школы Тип 1	41,8		
Гардеробы				
104	Гардероб для обучающихся (основная школа)	44,2		
106	Гардероб для обучающихся (начальная школа)	53,1		
146	Гардероб для учителей	19,7		
147	Гардероб для обучающихся (начальная школа)	46,4		
		165,4		
Медицинский блок				
140	Кабинет врача	18,7		
161	Процедурный (прибыльчатый) кабинет	12,9		
162	Гигиенический кабинет с моечной для приходящих, дезинфицирующих растворов и хранения дезинфицирующего вентилатора, предназначенных для помещений детского назначения	6,1		Б4
163	Кабинет медсестры	3,4		
		41,1		
Основная школа: Учебные кабинеты				
111	Учебный кабинет (математика)	53,3		
		53,3		
Пешеходы				
129	Учебный зал	10,2		
130	Общественный зал	104,7		
131	Мечеть для студентов посуды	16,9		
132	Коридор	22,7		
133	Кладовая и мечеть аварийной поры	40,0		
134	Защитный щит	6,6		
135	Кладовая сухих продуктов	3,7		
136	Помещение персонала с санузлом	6,5		
137	Помещение для временного хранения пешеходов	3,8		
138	ПМ	4,5		Б4
139	Помещение подсобного Ввод в эксплуатацию с участием мусорной посуды	29,3		Б4
148	Танк	2,2		
		214,9		

Формат	A0
--------	----

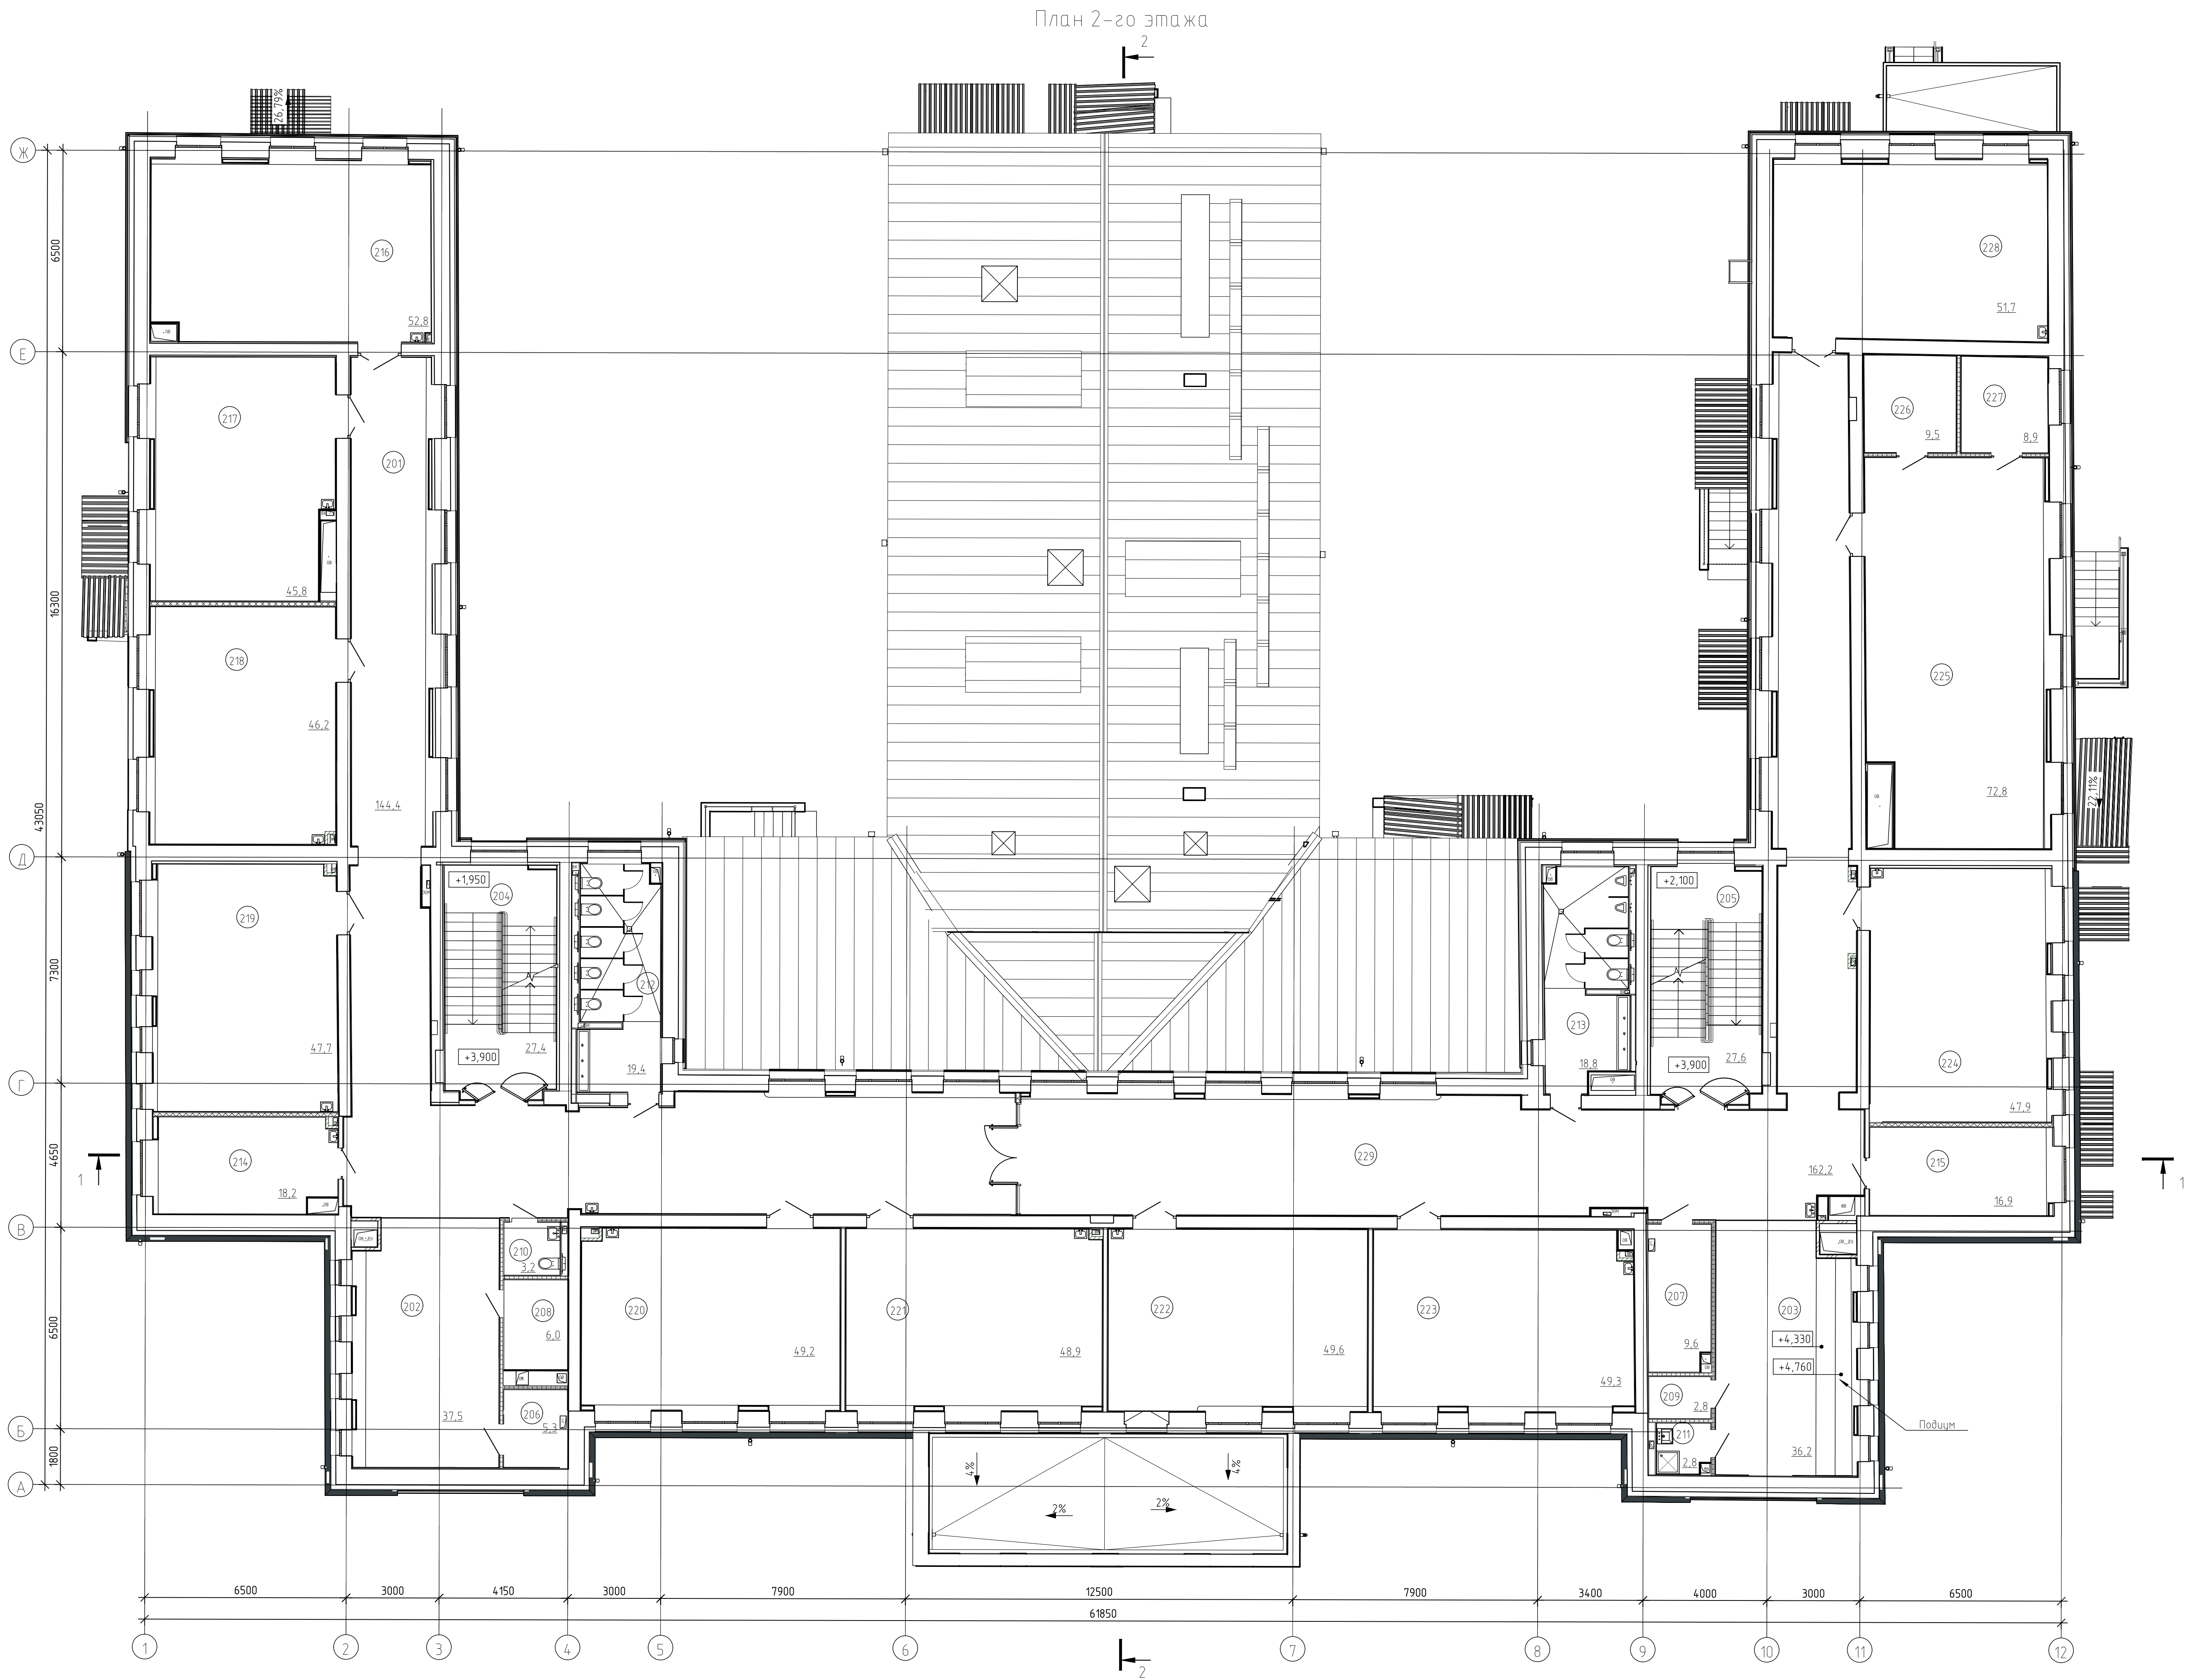

Экспликация помещений 2-го этажа			
Номер помеще-ния	Наименование	Площадь, м²	Кол. помеще-ния
Административные помещения			
214	Кабинет для индивидуальных занятий, в т.ч. учитель-логопед	18,2	
215	Административный кабинет (начальная школа) Тип 1	16,9	
		35,1	
Начальная школа. Учебные кабинеты			
216	Учебный кабинет (1 класс)	52,8	
217	Учебный кабинет (1 класс)	45,8	
218	Учебный кабинет (1 класс)	46,2	
219	Учебный кабинет (1 класс)	47,7	
220	Учебный кабинет (2-4 классы)	49,2	
221	Учебный кабинет (2-4 классы)	48,9	
222	Учебный кабинет (2-4 классы)	49,6	
223	Учебный кабинет (2-4 классы)	49,3	
224	Учебный кабинет (2-4 классы)	47,9	
228	Учебный кабинет (2-4 классы)	51,7	
		489,1	
Помещения общего пользования			
201	Коридор	14,4	
202	Рекреация	37,5	
203	Рекреация	36,2	
204	Лестничная клетка (Тип П)	27,4	
205	Лестничная клетка (Тип П)	27,6	
229	Коридор	162,2	
		435,2	
Специальные помещения			
210	Туалет для персонала	3,2	
211	ПВ	2,8	
212	Зеркала для девочек (начальная школа)	19,4	
213	Зеркала для мальчиков (начальная школа)	18,8	
		44,2	
Спортивно-оздоровительная группа помещений			
225	Гимнастический зал	72,8	
226	Раздевальня Тип 1	9,5	
227	Раздевальня Тип 1	8,9	
		91,3	
Технические помещения			
206	Помещение СС	5,3	В4
207	Помещение СС	9,6	В4
208	Подсобное помещение	6,1	
209	Подсобное помещение	2,8	В4
		23,7	
		118,5	


План 3-го этажа

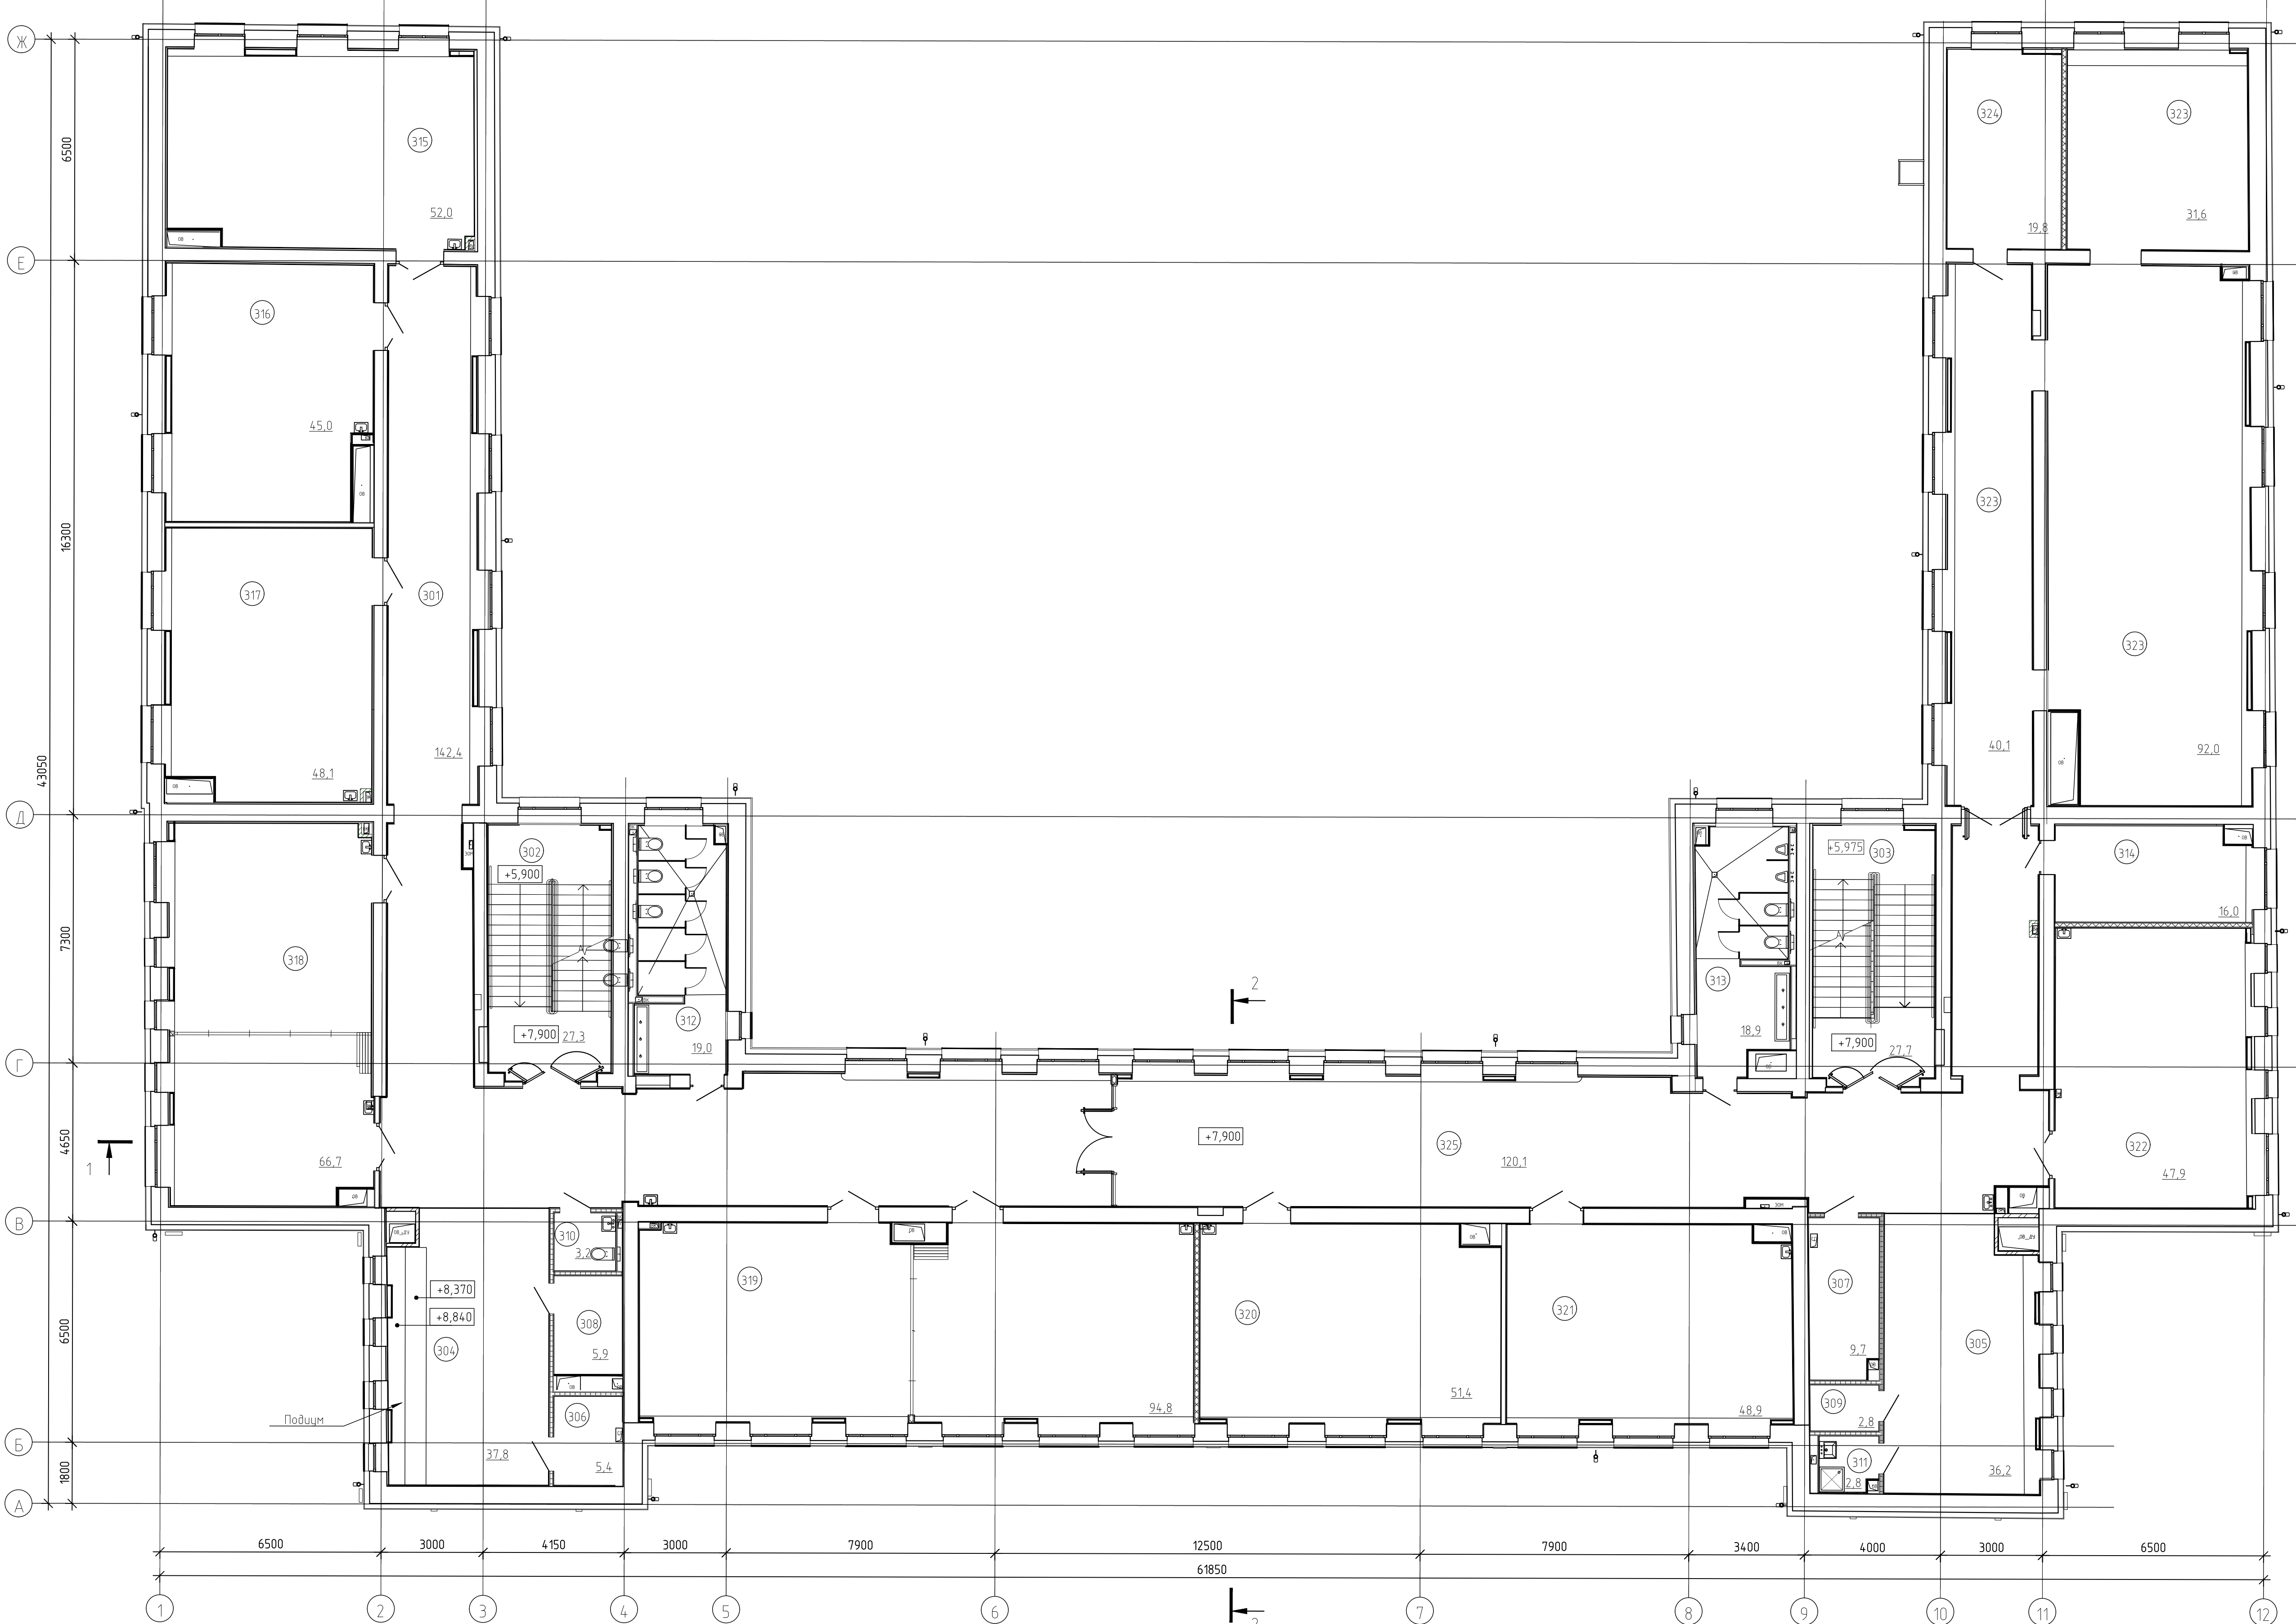

Экспликация помещений 3-го этажа				
Номер помещения	Наименование	Площадь, м²	Кат. помещений	
Административные помещения				
314	Кабинет для индивидуальных занятий, 6 в аккорсионном педагогом	16,0		
		16,0		
Выполнение учебной				
323	Многофункциональный информационный компьютерный центр с занятием для индивидуальных и групповых занятий, методичка, 163,7	163,7		
324	Многофункциональный информационный компьютерный центр с занятием для индивидуальных и групповых занятий, методичка, 19,8	19,8	83	
	Хранение (эксперимент) фонды в учебной книге	19,8		
		19,8		
Начальная школа. Учебные кабинеты				
315	Учебный кабинет (2-4 классы)	52,0		
316	Учебный кабинет (2-4 классы)	45,0		
317	Учебный кабинет (2-4 классы)	44,8		
318	Кабинет иностранного языка с возможностью автоматизированной переводной на два помещения (начальная школа)	66,1		
320	Учебный кабинет (2-4 классы)	51,4		
321	Учебный кабинет (2-4 классы)	48,9		
322	Учебный кабинет (2-4 классы)	47,9		
		360,0		
Помещения общего пользования				
301	Коридор	162,4		
302	Лестничная клетка (Тип А0)	24,3		
303	Лестничная клетка (Тип А0)	27,7		
304	Рекреация	37,8		
305	Рекреация	36,2		
325	Коридор	120,2		
		391,6		
Санитарно-технические помещения				
300	Туалет для персонала	3,2		
311	ПМ	2,0		
312	Уборная для девочек (начальная школа)	19,8		
313	Уборная для мальчиков (начальная школа)	18,9		
		43,8		
Технические помещения				
306	Помещение СС	5,9	84	
307	Помещение СС	9,7	84	
308	Подсобное помещение	5,7		
309	Подсобное помещение	2,8	84	
		23,8		
Информационная служба				
319	Творческая мастерская с возможностью автоматизированной переводной на два помещения	96,8		
		117,6		

696П-24-АНОУТЭК					
"Капитальный ремонт Государственного бюджетного образовательного учреждения города Москвы "Школа №1282 (составная) по адресу: г. Москва, ул. Бабьинский, д.1 корпус 1"					
Изм.	Кол-во	Листы	№ док.	Прин.	Дата
Р.1240	1	Соборный	1	12.24	12.24
Содержит	1	Соборный	1	12.24	12.24
Гл.т.	1	Соборный	1	12.24	12.24
Учредитель	1	Соборный	1	12.24	12.24
И.контр.	1	Соборный	1	12.24	12.24
Комплекс чертежей по результатам обследования помещений, сооружений, методов и средств выполнения работ по капитальному ремонту					
Планы 3-го этажа					
М 1:100					
000 "Арктика"					


План 4-го этажа

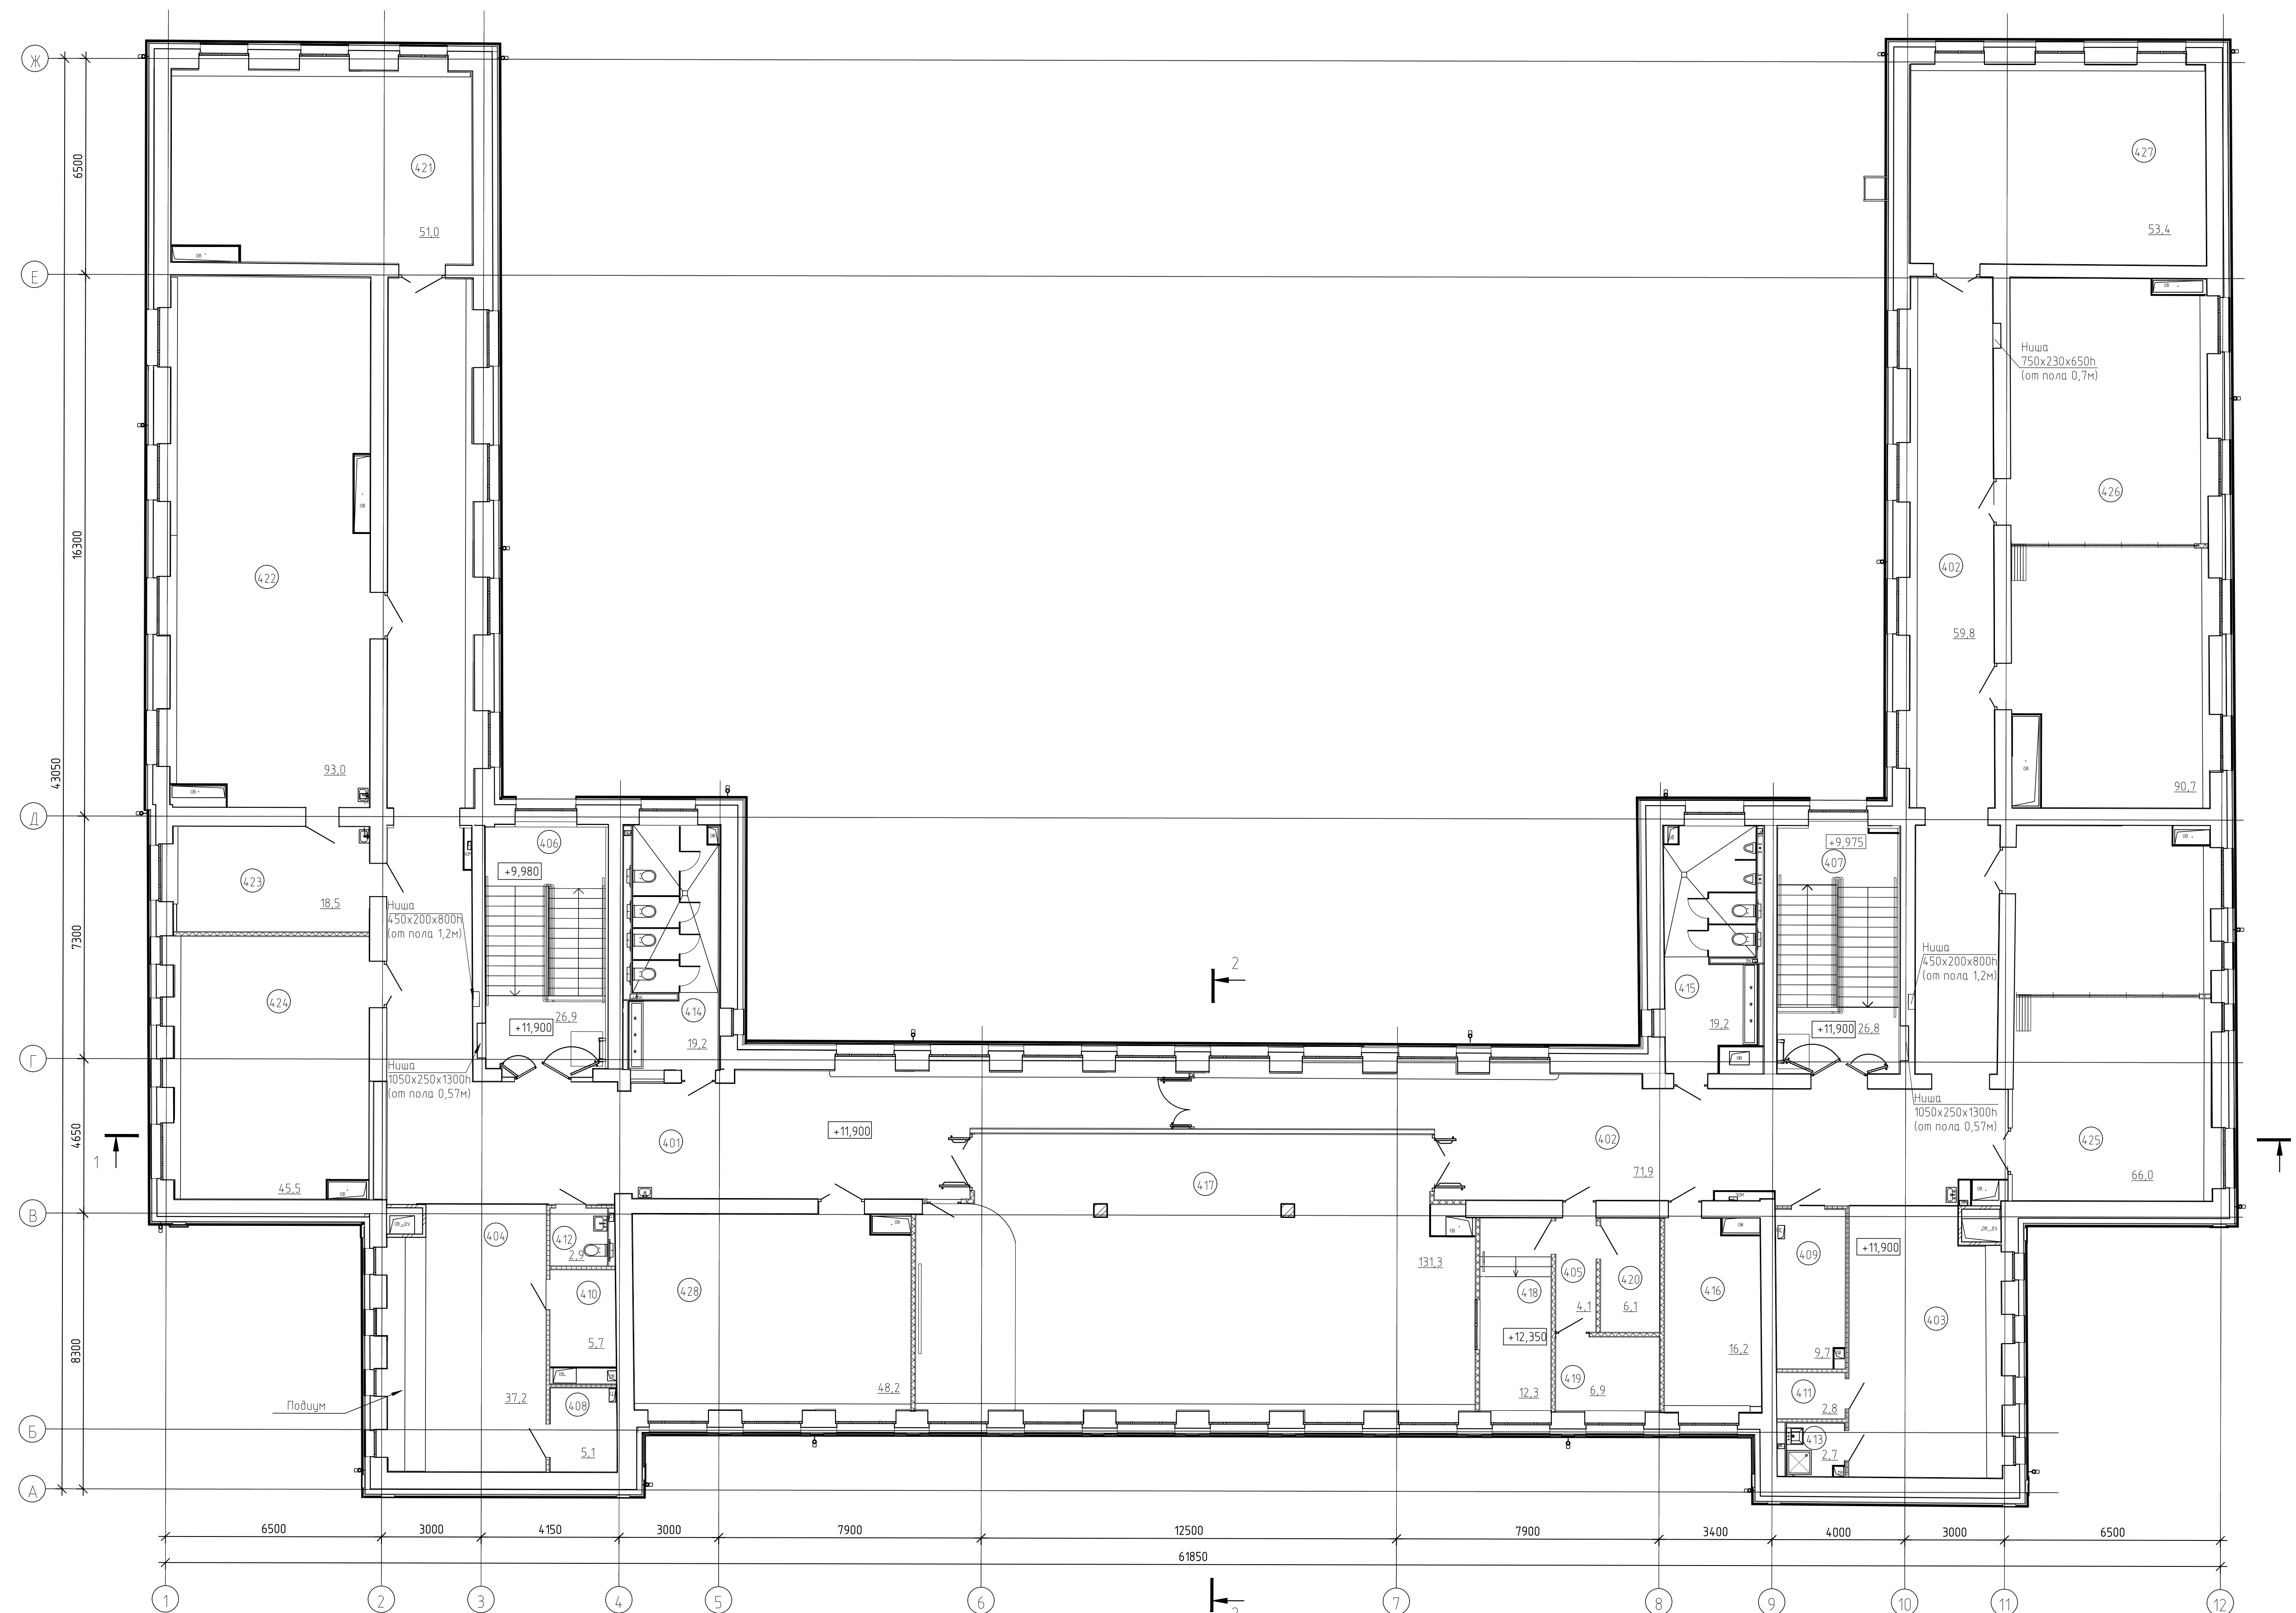

Экспликация помещений 4–20 этажа			
Номер помещения	Наименование	Площадь, кв. м	Кол-во помещений
Административные помещения			
416	Кабинет для индивидуальных занятий, в п.ч. (разговор-приемная)	16,2	
		16,2	
Зрительный зал			
417	Многофункциональное пространство с речевым/аудиторским залом (с эстрадой и драффе пола)	131,3	
418	Технический центр	12,4	
419	Артистическая	6,9	
420	Кладовая инвентаря	6,1	
		156,6	
Основной корпус. Учебные кабинеты			
421	Кабинет математики	51,0	
422	Учебный кабинет (для изучения естественных наук) (география Тун 2)	93,0	
423	Лабораторная физики	18,5	
424	Учебный кабинет (аудитория)	45,5	
425	Кабинет интерактивного языка с возможностью аудиовизуально-формированной переводческой на оба помещения	56,0	
426	Учебный кабинет информатики с возможностью аудиовизуально-формированной переводческой на оба помещения	90,8	
427	Кабинет русского языка и литературы	53,4	
428	Кабинет русского языка и литературы	48,2	
		466,3	
Помещения общего пользования			
401	Коридор	17,0	
402	Коридор	131,8	
403	Рекреация	35,9	
404	Рекреация	37,2	
405	Коридор	4,1	
406	Лестничная клетка (Тун III)	26,9	
407	Лестничная клетка (Тун III)	26,9	
		399,7	
Специализированные помещения			
412	Туалет для персонала	2,9	
413	Пти	2,7	
414	Уборная для девочек (основная школа)	19,2	
415	Уборная для мальчиков (основная школа)	19,2	
		44,4	
Технические помещения			
408	Помещение СС	5,1	
409	Помещение СС	9,7	
410	Подсобное помещение	5,7	
411	Подсобное помещение	8,8	
		29,3	
		106,1	

[illegible]

2

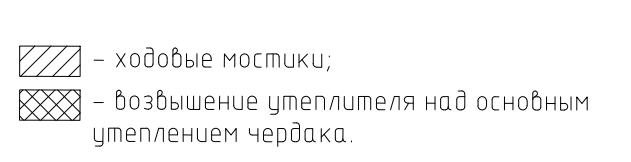[illegible]

Фасад в осях 1-12



Фасад в осях Ж-А*




						696/П-24-АНО/ТЭК			
						"Капитальный ремонт Государственного бюджетного общеобразовательного учреждения города Москва "Школа №1282 "Сокольники" по адресу: г. Москва, ул. Барболова, д.1, корпус 1"			
Изм.	Кол. изм.	Лист	№ док.	Проект	Дата	Комплект чертежей по результатам обмерных работ фасадов и внутренних помещений сооружения методом наземного лазерного сканирования	Стадия	Лист	Листов
Разработчик	Сидарко	1124		1124					
Проверил	Зеленцов	1124		1124				9	
ГИП	Емельянов	1124				Фасады в осях 1-12 и Ж-А*			ООО "Аркана"
Утвердил	Цыганков	1124		1124		М 1:100			
Ит. контр.	Цыганков	1124							Формат А1


This architectural elevation drawing shows a building facade with multiple levels and a complex roofline. The drawing includes numerous height annotations in meters, such as +15,180, +12,840, +11,060, +8,840, +7,120, +4,820, +4,015, +2,700, +0,860, -0,900, -0,820, -0,740, -0,610, -0,640, -0,570, -0,650, -0,700, +18,825, +19,480, +17,830, +16,890, +19,800, +19,405, +18,800, +15,590, +15,050, +12,730, +11,930, +15,060, +12,840, +11,100, +8,890, +7,110, +4,890, +4,770, +4,470, +4,015, -0,085, and -0,700. Width annotations include 22800, 43050, 18450, and 1800. The drawing also features a section line labeled 'А-А' and a section line labeled 'Б-Б'.

Формат	A1
--------	----

Фасад в осях 12-1

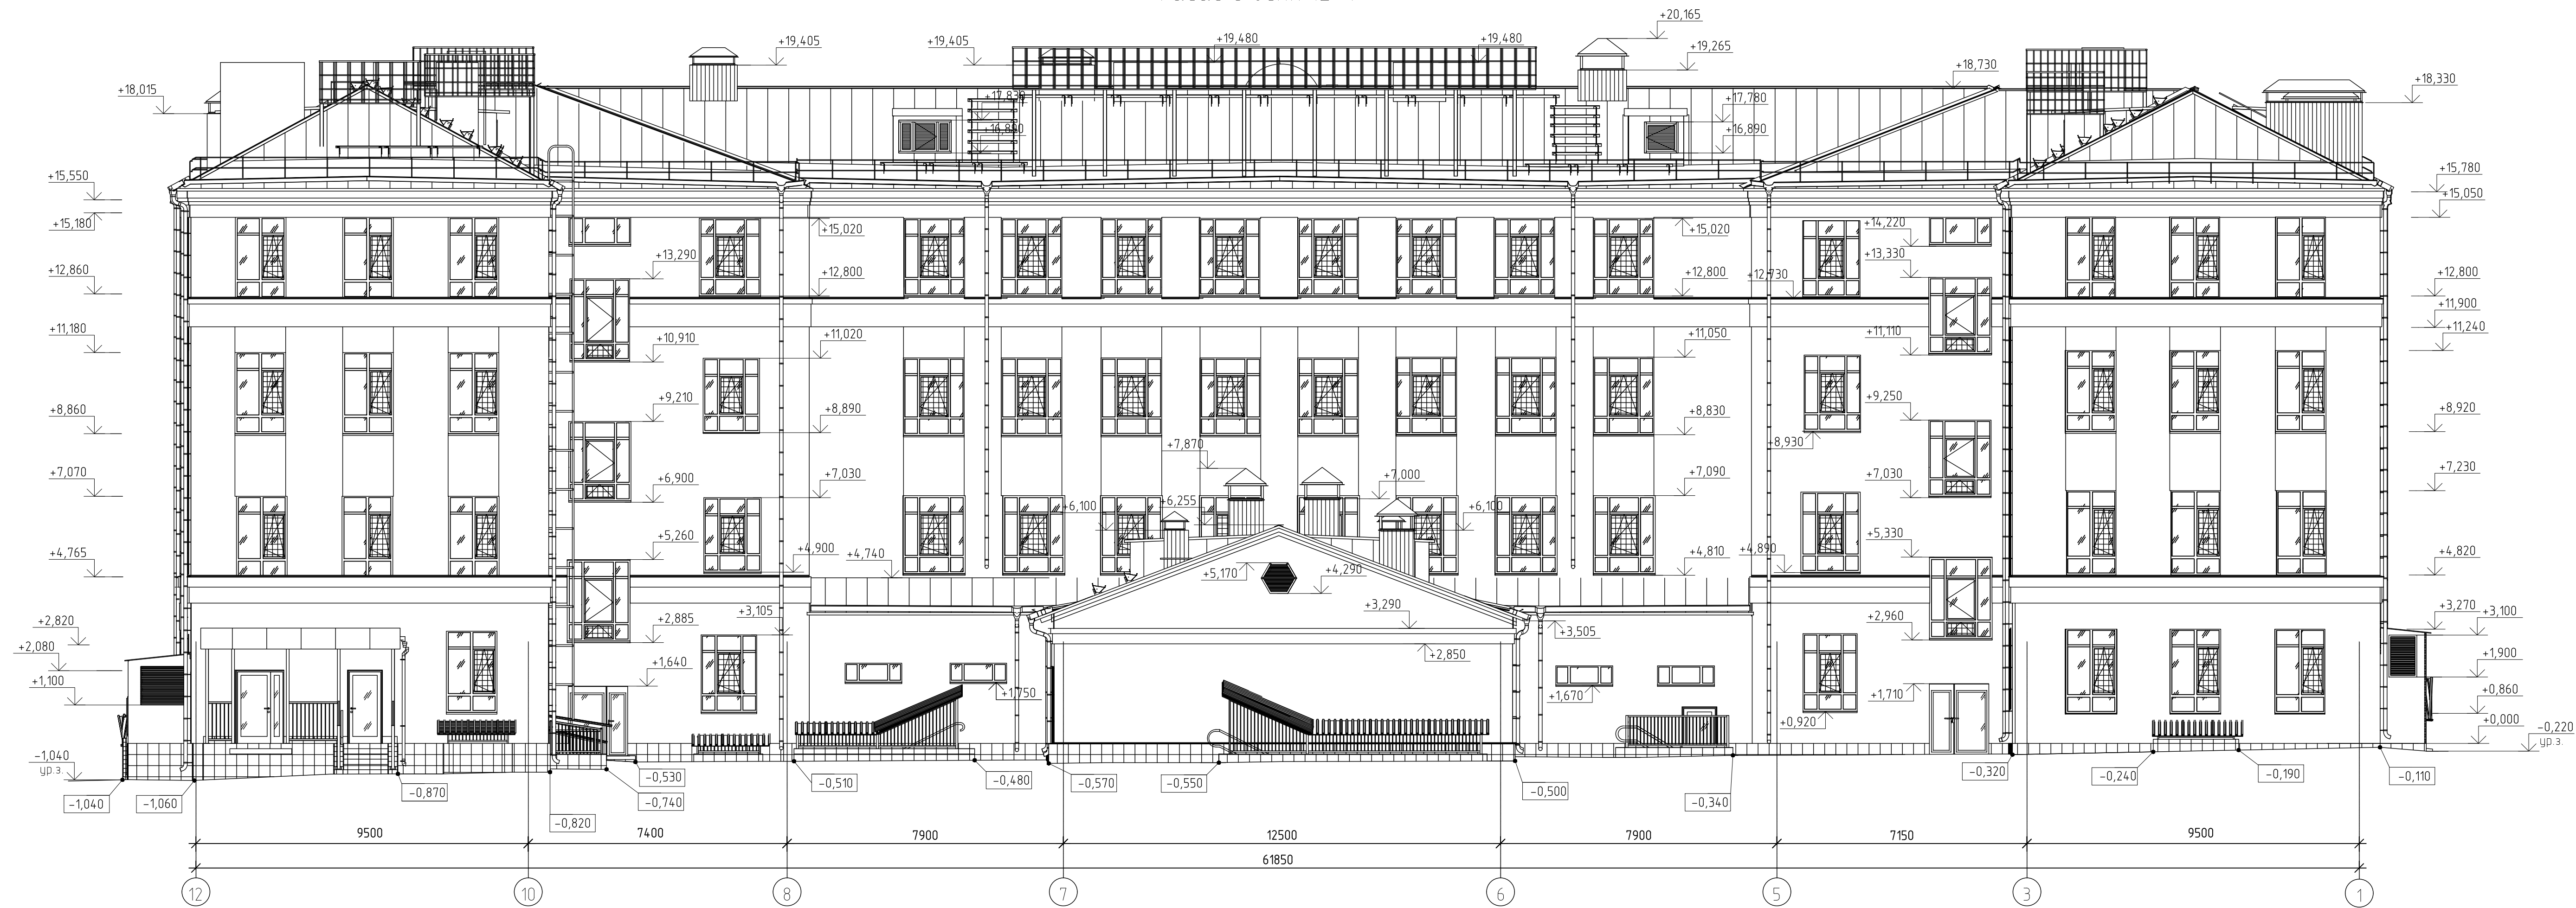


Фасад в осях А*-Ж

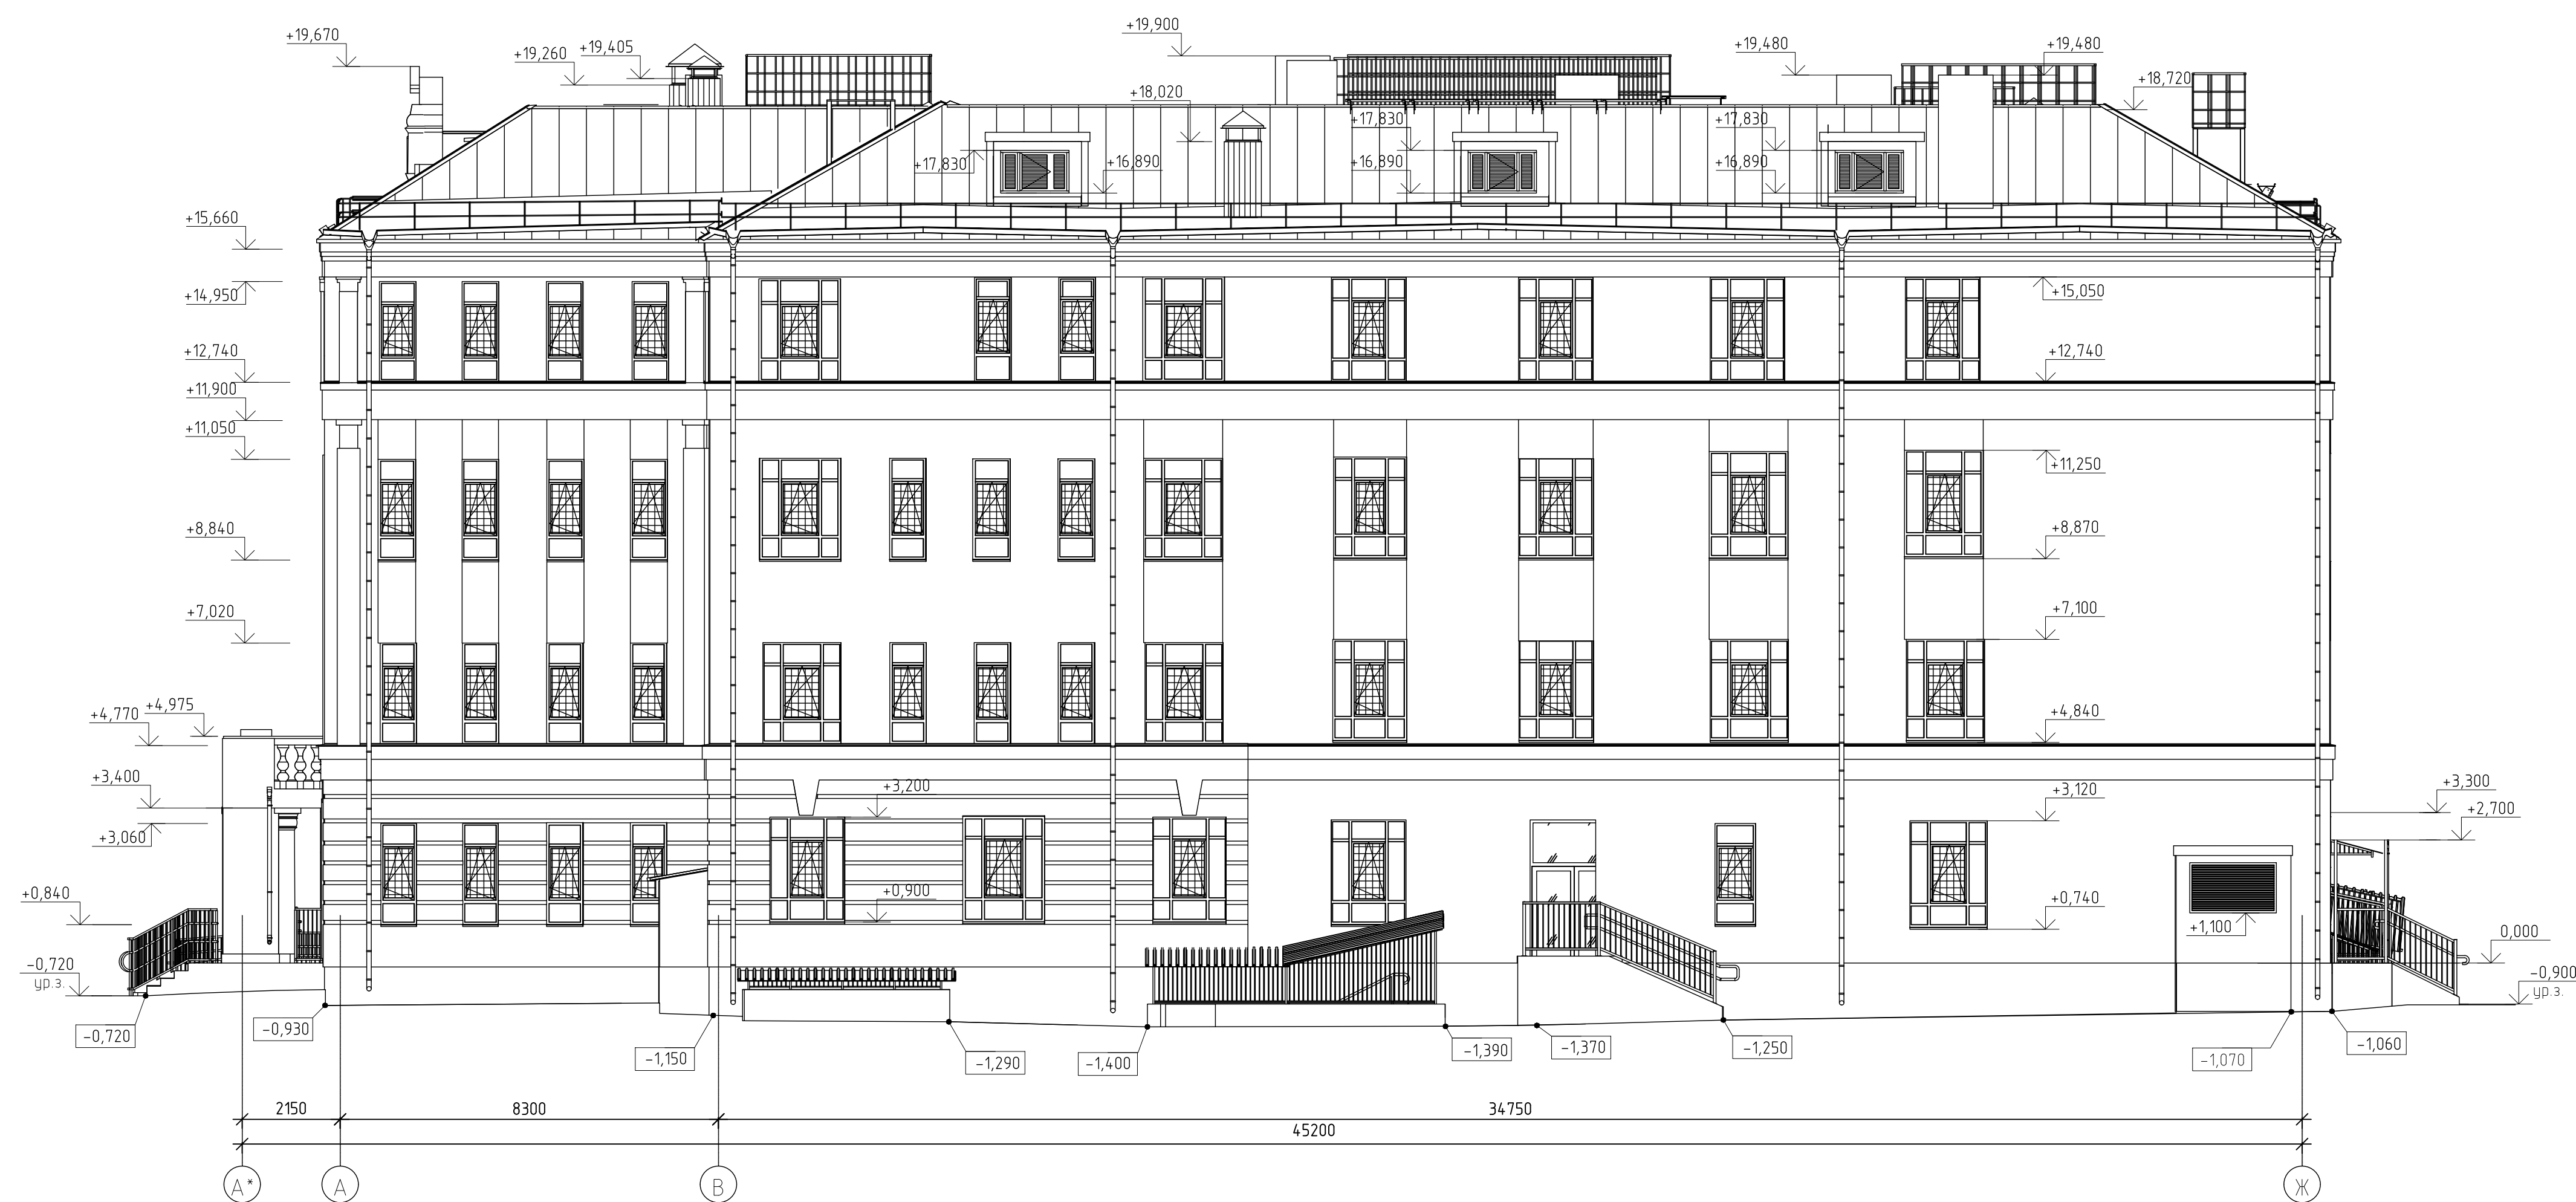

						696/П-24-АНО/ТЭК		
						"Капитальный ремонт Государственного бюджетного общеобразовательного учреждения города Москва "Школа №1282 (Сокольники)" по адресу: г. Москва, ул. Бардольна, д.1, корпус 1"		
Изм.	Кол. изм.	Лист	№ док.	Проект	Дата	Комплект чертежей по результатам обмерных работ фасадов и внутренних помещений сооружения методом наземного лазерного сканирования	Стация	Лист
Разраб.	Сидарков	1124			1124			Листов
Проверил	Зеленцов	1124			1124			
ГИП	Емельянов							
Утвердил	Цыганков	1124			1124	Фасады в осях 12-1 и А*-Ж		
И. контр.	Цыганков					М 1:100		
						ООО "Аркана"		
						Формат А1		

Фасад в осях Г-Ж по оси 7

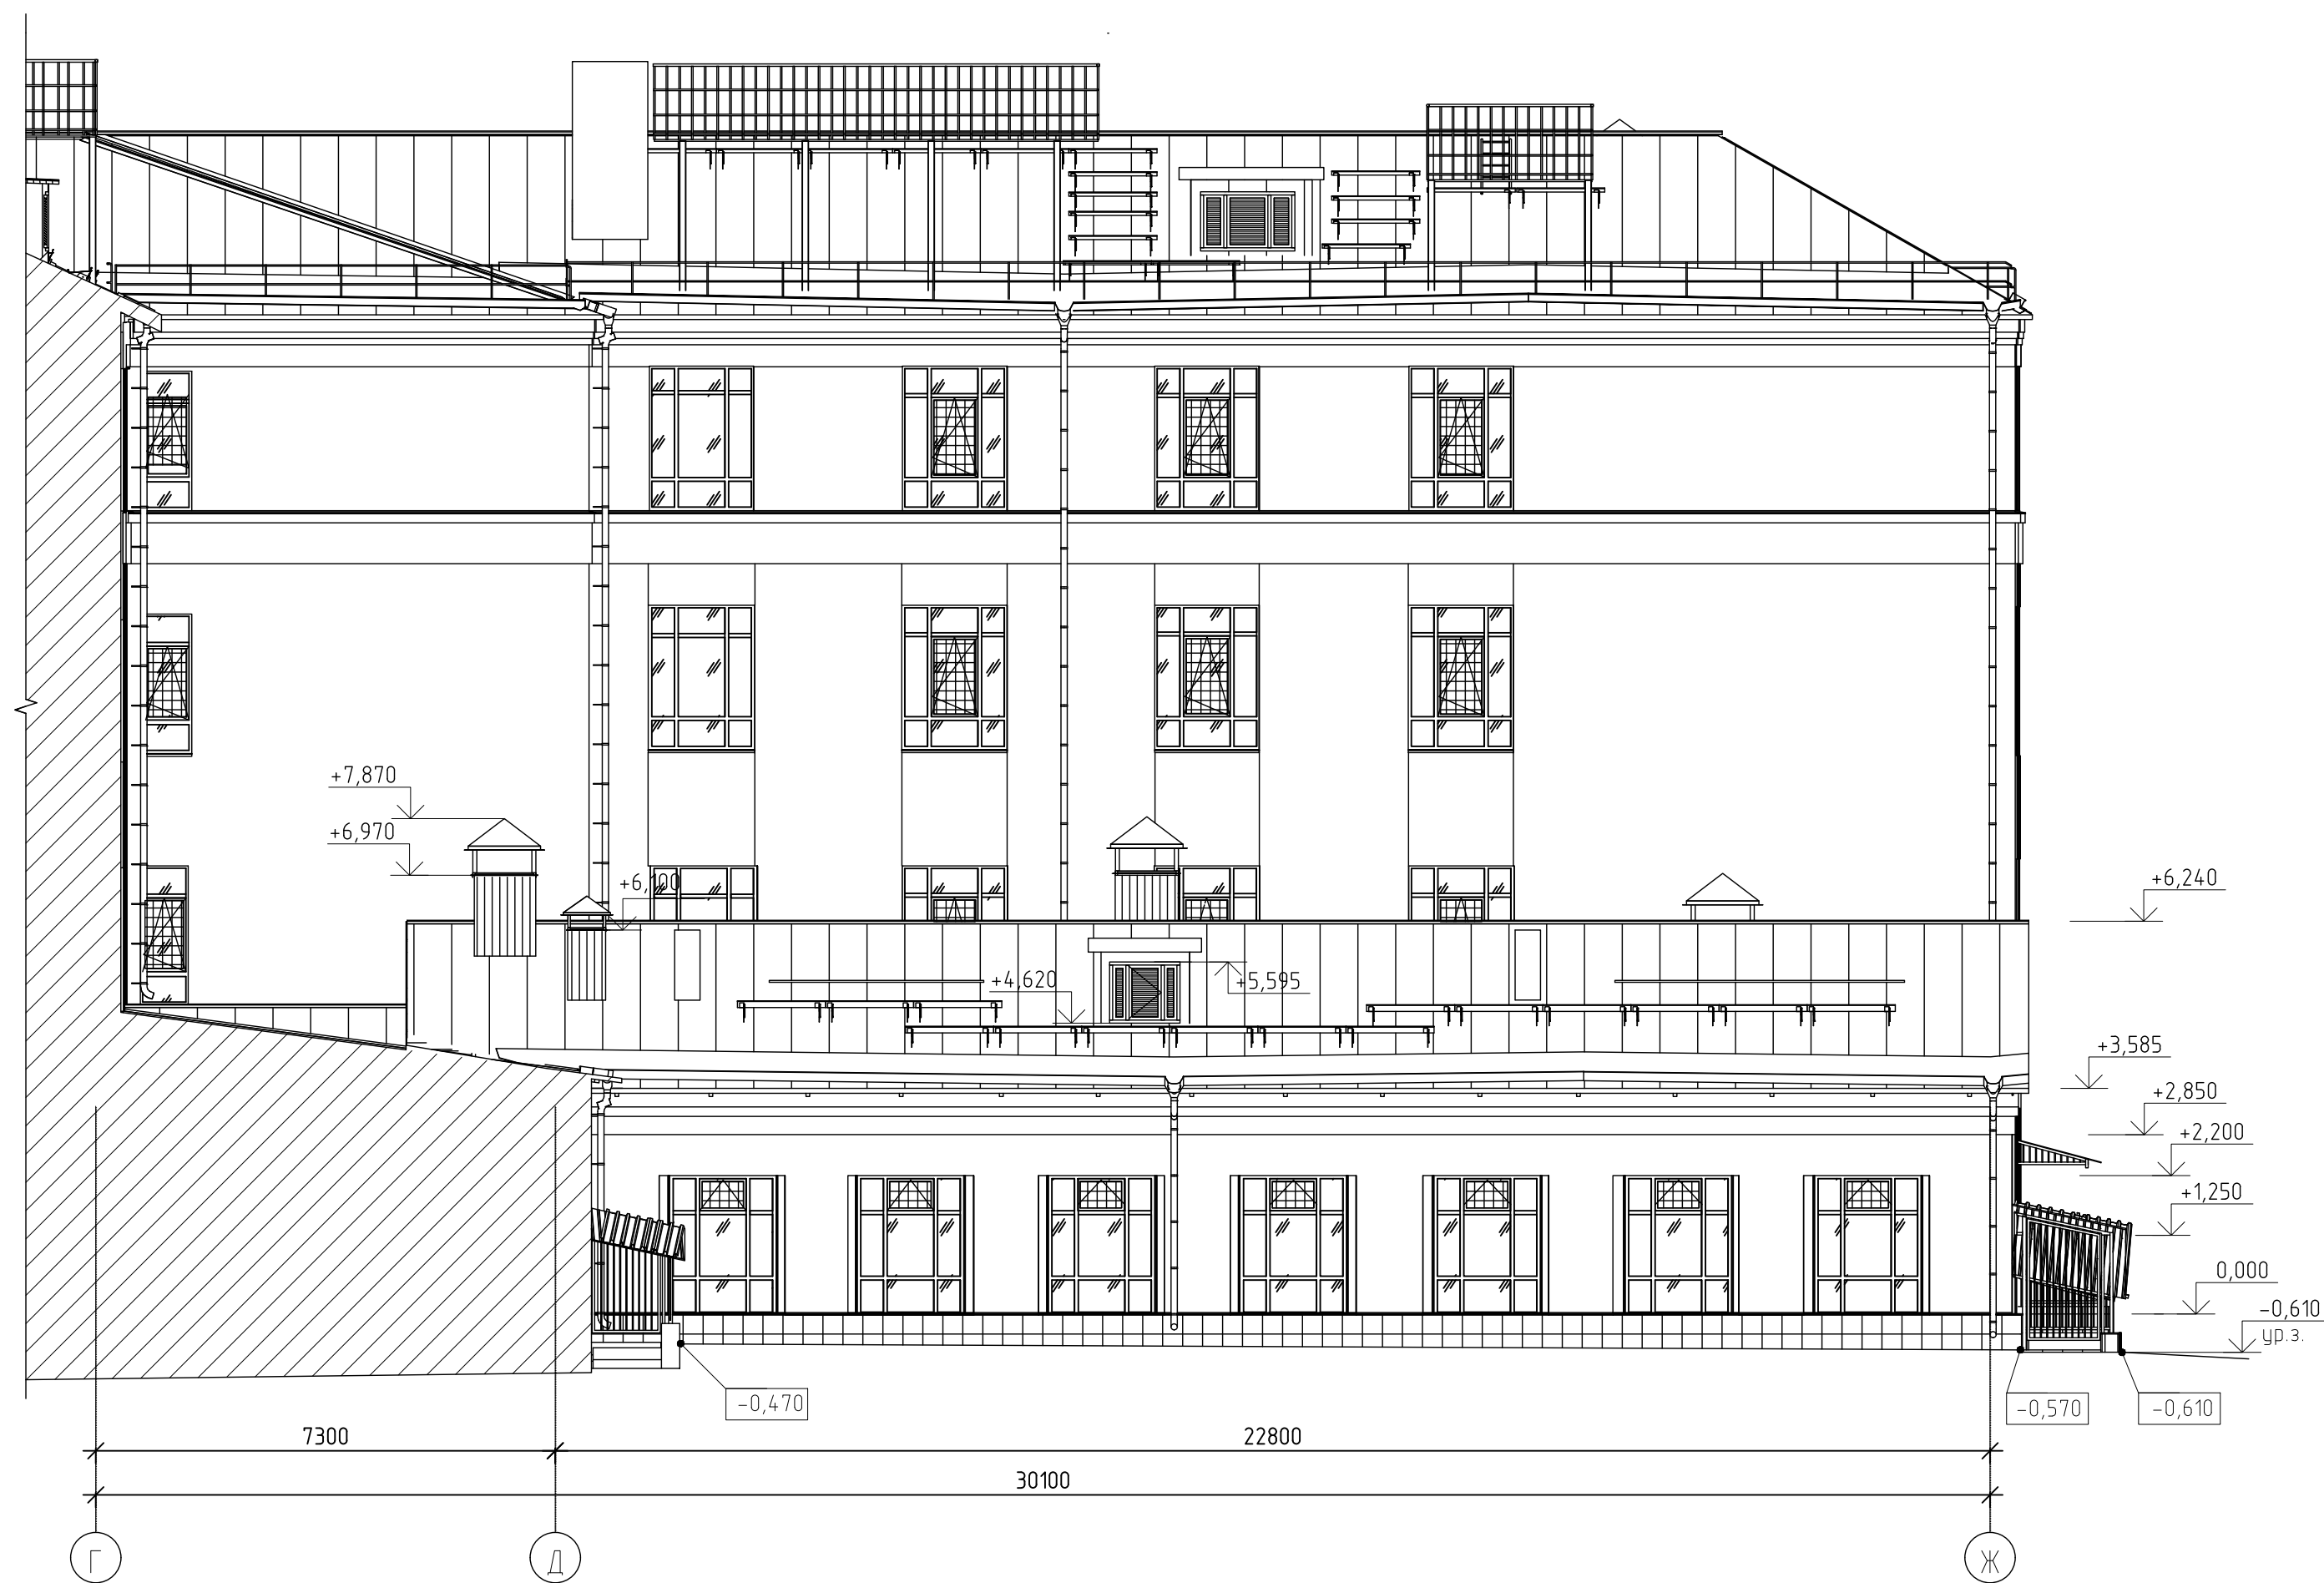

Фасад в осях А-Ж по оси 3




						696/П-24-АНО/ТЗК		
						"Капитальный ремонт Государственного бюджетного общеобразовательного учреждения города Москва "Школа №1282 "Сокольники" по адресу: г. Москва, ул. Бардолина, д.1, корпус 1"		
Изм.	Кол. изм.	Лист	№ док.	Проект	Дата	Комплект чертежей по результатам обмерных работ фасадов и внутренних помещений сооружения методом наземного лазерного сканирования	Стадия	Лист
Разраб.	Сидаркоб	1124			1124			Листов
Проверил	Зеленцов	1124			1124			12
ГИП	Емельянов	1124			1124	Фасады в осях Г-Ж по оси 7, и А-Ж по оси 3		
Утвердил	Цыганкоб	1124			1124	М 1:100		
Ит. контр.	Цыганкоб	1124			1124	ООО "Аркана"		
						Формат А1		

План перекрытия подвала

Условные обозначения

- П-1 - ж/б ребристая плита перекрытия 2,08х0,4х0,15 мм;
П-2 - ж/б ребристая плита перекрытия 2,98х0,40х0,12 мм;
П-3 - ж/б ребристая плита перекрытия 3,28х0,40х0,12 мм;
П-4 - ж/б ребристая плита перекрытия 2,40х0,40х0,12 мм;
П-5 - ж/б многослойная плита перекрытия 4,78х0,98х0,22 мм;
П-6 - ж/б многослойная плита перекрытия 3,98х0,98х0,22 мм;
П-7 - ж/б ребристая плита перекрытия 1,48х0,40х0,15 мм;
П-8 - ж/б ребристая плита перекрытия 2,80х0,40х0,15 мм;
П-9 - ж/б ребристая плита перекрытия 2,98х0,40х0,15 мм;
П-10 - ж/б ребристая плита перекрытия 3,28х0,40х0,15 мм;
П-11 - ж/б многослойная плита перекрытия 3,58х0,98х0,22 мм;
П-12 - ж/б ребристая плита перекрытия 3,80х0,40х0,15 мм;
П-13 - ж/б ребристая плита перекрытия 3,58х0,40х0,15 мм;
МП-1 - монолитной железобетонная плита перекрытия толщиной 120 мм;
МП-2 - монолитной железобетонная плита перекрытия толщиной 130 мм;
М/У - монолитный участок перекрытия 80 мм;
Б-1 - сборная железобетонная балка сечением 230х400(п) мм;
Б-2 - металлическая балка сечением I 27а по ГОСТ 16-1932 (общий размер сечения 300х270(п) мм);
Б-3 - металлическая балка сечением I 14 по ГОСТ 16-1932;
Б-4 - металлическая балка сечением I 36а по ГОСТ 16-1932;
Б-5 - сталежелезобетонная балка сечением 250х270(п) мм;
Б-6 - сталежелезобетонная балка сечением 250х280(п) мм;
Б-7 - сталежелезобетонная балка сечением 250х350(п) мм;
Б-8 - сталежелезобетонная балка сечением 300х340(п) мм;
Б-9 - сталежелезобетонная балка сечением 300х350(п) мм;
Б-10 - сталежелезобетонная балка сечением 40х350(п) мм;
Б-11 - сталежелезобетонная балка сечением 350х350 (п) мм;
Б-12 - металлическая балка сечением I 20а по ГОСТ 16-1932;
Б-13 - монолитная балка с рельсами внутри, рельс 170х170 мм;
Б-14 - сталежелезобетонная балка сечением 280х350(п) мм;
Б-15 - металлическая балка сечением I 27а по ГОСТ 16-1932;
Б-16 - сталежелезобетонная балка сечением 230х300(п) мм;
Б-17 - рельс сечением 170х170(п) мм;
Б-18 - сталежелезобетонная сечением 470х340(п) мм;
Б-19 - I 20;
Б-20 - сталежелезобетонная сечением 190х220(п) мм;
Б-21 - металлическая балка из I 36;
Б-22 - сталежелезобетонная балка из I 35;
Ф-1 - Металлическая ферма.

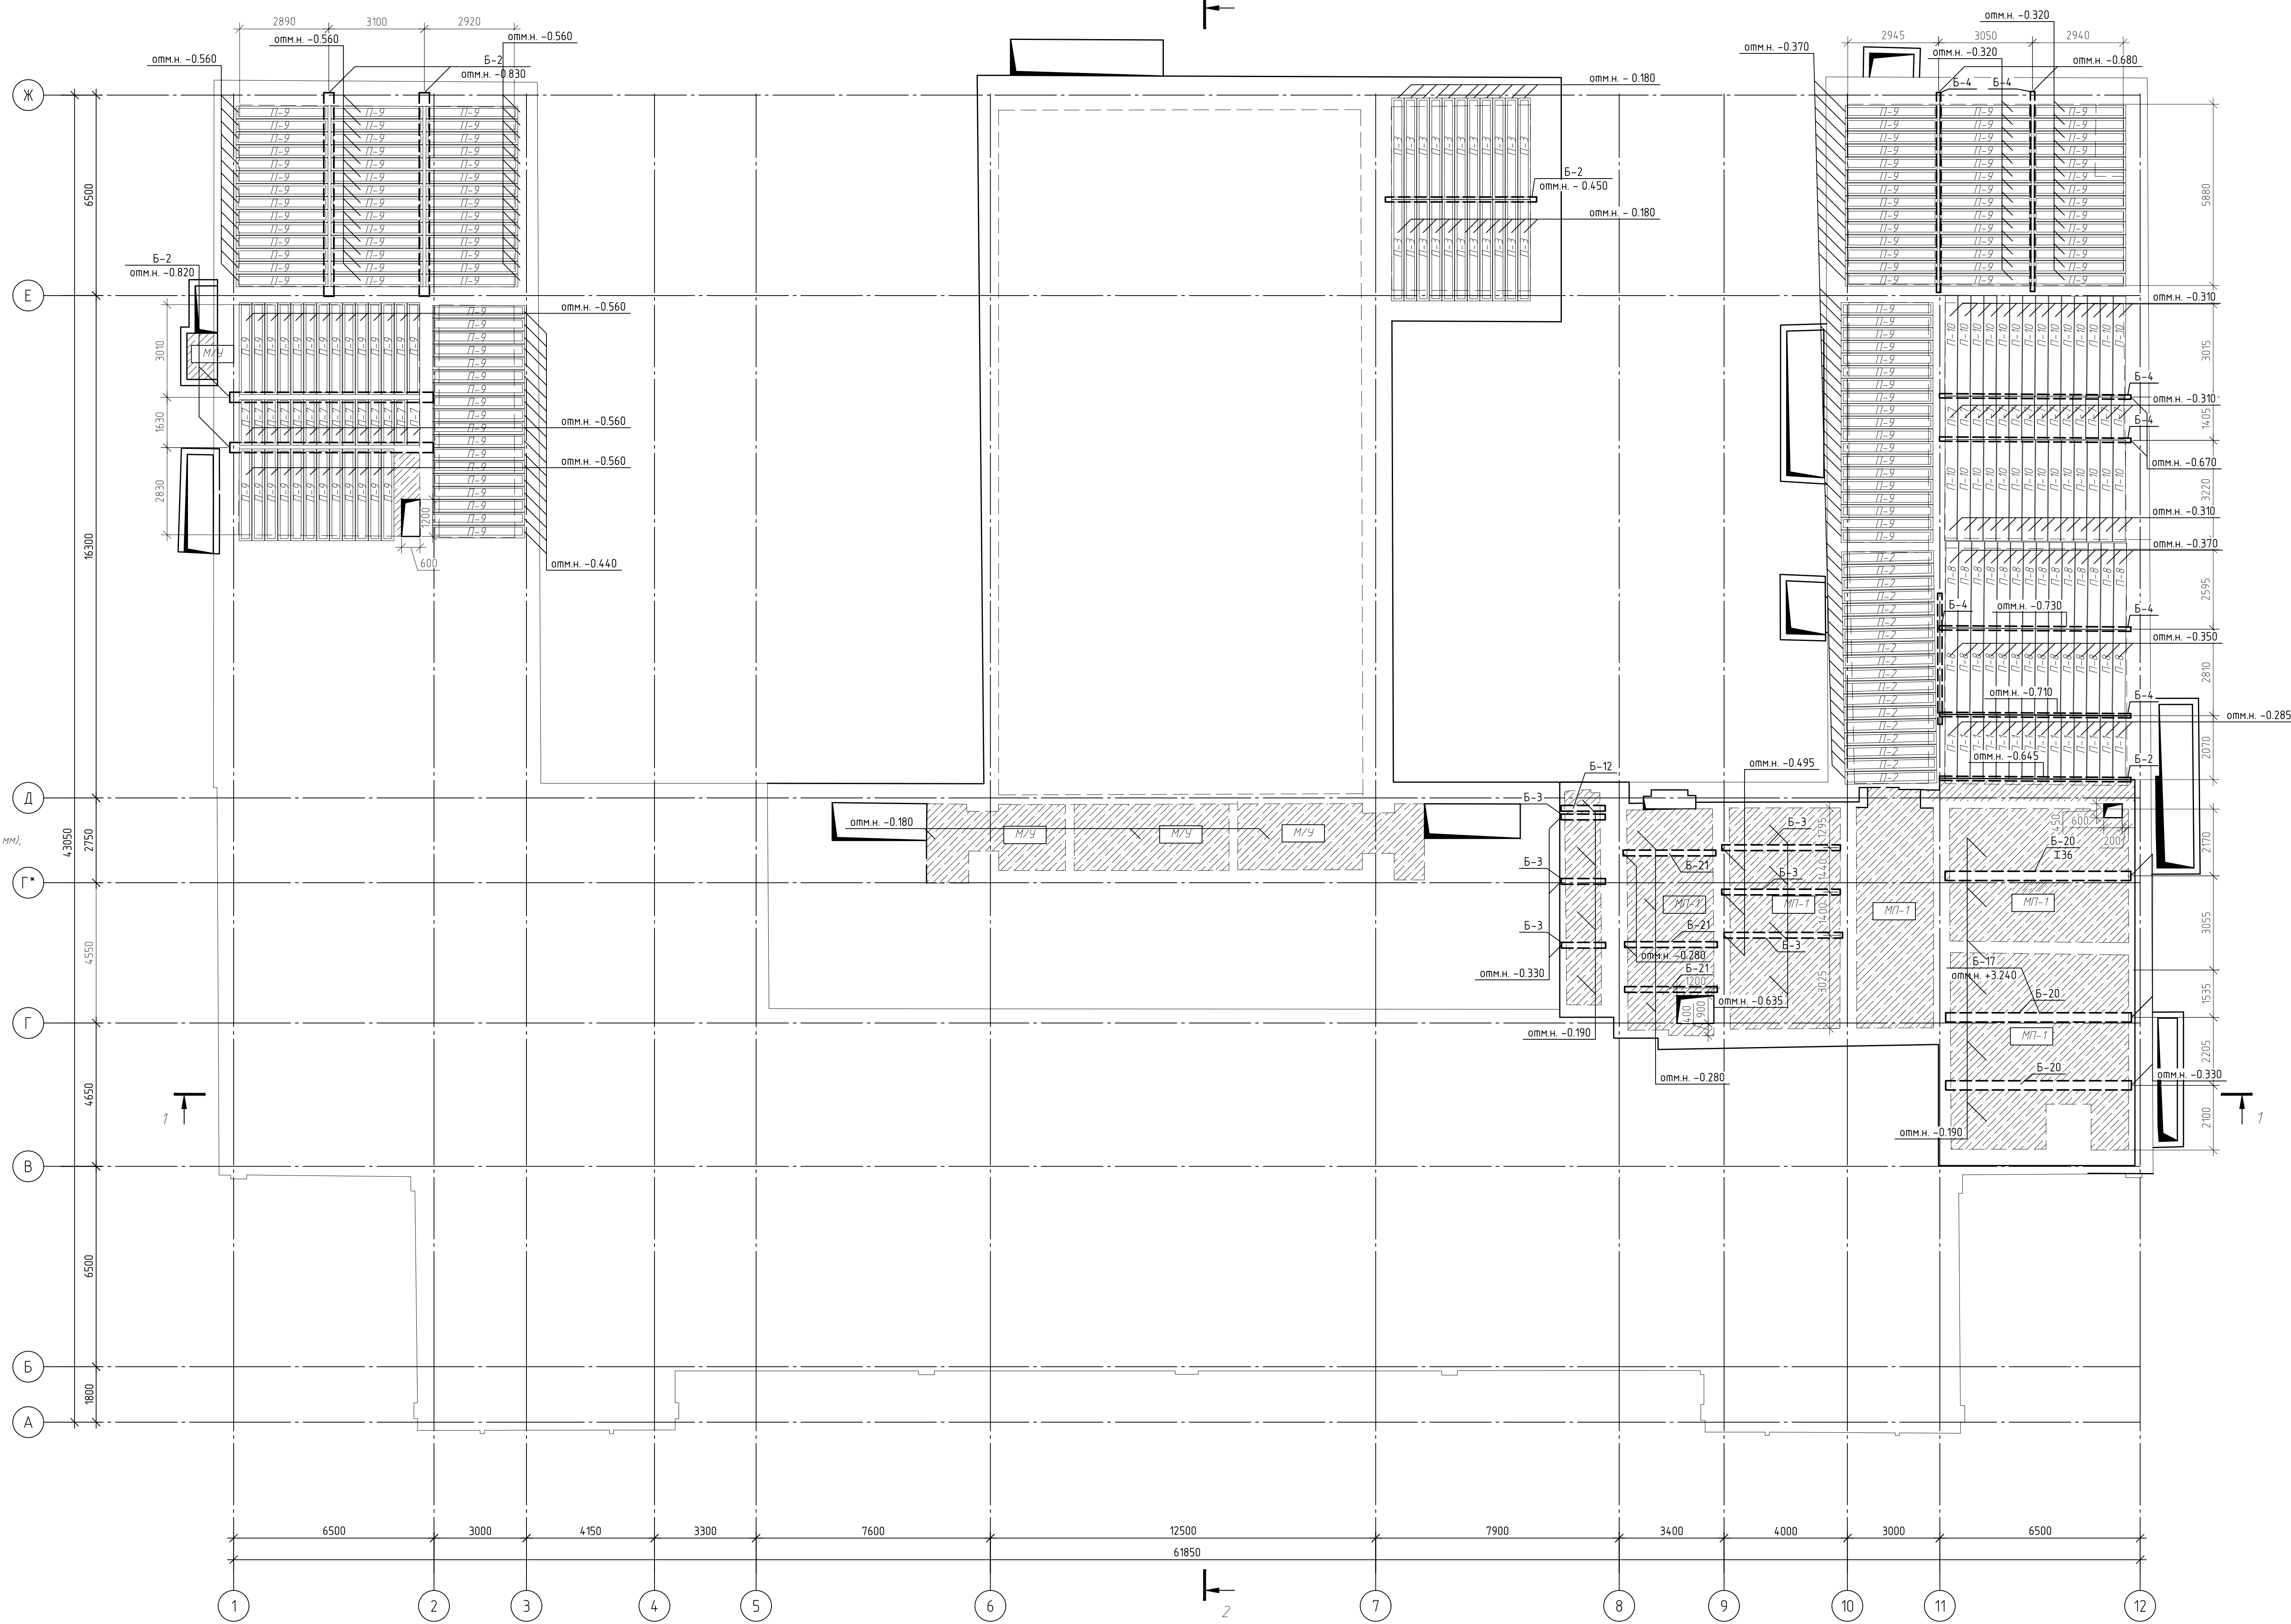


						696/П-24-АНО/ТЗК					
"Капитальный ремонт Государственного бюджетного общеобразовательного учреждения города Москвы "Школа №1292" (содержание) 1 по адресу: г. Москва, ул. Баболова, д.1, корпус 1"											
Изм.	Взм.	Лист	И. Л.	Лист	И. Л.	Комплект чертежей по результатам одобрения работ фасадов и внутренних помещений спортивной секции на первом этаже здания	Страниц	Лист	Листов		
Разработ	Соблагод	1/24	1/24	1/24	1/24		13				
Проверил	Зеленцов	2/24	2/24	2/24	2/24						
И.П.	Емельянов	3/24	3/24	3/24	3/24						
Утвердил	Шаранков	4/24	4/24	4/24	4/24	План перекрытия подвала	М 1:100			Формат А0	
И. комп.	Шаранков	5/24	5/24	5/24	5/24						

План перекрытия 1-го этажа

Условные обозначения

- П-1 - ж/б ребристая плита перекрытия 2,08x0,4x0,15 мм;
П-2 - ж/б ребристая плита перекрытия 2,98x0,40x0,12 мм;
П-3 - ж/б ребристая плита перекрытия 3,28x0,40x0,12 мм;
П-4 - ж/б ребристая плита перекрытия 2,40x0,40x0,12 мм;
П-5 - ж/б многослойная плита перекрытия 4,78x0,98x0,22 мм;
П-6 - ж/б ребристая плита перекрытия 1,48x0,40x0,15 мм;
П-7 - ж/б ребристая плита перекрытия 2,80x0,40x0,15 мм;
П-8 - ж/б ребристая плита перекрытия 2,98x0,40x0,15 мм;
П-9 - ж/б ребристая плита перекрытия 3,28x0,40x0,15 мм;
П-10 - ж/б ребристая плита перекрытия 3,58x0,98x0,22 мм;
П-11 - ж/б ребристая плита перекрытия 3,80x0,40x0,15 мм;
П-12 - ж/б ребристая плита перекрытия 3,58x0,40x0,15 мм;
П-13 - ж/б ребристая плита перекрытия 3,58x0,40x0,15 мм;
МТ-1 - монолитной железобетонная плита перекрытия толщиной 120 мм;
МТ-2 - монолитной железобетонная плита перекрытия толщиной 130 мм;
МУ-1 - монолитной участок перекрытия 80 мм;
Б-1 - сборная железобетонная балка сечением 230x460(н) мм;
Б-2 - металлическая балка сечением I 27а по ГОСТ 16-1932 (общий размер сечения 300x270(н) мм);
Б-3 - металлическая балка сечением I 14 по ГОСТ 16-1932;
Б-4 - металлическая балка сечением I 36а по ГОСТ 16-1932;
Б-5 - сталежелезобетонная балка сечением 250x270(н) мм;
Б-6 - сталежелезобетонная балка сечением 250x280(н) мм;
Б-7 - сталежелезобетонная балка сечением 250x350(н) мм;
Б-8 - сталежелезобетонная балка сечением 300x340(н) мм;
Б-9 - сталежелезобетонная балка сечением 300x350(н) мм;
Б-10 - сталежелезобетонная балка сечением 40x350(н) мм;
Б-11 - сталежелезобетонная балка сечением 350x350 (н) мм;
Б-12 - металлическая балка сечением I 20а по ГОСТ 16-1932;
Б-13 - монолитная балка с рельсами внутри, рельс 170x170 мм;
Б-14 - сталежелезобетонная балка сечением 280x350(н) мм;
Б-15 - металлическая балка сечением I 27а по ГОСТ 16-1932;
Б-16 - сталежелезобетонная балка сечением 230x310(н) мм;
Б-17 - рельс сечением 170x170(н) мм;
Б-18 - сталежелезобетонная сечением 470x340(н) мм;
Б-19 - I 20;
Б-20 - сталежелезобетонная сечением 190x220(н) мм;
Б-21 - металлическая балка из I 36;
Б-22 - сталежелезобетонная балка из I 35;
Ф-1 - Металлическая ферма.

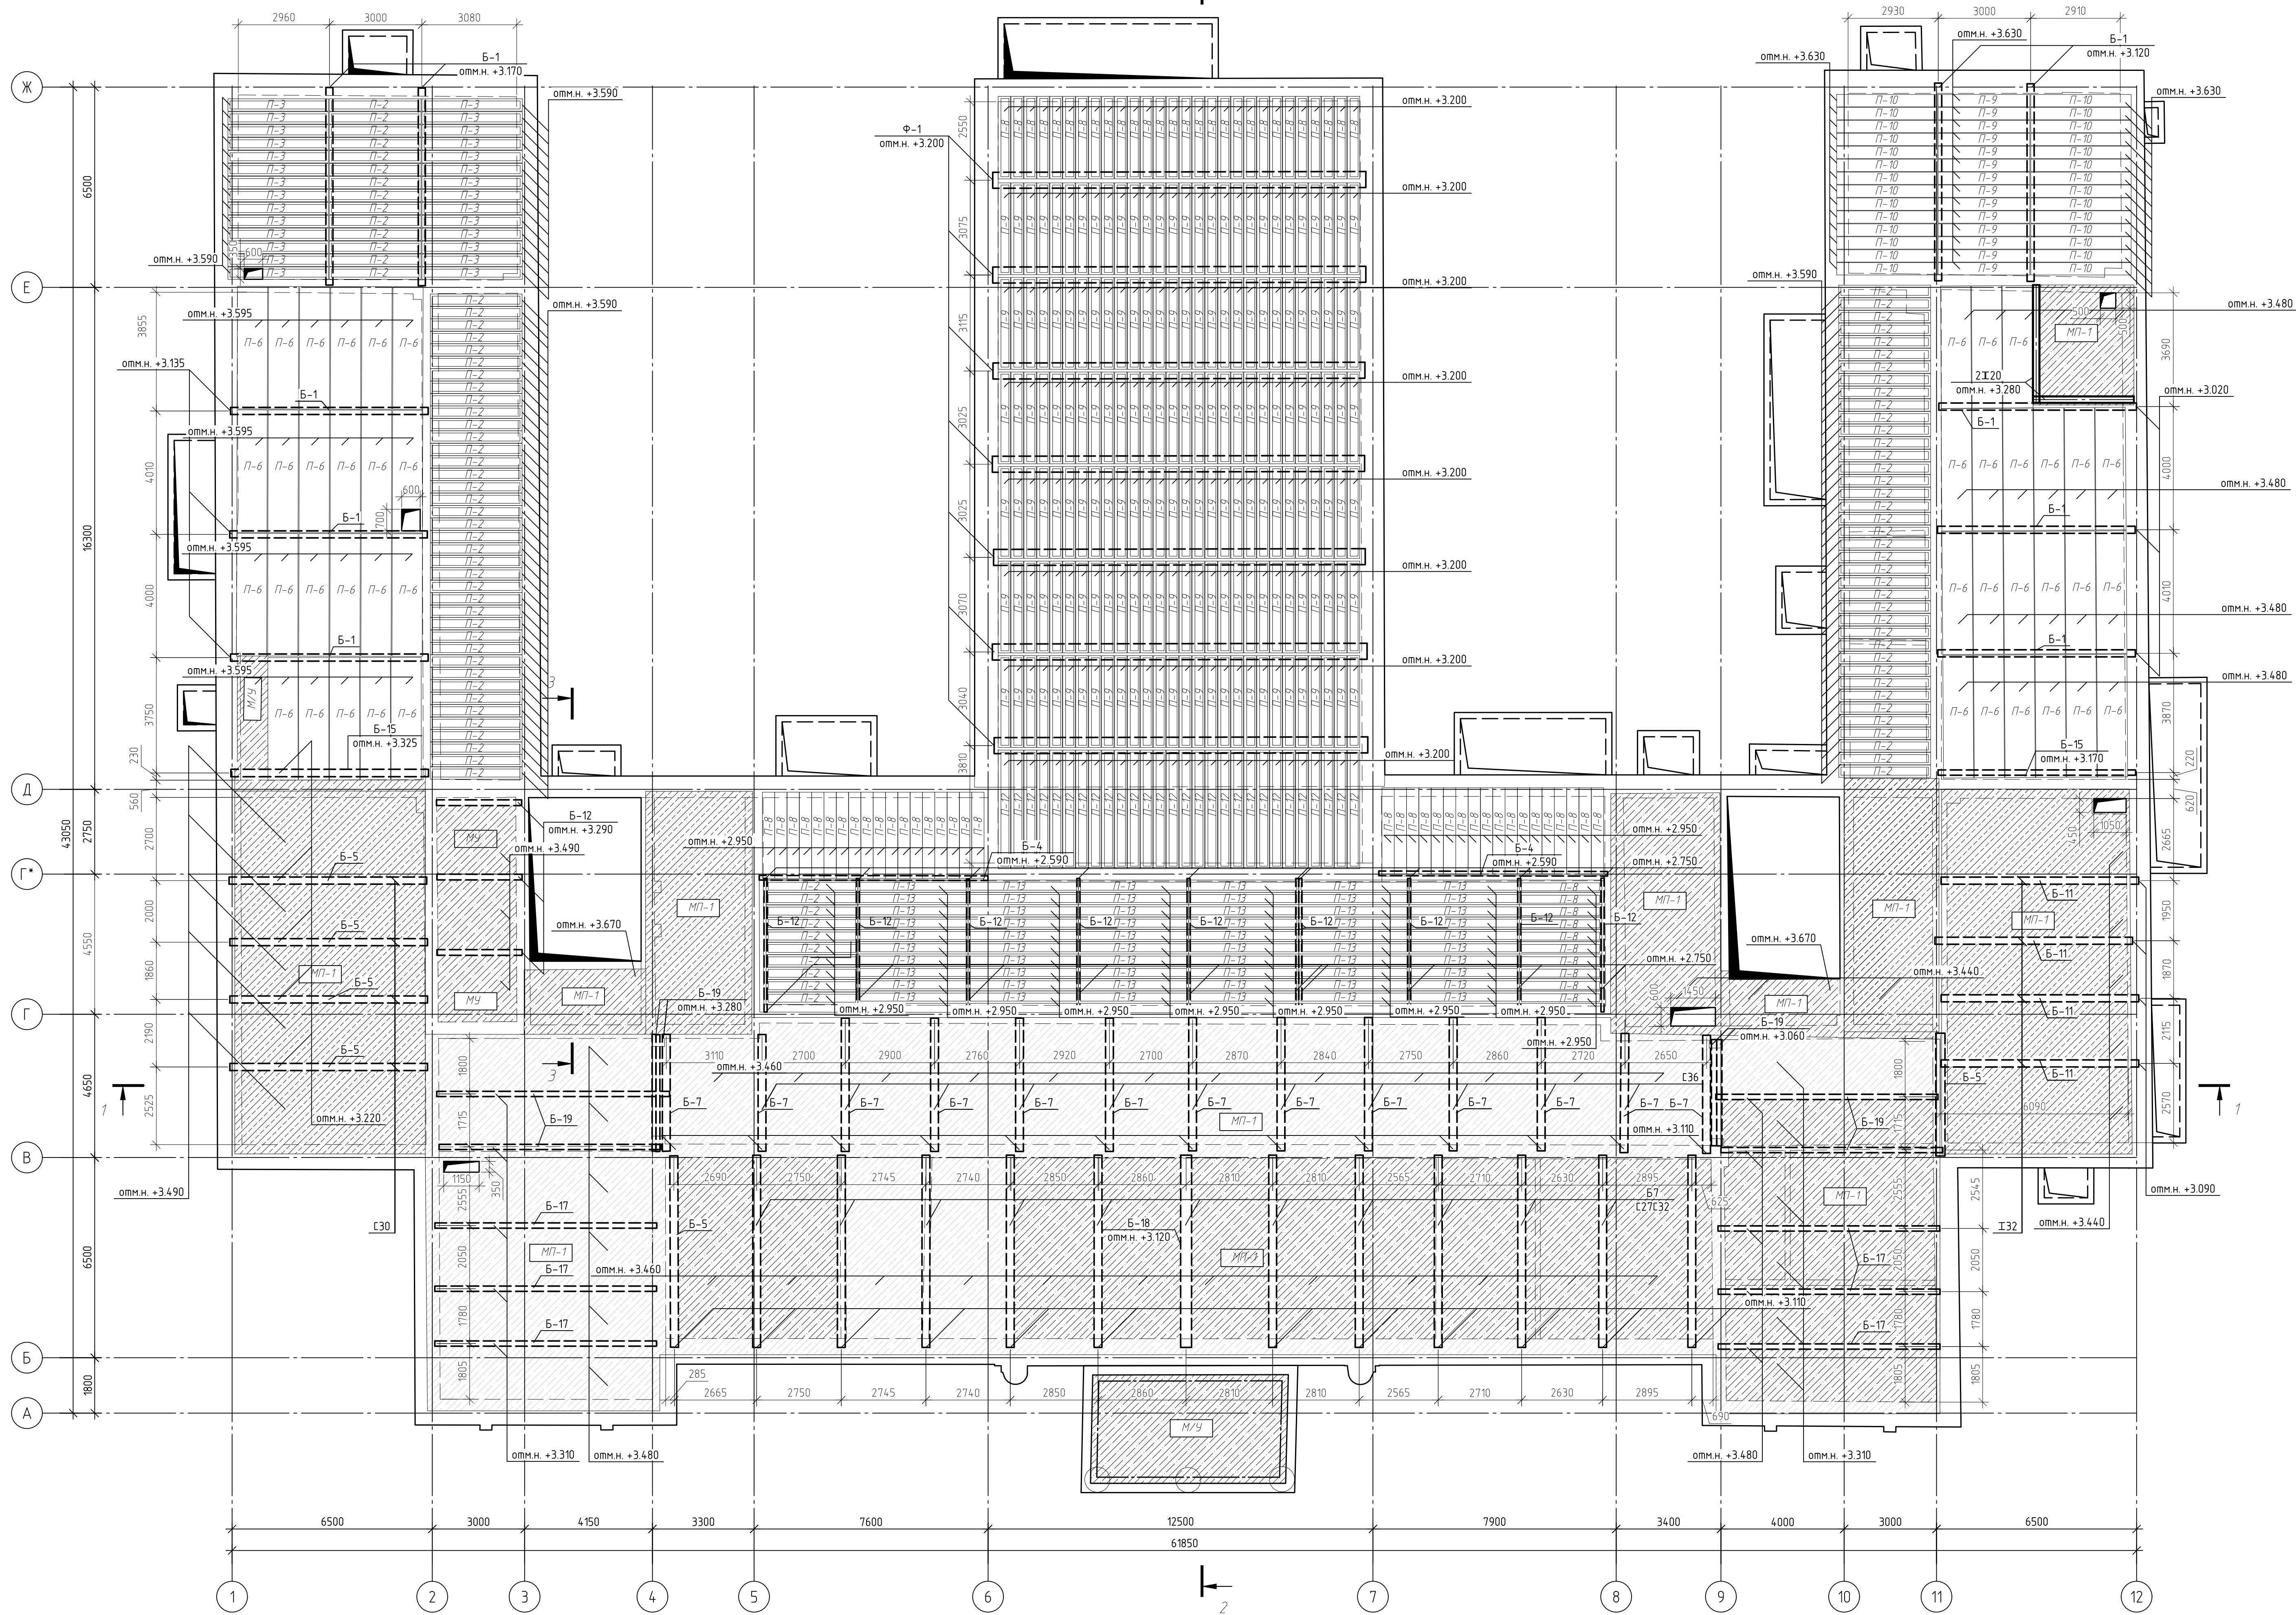


						696/П-24-АНО/ТЭК	
				"Капитальный ремонт Государственного бюджетного общеобразовательного учреждения города Москвы "Школа №1292" (секция №1) по адресу: г. Москва, ул. Баболова, д.1, корпус 1"			
Изм.	Взм.	Лист	М.в.	Изд.	Шта	Комплект чертежей по результатам одобрения работ фасадов и внутренних помещений спортивной секцией на званого логотипа сжидирования	
Разреш.	Соблагод.	Зеленцов	И.В.	И.В.	И.В.		
Проверил	Емельянов	И.В.	И.В.	И.В.	И.В.		
И.П.	И.П.	И.П.	И.П.	И.П.	И.П.	План перекрытия 1-го этажа	
И.В.	И.В.	И.В.	И.В.	И.В.	И.В.	М 1:100	
И.В.	И.В.	И.В.	И.В.	И.В.	И.В.	000 "Арктик"	
				Формат А0			

План перекрытия 2-го этажа

Сквозные обозначения

- П-1 - ж/б ребристая плита перекрытия 2,08x0,4x0,15 мм,
П-2 - ж/б ребристая плита перекрытия 2,98x0,4x0,12 мм,
П-3 - ж/б ребристая плита перекрытия 3,28x0,4x0,12 мм,
П-4 - ж/б ребристая плита перекрытия 2,40x0,4x0,12 мм,
П-5 - ж/б многослойная плита перекрытия 4,78x0,98x0,22 мм,
П-6 - ж/б многослойная плита перекрытия 3,98x0,98x0,22 мм,
П-7 - ж/б ребристая плита перекрытия 1,48x0,4x0,15 мм,
П-8 - ж/б ребристая плита перекрытия 2,80x0,4x0,15 мм,
П-9 - ж/б ребристая плита перекрытия 2,98x0,4x0,15 мм,
П-10 - ж/б ребристая плита перекрытия 3,28x0,4x0,15 мм,
П-11 - ж/б многослойная плита перекрытия 3,58x0,98x0,22 мм,
П-12 - ж/б ребристая плита перекрытия 3,80x0,4x0,15 мм,
П-13 - ж/б ребристая плита перекрытия 3,58x0,4x0,15 мм,
МП-1 - монолитной железобетонная плита перекрытия толщиной 120 мм,
МП-2 - монолитной железобетонная плита перекрытия толщиной 130 мм,
М/У - монолитный участок перекрытия 80 мм,
Б-1 - сборная железобетонная балка сечением 230x460(н) мм,
Б-2 - металлическая балка сечением II 27а по ГОСТ 16-1932 (общий размер сечения 300x270(н) мм),
Б-3 - металлическая балка сечением I 14 по ГОСТ 16-1932,
Б-4 - металлическая балка сечением I 36а по ГОСТ 16-1932,
Б-5 - сталежелезобетонная балка сечением 250x270(н) мм,
Б-6 - сталежелезобетонная балка сечением 250x280(н) мм,
Б-7 - сталежелезобетонная балка сечением 250x350(н) мм,
Б-8 - сталежелезобетонная балка сечением 300x400(н) мм,
Б-9 - сталежелезобетонная балка сечением 300x350(н) мм,
Б-10 - сталежелезобетонная балка сечением 40x350(н) мм,
Б-11 - сталежелезобетонная балка сечением 350x350 (н) мм,
Б-12 - металлическая балка сечением I 20а по ГОСТ 16-1932,
Б-13 - монолитная балка с рельсами внутри, рельс 170x170 мм,
Б-14 - сталежелезобетонная балка сечением 280x350(н) мм,
Б-15 - металлическая балка сечением I 27а по ГОСТ 16-1932,
Б-16 - сталежелезобетонная балка сечением 230x300(н) мм,
Б-17 - рельс сечением 170x170(н) мм,
Б-18 - сталежелезобетонная сечением 470x340(н) мм,
Б-19 - I 20,
Б-20 - сталежелезобетонная сечением 190x220(н) мм,
Б-21 - металлическая балка из I 36,
Б-22 - сталежелезобетонная балка из I 35,
Ф-1 - Металлическая ферма.

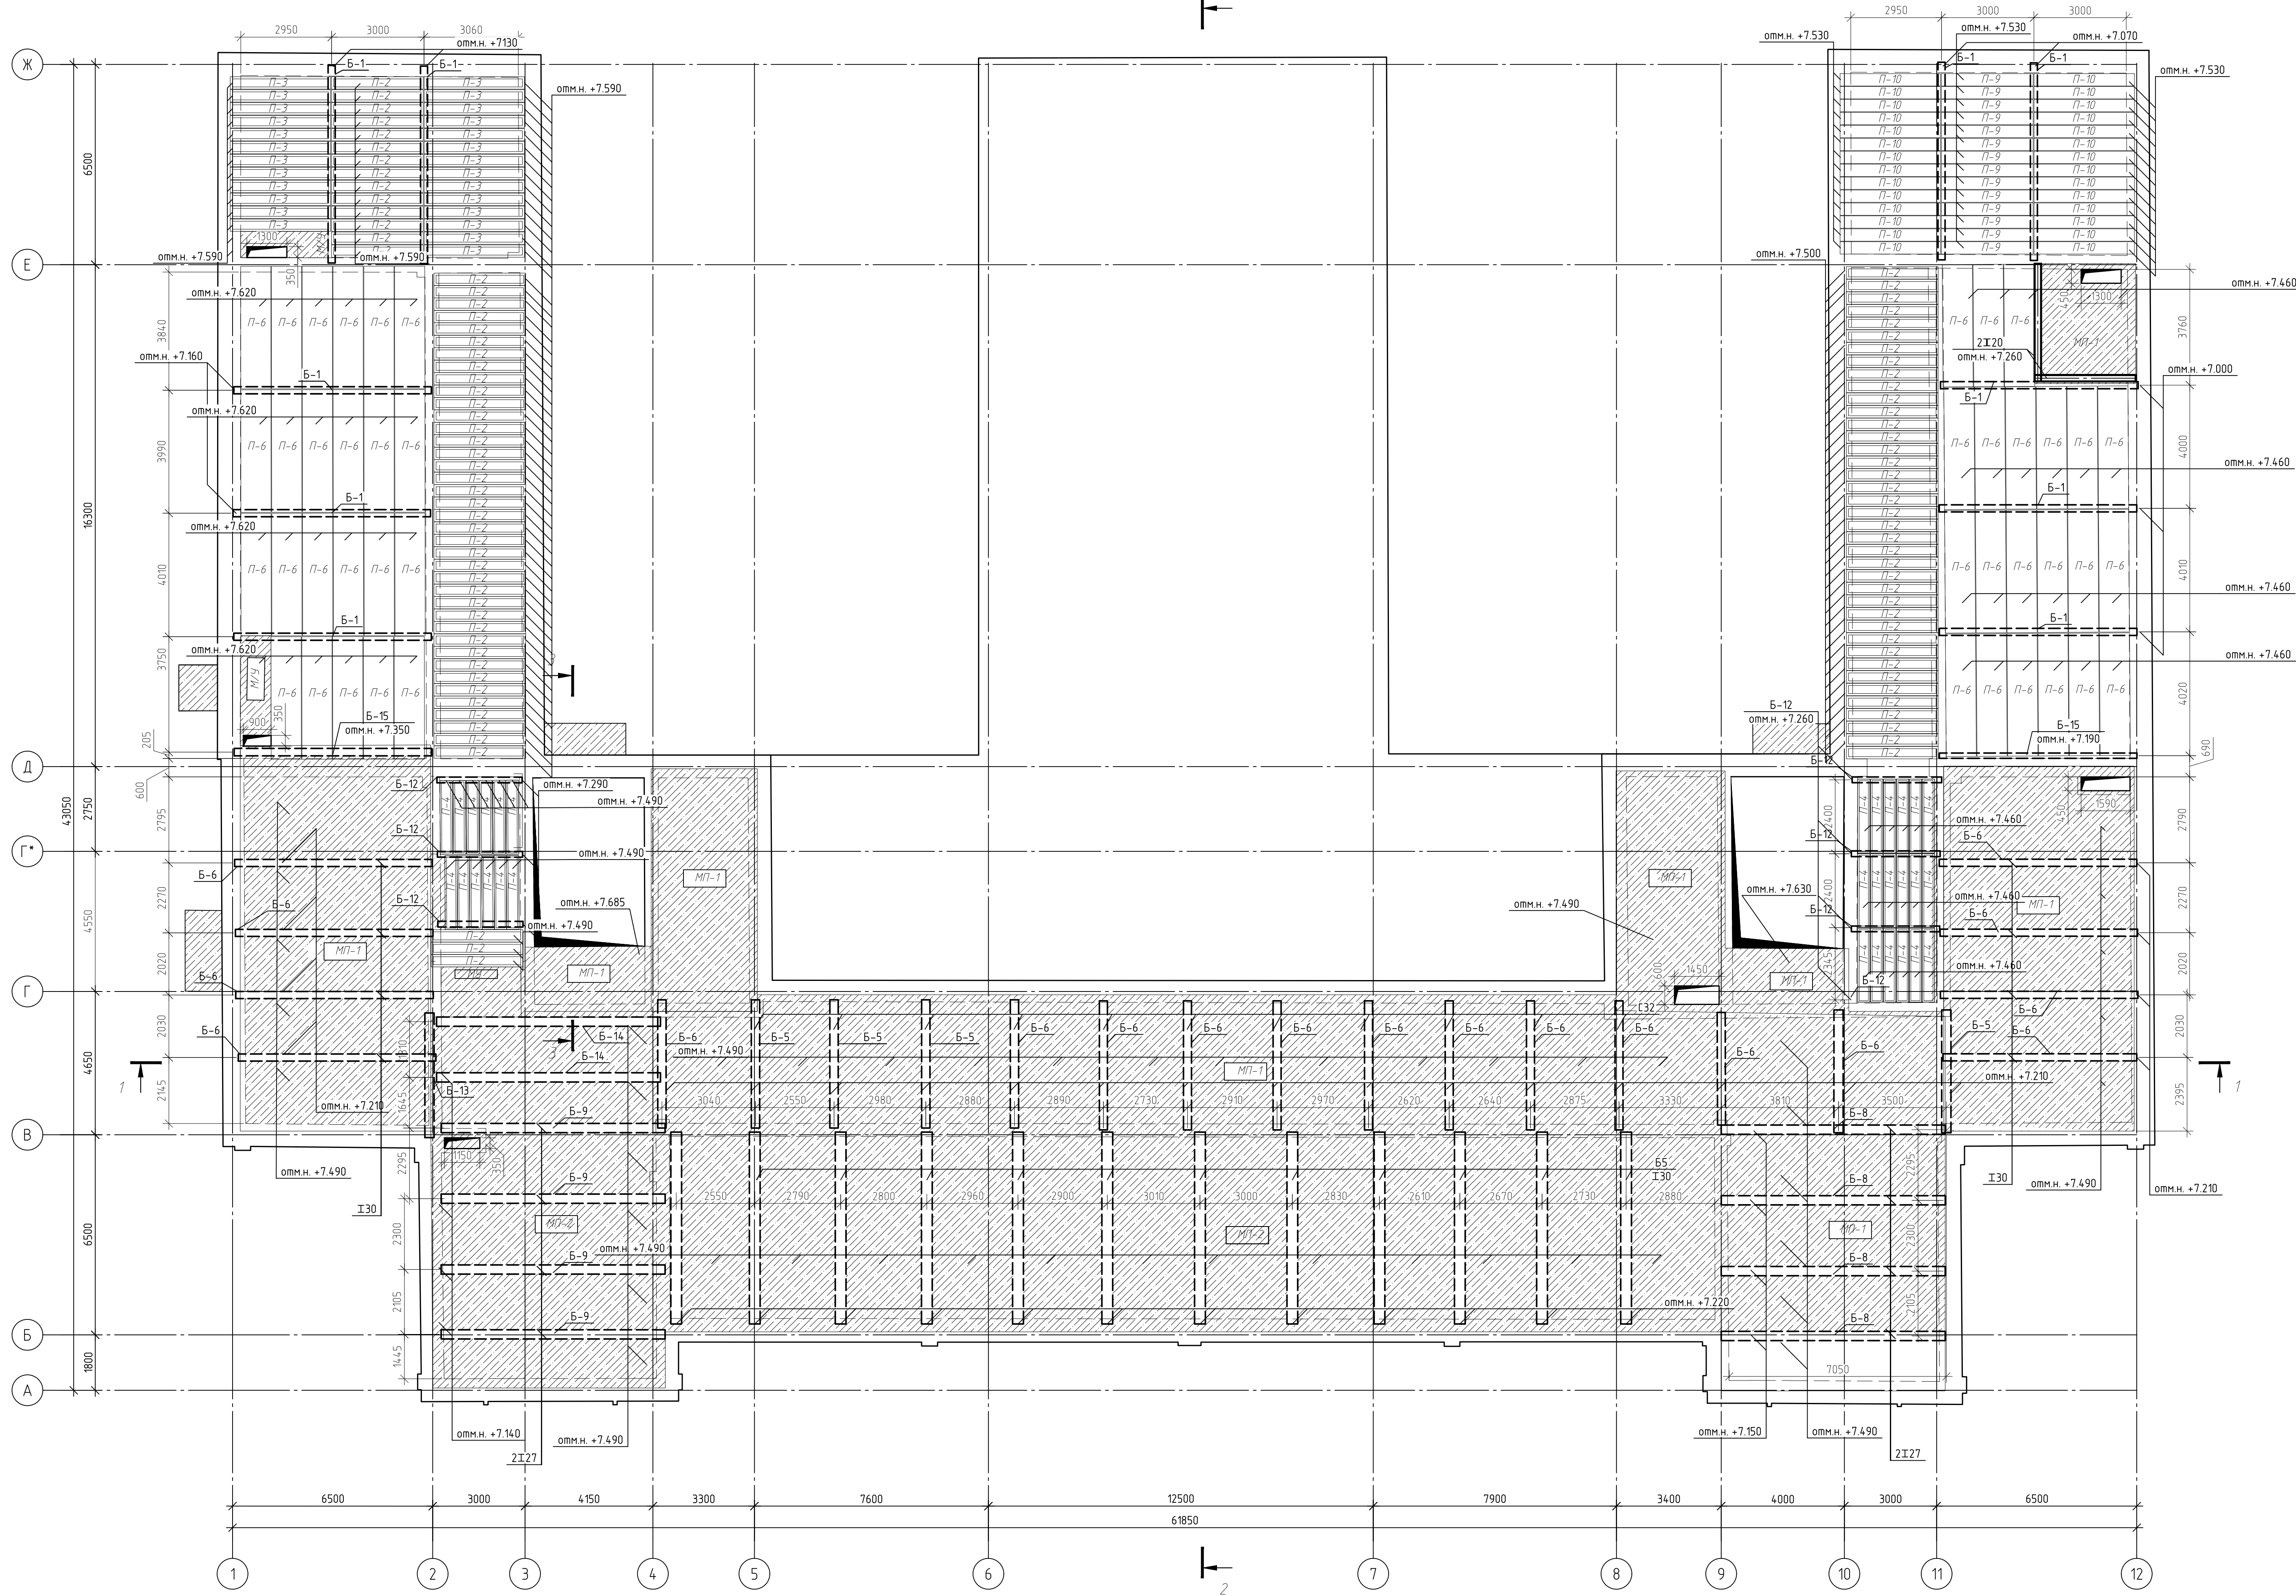


696/П-24-АНО/ТЭК					
"Капитальный ремонт Государственного бюджетного общеобразовательного учреждения города Москвы "Школа №1292" (составляющие 1 по объекту в Москве, ул. Баболова, д.1, корпус 11"					
Изм.	Взм.	Лист	И. Л.	Лист	Лист
Разработ	С.И.Павлов	1/24	1/24	1/24	1/24
Проверил	Зеленцов	1/24	1/24	1/24	1/24
ГИП	Емельянов	1/24	1/24	1/24	1/24
Утвердил	Шаталов	1/24	1/24	1/24	1/24
Н. контр.	Шаталов	1/24	1/24	1/24	1/24
Комплект чертежей по результатам одноконт. работ фасадов и внутренних помещений спортивной резиденции на земельном участке с кадастровым				Лист	Лист
План перекрытия 2-го этажа				15	Лист
М 1:100				000 "Аркан"	
				Формат А0	

План перекрытия 3-го этажа

Условные обозначения

- П-1 - ж/б ребристая плита перекрытия 2,08х0,4х0,15 мм;
П-2 - ж/б ребристая плита перекрытия 2,98х0,4х0,12 мм;
П-3 - ж/б ребристая плита перекрытия 3,28х0,4х0,12 мм;
П-4 - ж/б ребристая плита перекрытия 2,40х0,4х0,12 мм;
П-5 - ж/б многослойная плита перекрытия 4,78х0,98х0,22 мм;
П-6 - ж/б многослойная плита перекрытия 3,98х0,98х0,22 мм;
П-7 - ж/б ребристая плита перекрытия 1,48х0,4х0,15 мм;
П-8 - ж/б ребристая плита перекрытия 2,80х0,4х0,15 мм;
П-9 - ж/б ребристая плита перекрытия 2,98х0,4х0,15 мм;
П-10 - ж/б ребристая плита перекрытия 3,28х0,4х0,15 мм;
П-11 - ж/б многослойная плита перекрытия 3,58х0,98х0,22 мм;
П-12 - ж/б ребристая плита перекрытия 3,80х0,4х0,15 мм;
П-13 - ж/б ребристая плита перекрытия 3,58х0,4х0,15 мм;
МТ-1 - монолитная железобетонная плита перекрытия толщиной 120 мм;
МТ-2 - монолитная железобетонная плита перекрытия толщиной 130 мм;
М/У - монолитный участок перекрытия 80 мм;
Б-1 - сборная железобетонная балка сечением 230х460(н) мм;
Б-2 - металлическая балка сечением И 270 по ОСТ 16-1932 (общий размер сечения 300х270(н) мм);
Б-3 - металлическая балка сечением И 16 по ОСТ 16-1932;
Б-4 - металлическая балка сечением И 36а по ОСТ 16-1932;
Б-5 - сталежелезобетонная балка сечением 250х270(н) мм;
Б-6 - сталежелезобетонная балка сечением 250х280(н) мм;
Б-7 - сталежелезобетонная балка сечением 250х350(н) мм;
Б-8 - сталежелезобетонная балка сечением 300х340(н) мм;
Б-9 - сталежелезобетонная балка сечением 300х350(н) мм;
Б-10 - сталежелезобетонная балка сечением 410х350(н) мм;
Б-11 - сталежелезобетонная балка сечением 350х350 (н) мм;
Б-12 - металлическая балка сечением И 20а по ОСТ 16-1932;
Б-13 - монолитная балка с рельсами внутри, релсы 170х170 мм;
Б-14 - сталежелезобетонная балка сечением 280х350(н) мм;
Б-15 - металлическая балка сечением И 27а по ОСТ 16-1932;
Б-16 - сталежелезобетонная балка сечением 230х310(н) мм;
Б-17 - релсы сечением 170х170(н) мм;
Б-18 - сталежелезобетонная сечением 470х340(н) мм;
Б-19 - И 20;
Б-20 - сталежелезобетонная сечением 190х220(н) мм;
Б-21 - металлическая балка из И 36;
Б-22 - сталежелезобетонная балка из И 35;

Ф-1 - Металлическая ферма

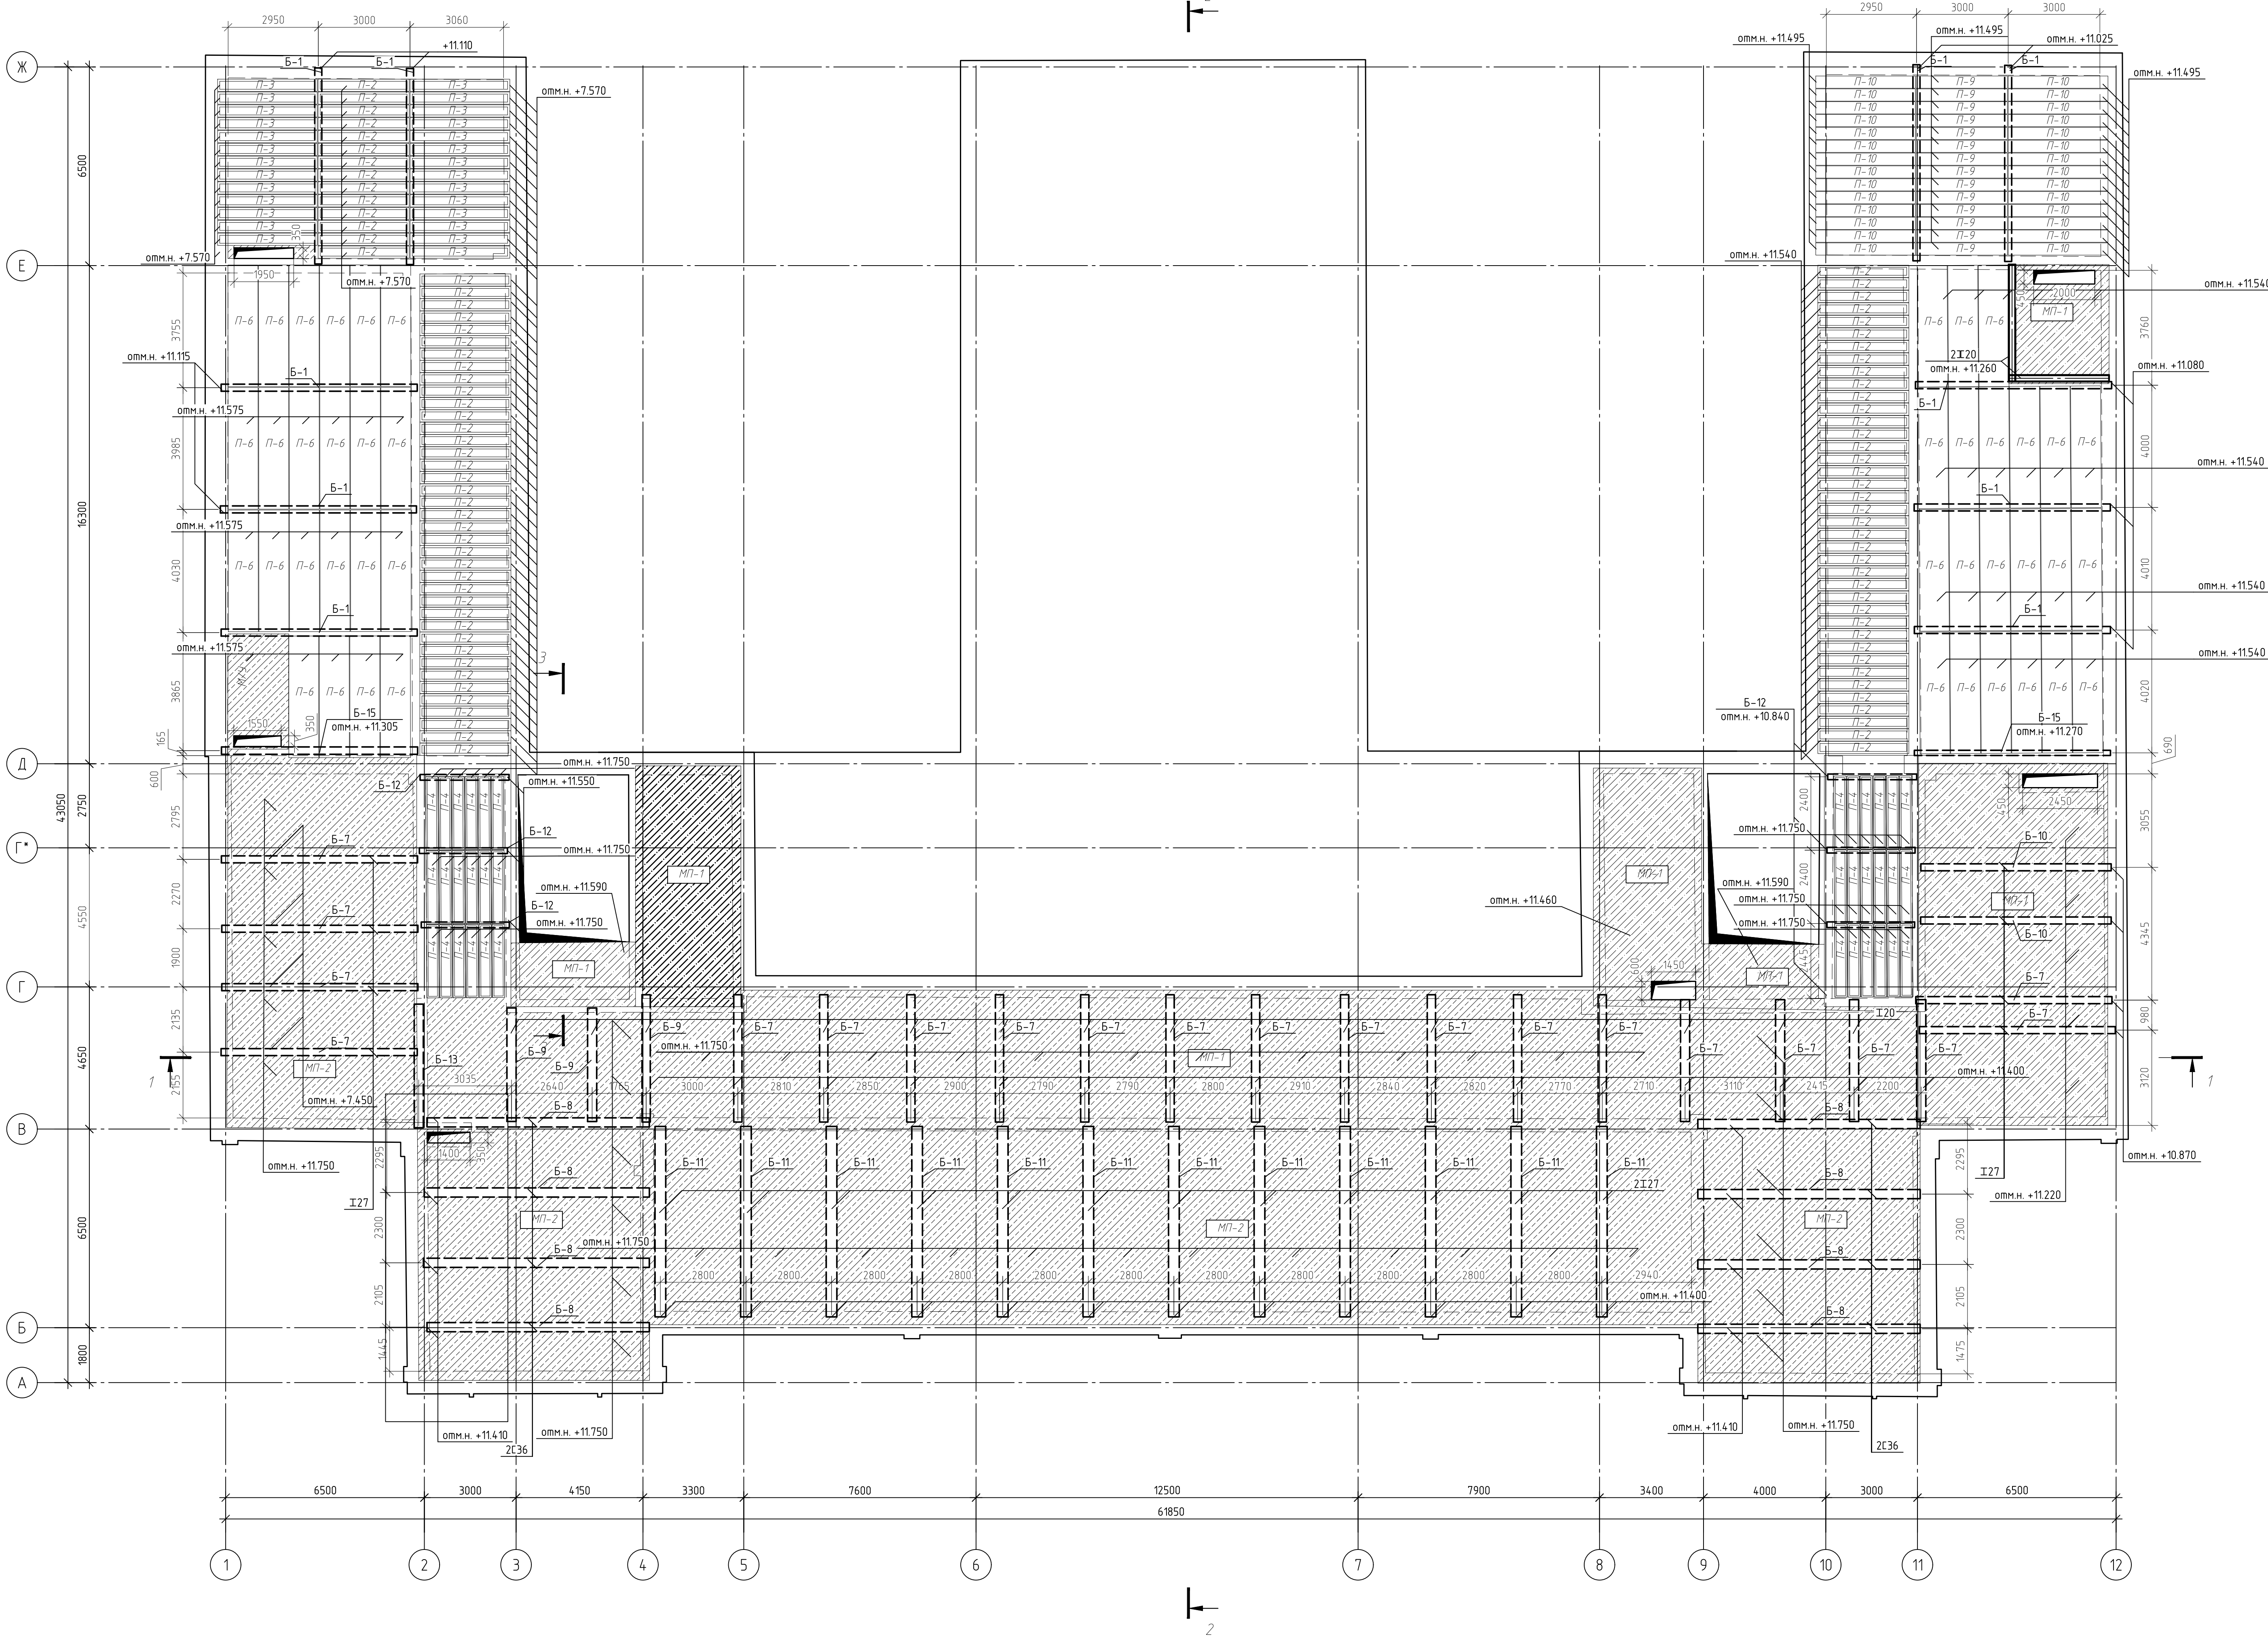

				696/П-24-АНО/ТЭК				
				"Капитальный ремонт Государственного бюджетного образовательного учреждения города Москвы "Школа №1292" (секции №1 по адресу: г. Москва, ул. Баболова, д.1, корпус 11"				
Изм.	Взм.	Лист	М.в.	Изд.	Дата	Комплект чертежей по результатам одобрения работ фасадов и внутренних помещений спортивной секции на зенитного скандинавия	Лист	
Разработ	С.П.Павлов	1/24	12.12.23	1/24	12.12.23			
Проектиров	Зеленцов	2/24	12.12.23	2/24	12.12.23			
ГИП	Емельянов	3/24	12.12.23	3/24	12.12.23			
Утвердил	Шаранков	4/24	12.12.23	4/24	12.12.23	План перекрытия 3-го этажа		
Н.инж.	Шаранков	5/24	12.12.23	5/24	12.12.23	М 1:100		
				ООО "Аркан"				
				Формат А0				


Free-body diagram of the left block (mass 2). A horizontal arrow labeled N points to the right, representing the normal force exerted by the right block.

П-1	- ж/б ребристая плита перекрытия 2,080x4,0x15 мм.
П-2	- ж/б ребристая плита перекрытия 2,980x4,0x12 мм.
П-3	- ж/б ребристая плита перекрытия 2,280x4,0x12 мм.
П-4	- ж/б ребристая плита перекрытия 2,400x4,0x12 мм.
П-5	- ж/б многослойная плита перекрытия 4,78x0,98x0,12
П-6	- ж/б многослойная плита перекрытия 3,98x0,98x0,12
П-7	- ж/б ребристая плита перекрытия 1,48x0,4x0,15 мм.
П-8	- ж/б ребристая плита перекрытия 2,80x4,0x15 мм.
П-9	- ж/б ребристая плита перекрытия 2,980x4,0x15 мм.
П-10	- ж/б ребристая плита перекрытия 3,28x4,0x15 мм.
П-11	- ж/б многослойная плита перекрытия 3,58x0,98x0,12
П-12	- ж/б ребристая плита перекрытия 3,80x4,0x15 мм.
П-13	- ж/б ребристая плита перекрытия 3,58x4,0x15 мм.


М/У – монолитный участок перекрытия 80 мм;

Б-1	- сборная железобетонная балка сечением 230х460(п) мм;
Б-2	- металлическая балка сечением $\text{I} 20$ по ГОСТ 16-1932 (общий размер сечения 300х270(п) мм);
Б-3	- металлическая балка сечением $\text{I} 14$ по ГОСТ 16-1932;
Б-4	- металлическая балка сечением $\text{I} 30a$ по ГОСТ 16-1932;
Б-5	- сталежелезобетонная балка сечением 250х270(п) мм;
Б-6	- сталежелезобетонная балка сечением 250х280(п) мм;
Б-7	- сталежелезобетонная балка сечением 250х350(п) мм;
Б-8	- сталежелезобетонная балка сечением 300х340(п) мм;
Б-9	- сталежелезобетонная балка сечением 300х350(п) мм;
Б-10	- сталежелезобетонная балка сечением 410х350(п) мм;
Б-11	- сталежелезобетонная балка сечением 350х350 (п) мм;
Б-12	- металлическая балка сечением $\text{I} 20a$ по ГОСТ 16-1932;
Б-13	- монолитная балка с рельсами внутри, рельс 170х170 мм;
Б-14	- сталежелезобетонная балка сечением 280х350(п) мм;
Б-15	- металлическая балка сечением $\text{I} 27a$ по ГОСТ 16-1932
Б-16	- сталежелезобетонная балка сечением 230х310(п) мм;
Б-17	- рельс сечением 170х170(п) мм;
Б-18	- сталежелезобетонная сечением 470х340(п) мм;
Б-19	- $\text{I} 20$;
Б-20	- сталежелезобетонная сечением 190х220(п) мм;
Б-21	- металлическая балка из $\text{I} 36$;
Б-22	- сталежелезобетонная балка из $\text{I} 35$;

Ф-1 - Металлическая ферма.

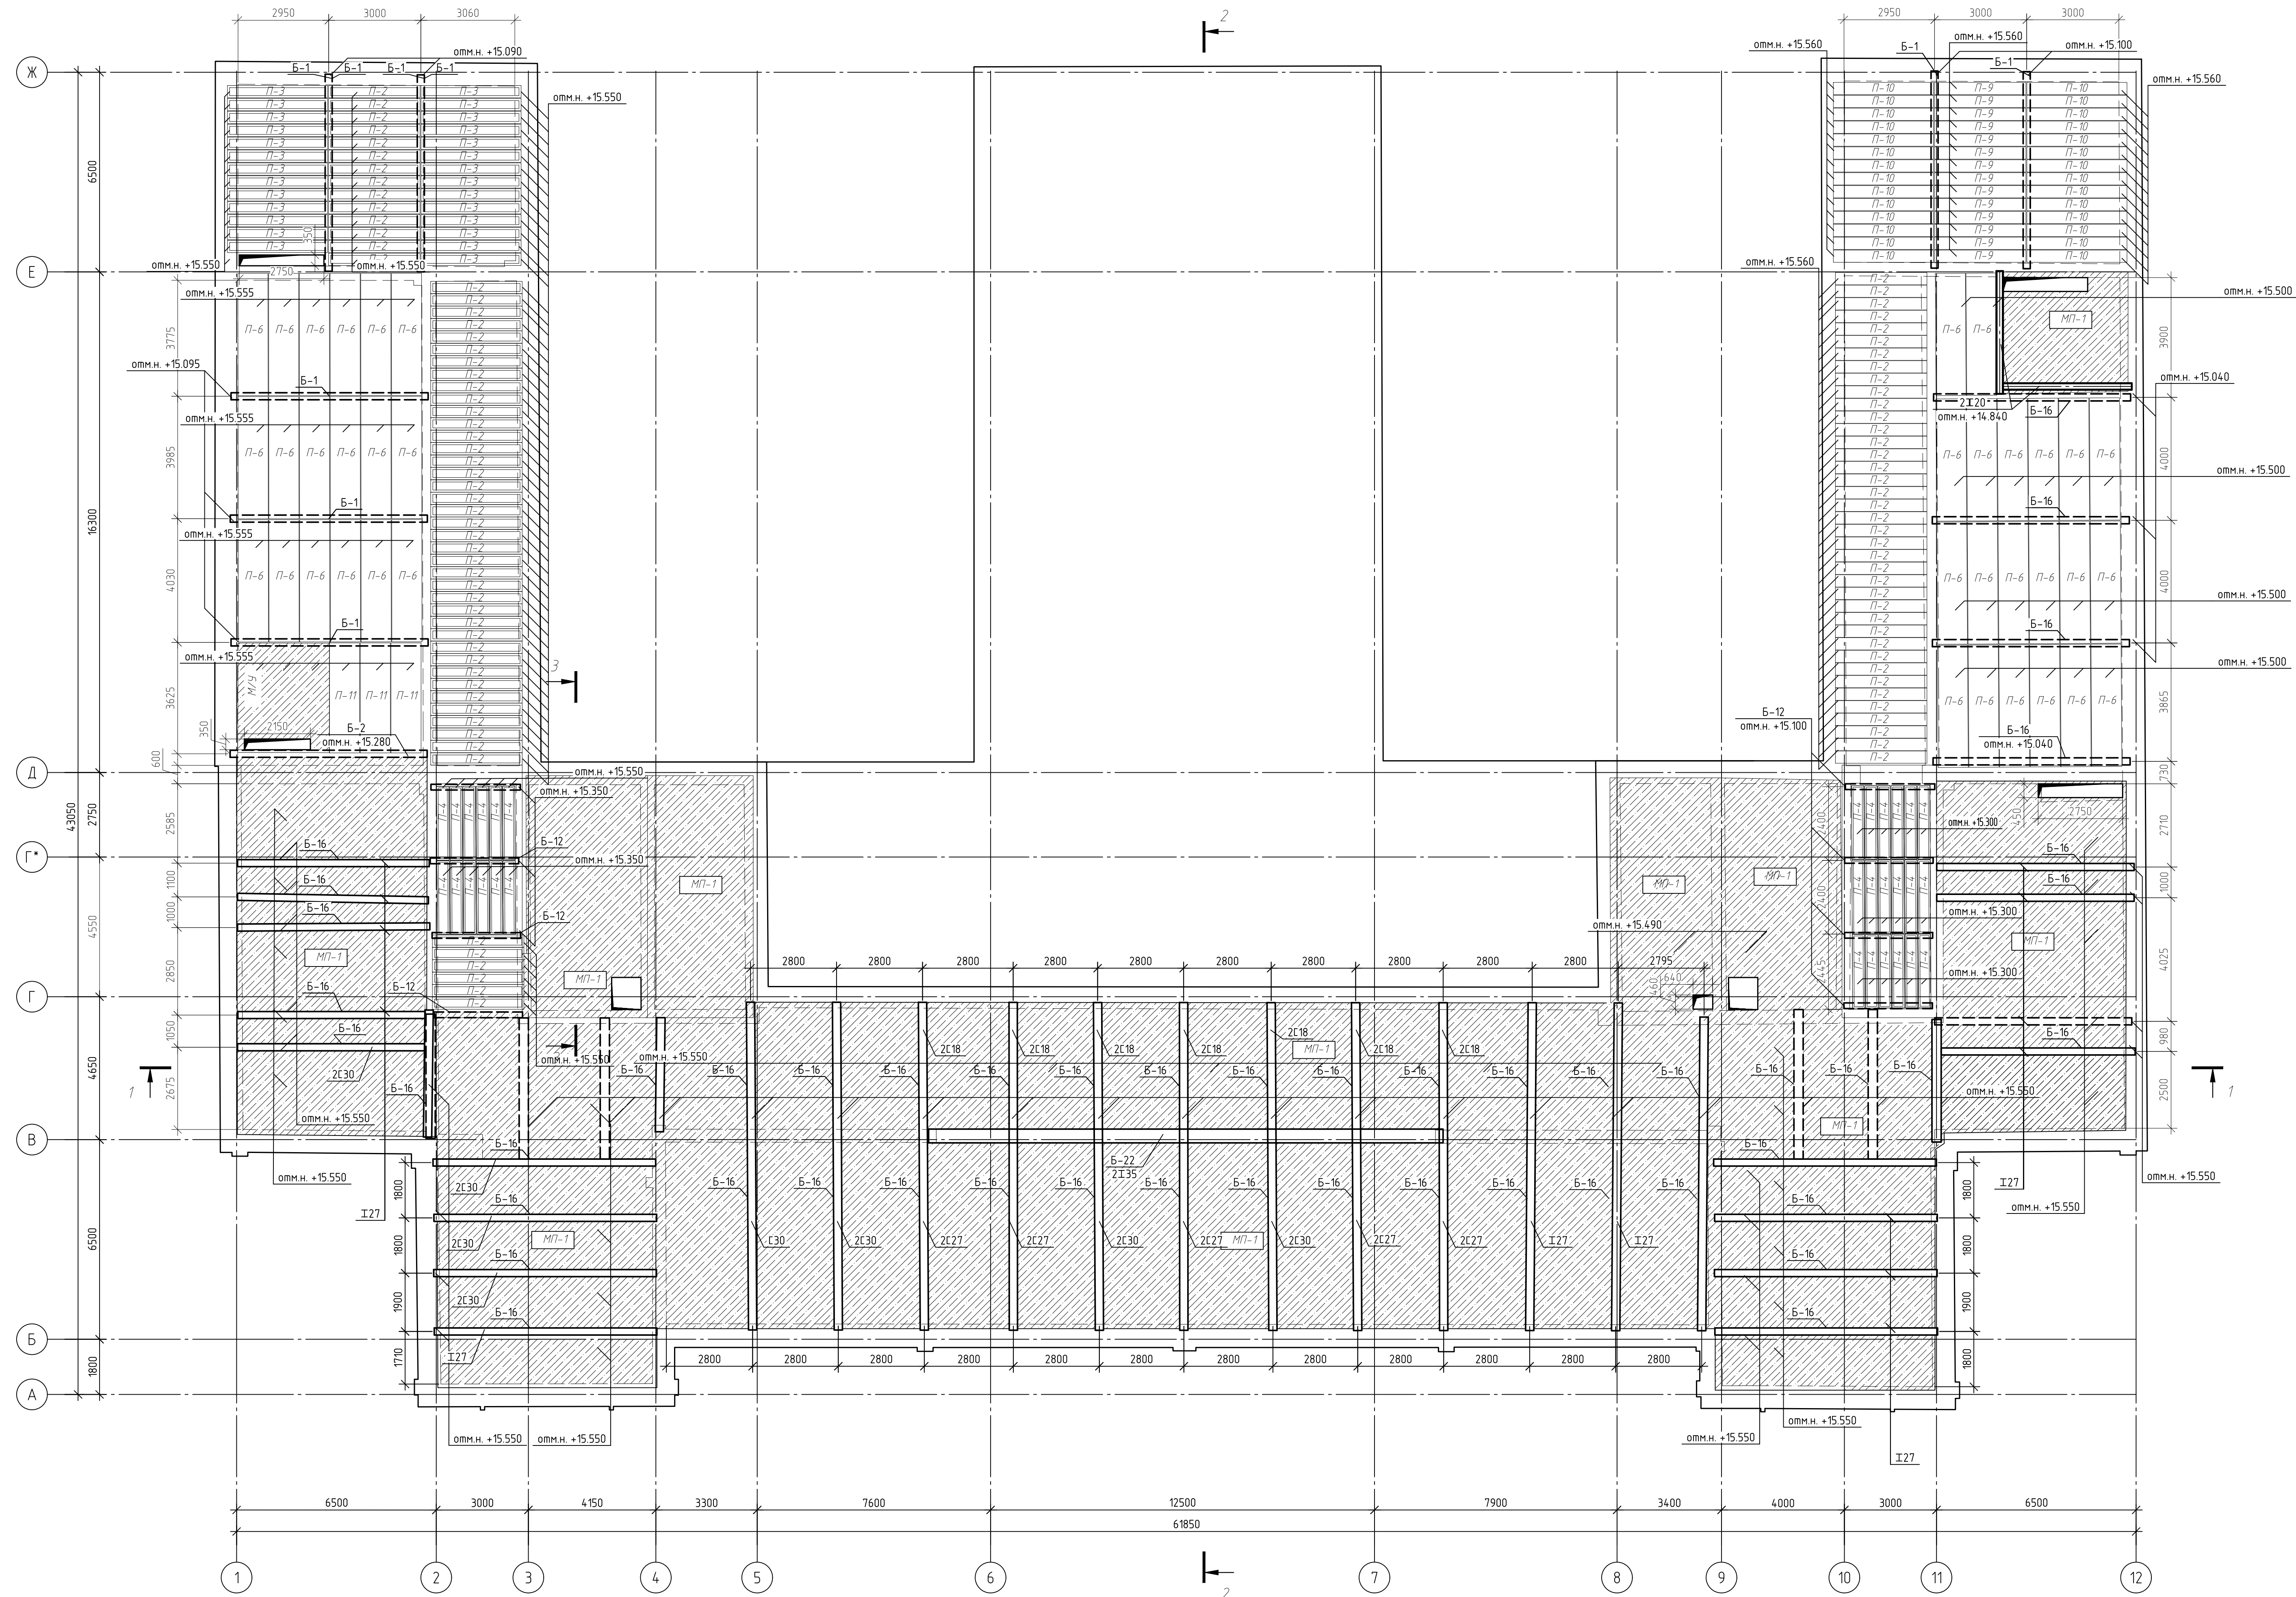[illegible]



План балок под стойки стропильной системы

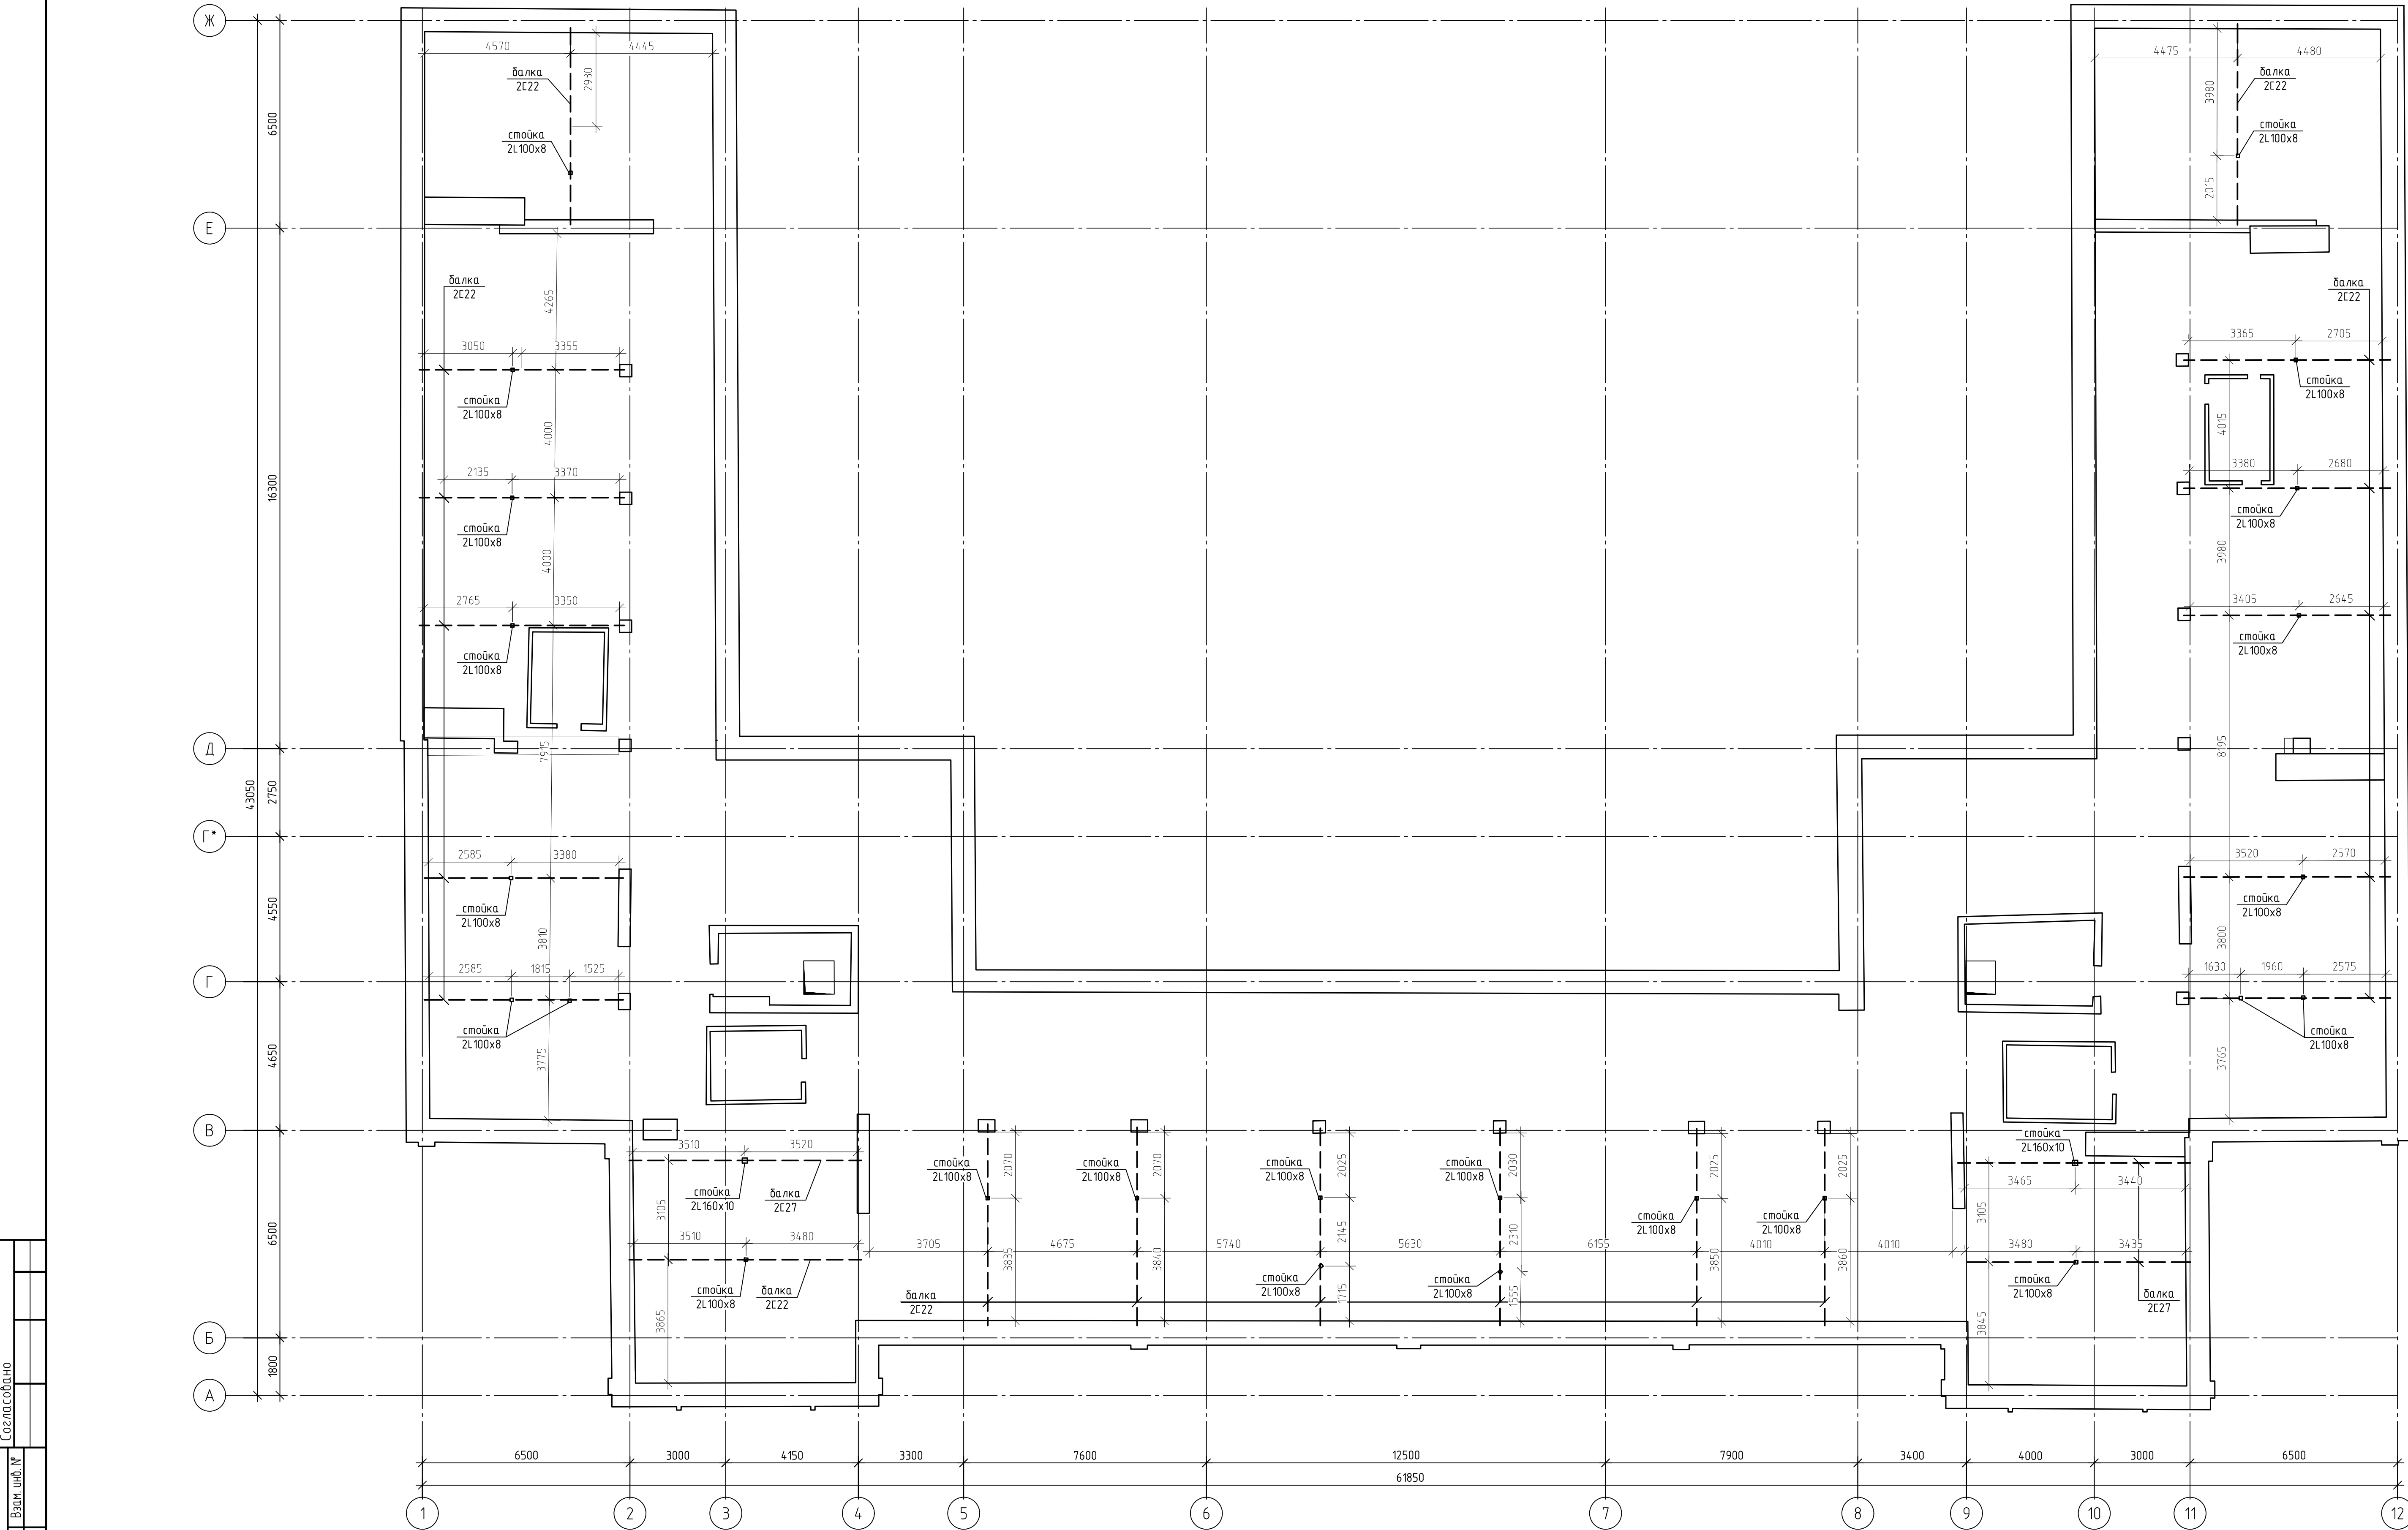

Согласовано	
Подп. и дата	Взам. инв. №
Инв. № подл.	

696/П-24-АНО/ТЭК					
"Капитальный ремонт Государственного бюджетного общеобразовательного учреждения города Москва "Школа №1282 "Сокольники" по адресу: г. Москва, ул. Барболина, д.1, корпус 1"					
Изм.	Кол. ч.	Лист	№ док.	Подп.	Дата
Разраб.	Сидарков	112L			
Проверил	Зеленцов	112L			
ГИП	Емельянов	112L			
Комплект чертежей по результатам обмерных работ фасадов и внутренних помещений сооружения методом наземного лазерного сканирования					
План балок под стойки стропильной системы					
М 1:100					
000 "Аркана"					
Формат А1					











Схема расположения конструкций покрытия

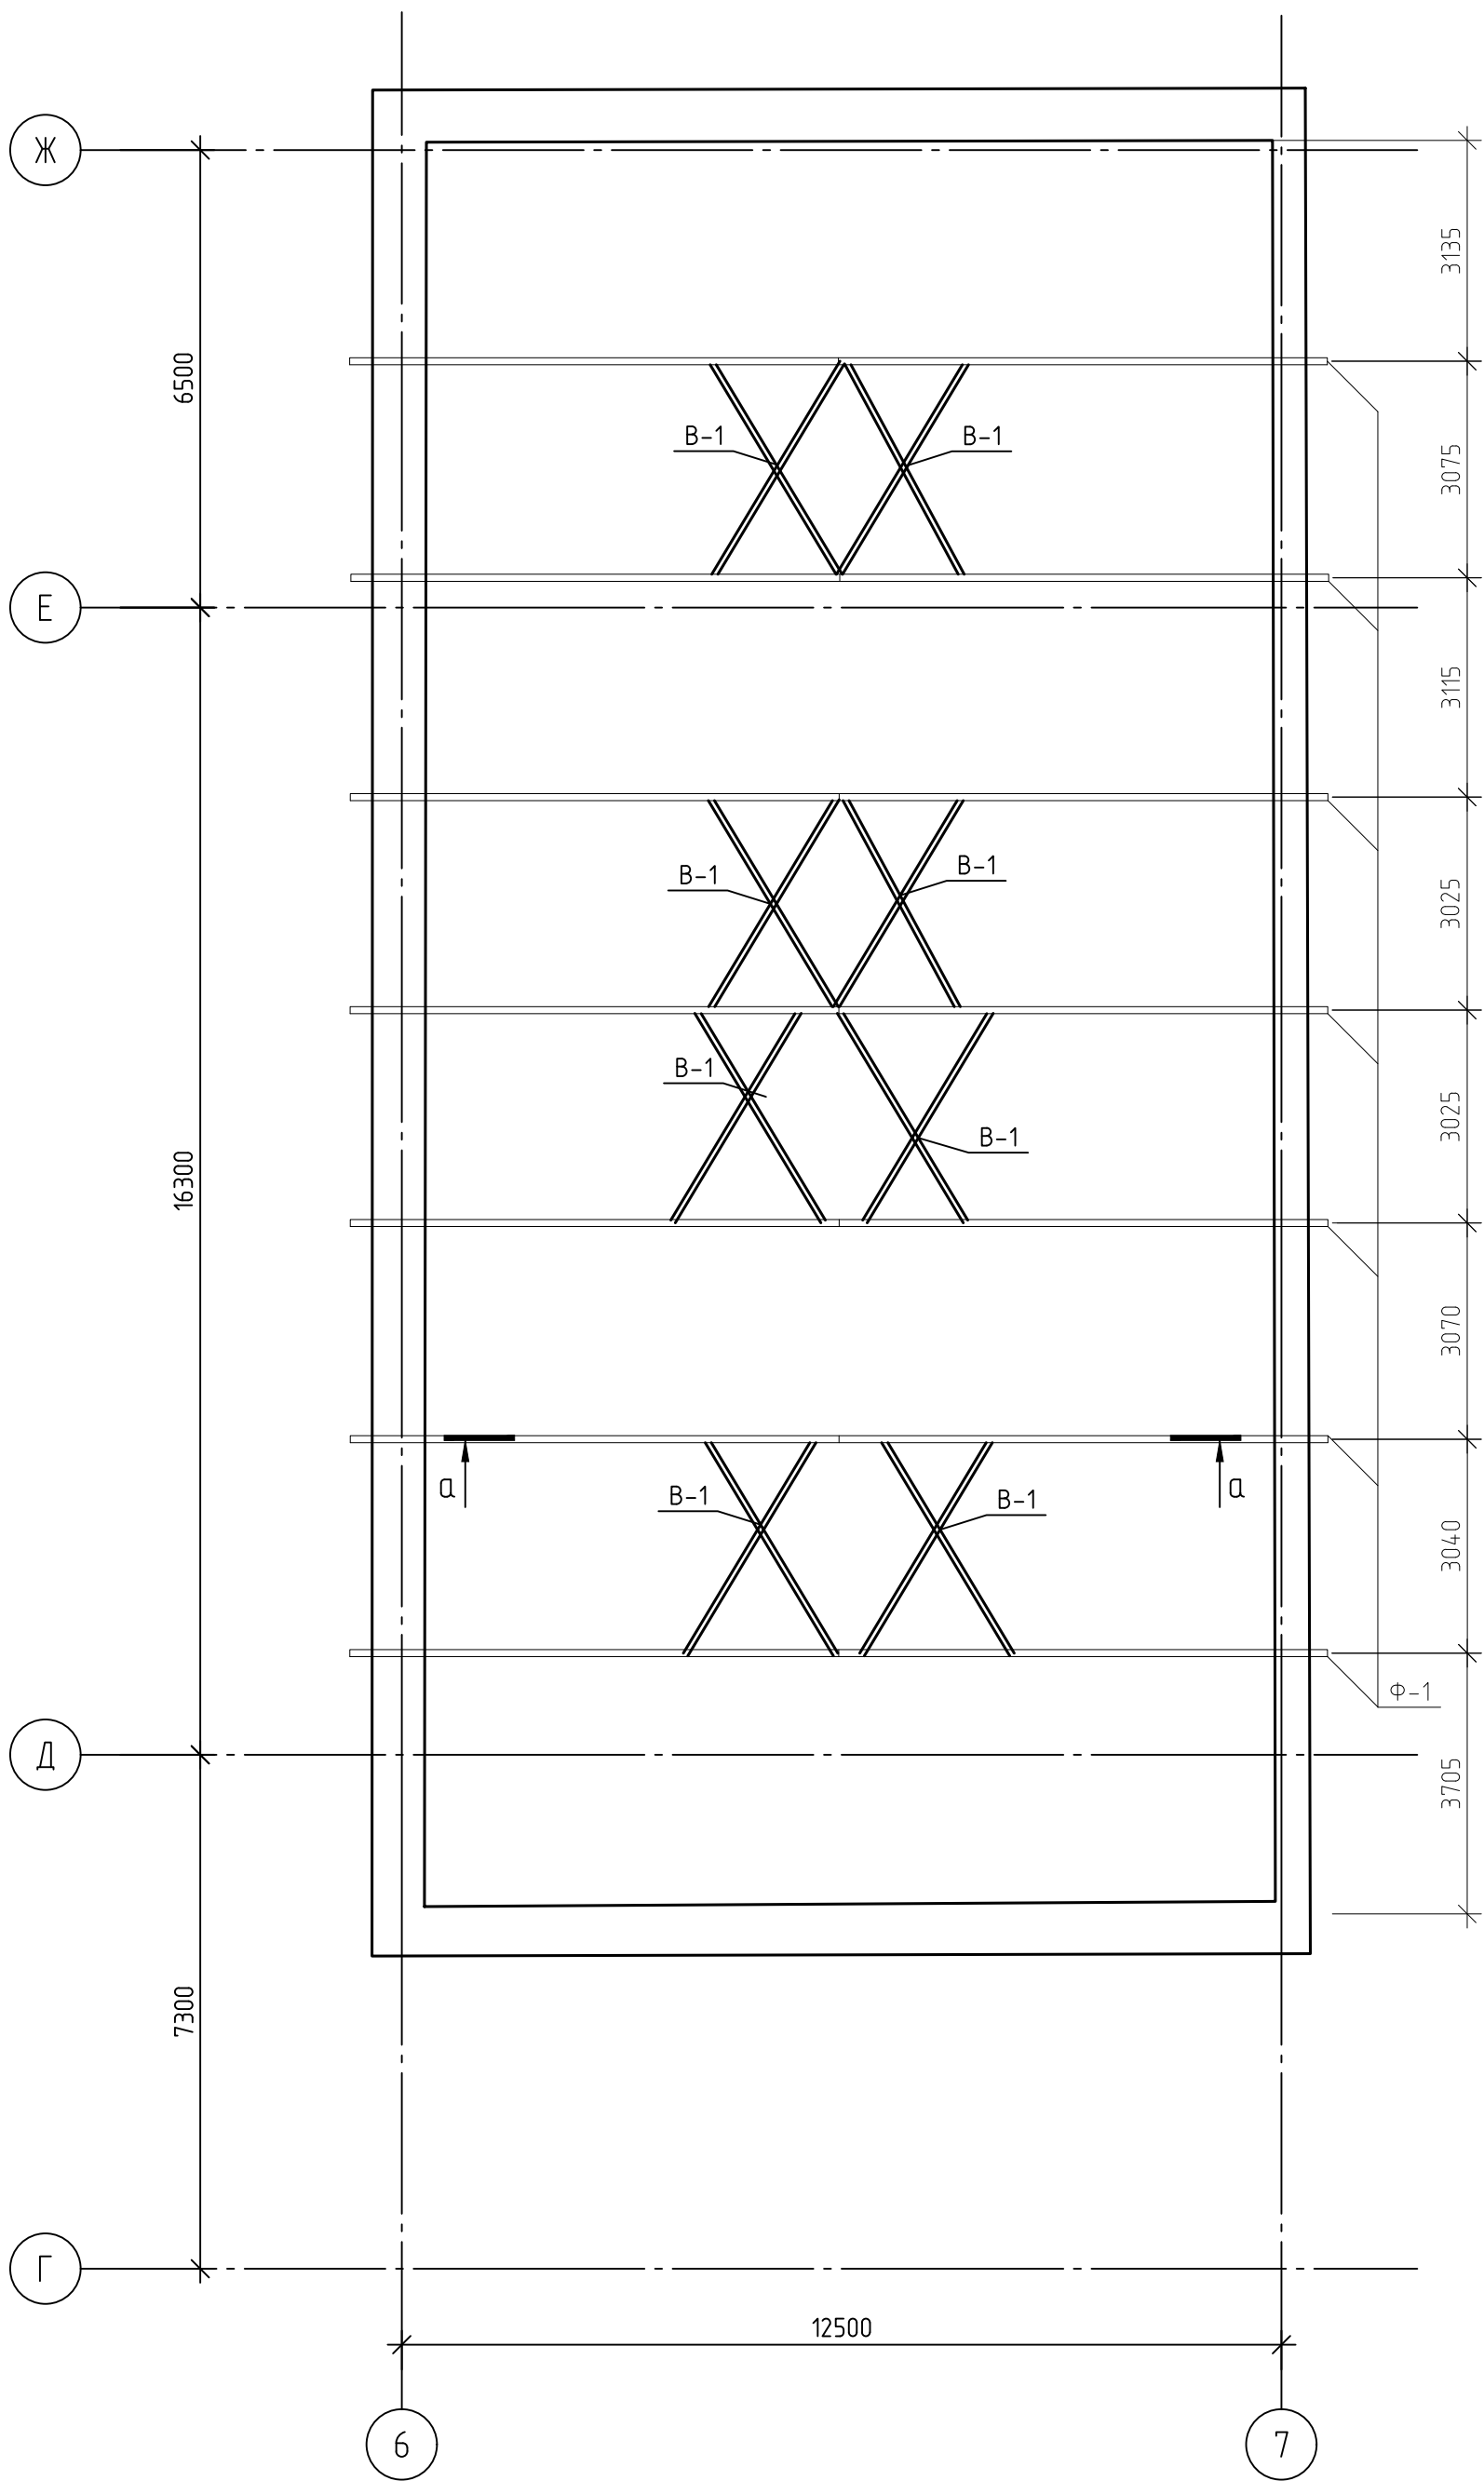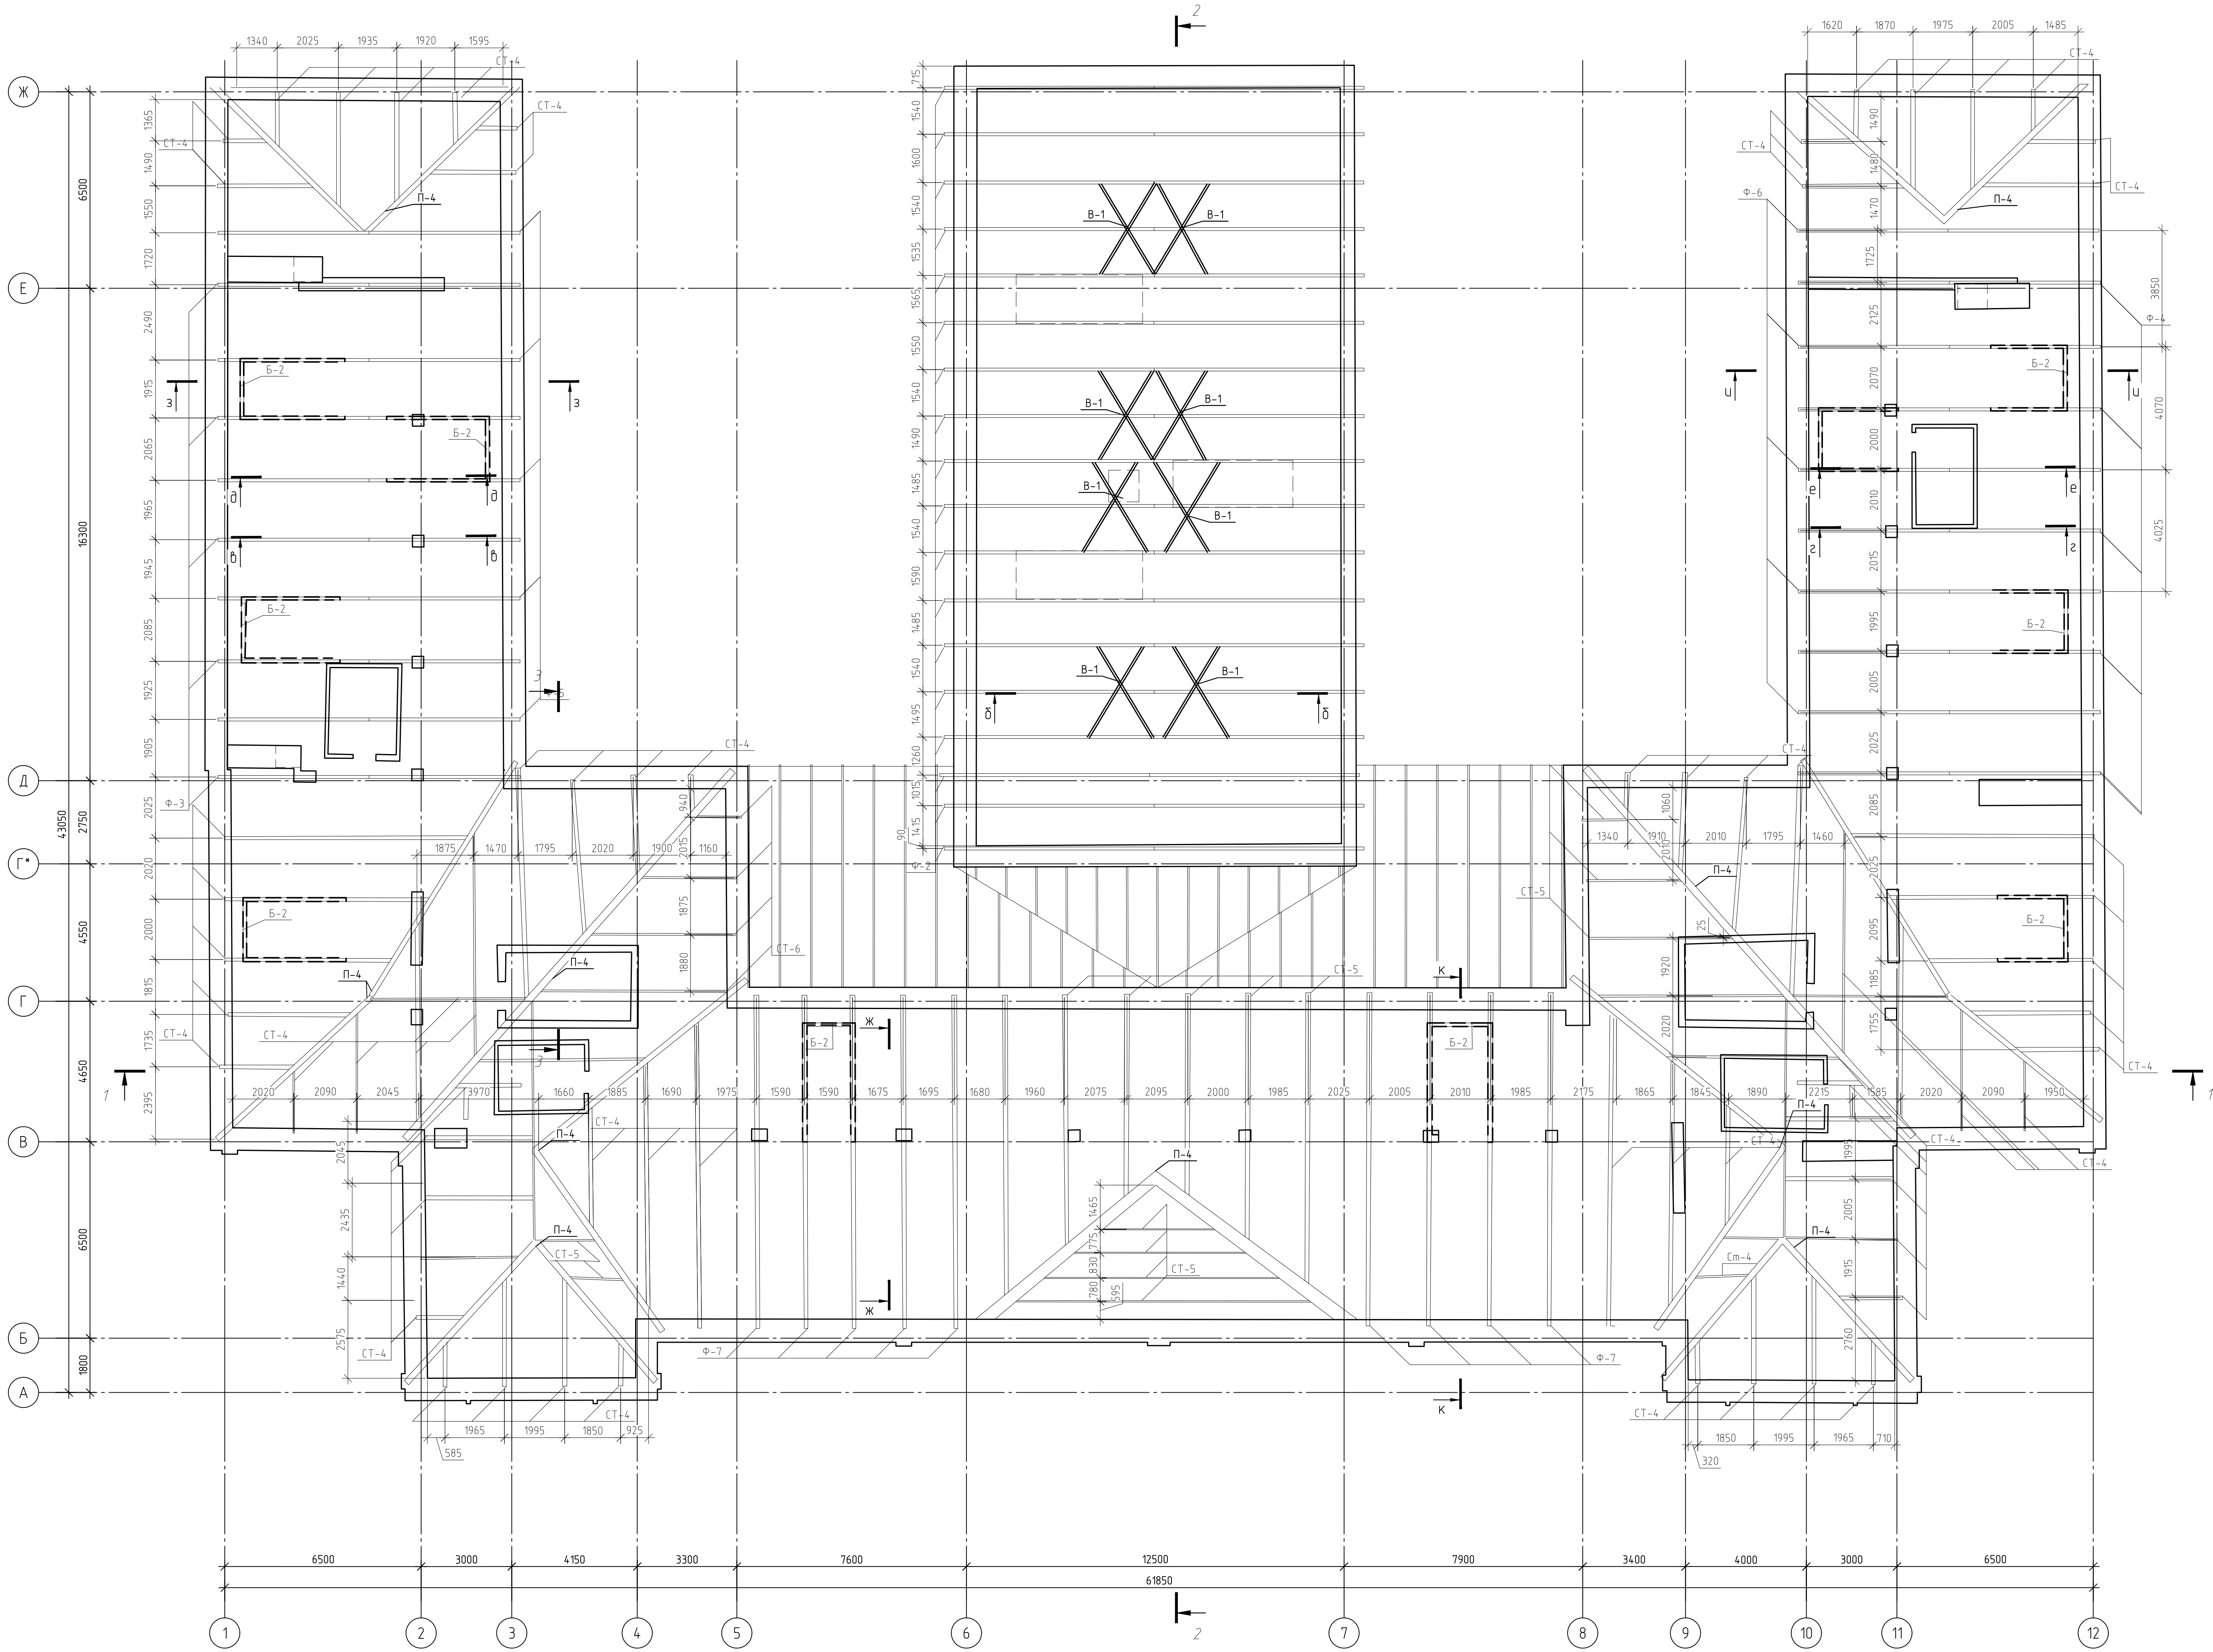



Условные обозначения

- CT-1 Обрезная доска 60х140(н)
стропильная нога
- CT-2 2х75/8
стропильная нога
- П-1 Обрезная доска 75х190(н)
Прогон
- С-1 2х75/8
Стяжка
- П-2 2х75/8
Полоса
- Б-1 I 20
Балка
- Б-2 I 16
Балка
- Б-3 I 16
Балка
- CT-3 стропильная нога
- П-3 I 20х100х75х12
прогон
- С-2 I 10
Стяжка
- О-1 Обрезная доска 50х45(н)
Обрешетка
- CT-4 I 10
стропильная нога
- CT-5 I 16
стропильная нога
- П-4 I 20
коньковый прогон
- CT-6 I 20
стропильная нога
- 1 - опорная стальная пластина с пяткой 250х250х5мм
- 2 - бетонная подушка 250(н)х300х300мм

— сплюснутое окно с толщиной стенки 140 мм, оштукатурено и окрашено с двух сторон

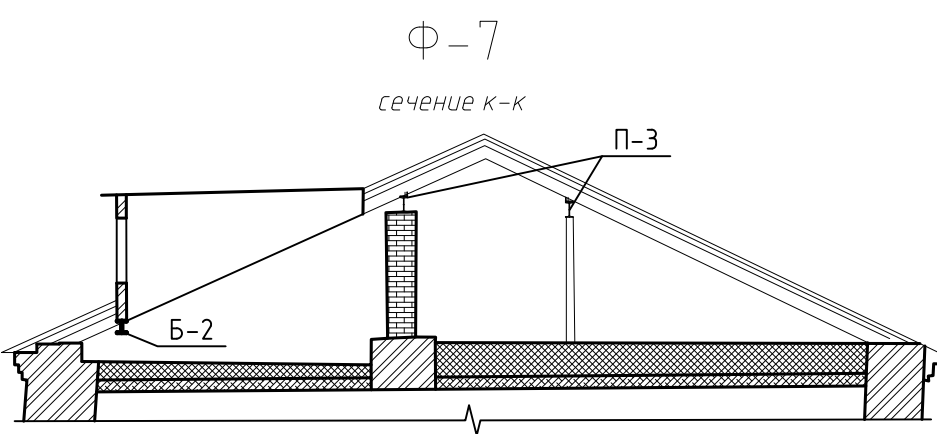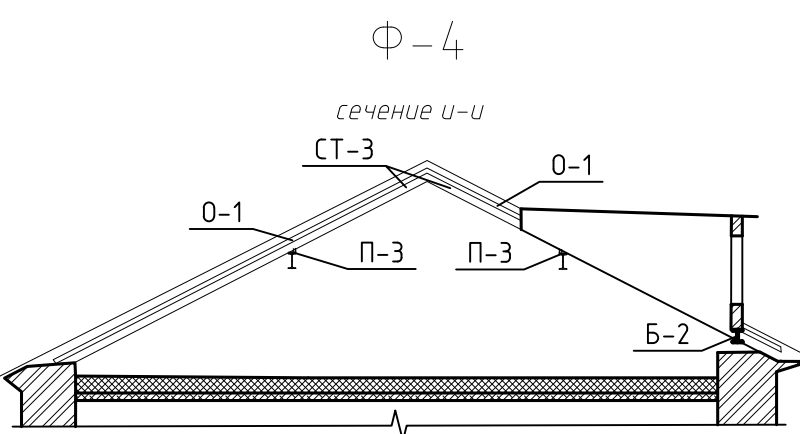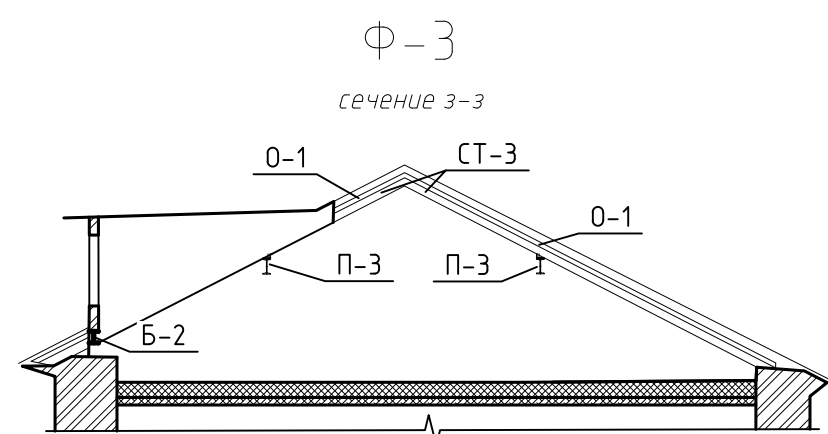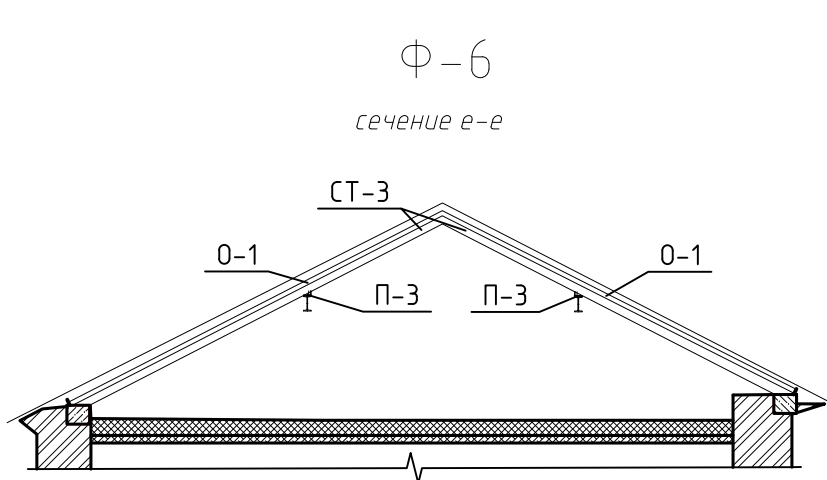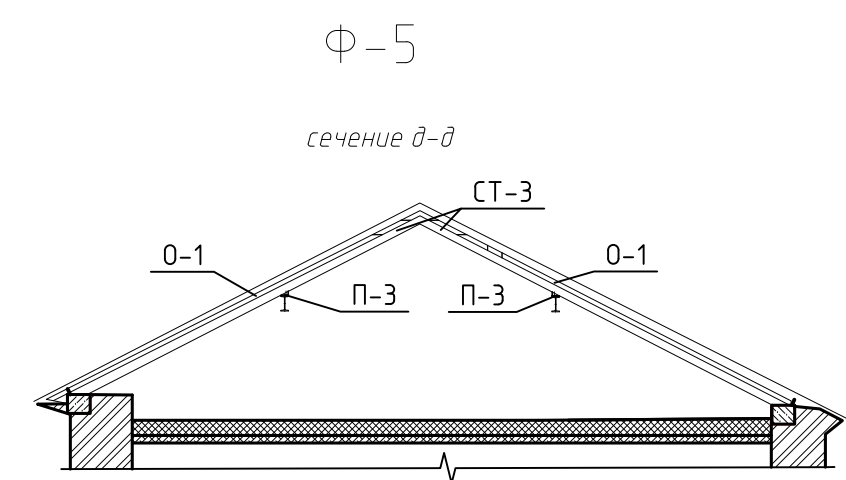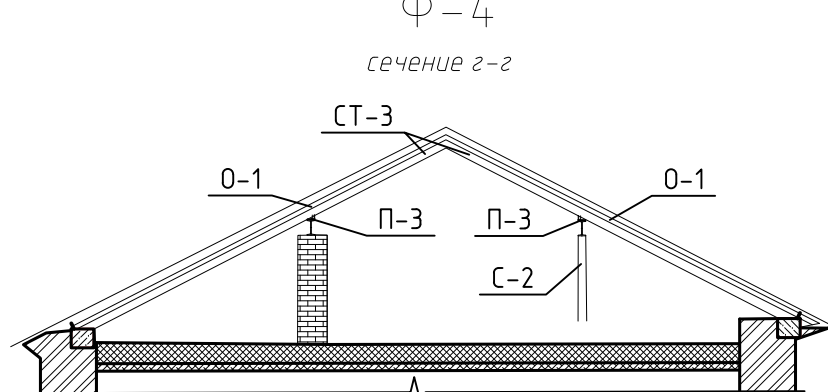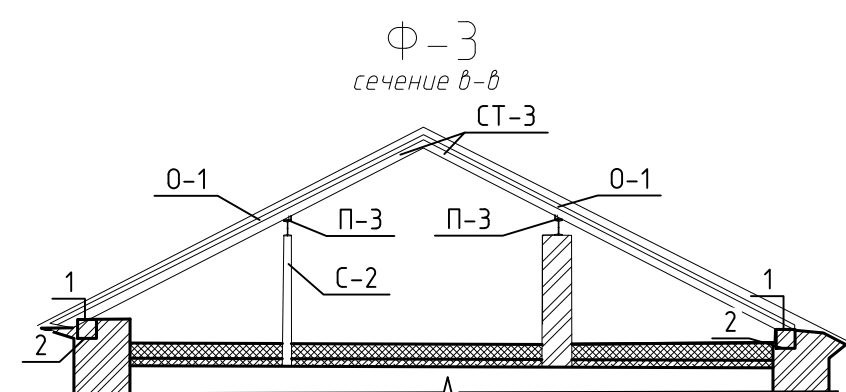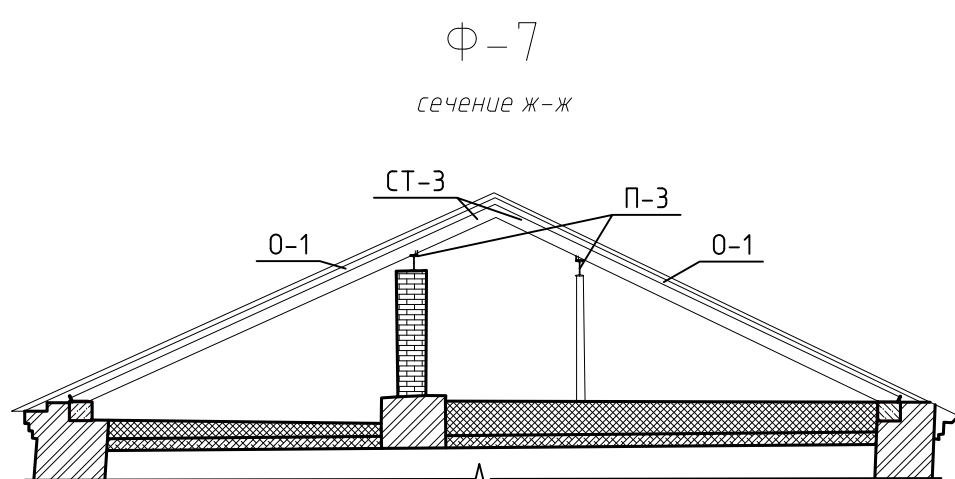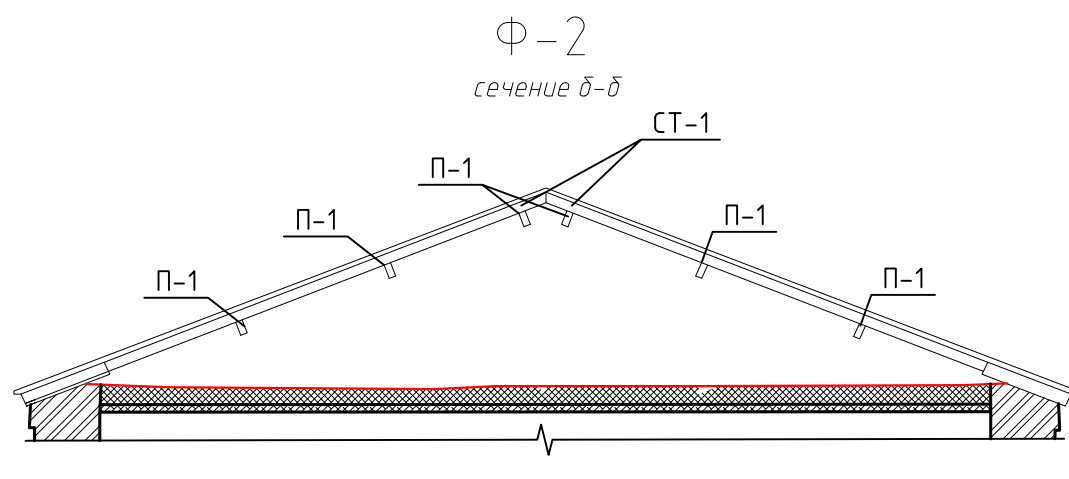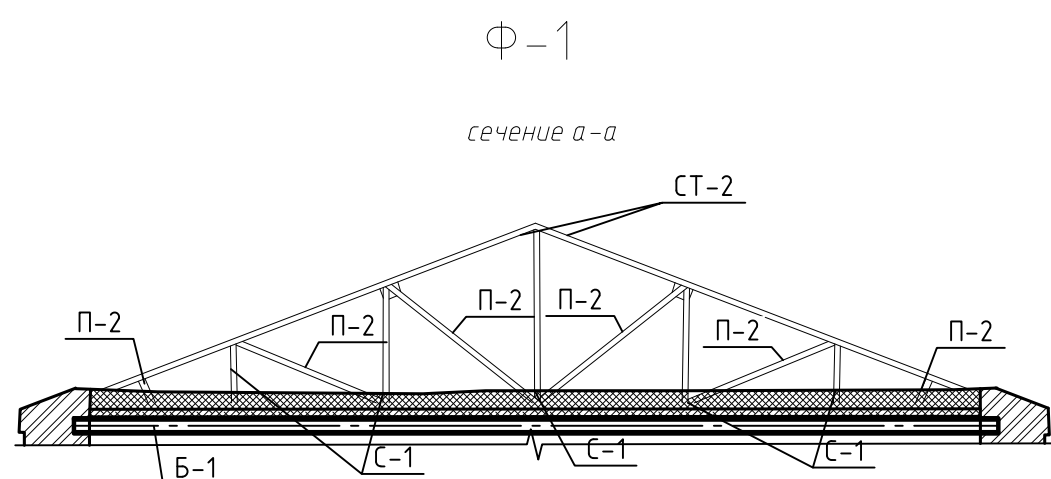

696/П-24-АНО/ТЗК					
"Жилищный отдел" Государственного бюджетного учреждения жилищного управления города Москвы "Центр №1282" (составили) по адресу: г. Москва, ул. Бородинская, д.1, корпус 11					
Изм.	Взм.	Лист	Изм.	Лист	Лист
Разработ	С.П.Павлов	1/24	Конструктор	А.В.Павлов	1/24
Проектиров	Е.В.Павлов	1/24	Инженер	А.В.Павлов	1/24
Исполн	Е.В.Павлов	1/24	Инженер	А.В.Павлов	1/24
Проверен	А.В.Павлов	1/24	Инженер	А.В.Павлов	1/24
И.контр.	А.В.Павлов	1/24	Инженер	А.В.Павлов	1/24
Схема расположения конструкций покрытия					
М.100					
000 "Арка"					
А0					

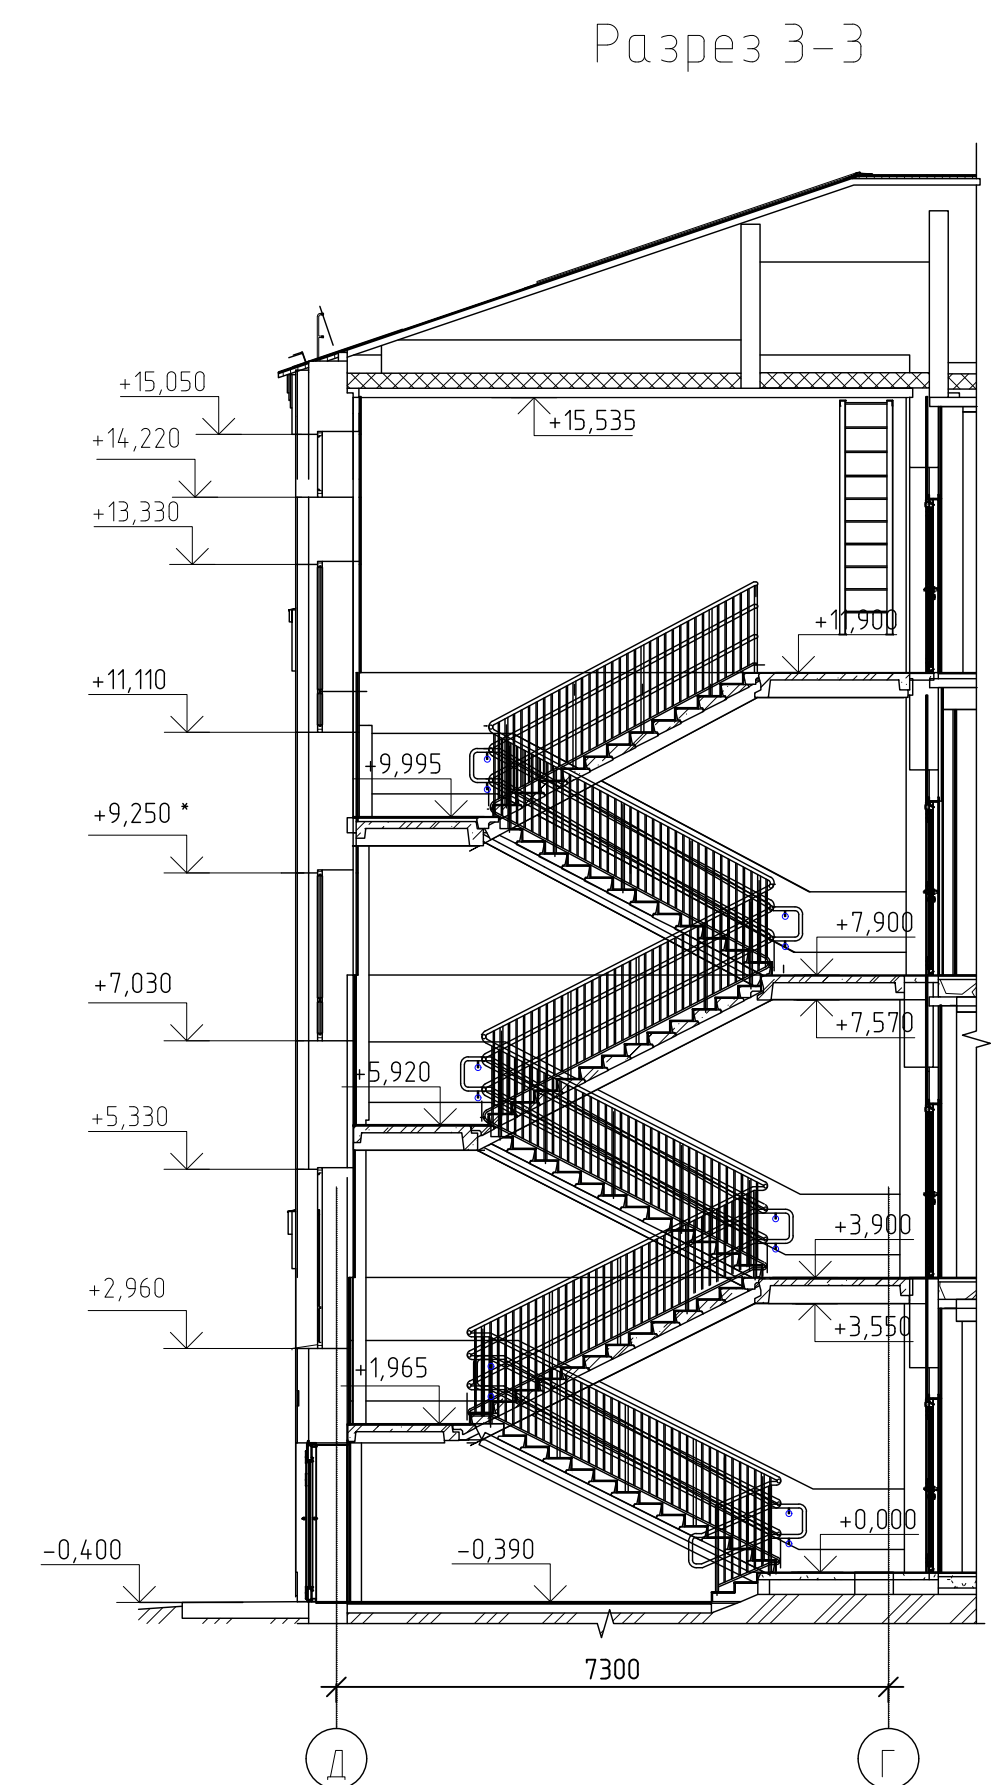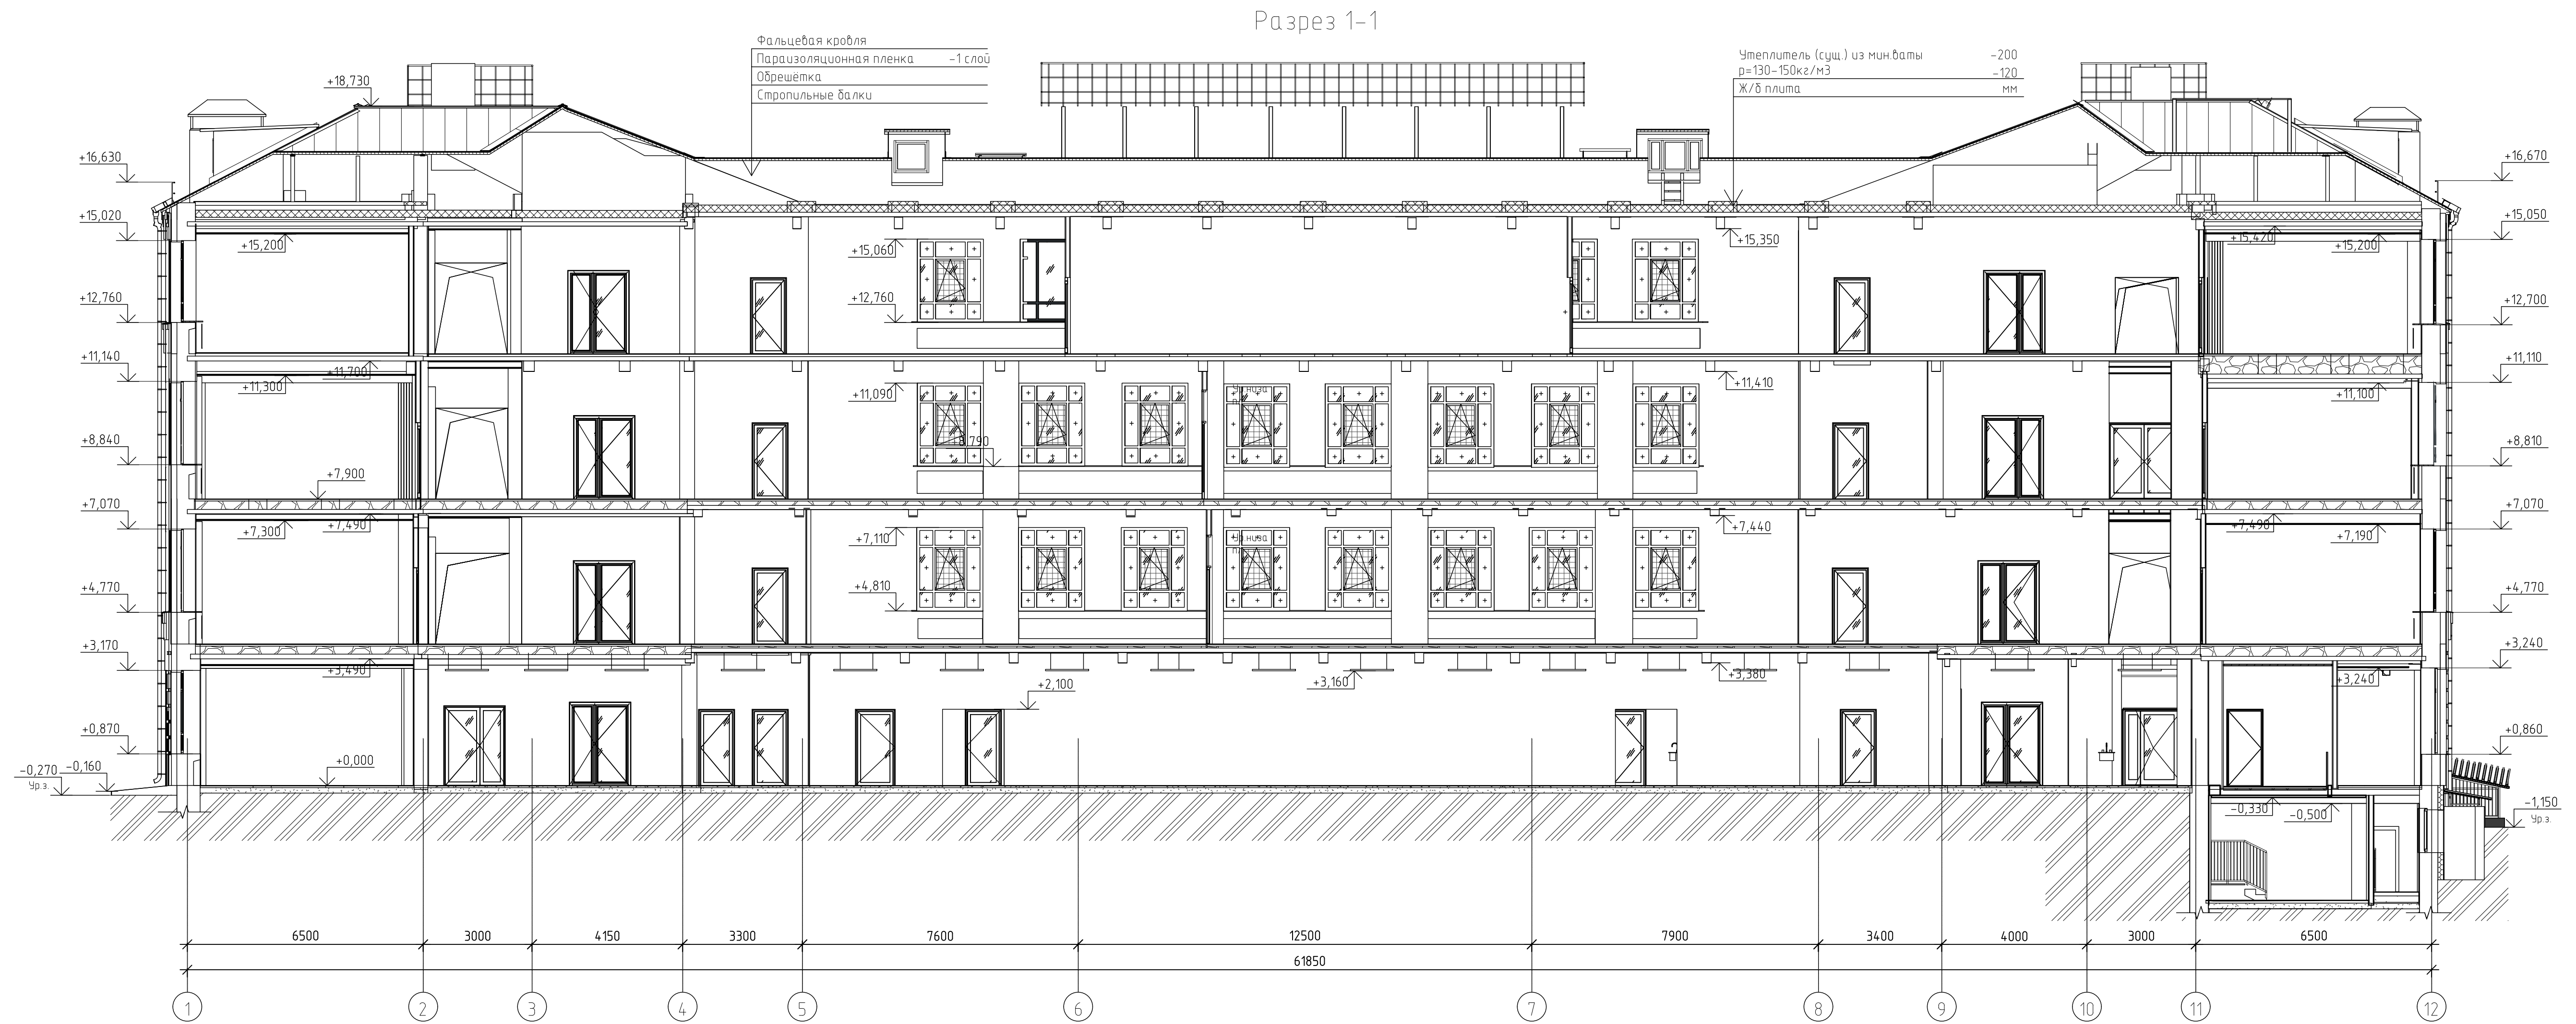

						696/П-24-АНО/ТЭК			
						"Капитальный ремонт Государственного бюджетного общеобразовательного учреждения города Москва "Школа №1282 "Сокольники" по адресу: г. Москва, ул. Барболина, д.1, корпус 1"			
Изм.	Кол.чт.	Лист	№ док.	Подп.	Дата				
Разраб.		Сидарков		<i>Сидарков</i>	1124	Комплект чертежей по результатам обмерных работ фасадов и внутренних помещений сооружения методом наземного лазерного сканирования	Стадия	Лист	Листов
Проверил		Зеленцов		<i>Зеленцов</i>	1124				
ГИП		Емельянов		<i>Емельянов</i>	1124				
Разрезы 1-1, 2-2 и 3-3									
М 1:100									
Утвердил		Цыганков		<i>Цыганков</i>	1124	000 "Аркана"			
Н. контр.		Цыганков		<i>Цыганков</i>	1124				

ПРИЛОЖЕНИЕ 11 Схемы инженерных сетей


Изм.	Кол. уч.	Лист	№ док.	Подп.	Дата	696/П-24-АНО-ТЗК	Лист
							239

Согласовано

Инв. ? подл. Подр. и зам. инв.


Ведомость чертежей		
Лист	Наименование	Примечание
1	Ведомость чертежей	
2	План подвала М1:100. Система отопления	
3	План 1 этажа М1:100. Система отопления	
4	План 2 этажа М1:100. Система отопления	
5	План 3 этажа М1:100. Система отопления	
6	План 4 этажа М1:100. Система отопления	
7	План чердака М1:100. Система отопления	
8	План подвала М1:100. Система вентиляции	
9	План 1 этажа М1:100. Система вентиляции	
10	План 2 этажа М1:100. Система вентиляции	
11	План 3 этажа М1:100. Система вентиляции	
12	План 4 этажа М1:100. Система вентиляции	
13	План кровли М1:100. Система вентиляции	
14	Характеристика отопительно–вентиляционного оборудования	
15	План подвала М1:100. Система водоснабжения	
16	План 1 этажа М1:100. Система водоснабжения	
17	План 2 этажа М1:100. Система водоснабжения	
18	План 3 этажа М1:100. Система водоснабжения	
19	План 4 этажа М1:100. Система водоснабжения	
20	План чердака М1:200. Система водоснабжения	
21	План подвала М1:100. Система водоотведения	
22	План 1 этажа М1:100. Система водоотведения	
23	План 2 этажа М1:100. Система водоотведения	
24	План 3 этажа М1:100. Система водоотведения	
25	План 4 этажа М1:100. Система водоотведения	
26	План чердака М1:100. Система водоотведения	
27	План подвала М1:100. Системы электронсабжения и слабых токов	
28	План 1 этажа М1:100. Системы электронсабжения и слабых токов	
29	План 2 этажа М1:100. Системы электронсабжения и слабых токов	
30	План 3 этажа М1:100. Системы электронсабжения и слабых токов	
31	План 4 этажа М1:100. Системы электронсабжения и слабых токов	

						696/П–24–АНО/ТЗК		
						Выполнение проектно–изыскательских работ на капитальный ремонт общеобразовательного учреждения (ГБОУ Школа №1282 "Сокольники"), по адресу: г. Москва, ул. Барболина, д. 1, стр. 1		
Изм.	Кол. уч.	Лист	?	док.	Подп.	Дата	Стадия	Лист
Разраб.	Выжигин А.В.					10.24	Обследование технического состояния строительных конструкций и инженерных систем здания	
Проверил	Зеленцов А.А.					10.24		1
ГИП	Емельянов Д.А.					10.24		31
							Ведомость чертежей	
Н. контр.	Цыганков А.А.					10.24	ООО "Аркана"	

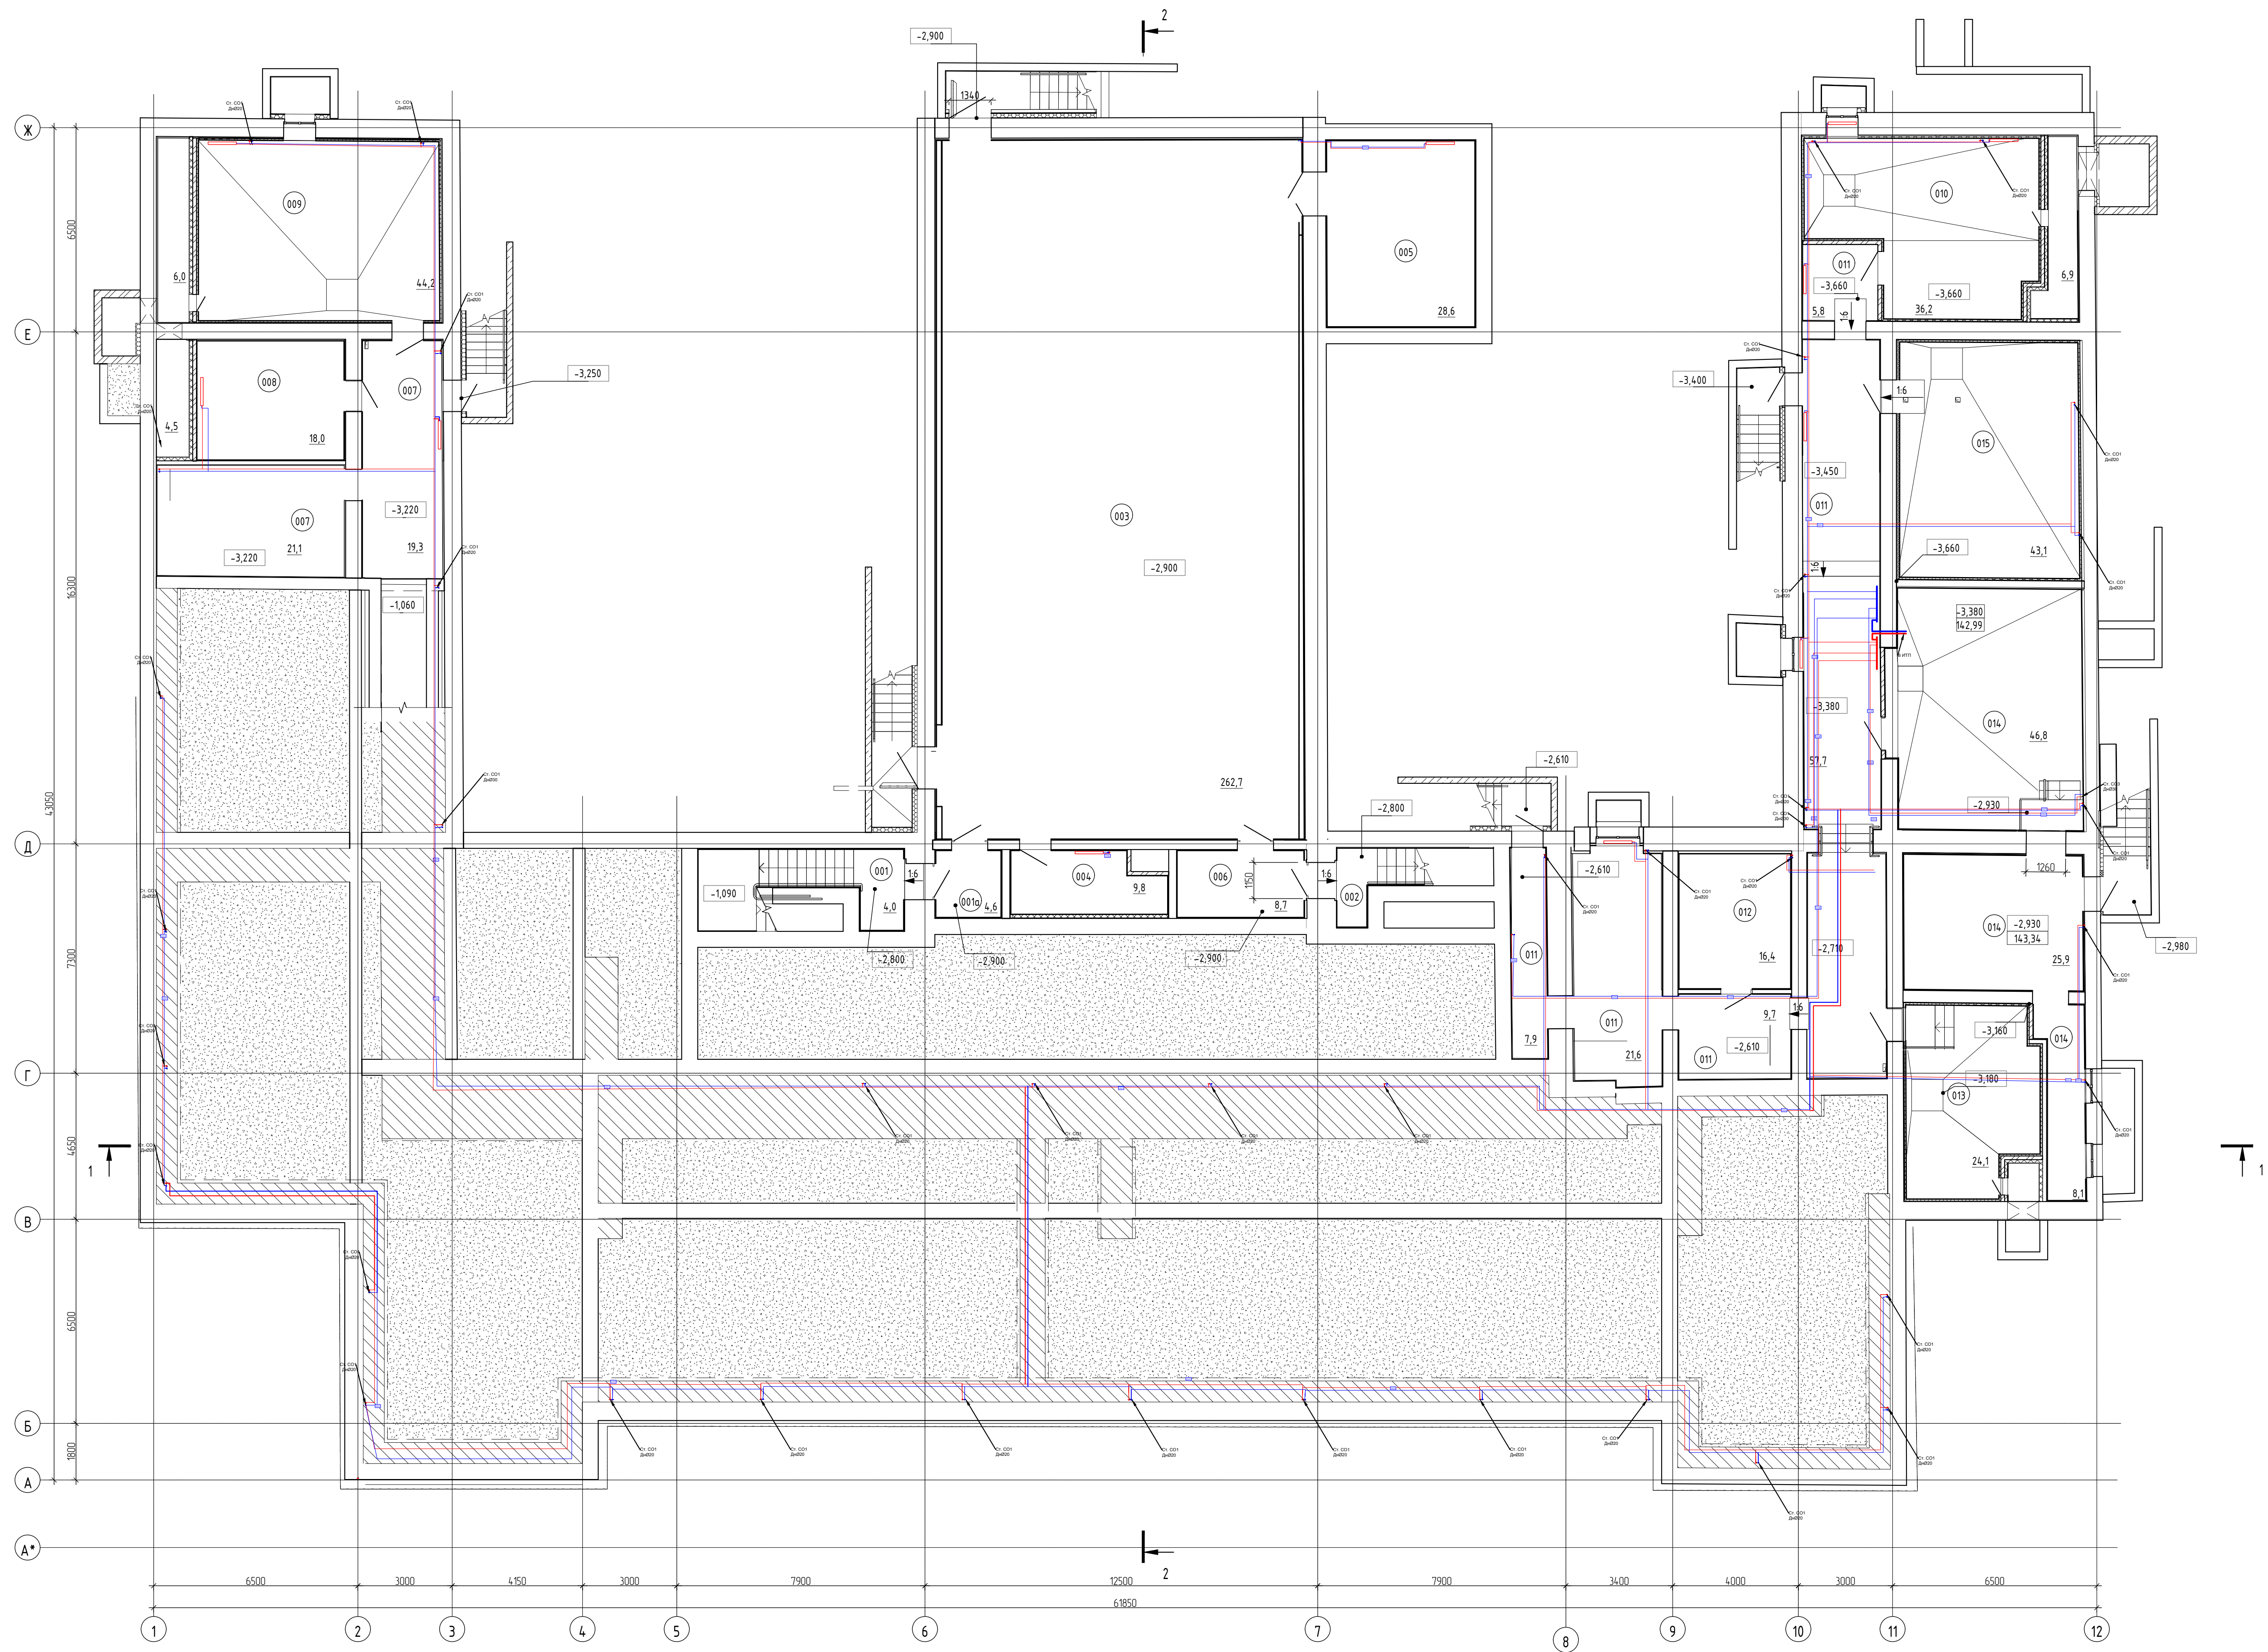

Экспликация помещений			
Номер помещения	Наименование	Площадь, м²	Кл. помещения
001	Технологическая лестница	10,1	
001а	Гранд-шлюз 1-го этажа	4,6	
002	Технологическая лестница	7,3	
003	Спортивный зал	262,7	
004	Складская	9,8	В3
005	Складская	28,6	В3
006	Гранд-шлюз 1-го этажа	6,7	
007	Коридор	40,4	
008	Кладовая	18,0	В3
009	Венткамера	44,2	В4
010	Венткамера	36,2	В4
011	Коридор	102,8	
012	Наосная	16,4	В4
013	Венткамера	24,1	В4
014	ИТП	80,8	Д
015	Венткамера	43,1	В4
		137,8	


636/П-24-АНО/ТЗК									
Выполнение проектно-изыскательских работ на капитальный ремонт общеобразовательного учреждения (ГБОУ Школа №282 "Соколиный"), по адресу: г. Москва, ул. Барбосова, д. 1, стр. 1									
Изм.	Кол.	Исполн.	Доп.	Дата	Осуществление технического сопровождения строительных и инженерных систем здания				
Разработ.	Земсков А.В.	10.24			Этапия	Пуст	Пустов		
Проверил	Земсков А.В.	10.24				2			
Гип	Емельянов А.В.	10.24							
План поэтажа М1:100. Система отопления					ООО "Аркана"				
Н. контр.	Цыганков А.В.	10.24			Формат А0				

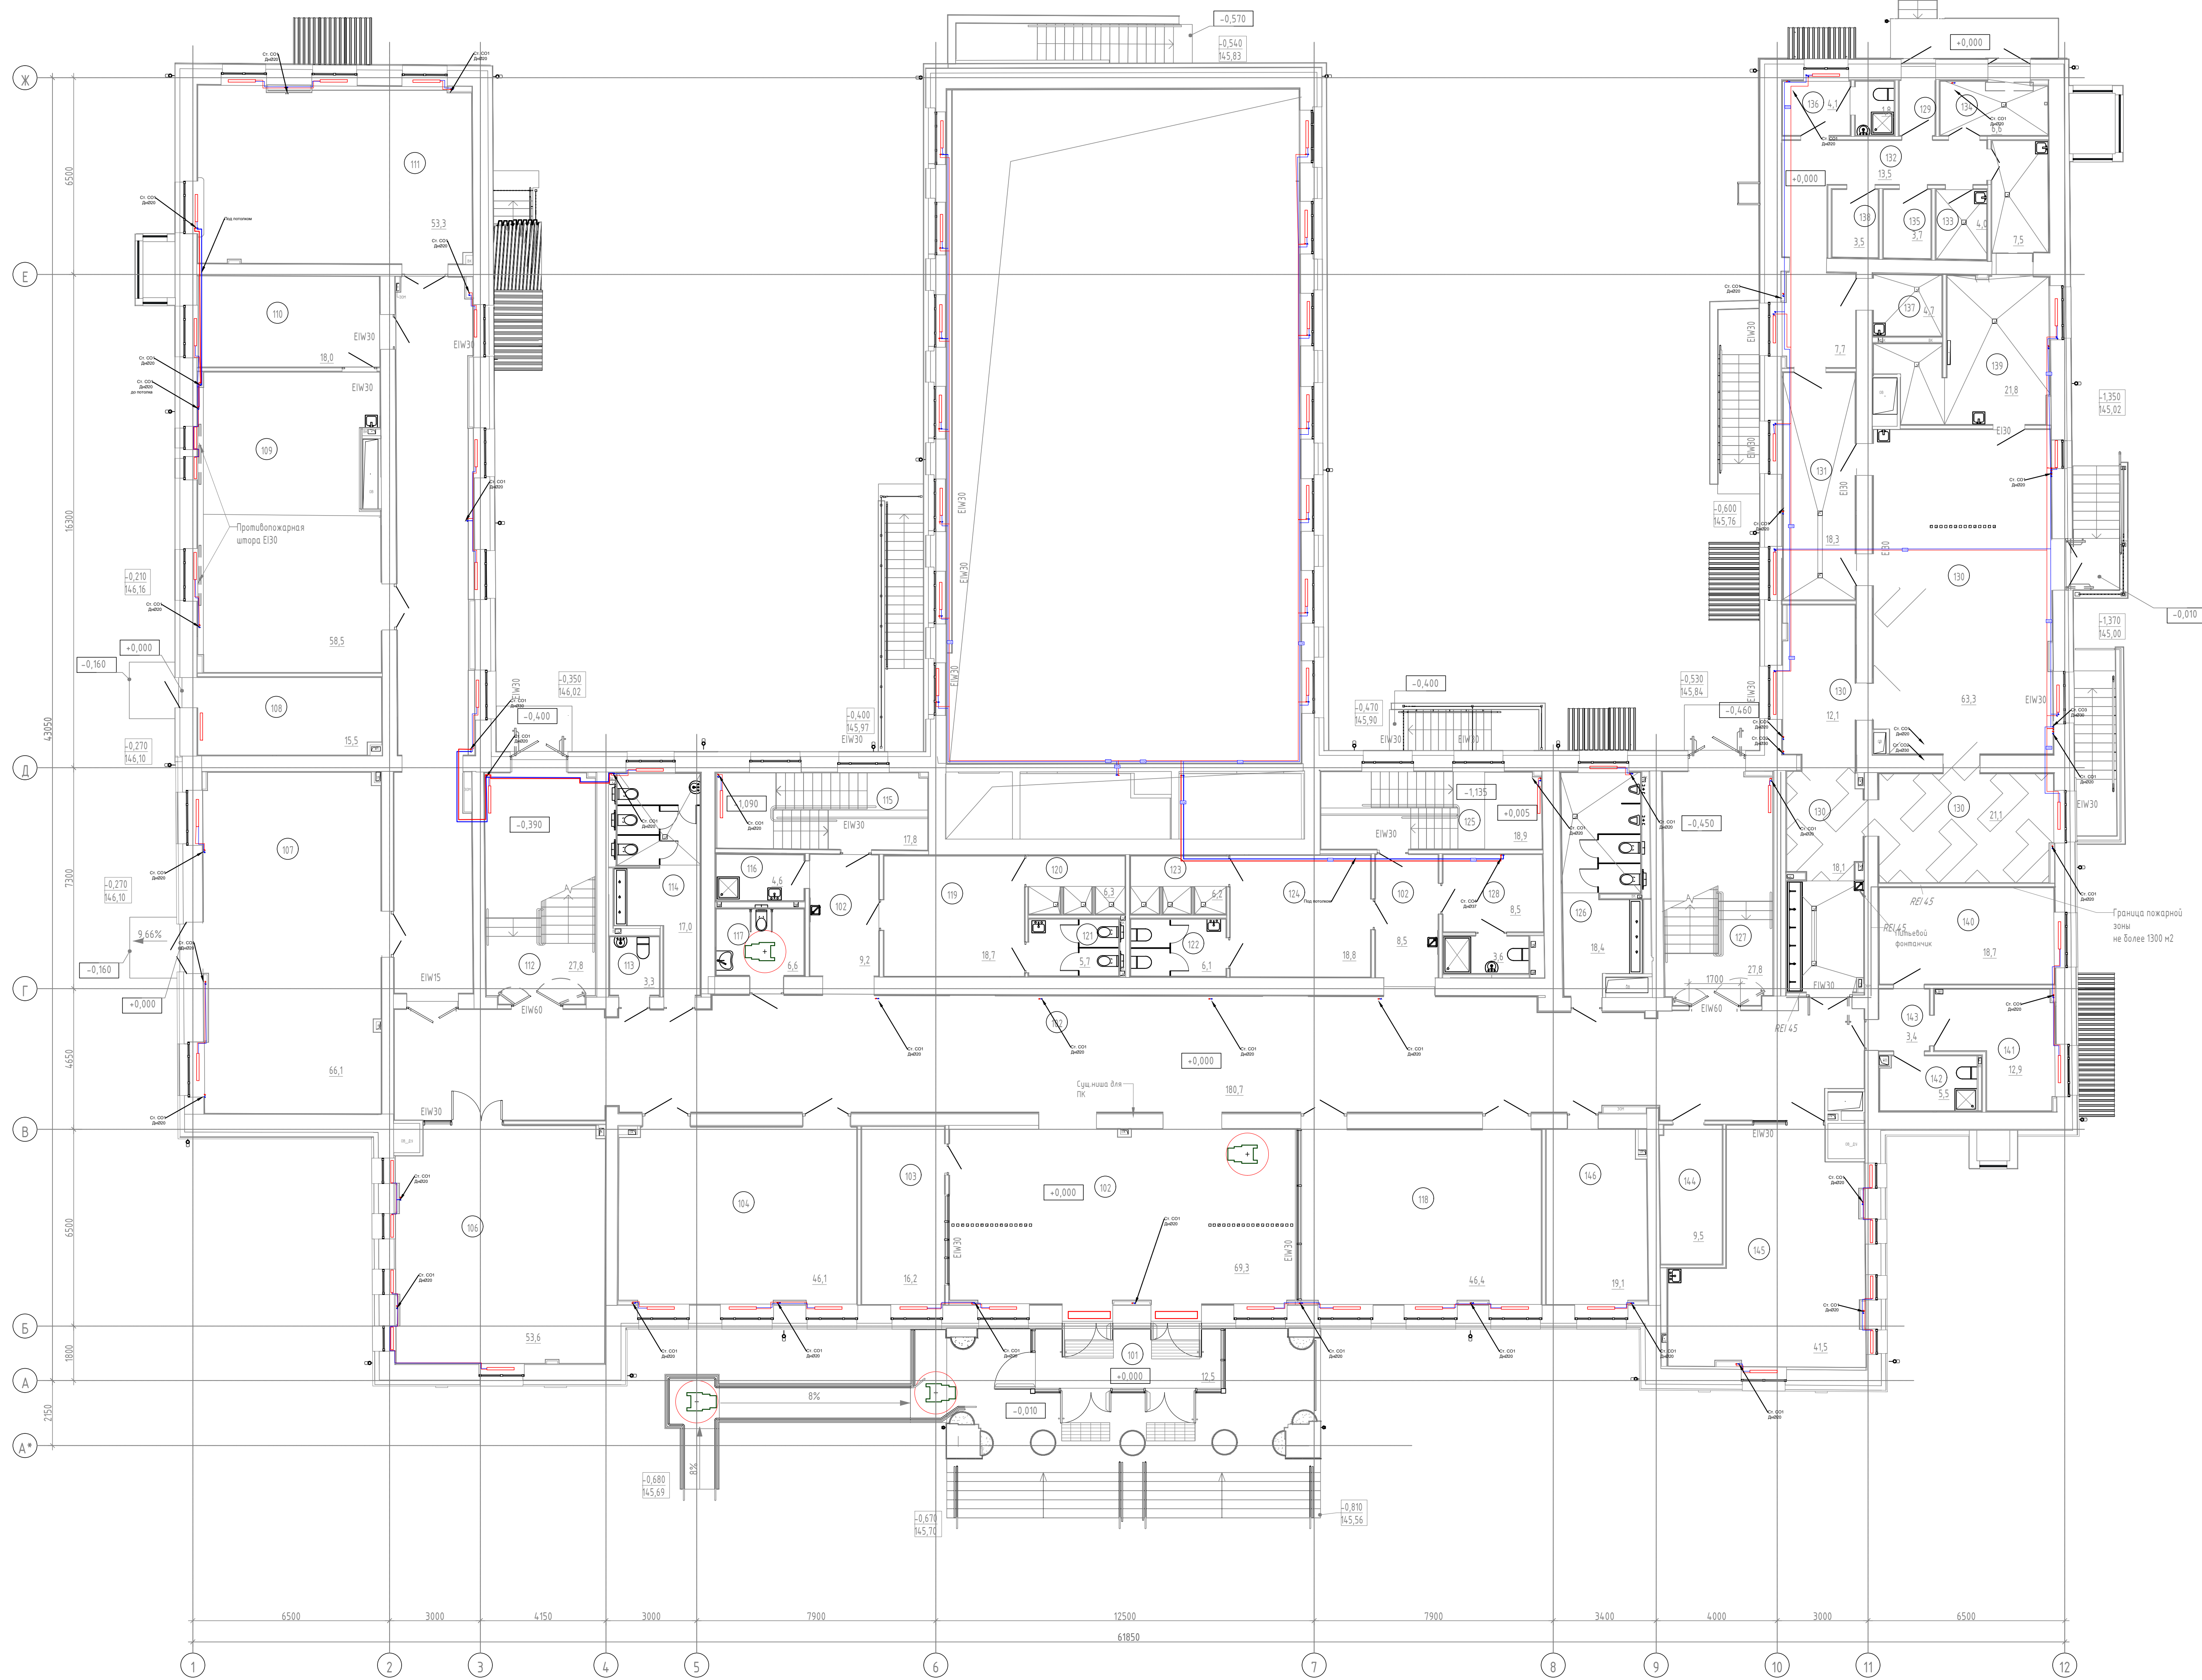

Экспликация помещений 1-го этажа			
Номер помещения	Наименование	Площадь, м²	Кат. помещения
131	Мечная для столовой посуды	18,4	B4
132	Коридор	21,2	
133	Кладовая и мечная оборотной тары	4,0	B4
134	Загрузочный цех	6,6	B4
135	Кладовая сухих продуктов	3,7	B4
136	Помещение персонала с санузлом	6,0	
137	Помещение для временного хранения посуды оттодов	4,8	B4
138	ПМ	3,5	B4
139	Помещение подготовки для к реализации с участка	29,2	B4
140	Кабинет врача	18,7	
141	Процедурный (придабачный) кабинет	12,9	
142	Помещение для хранения уборочного инвентаря,принадлежности дезинфицирующих растворов	5,5	B4
143	Ожидательная медбюро	3,4	
144	Помещение СС	9,5	B4
145	Кабинет с рабочим пространством для учителей, Тип 1	4,15	
146	Гардероб для учителей	19,1	
		1254,5	


Экспликация помещений 1-го этажа			
Номер помещения	Наименование	Площадь, м²	Кат. помещения
101	Танцбур	12,5	
102	Вестибиль	267,7	
103	Капната охраны (с диспетчерским пунктом)	16,2	
104	Гардероб для обучающихся	46,2	
105	Коридор	59,9	
106	Гардероб для обучающихся	53,7	
107	Учебный кабинет (Тип 1)	66,1	
108	Электрощитовая	15,5	B3
109	Учебный кабинет (Тип 2)	58,5	
110	Кладовая	18,0	B3
111	Учебный кабинет (настенника)	53,3	
112	Лестничная клетка (Тип 1)	27,8	
113	Туалет для персонала	3,3	
114	Уборная для девочек	17,0	
115	Технологическая лестница	17,8	
116	ПМ	4,6	B4
117	Универсальная уборная для МГН	6,6	
118	Гардероб для обучающихся	46,4	
119	Раздевальня Тип 1	18,7	
120	Учебная	6,3	
121	Уборная	5,7	
122	Уборная	6,1	
123	Учебная	6,2	
124	Раздевальня Тип 1	18,8	
125	Технологическая лестница	18,9	
126	Уборная для мальчиков	18,4	
127	Лестничная клетка (Тип 1)	27,8	
128	Трансформатор с санузлом	12,1	
129	Танцбур	2,2	
130	Общеданный зал	114,5	

636/П-24-АНО/ТЗК			
Выполнение проектно-изыскательских работ на капитальный ремонт общеобразовательного учреждения (ГБОУ Школа №282 "Соколники"), по адресу: г. Москва, ул. Барбосова, д. 1, стр. 1			
Изм. Кол. листы	Изм. Кол. листы	Изм. Кол. листы	Изм. Кол. листы
Разработ. Давыдов А.В.	10.24	Осуществление технического	Этапия
Проектиров. Зеленцов А.В.	10.24	осуществление строительства и инженерных систем здания	Пуст
ГИП	Емельянов А.В.	10.24	Пуст
План 1 этажа М:100, Система отопления			000 "Аркано"
Н. контр. Циванов А.В.			3
10.24			Формат А0

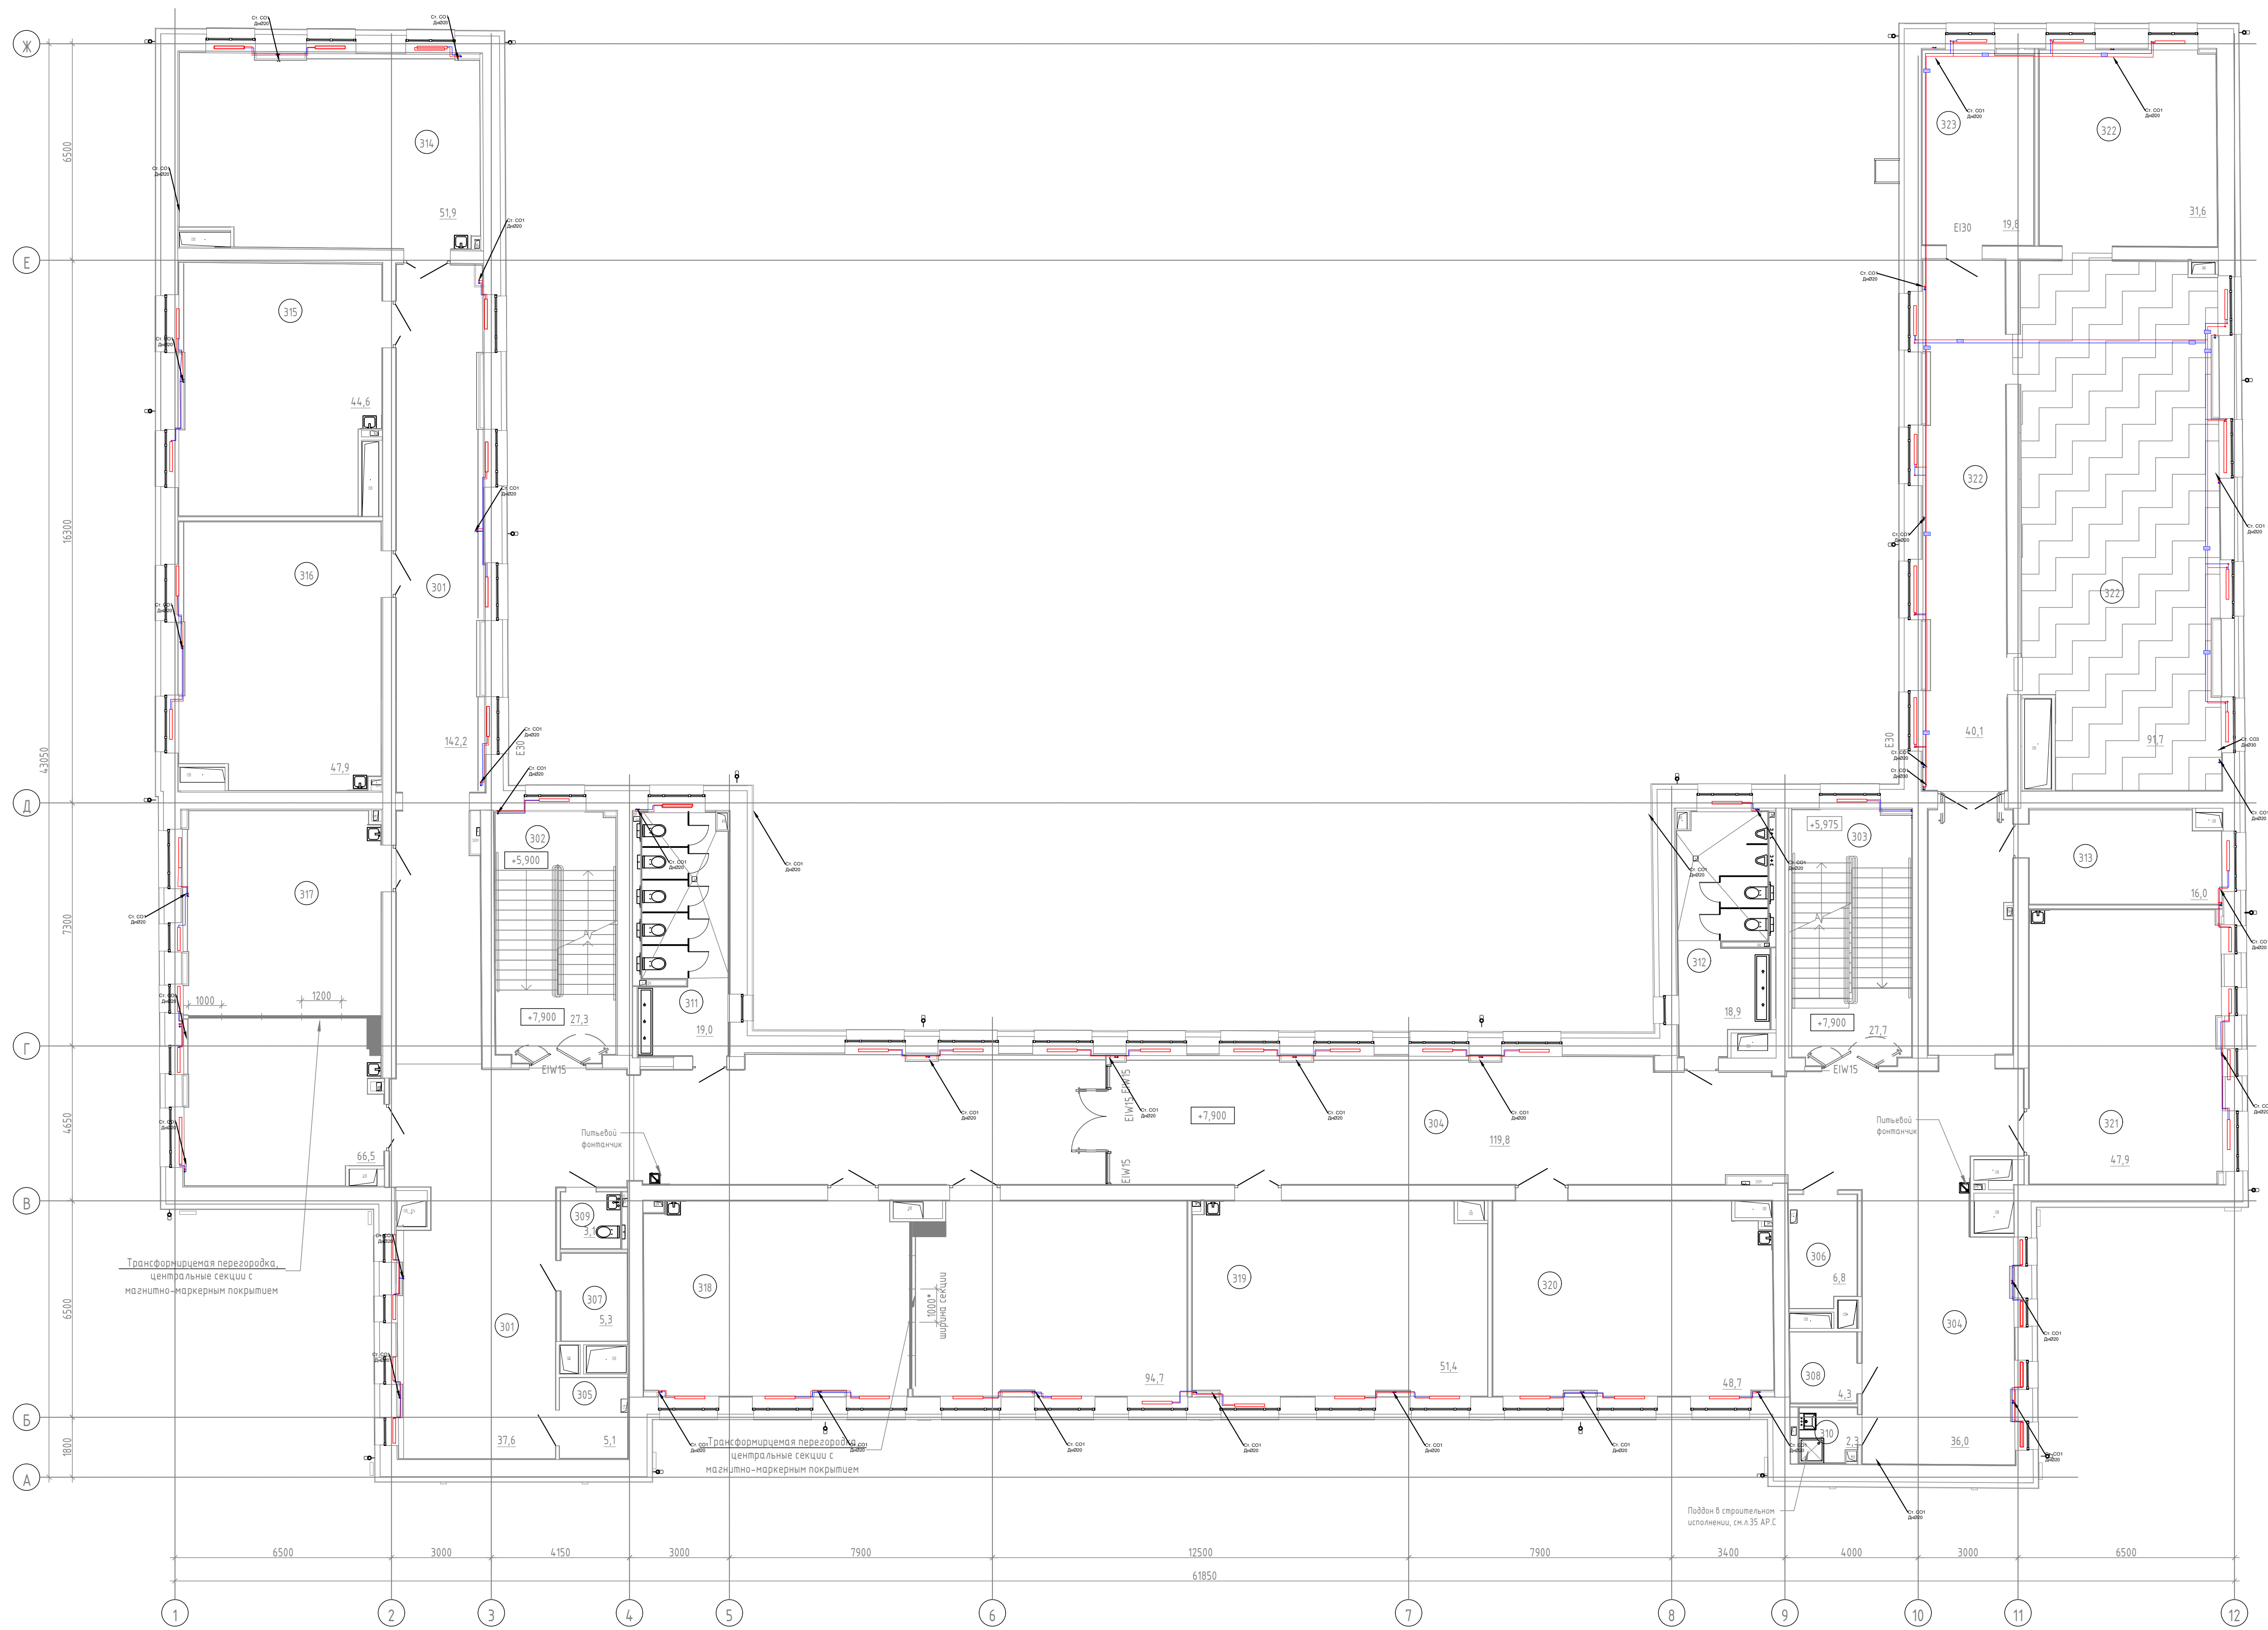

Экспликация помещений 3-го этажа			
Номер помеще-ния	Наименование	Площадь, м²	Кат. помеще-ния
301	Коридор с рекреацией	179,8	
302	Вестибунная клетка (Тул. ЛП)	27,3	
303	Вестибунная клетка (Тул. ЛП)	27,7	
304	Коридор с рекреацией	155,8	
305	Помещение СС	5,1	В4
306	Помещение СС	6,8	В4
307	Пособное помещение	5,3	В4
308	Пособное помещение	6,3	В4
309	Туалет для персонала	3,1	
310	Тум	2,3	В4
311	Ванная для девочек	19,0	
312	Ванная для мальчиков	18,9	
313	Кабинет для индивидуальных занятий, 8 в.ч. скоррекционным педагогом	16,0	
314	Учебный кабинет	51,9	
315	Учебный кабинет	44,6	
316	Учебный кабинет	47,9	
317	Кабинет иностранного языка с возможностью деления/трансформированной перегородкой на два помещения	66,5	
318	Творческая студия с возможностью деления/трансформированной перегородкой на два помещения	94,7	
319	Учебный кабинет	51,4	
320	Учебный кабинет	48,7	
321	Учебный кабинет	47,9	
322	Мультифункциональный информационный библиотечный центр с зонами для индивидуальных и групповых занятий, медиатеки, 163,4 (в том числе детская библиотека)	163,4	
323	Мультифункциональный информационный библиотечный центр. Кроме того (закрытый фонд) и библиотека	19,8	В3
		1088,1	

636/П-24-АНО/ТЗК									
Выполнение проектно-изыскательских работ на капитальный ремонт общеобразовательного учреждения (ГБОУ Школа №282 "Соколники"), по адресу: г. Москва, ул. Барбосова, 9, п. 1, стр. 1									
Имя	Вал.	Исст.	Исст.	Исст.	Исст.	Исст.	Исст.	Исст.	Исст.
Роздоб.	Роздоб.	Роздоб.	Роздоб.	Роздоб.	Роздоб.	Роздоб.	Роздоб.	Роздоб.	Роздоб.
Пробер.	Пробер.	Пробер.	Пробер.	Пробер.	Пробер.	Пробер.	Пробер.	Пробер.	Пробер.
Гип	Гип	Гип	Гип	Гип	Гип	Гип	Гип	Гип	Гип
План 3 этажа М1:100. Система отопления							5	5	5
ООО "Аркан"							Формат А0		

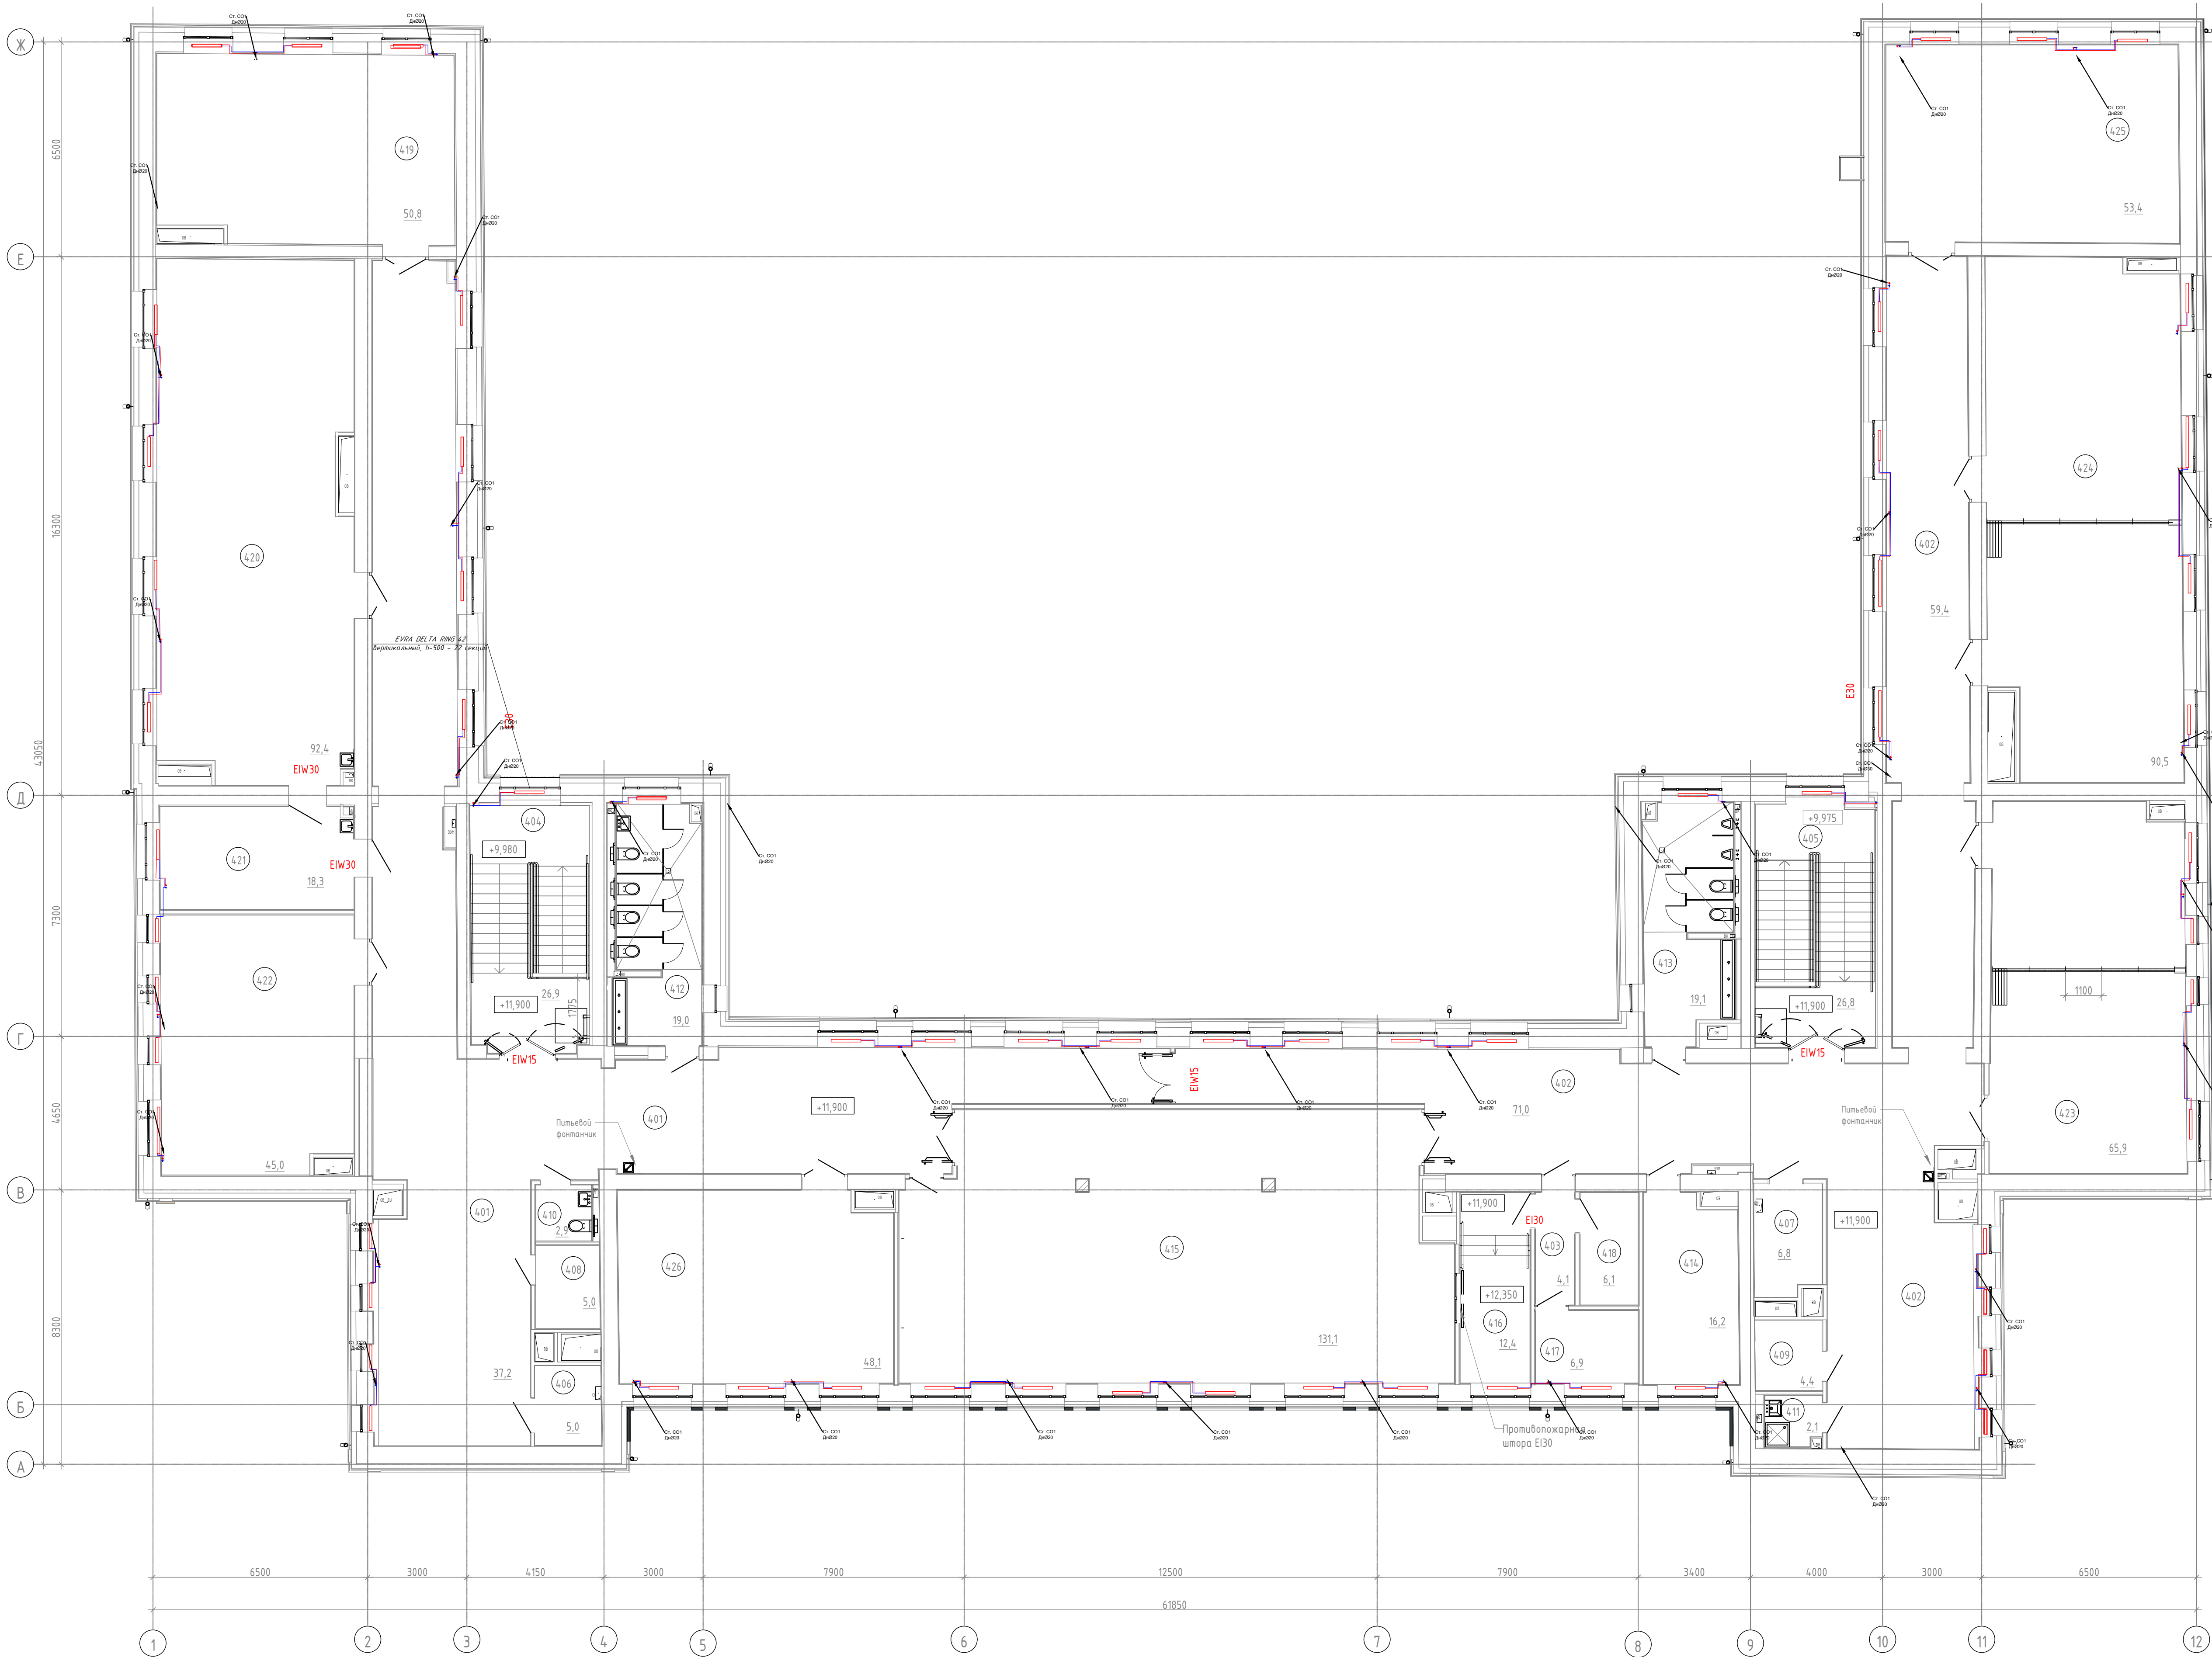

Экспликация помещений 4-го этажа			
Номер помеще-ния	Назначение	Площадь, м²	Кот. помеще-ния
401	Коридор с рекреацией	173,6	
402	Коридор с рекреацией	166,2	
403	Томбур	4,1	
404	Лестничная клетка (Тип Л1)	26,9	
405	Лестничная клетка (Тип Л1)	26,8	
406	Помещение СС	5,0	84
407	Помещение СС	6,8	84
408	Подсобное помещение	5,0	84
409	Подсобное помещение	4,4	84
410	Туалет для персонала	2,9	
411	ПМ	2,1	84
412	Забора для девочек	19,0	
413	Забора для мальчиков	19,1	
414	Кабинет для индивидуальных занятий, в т.ч. следоизом-психологом	16,2	
415	Актовый зал (с эстрадой в уровне пола)	131,1	
416	Технический центр	12,4	83
417	Арт-студия	6,9	
418	Кабинет информатики	6,1	84
419	Кабинет математики	50,8	
420	Учебный кабинет (для изучения естественных наук/географии Тип 2)	92,4	
421	Лаборатория биологии	18,3	83
422	Учебный кабинет (история)	45,0	
423	Кабинет иностранного языка с возможностью видеотрансформированной переработки на два помещения	65,9	
424	Учебный кабинет информатики с возможностью видеотрансформированной переработки на два помещения	90,5	
425	Кабинет русского языка и литературы	53,4	
426	Кабинет русского языка и литературы	48,1	
		1098,8	

636/П-24-АНО/ТЗК									
Выполнение проектно-изыскательских работ на капитальный ремонт общеобразовательного учреждения (ГБОУ Школа №282 "Соколники"), по адресу: г. Москва, ул. Барыкина, д. 9, стр. 1									
Изм. №	Контр. №	Дата	Подп.	Дата	Осуществление технического сопровождения строительства и инженерных систем здания				
Разработ.	Иванов А.А.	10.24	Иванов А.А.	10.24	Этап	Пуст	Пуст	Пуст	Пуст
Проверил	Зеленцов А.А.	10.24	Зеленцов А.А.	10.24	6				
ГИП	Емельянов А.А.	10.24	Емельянов А.А.	10.24					
Н. контр. Иванова А.А.					План 4 этажа М1:100. Система отопления				
					ООО "Аркан"				
					Формат А0				