





**АНАЛИТИКА ПО УВЕЛИЧЕНИЮ ЖИЛОЙ
ЗАСТРОЙКИ ТЕРРИТОРИИ ППТ МКР. 37-38,
39, ППТ МКР. 80, ППТ МКР. 41-42, 43-45, 44-46,
47-48, 49-50, КОНЦЕПЦИИ РАЙОНА
СЕВЕРНОЕ ИЗМАЙЛОВО (ВАО)**



СХЕМА РАСПОЛОЖЕНИЯ РАССМАТРИВАЕМОЙ ТЕРРИТОРИИ В СТРУКТУРЕ ГОРОДА МОСКВЫ И АДМИНИСТРАТИВНОГО ОКРУГА ГОРОДА МОСКВЫ

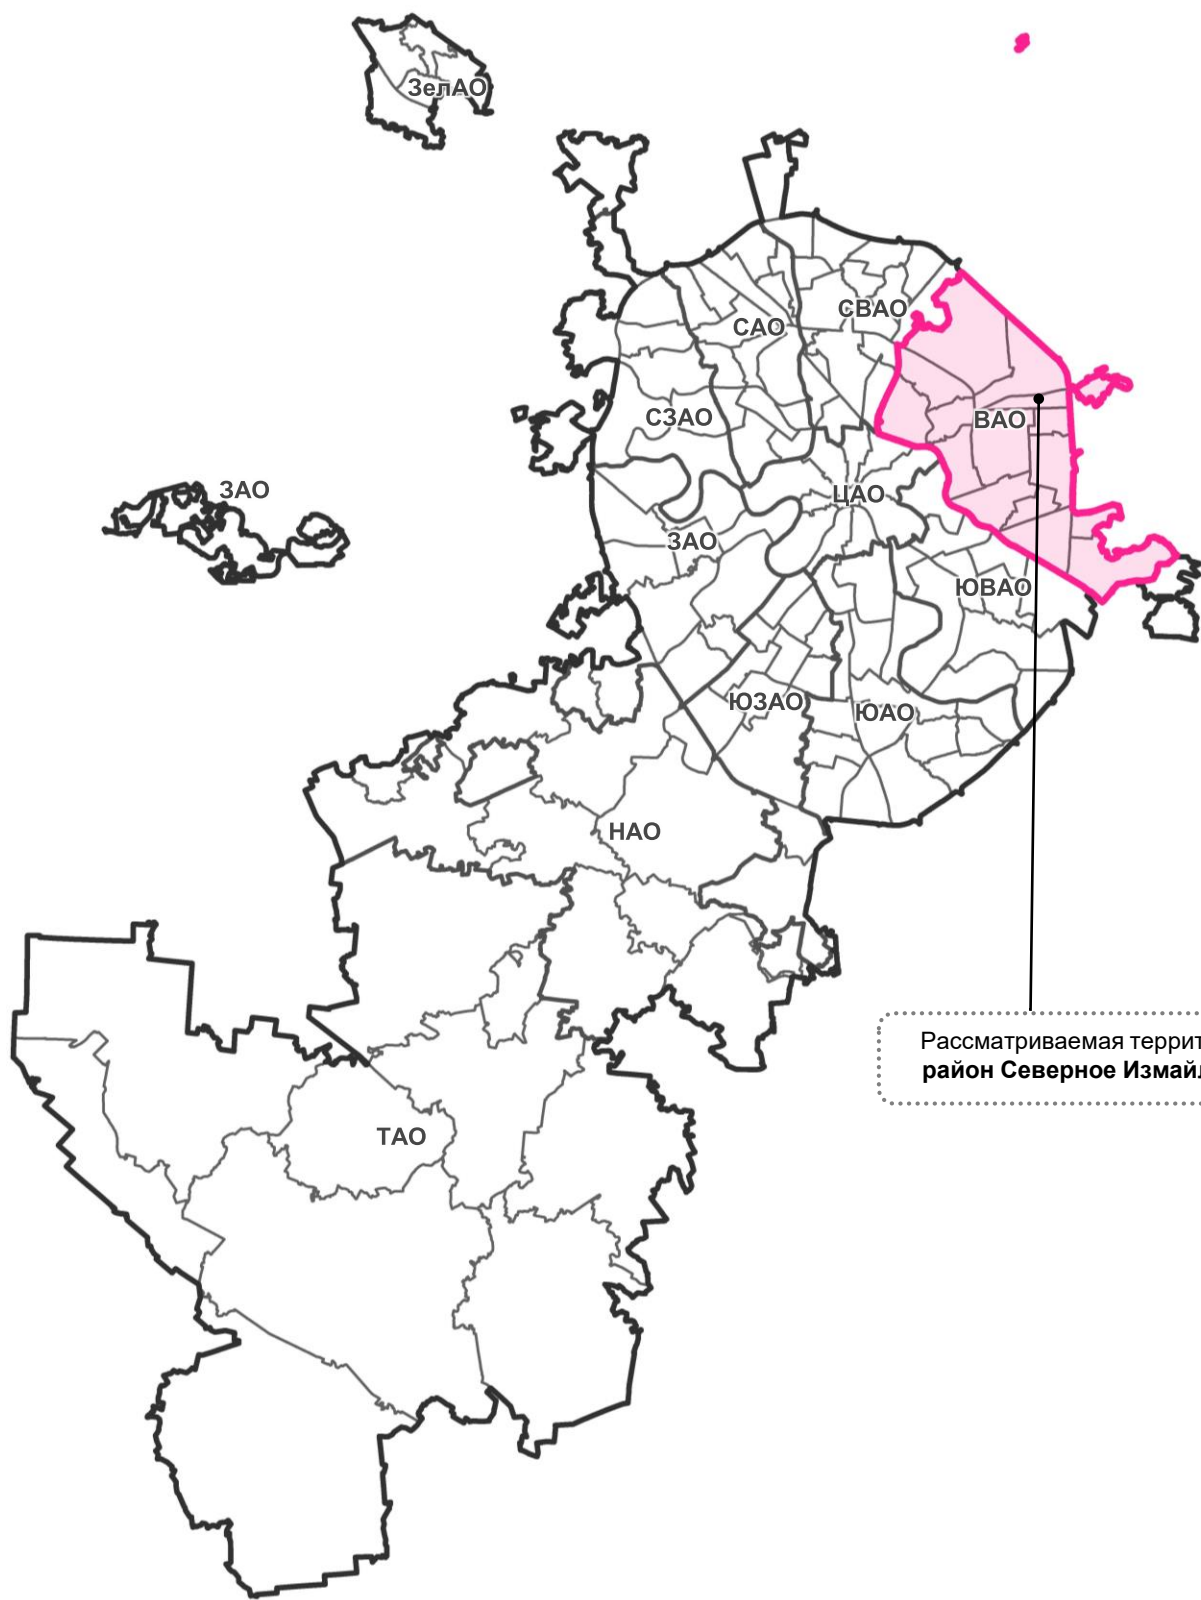


Рассматриваемая территория
район Северное Измайлово

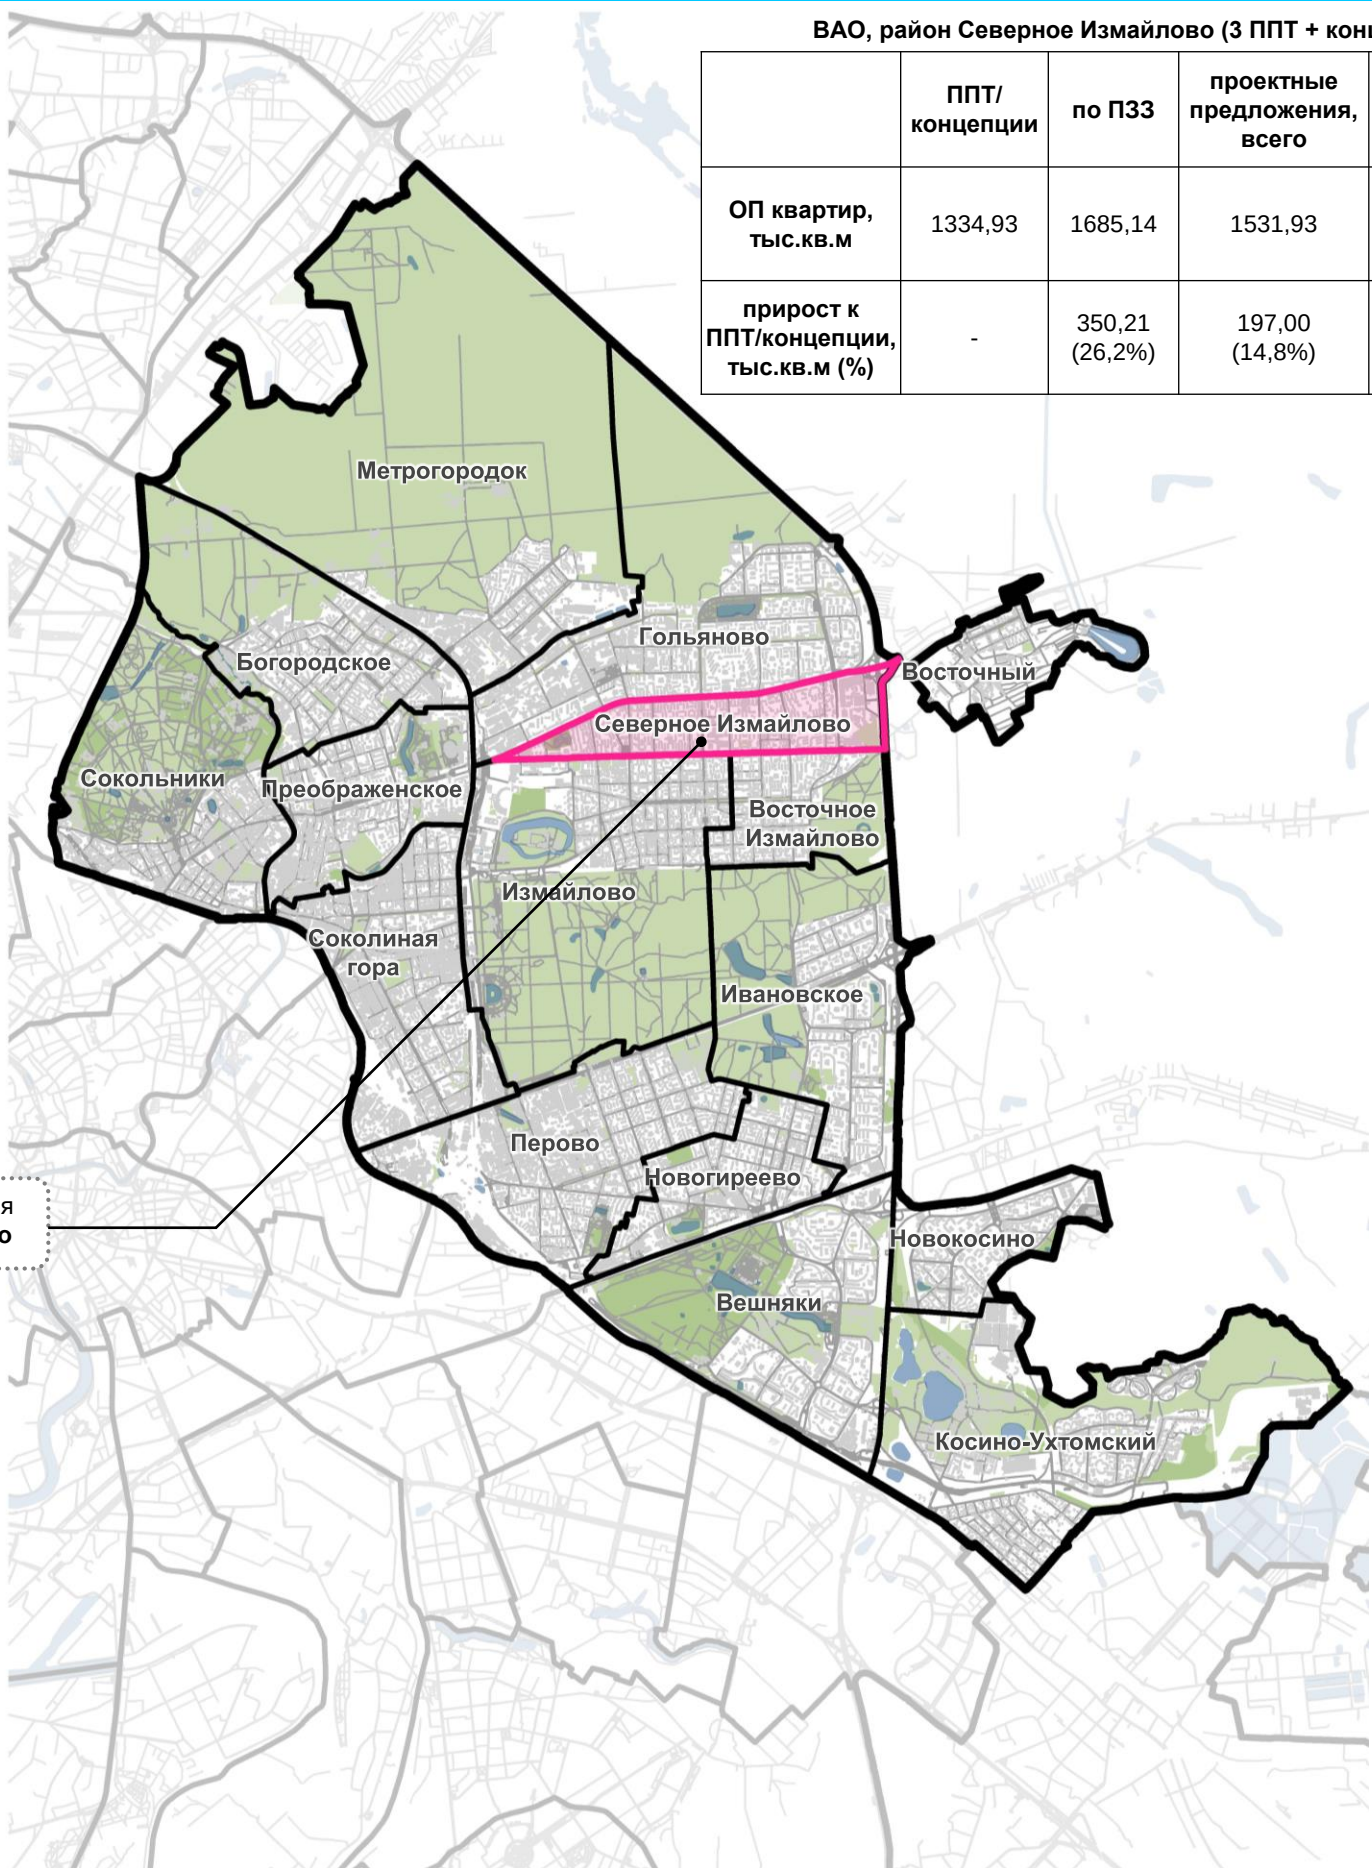


BAO, район Северное Измайлово (3 ППТ + концепция)

	ППТ/ концепции	по ПЗЗ	проектные предложения, всего	Дельта (проектные предложения- ПЗЗ)
ОП квартир, тыс.кв.м	1334,93	1685,14	1531,93	-153,21
прирост к ППТ/концепции, тыс.кв.м (%)	-	350,21 (26,2%)	197,00 (14,8%)	

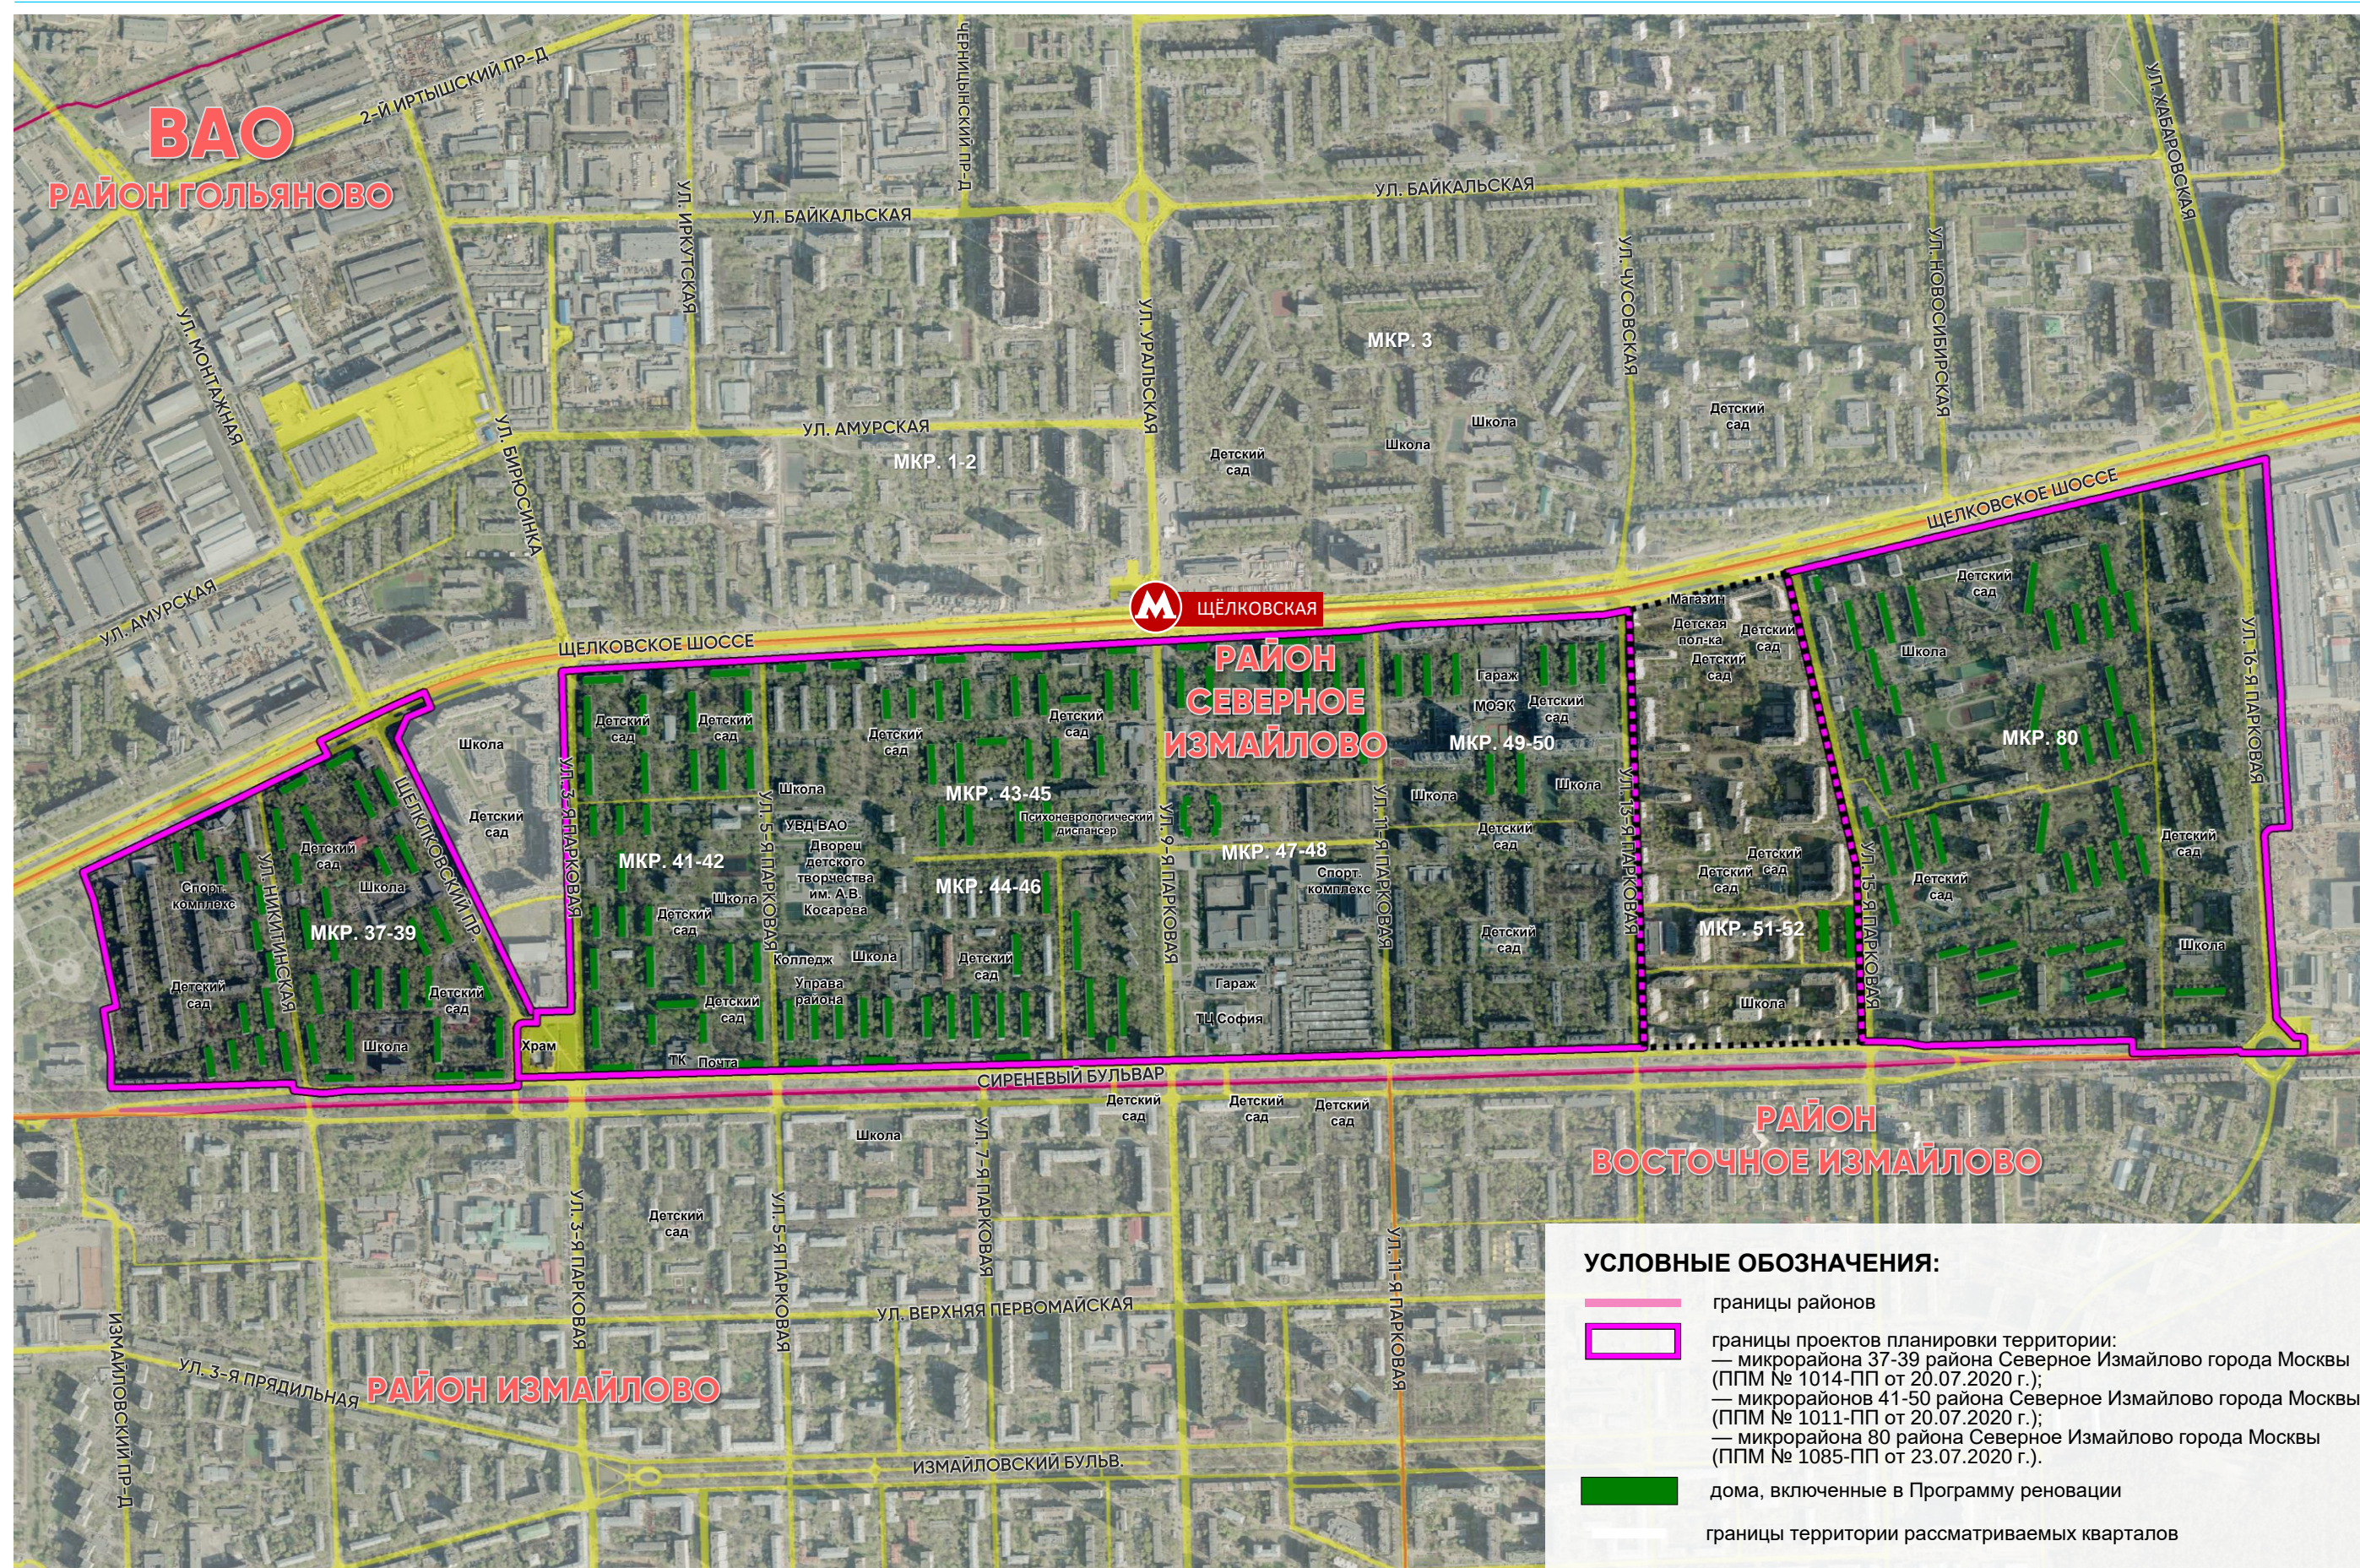

АНАЛИТИКА ПО УВЕЛИЧЕНИЮ ЖИЛОЙ ЗАСТРОЙКИ ПРОЕКТА ПЛАНИРОВКИ ТЕРРИТОРИИ МКР. 37-38, 39 РАЙОНА СЕВЕРНОЕ ИЗМАЙЛОВО (ВАО)

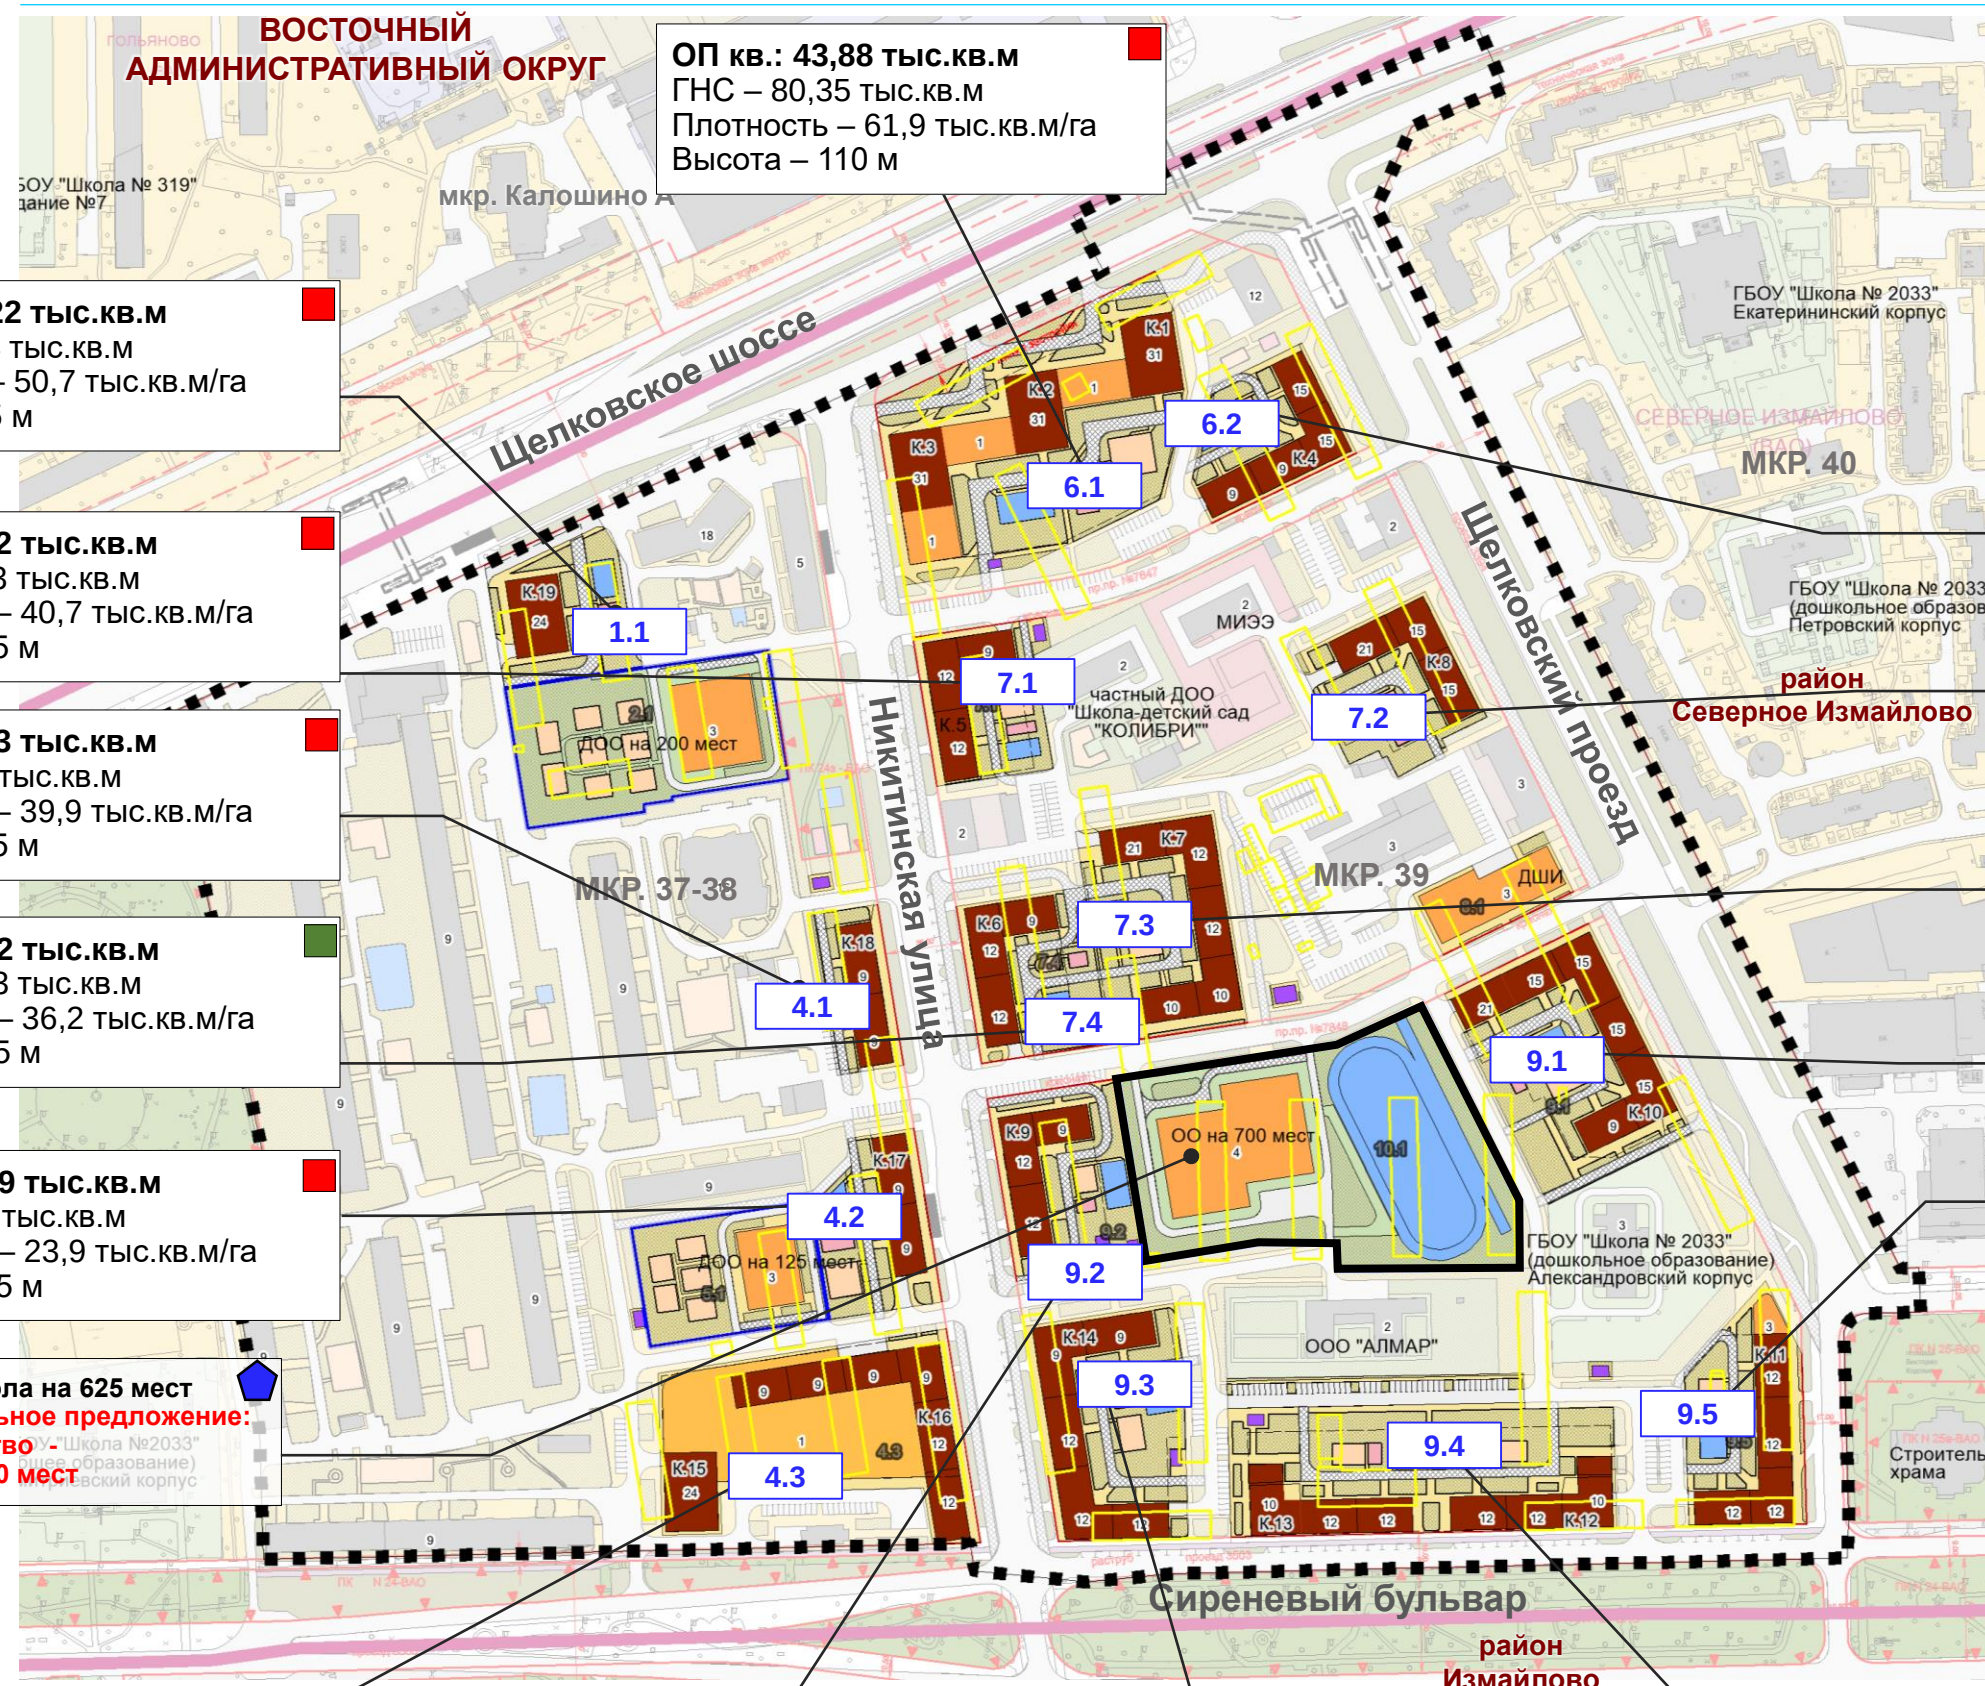

УСЛОВНЫЕ ОБОЗНАЧЕНИЯ:

- границы территорий кварталов градостроительного развития, $S = 36,7$ га
- планируемые участки общественной застройки
- участки объектов образования
- коммерческие дома
- дома под переселение
- объекты образования, новое предложение

ОП кв.: 43,88 тыс.кв.м
ГНС – 80,35 тыс.кв.м
Плотность – 61,9 тыс.кв.м/га
Высота – 110 м

ОП кв.: 11,22 тыс.кв.м
ГНС – 20,74 тыс.кв.м
Плотность – 50,7 тыс.кв.м/га
Высота – 85 м

ОП кв.: 9,52 тыс.кв.м
ГНС – 15,53 тыс.кв.м
Плотность – 40,7 тыс.кв.м/га
Высота – 45 м

ОП кв.: 5,53 тыс.кв.м
ГНС – 9,10 тыс.кв.м
Плотность – 39,9 тыс.кв.м/га
Высота – 35 м

ОП кв.: 9,52 тыс.кв.м
ГНС – 15,53 тыс.кв.м
Плотность – 36,2 тыс.кв.м/га
Высота – 45 м

ОП кв.: 5,39 тыс.кв.м
ГНС – 8,99 тыс.кв.м
Плотность – 23,9 тыс.кв.м/га
Высота – 35 м

По ППТ: Школа на 625 мест
Дополнительное предложение:
Строительство
Школа на 700 мест

ОП кв.: 26,70 тыс.кв.м
ГНС – 47,49 тыс.кв.м
Плотность – 53,1 тыс.кв.м/га
Высота – 85 м

ОП кв.: 9,52 тыс.кв.м
ГНС – 15,53 тыс.кв.м
Плотность – 31,1 тыс.кв.м/га
Высота – 45 м

ОП кв.: 16,98 тыс.кв.м
ГНС – 28,36 тыс.кв.м
Плотность – 42,0 тыс.кв.м/га
Высота – 45 м

ОП кв.: 18,05 тыс.кв.м
ГНС – 31,30 тыс.кв.м
Плотность – 26,1 тыс.кв.м/га
Высота – 45 м

ОП кв.: 11,28 тыс.кв.м
ГНС – 19,90 тыс.кв.м
Плотность – 54,9 тыс.кв.м/га
Высота – 55 м

ОП кв.: 14,84 тыс.кв.м
ГНС – 23,72 тыс.кв.м
Плотность – 55,9 тыс.кв.м/га
Высота – 75 м

ОП кв.: 18,74 тыс.кв.м
ГНС – 31,31 тыс.кв.м
Плотность – 49,9 тыс.кв.м/га
Высота – 75 м

ОП кв.: 24,61 тыс.кв.м
ГНС – 40,69 тыс.кв.м
Плотность – 51,8 тыс.кв.м/га
Высота – 75 м

ОП кв.: 13,01 тыс.кв.м
ГНС – 21,57 тыс.кв.м
Плотность – 44,7 тыс.кв.м/га
Высота – 45 м

ПО ППТ: ОП кв. – 238,79 тыс. кв. м.

ПО ПЗЗ: ОП кв. – 319,68 тыс. кв. м.
(прирост 80,89 тыс.кв.м или 34 %)


ПО ПРОЕКТУ: ОП кв. – 238,79 тыс. кв. м.
(прирост 0 тыс.кв.м или 0 %)


ПЕРЕСЕЛЕНИЕ: ОП кв. – 67,71 тыс. кв. м.
(прирост 0 тыс.кв.м или 0 %)

КОММЕРЧЕСКИЕ ДОМА: ОП кв. – 171,08 тыс. кв. м.
(прирост 0 тыс.кв.м или 0 %)



АНАЛИТИКА ПО УВЕЛИЧЕНИЮ ЖИЛОЙ ЗАСТРОЙКИ ПРОЕКТА ПЛАНИРОВКИ ТЕРРИТОРИИ МКР. 41-42, 43-45, 44-46, 47-48, 49-50 РАЙОНА СЕВЕРНОЕ ИЗМАЙЛОВО (ВАО)

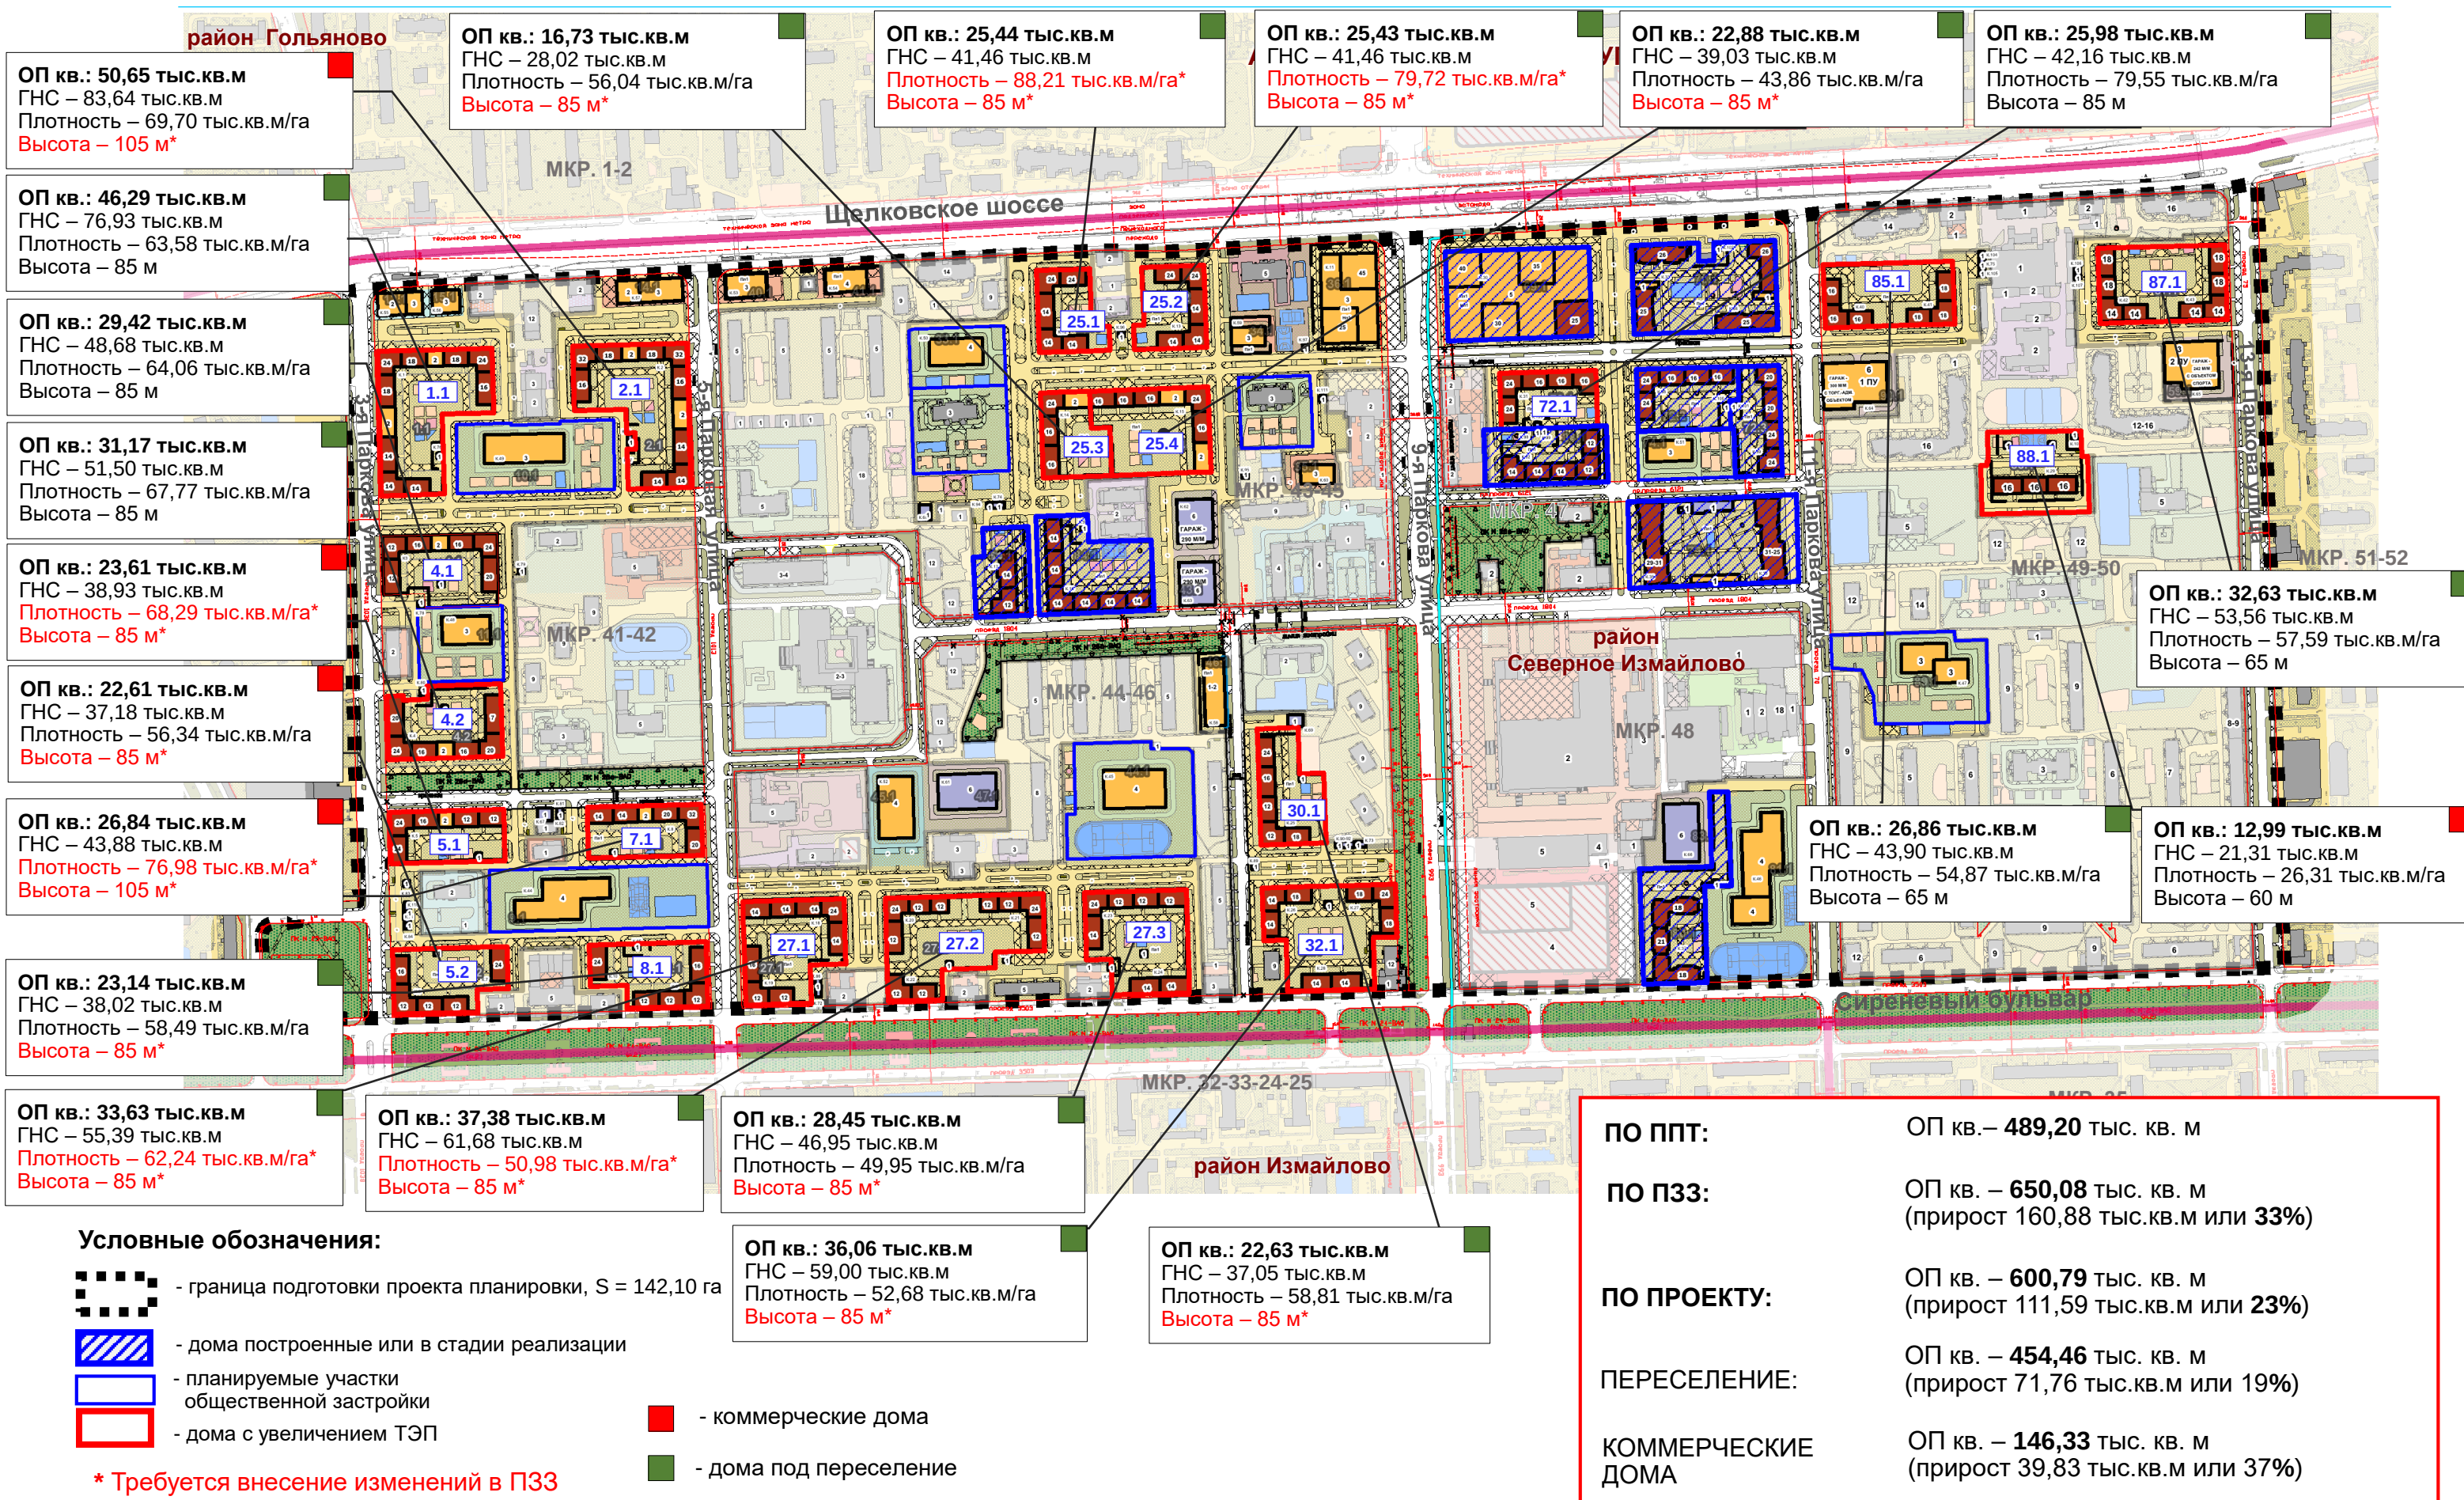

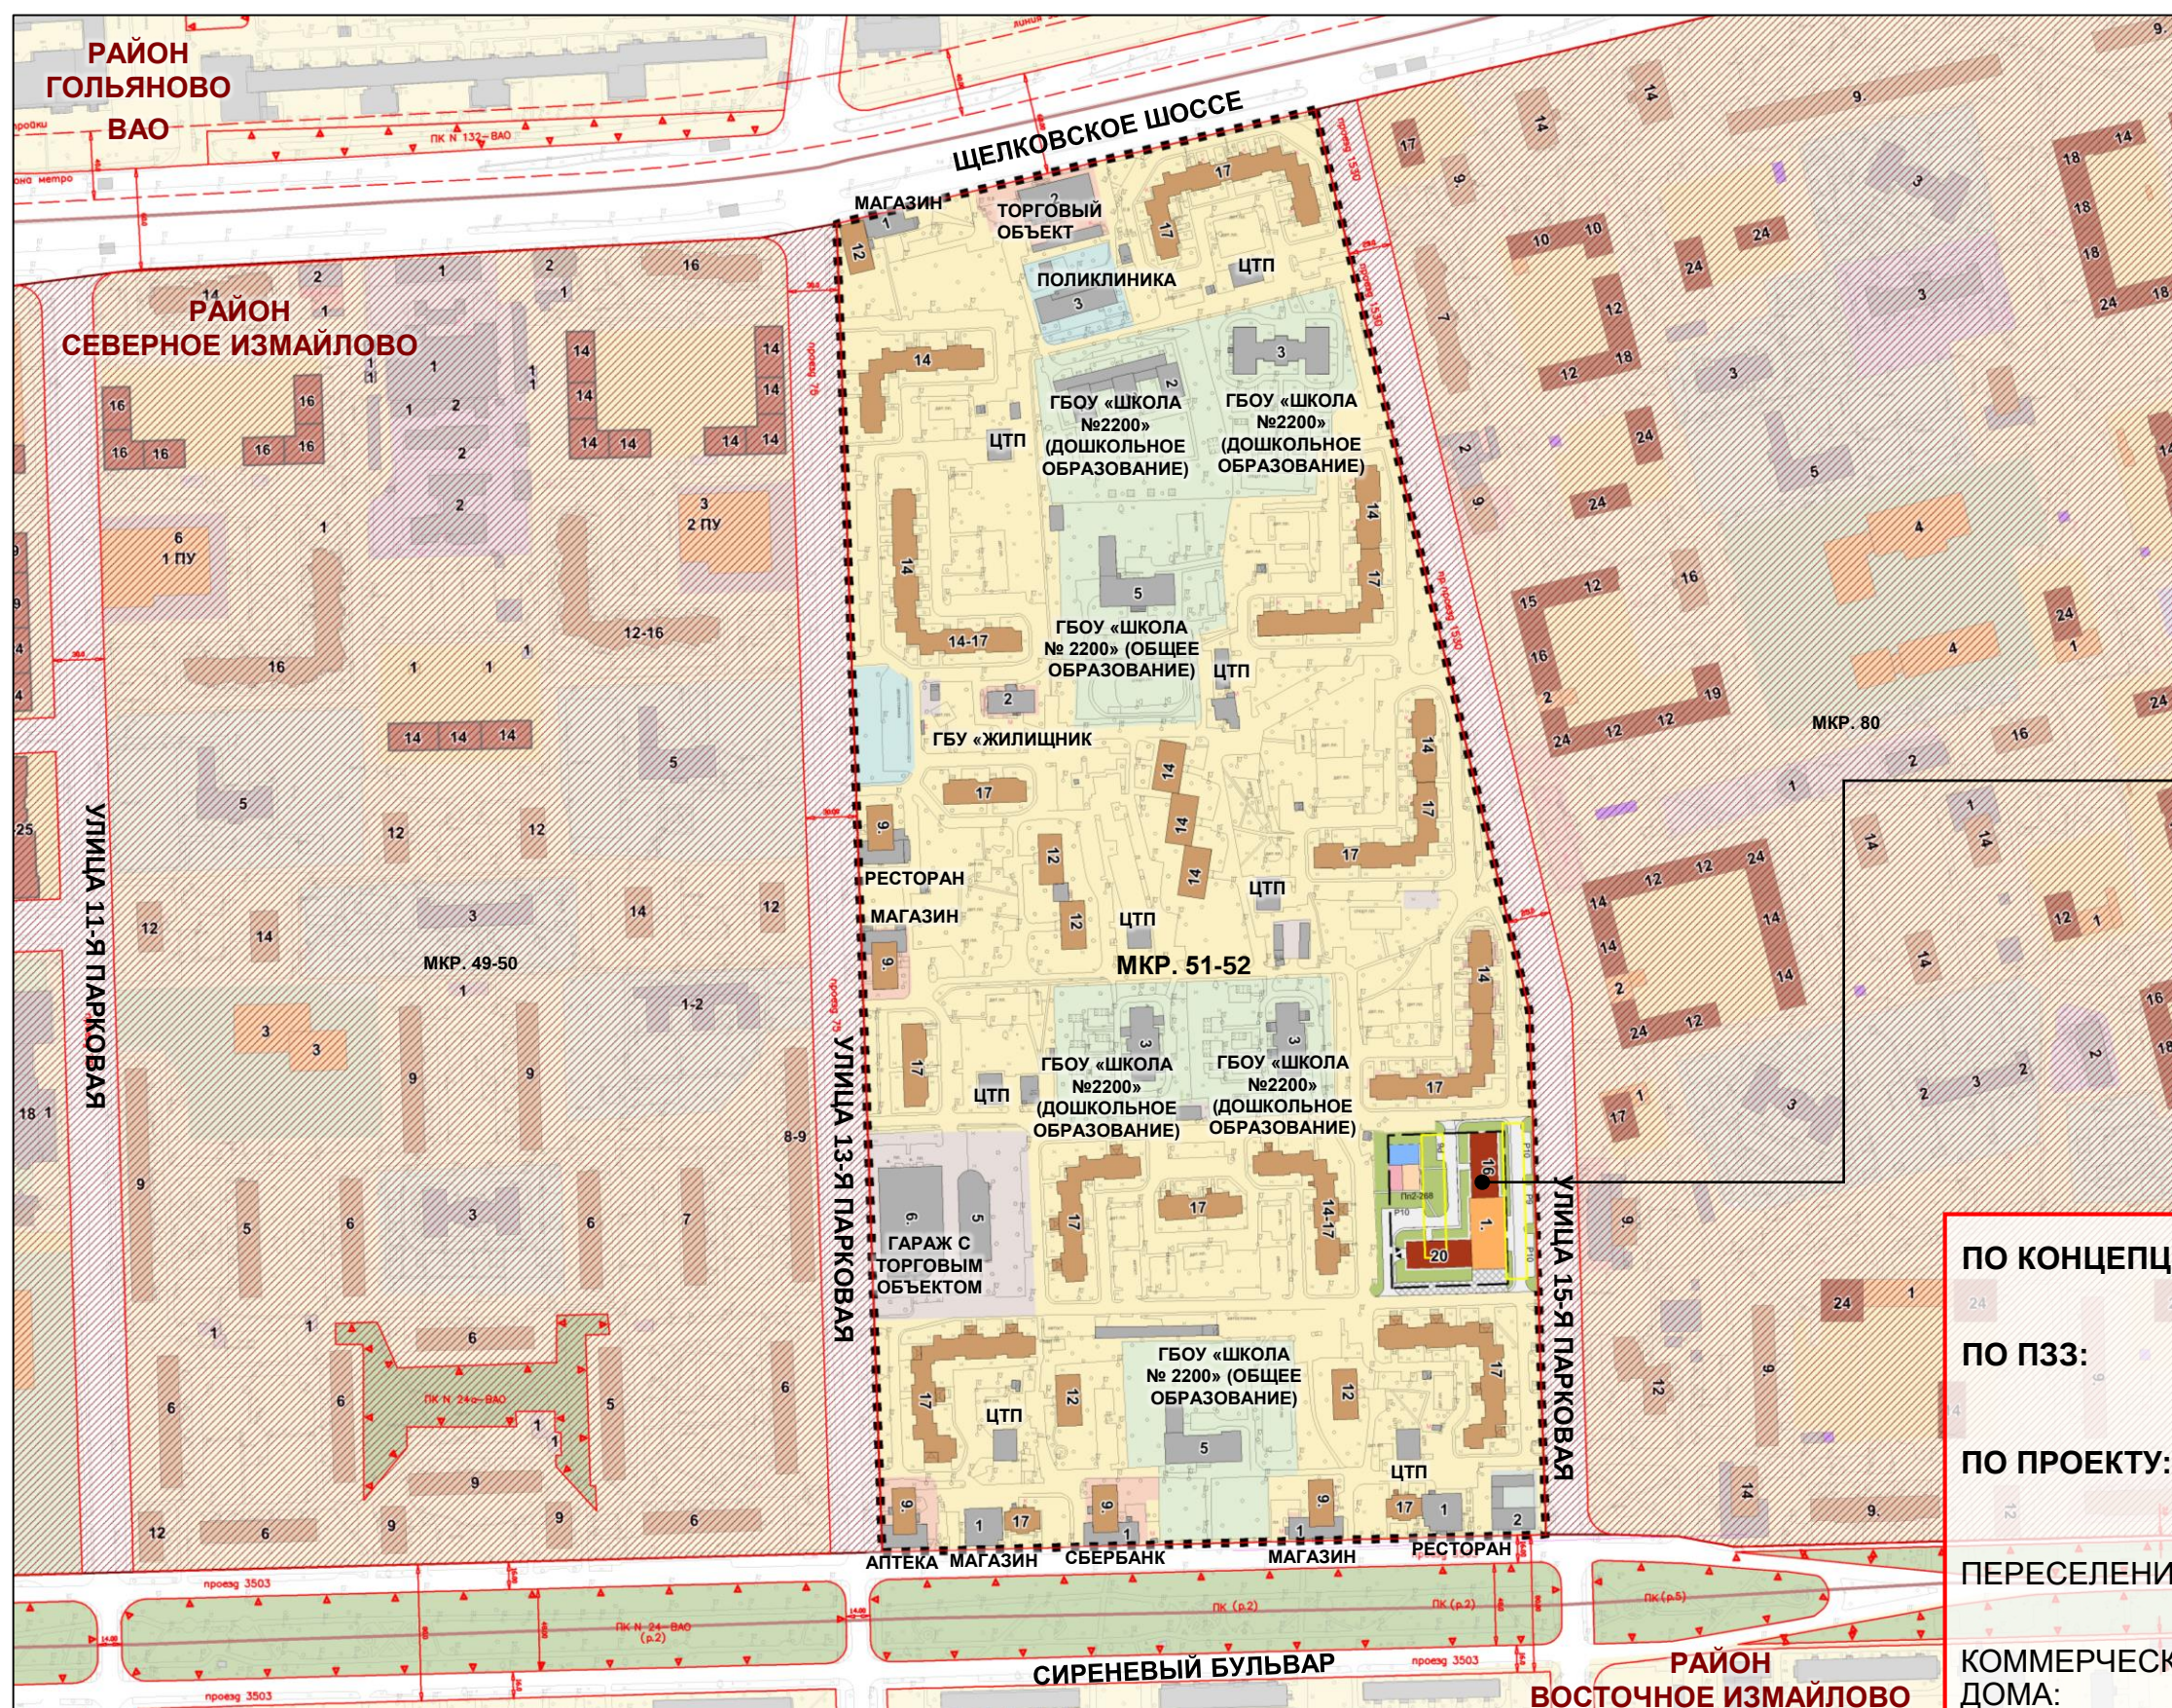


УСЛОВНЫЕ ОБОЗНАЧЕНИЯ:
 - границы территорий кварталов градостроительного развития
 - коммерческие дома

ОП кв.: 13,41 тыс.кв.м
 ГНС – 22,70 тыс.кв.м
 Плотность – 24,67 тыс.кв.м/га
 Высота – 70 м

ПО КОНЦЕПЦИИ: ОП кв. – 13,41 тыс. кв. м.
ПО ПЗЗ: ОП кв. – 17,84 тыс. кв. м.
 (прирост 4,43 тыс.кв.м или 33 %)
ПО ПРОЕКТУ: ОП кв. – 13,41 тыс. кв. м.
 (прирост 0 тыс.кв.м или 0 %)
ПЕРЕСЕЛЕНИЕ: ОП кв. – 0 тыс. кв. м.
 (прирост 0 тыс.кв.м или 0 %)
КОММЕРЧЕСКИЕ ДОМА: ОП кв. – 0 тыс. кв. м.
 (прирост 0 тыс.кв.м или 0 %)

АНАЛИТИКА ПО УВЕЛИЧЕНИЮ ЖИЛОЙ ЗАСТРОЙКИ ПРОЕКТА ПЛАНИРОВКИ ТЕРРИТОРИИ МКР. 80 РАЙОНА СЕВЕРНОЕ ИЗМАЙЛОВО (ВАО)

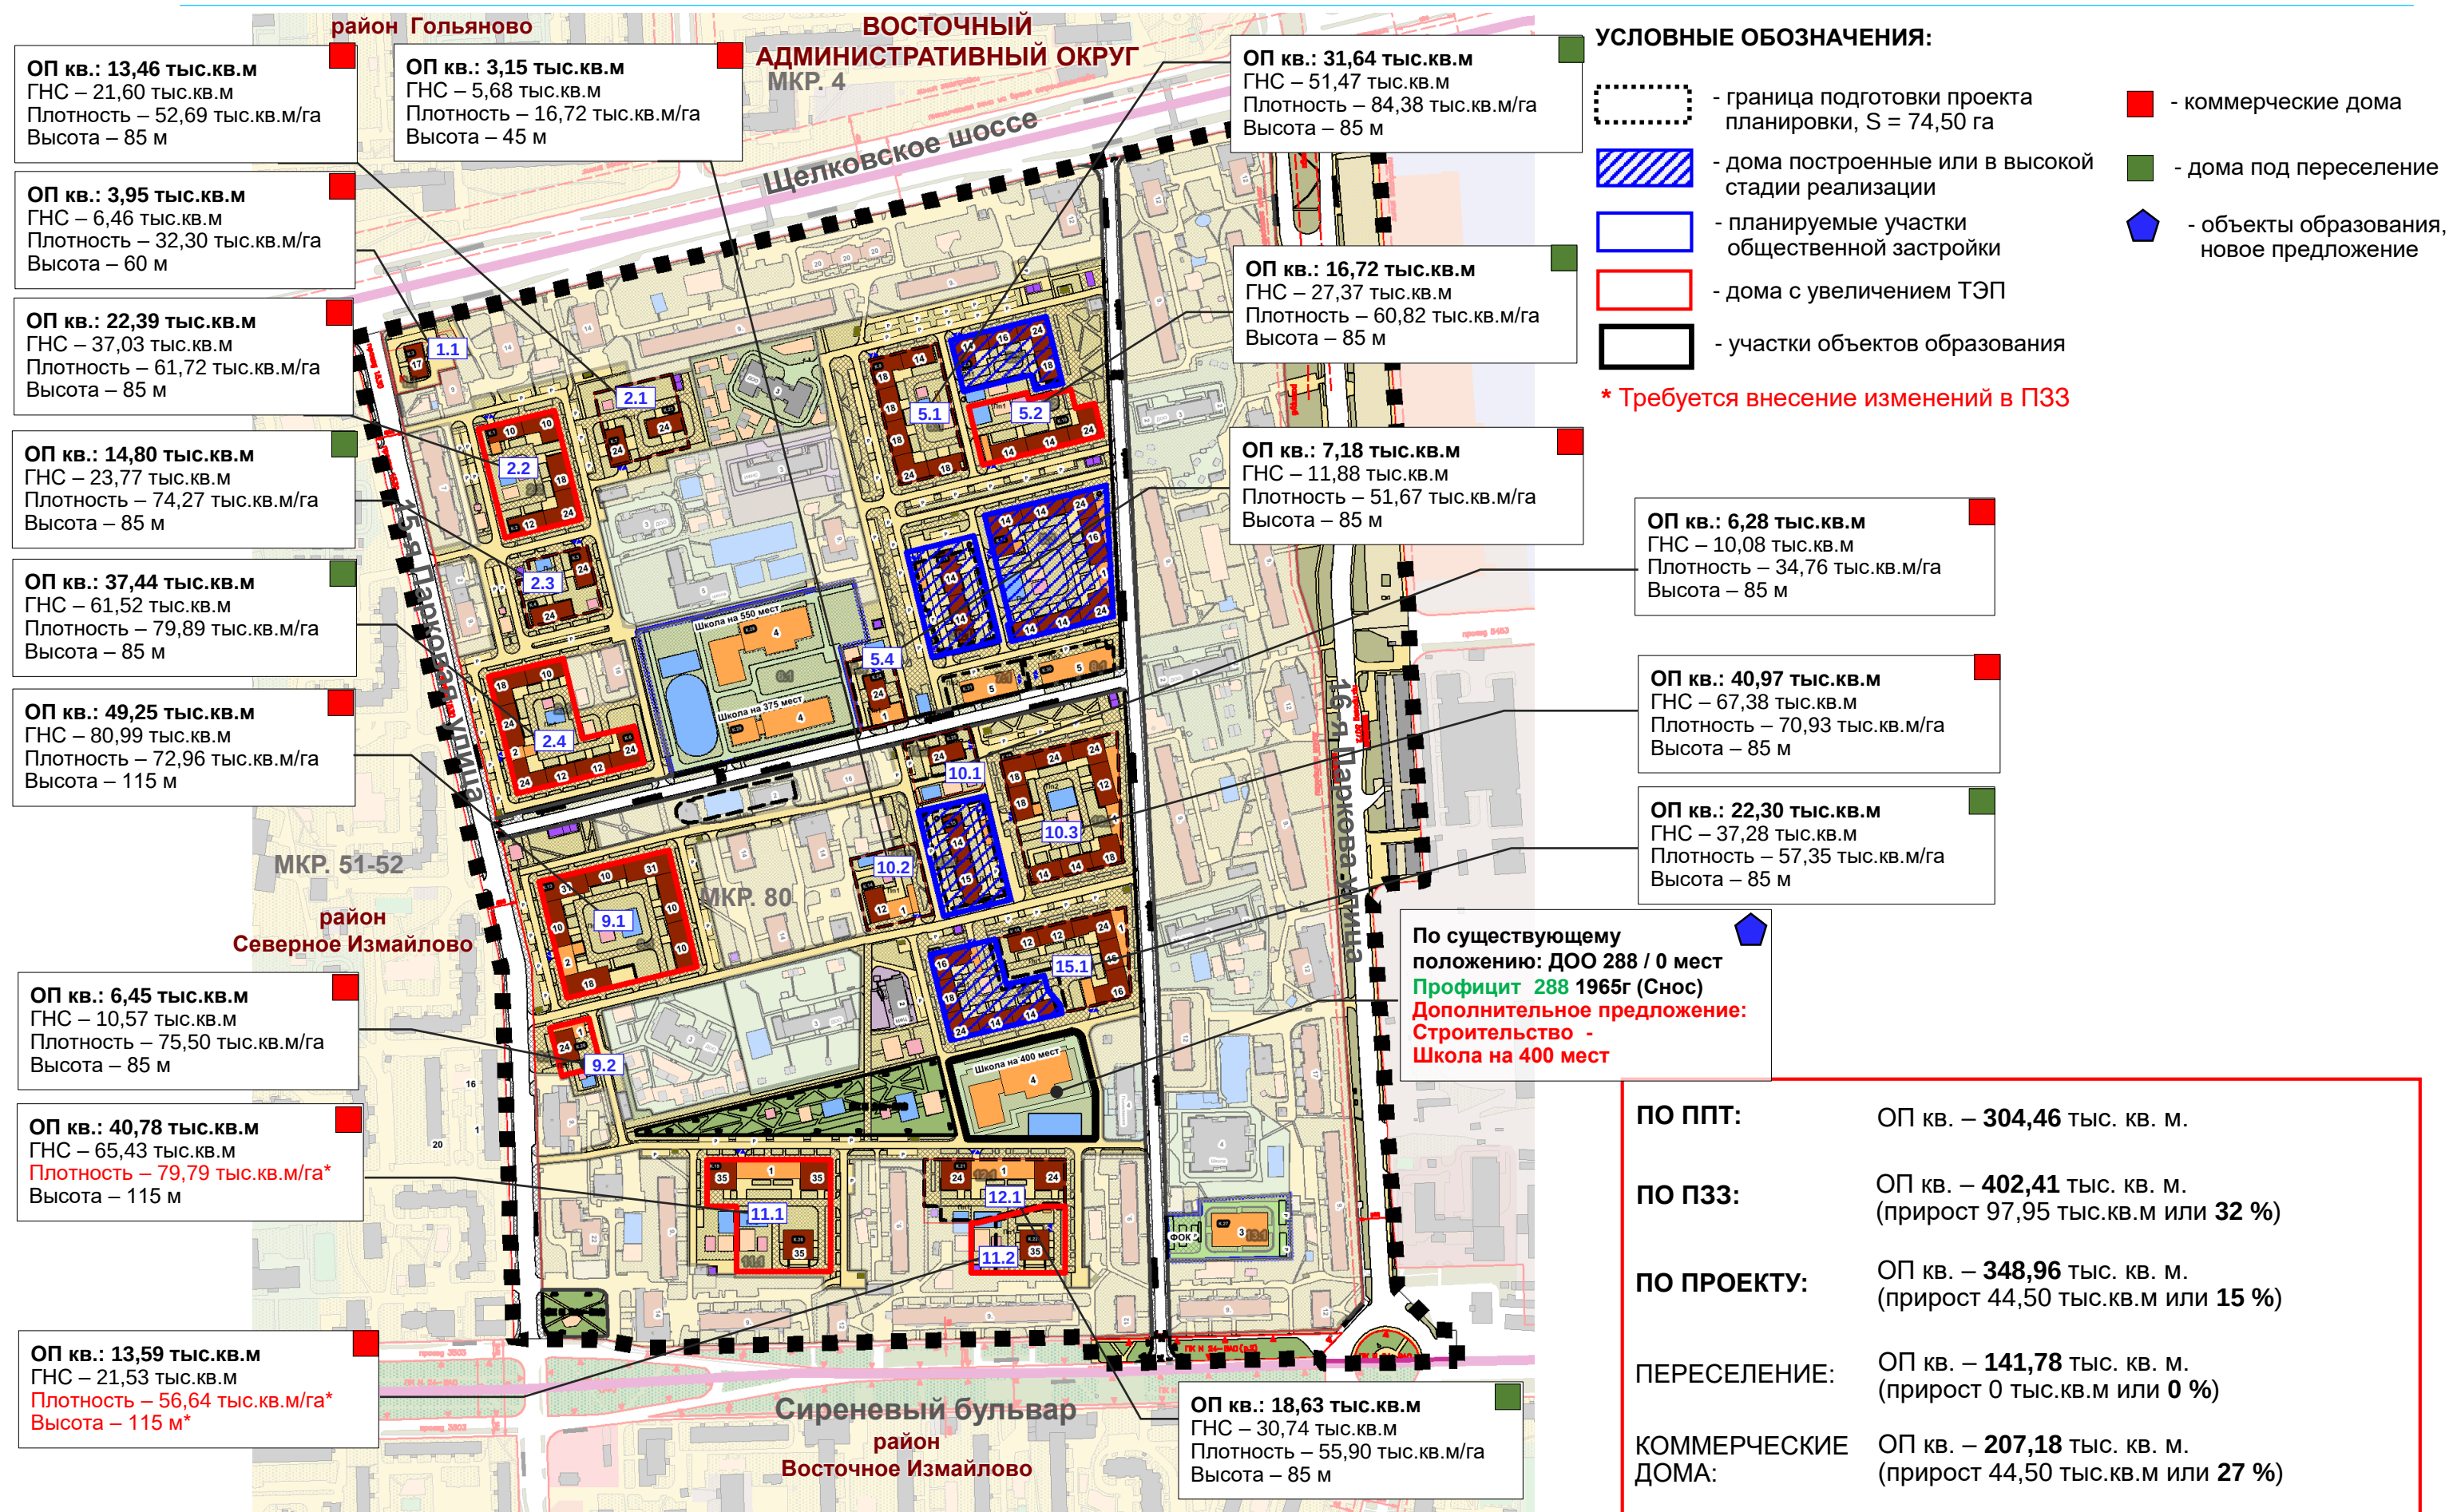

АНАЛИЗ ПРОЕКТНОГО ПРЕДЛОЖЕНИЯ НА ПРЕДМЕТ ОБЕСПЕЧЕННОСТИ ТЕРРИТОРИИ ОБЪЕКТАМИ ОБРАЗОВАНИЯ

Проект планировки территории мкр. 37-38, 39 района Северное Измайлово города Москвы

Проект планировки территории мкр. 41-42, 43-45, 44-46, 47-48, 49-50 района Северное Измайлово города Москвы

Концепция развития жилых и прилегающих к ним территорий мкр. 51-52 района Северное Измайлово города Москвы

Проект планировки территории мкр. 80 района Северное Измайлово города Москвы



УСЛОВНЫЕ ОБОЗНАЧЕНИЯ

ГРАНИЦЫ:

- граница района Северное Измайлово
- границы территорий кварталов градостроительного развития

ЗАСТРОЙКА:


- существующая сохраняемая
- проектируемая жилая
- проектируемая общественная

ОБЪЕКТЫ ДОО И СОШ:

- участки существующих дошкольных образовательных организаций
- участки существующих общеобразовательных организаций
- участки проектируемых дошкольных образовательных организаций
- участки проектируемых общеобразовательных организаций

- радиусы доступности от участков существующих дошкольных образовательных организаций
- радиусы доступности от участков проектируемых детских садов

ОБЕСПЕЧЕННОСТЬ ТЕРРИТОРИИ ОБЪЕКТАМИ ДОШКОЛЬНЫХ ОБРАЗОВАТЕЛЬНЫХ ОРГАНИЗАЦИЙ. ПРОЕКТНОЕ ПРЕДЛОЖЕНИЕ (ТЕРРИТОРИЯ 1)

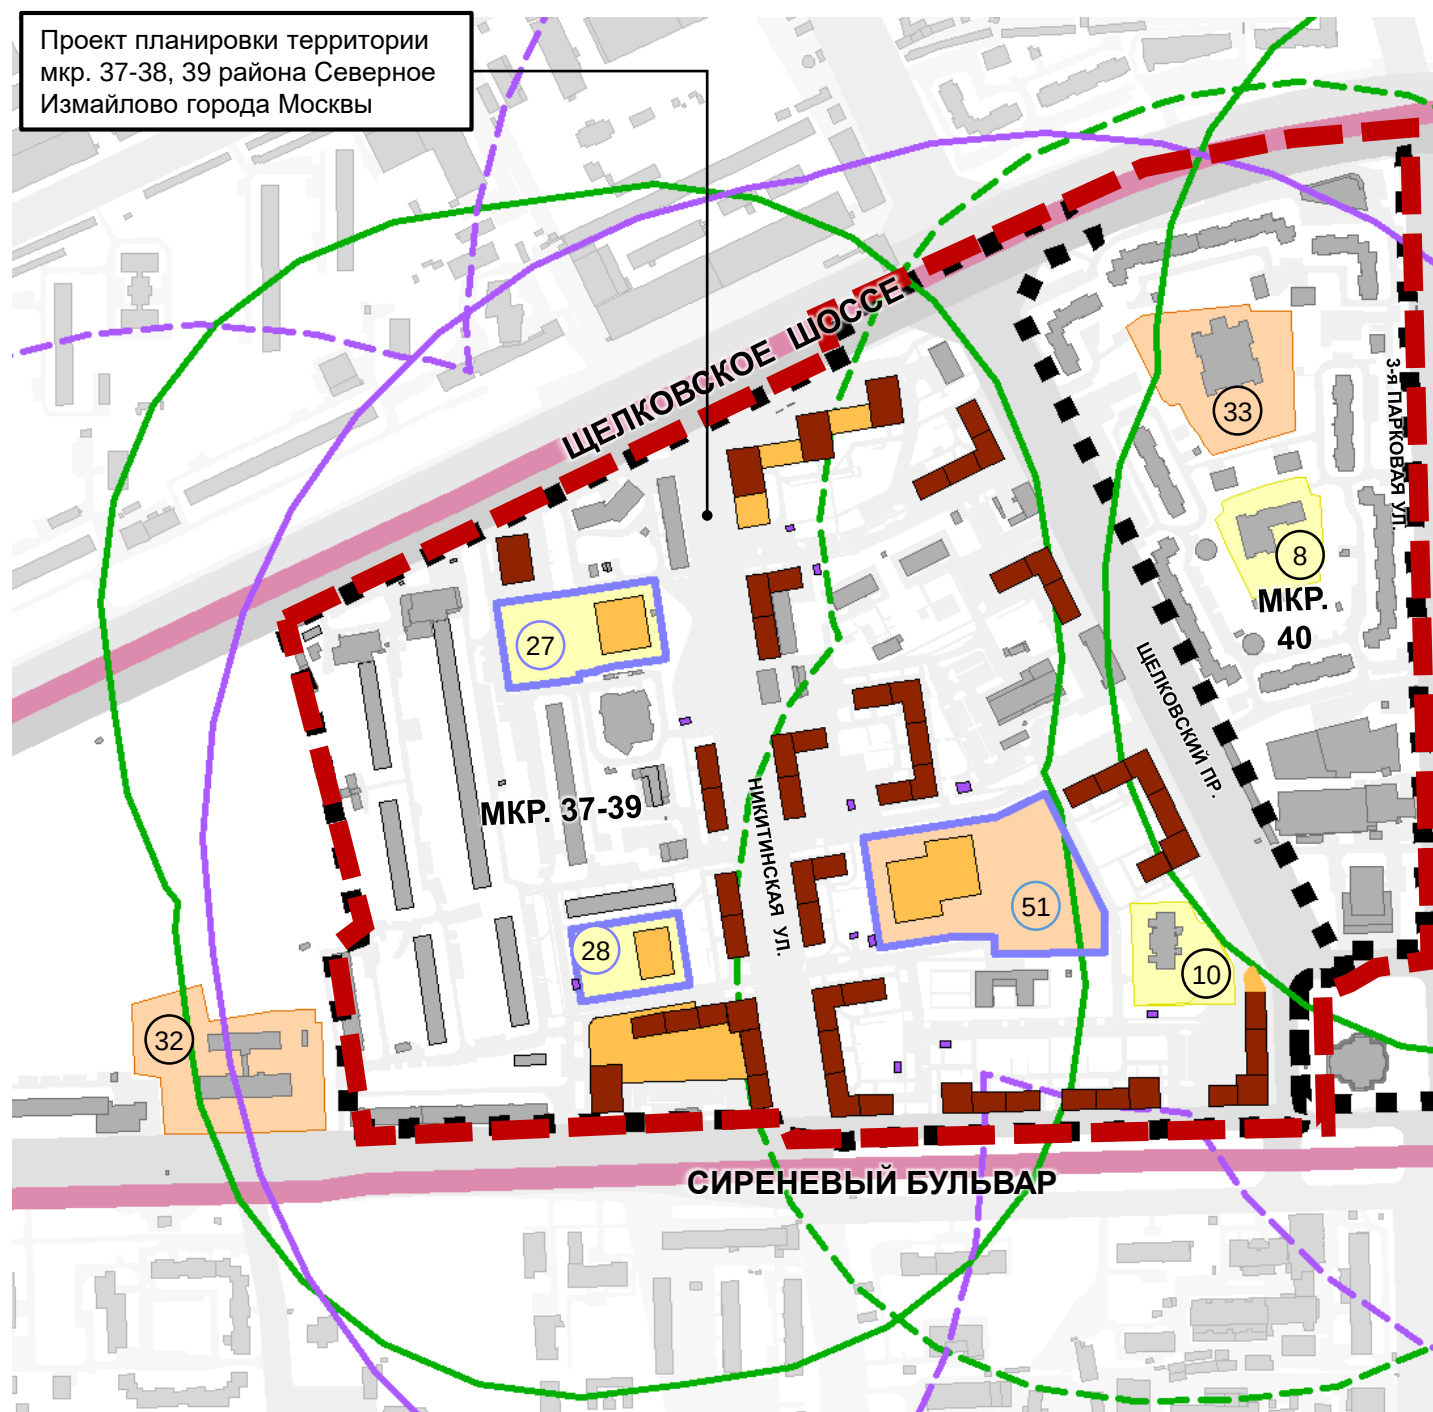

Объекты дошкольного образования в пешеходной доступности от территории 1 (расчетный прирост свободного фонда: 4557 чел.)						
Существующие объекты ДОО						
№ уч.	Наименование объекта	Год постройки	Существующая емкость (расчетная), мест	Фактическая наполняемость, мест	Дефицит / Профицит	Примечание
7	ГБОУ Школа № 2033 (Щелковское ш., д. 14А)	1962	СНОС	67	-67	
8	ГБОУ Школа № 2033 (3-я Парковая ул., д. 61А)	2006	168	0	168	Отселено для проведения ремонта
10	ГБОУ Школа № 2033 (Щелковский пр-д, д. 1А)	2014	150	105	45	
Итого сохраняемые объекты ДОО		-	318	172	146	
Проектируемые объекты ДОО						
№ уч.	Наименование объекта	-	Проектная емкость, мест	Требуется на прирост, мест	Дефицит / Профицит	Примечание
Объекты на территории ППТ						
27	ДОО	-	200	251	74	
28	ДОО	-	125			
Итого проектируемые объекты ДОО		-	325	251	74	
Всего мест ДОО на рассматриваемой территории 1		-	643	423	220	

Данные Департамента образования и науки города Москвы по фактической наполняемости в районе Северное Измайлово актуальны на сентябрь 2022 года.

УСЛОВНЫЕ ОБОЗНАЧЕНИЯ

ГРАНИЦЫ:

- района Северное Измайлово
- территорий кварталов градостроительного развития
- территории 1


ЗАСТРОЙКА:

- существующая сохраняемая
- проектируемая жилая
- проектируемая общественная

ОБЪЕКТЫ ДОО И СОШ:

- участки существующих дошкольных образовательных организаций
- участки существующих общеобразовательных организаций
- участки проектируемых дошкольных образовательных организаций
- участки проектируемых общеобразовательных организаций
- радиусы доступности от участков существующих дошкольных образовательных организаций
- радиусы доступности от участков существующих общеобразовательных организаций
- радиусы доступности от участков проектируемых детских садов
- радиусы доступности от участков проектируемых школ

ОБЕСПЕЧЕННОСТЬ ТЕРРИТОРИИ ОБЪЕКТАМИ ОБЩЕОБРАЗОВАТЕЛЬНЫХ ОРГАНИЗАЦИЙ. ПРОЕКТНОЕ ПРЕДЛОЖЕНИЕ (ТЕРРИТОРИЯ 1)

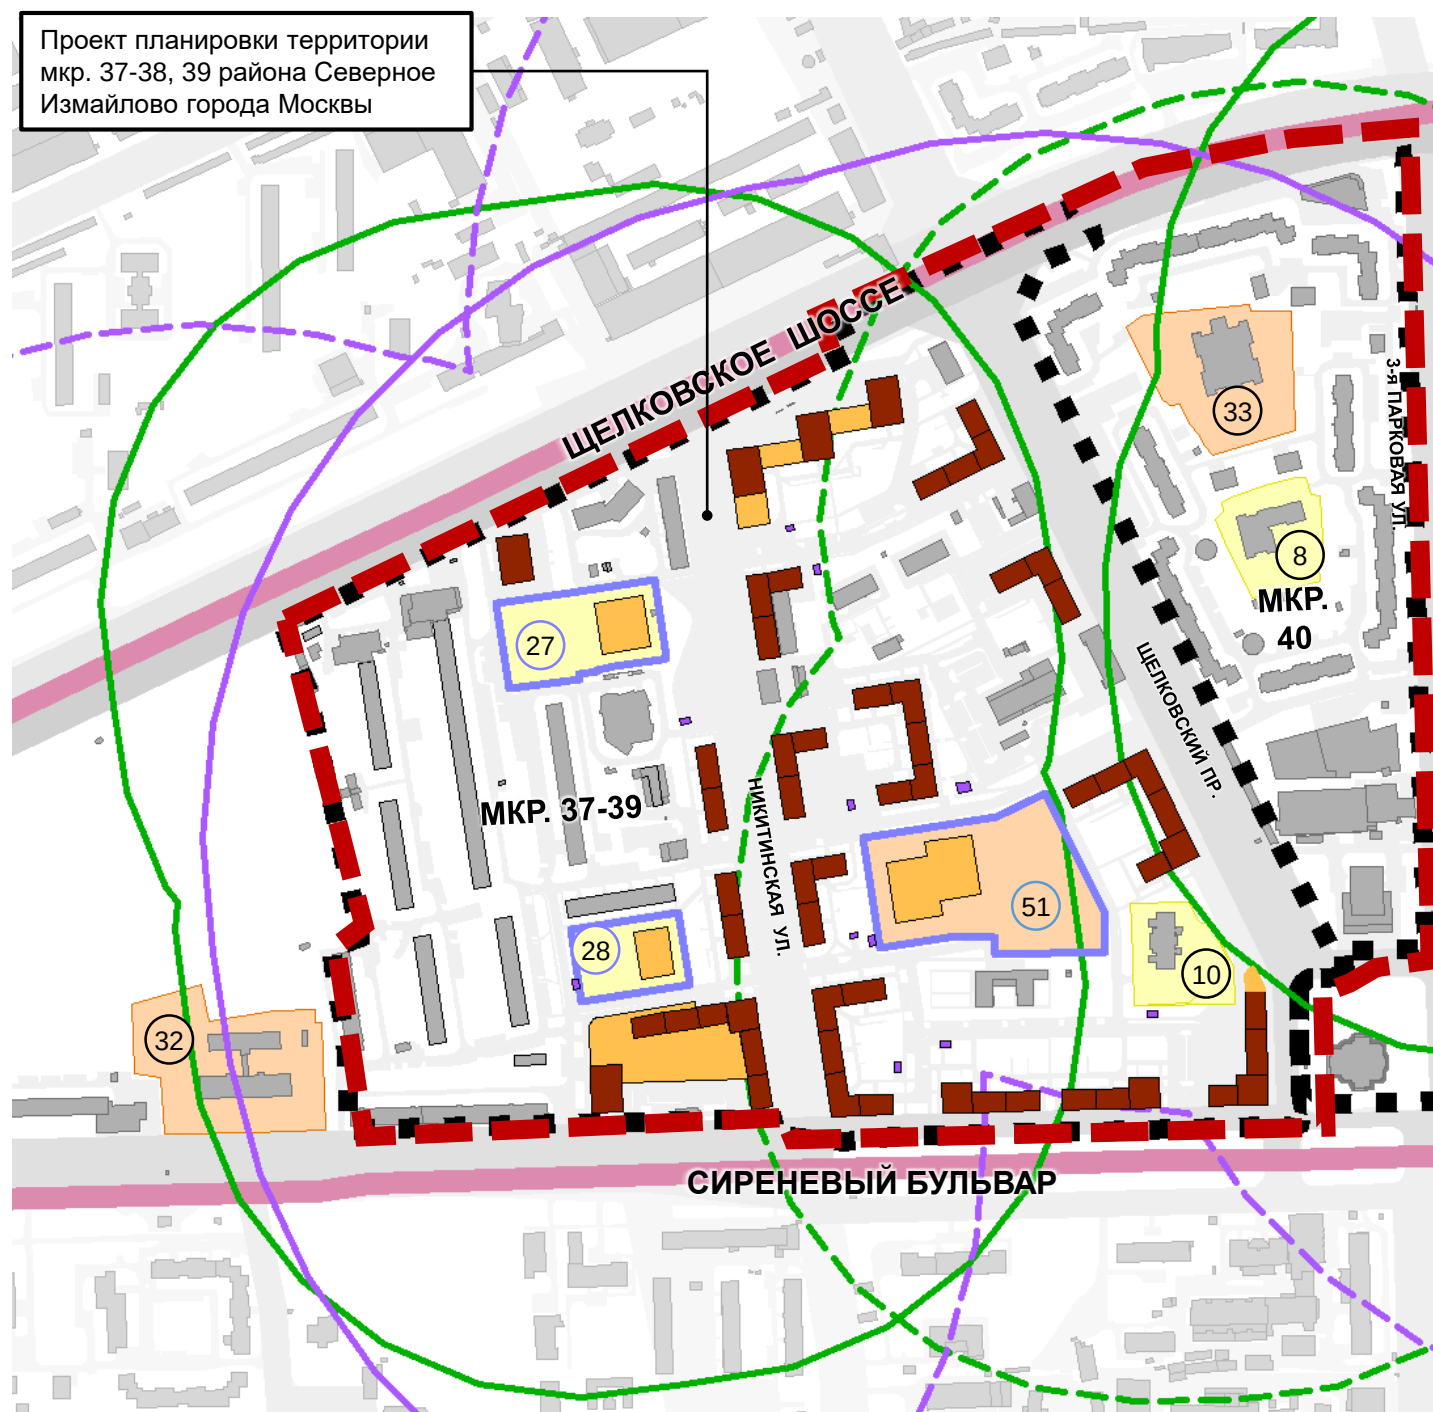

Объекты общего образования в пешеходной доступности от территории 1 (расчетный прирост свободного фонда: 4557 чел.)						
Существующие объекты общего образования						
№ уч.	Наименование объекта	Год постройки	Существующая емкость (расчетная), мест	Фактическая наполняемость, мест	Дефицит / Профицит	Примечание
32	ГБОУ Школа № 2033 (Сиреневый б-р, д. 3)	1972	605	427	178	
33	ГБОУ Школа № 2033 (Щелковское ш., 26А)	2008	605	742	-137	
45	ГБОУ Школа № 2033 (Сиреневый б-р, д. 9)	1962	СНОС	326	-326	
Итого сохраняемые школы		-	1210	1495	-285	
Проектируемые объекты общего образования						
№ уч.	Наименование объекта	-	Проектная емкость, мест	Требуется на прирост, мест	Дефицит / Профицит	Примечание
Объекты на территории ППТ						
51	школа	-	700	510	190	в ППТ на 625
Итого проектируемые школы		-	700	510	190	
Всего школьных мест на рассматриваемой территории 1		-	1910	2005	-95	

Данные Департамента образования и науки города Москвы по фактической наполняемости в районе Северное Измайлово актуальны на сентябрь 2022 года.

УСЛОВНЫЕ ОБОЗНАЧЕНИЯ

ГРАНИЦЫ:

- района Северное Измайлово
- территорий кварталов градостроительного развития
- территории 1


ЗАСТРОЙКА:

- существующая сохраняемая
- проектируемая жилая
- проектируемая общественная

ОБЪЕКТЫ ДОО И СОШ:

- участки существующих дошкольных образовательных организаций
- участки существующих общеобразовательных организаций
- участки проектируемых дошкольных образовательных организаций
- участки проектируемых общеобразовательных организаций
- радиусы доступности от участков существующих дошкольных образовательных организаций
- радиусы доступности от участков существующих общеобразовательных организаций
- радиусы доступности от участков проектируемых детских садов
- радиусы доступности от участков проектируемых школ

ОБЕСПЕЧЕННОСТЬ ТЕРРИТОРИИ ОБЪЕКТАМИ ДОШКОЛЬНЫХ ОБРАЗОВАТЕЛЬНЫХ ОРГАНИЗАЦИЙ. ПРОЕКТНОЕ ПРЕДЛОЖЕНИЕ (ТЕРРИТОРИЯ 2)

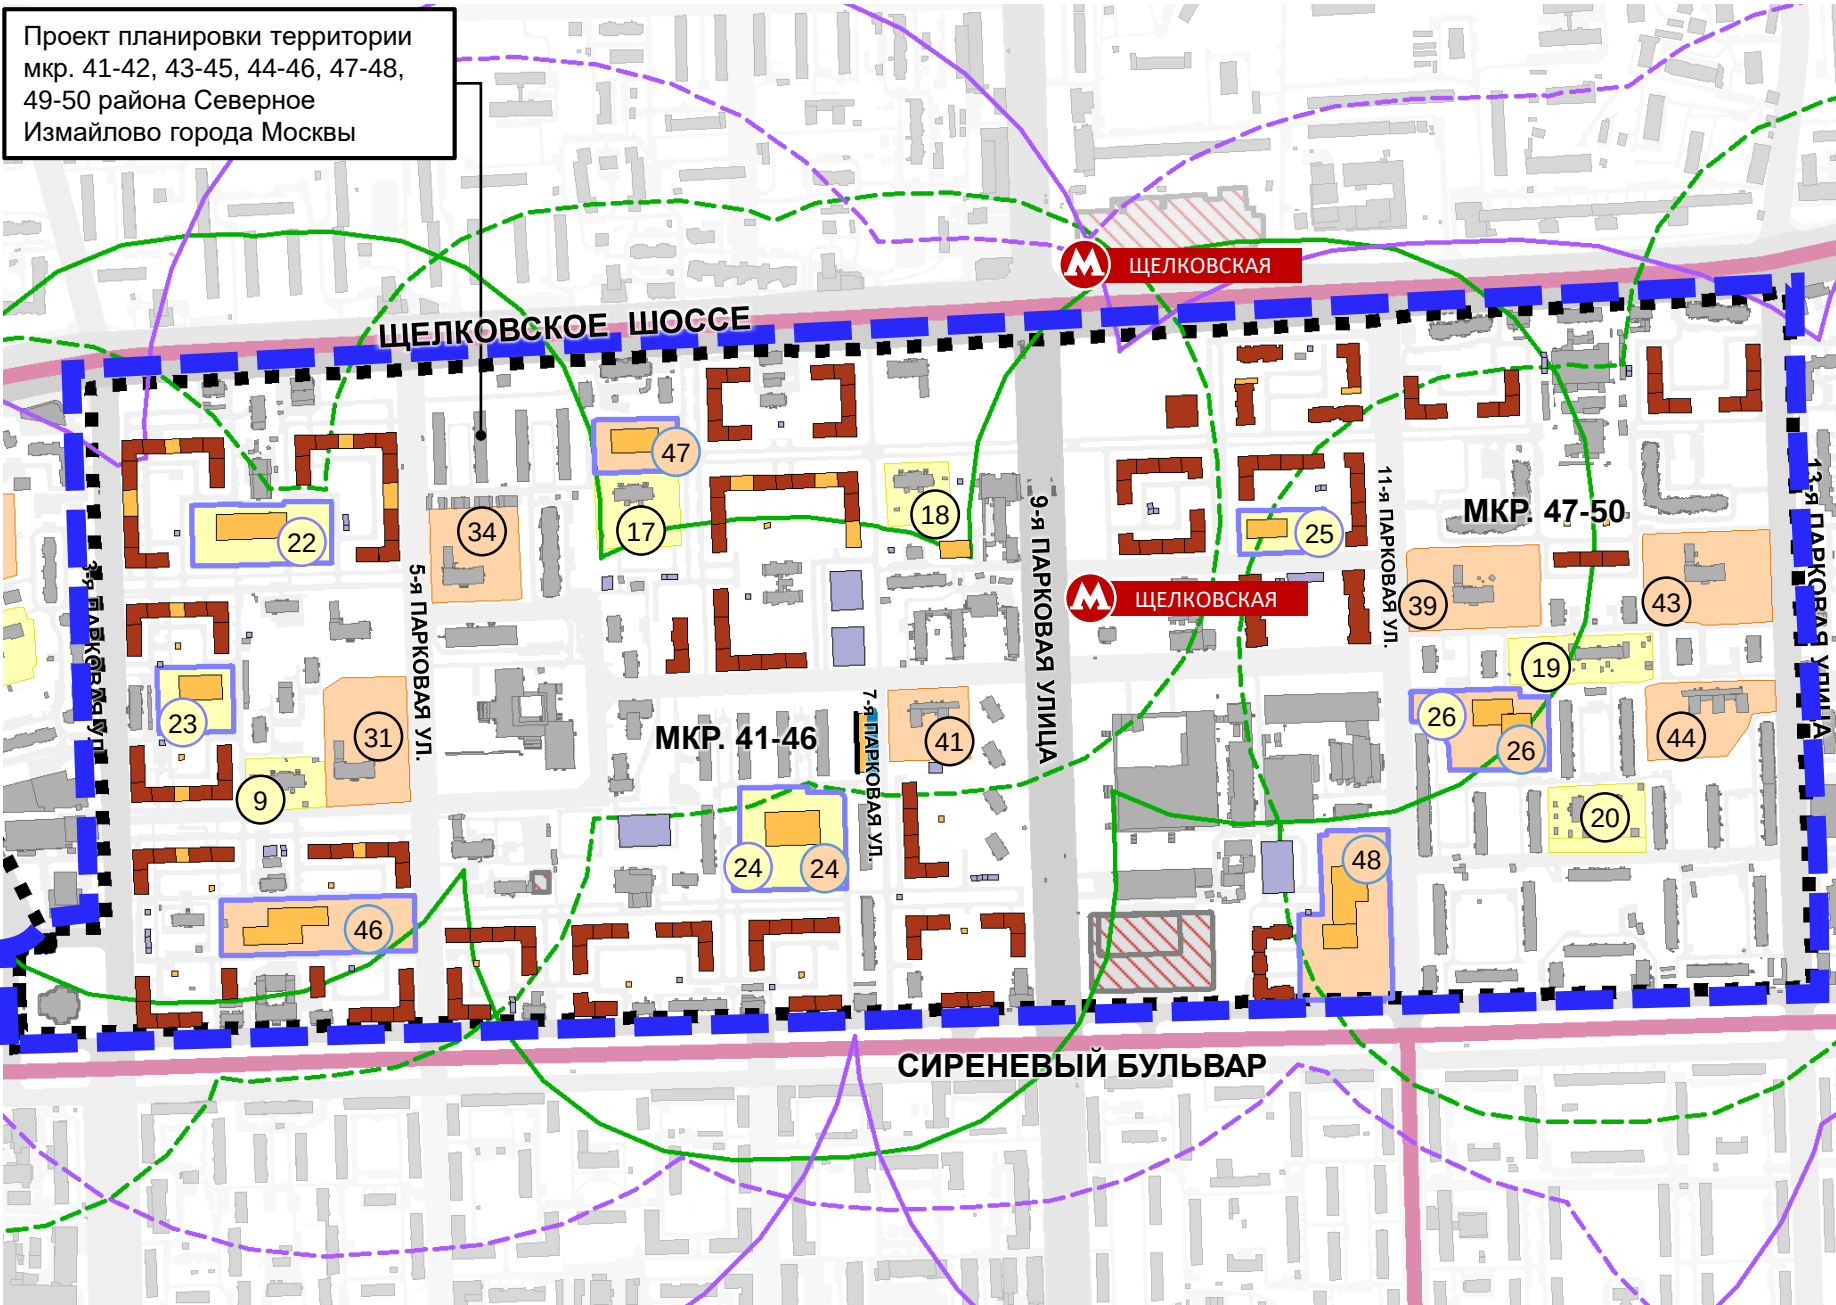

Объекты дошкольного образования в пешеходной доступности от территории 2 (расчетный прирост свободного фонда: 9771 чел.)						
Существующие объекты ДОО						
№ уч.	Наименование объекта	Год постройки	Существующая емкость (расчетная), мест	Фактическая наполняемость, мест	Дефицит / Профицит	Примечание
1	ГБОУ Школа № 444 (7-я Парковая ул., д. 33, корп. 3)	1960	СНОС	98	-98	
6	ГБОУ Школа № 2033 (3-я Парковая ул., д. 54А)	1961	СНОС	50	-50	
9	ГБОУ Школа № 2033 (3-я Парковая ул., д. 46А)	2006	150	109	41	
11	ГБОУ Школа № 2033 (5-я Парковая ул., д. 43А)	1962	СНОС	84	-84	
17	ГБОУ Школа № 2200 (Щелковское ш., д. 44А)	2006	150	150	0	
18	ГБОУ Школа № 2200 (Щелковское ш., д. 52А)	2008	150	140	10	
19	ГБОУ Школа № 2033 (11-я Парковая ул., д. 48А)	1966	288	82	206	
20	ГБОУ Школа № 2033 (11-я Парковая ул., д. 44А)	2013	264	150	114	
21	ГБОУ Школа № 444 (7-я Парковая ул., д. 33, корп. 4)	1960	СНОС	118	-118	
Итого сохраняемые объекты ДОО			1002	981	21	
Проектируемые объекты ДОО						
№ уч.	Наименование объекта	-	Проектная емкость, мест	Требуется на прирост, мест	Дефицит / Профицит	Примечание
Объекты на территории ППТ						
22	ДОО	-	300	537	488	
23	ДОО	-	175			
24	ДОО	-	250			
25	ДОО	-	125			
26	ДОО	-	175			
Итого проектируемые объекты ДОО			1025	537	488	
Всего мест ДОО на рассматриваемой территории 2			2027	1518	509	

Данные Департамента образования и науки города Москвы по фактической наполняемости в районе Северное Измайлово актуальны на сентябрь 2022 года.

УСЛОВНЫЕ ОБОЗНАЧЕНИЯ

ГРАНИЦЫ:

- района Северное Измайлово
- территорий кварталов градостроительного развития
- территории 2

ЗАСТРОЙКА:


- существующая сохраняемая
- проектируемая жилая
- проектируемая общественная

ОБЪЕКТЫ ДОО И СОШ:

- участки существующих дошкольных образовательных организаций
- участки существующих общеобразовательных организаций
- участки проектируемых дошкольных образовательных организаций
- участки проектируемых общеобразовательных организаций

- радиусы доступности от участков существующих дошкольных образовательных организаций
- радиусы доступности от участков существующих общеобразовательных организаций
- радиусы доступности от участков проектируемых детских садов
- радиусы доступности от участков проектируемых школ

ОБЕСПЕЧЕННОСТЬ ТЕРРИТОРИИ ОБЪЕКТАМИ ОБЩЕОБРАЗОВАТЕЛЬНЫХ ОРГАНИЗАЦИЙ. ПРОЕКТНОЕ ПРЕДЛОЖЕНИЕ (ТЕРРИТОРИЯ 2)

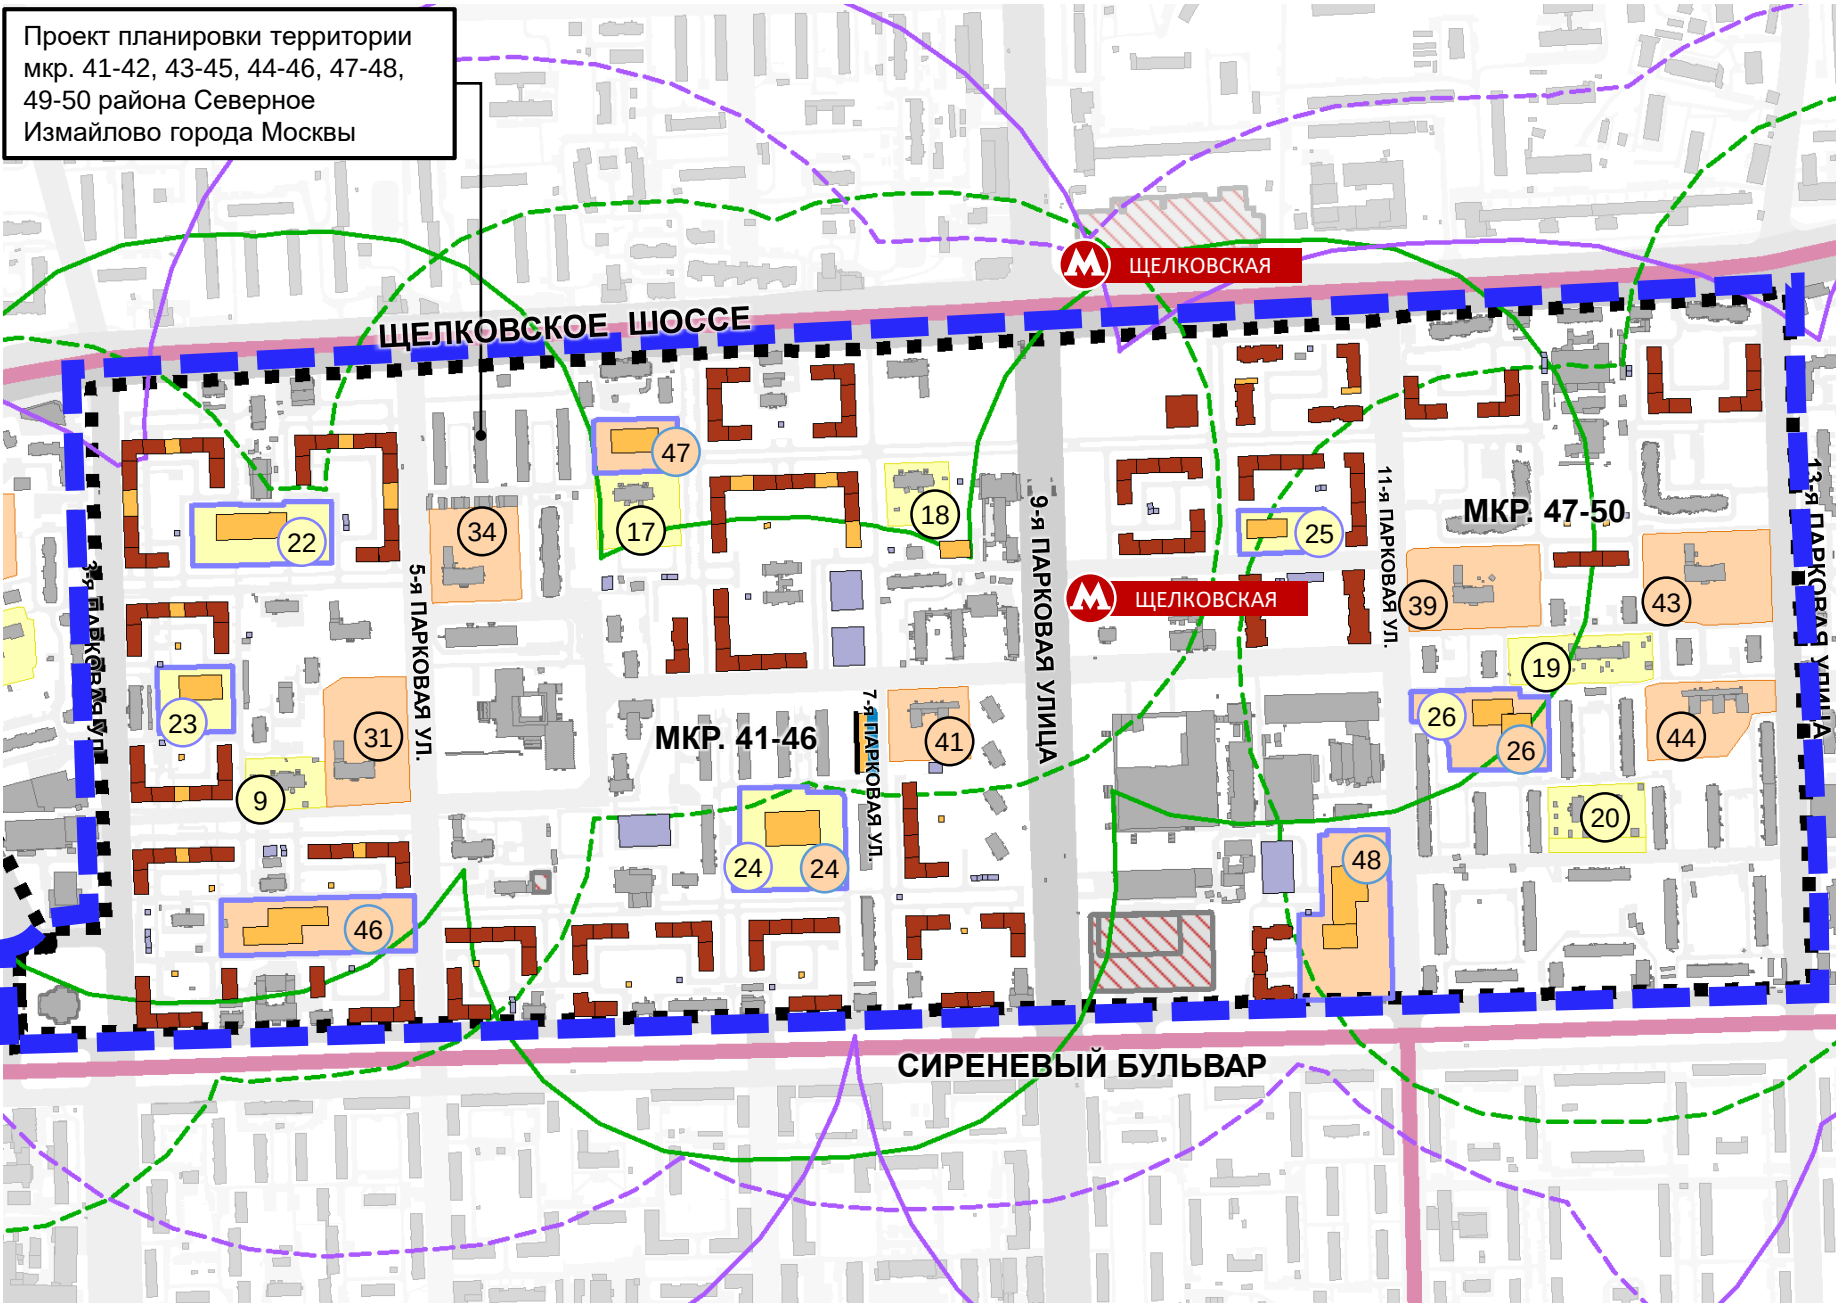

Объекты общего образования в пешеходной доступности от территории 2 (расчетный прирост свободного фонда: 9771 чел.)						
Существующие объекты общего образования						
№ уч.	Наименование объекта	Год постройки	Существующая емкость (расчетная), мест	Фактическая наполняемость, мест	Дефицит / Профицит	Примечание
31	ГБОУ Школа № 2033 (5-я Парковая ул., д. 49)	1996	605	479	126	
34	ГБОУ Школа № 2033 (5-я Парковая ул., д. 62)	1961	605	525	80	
39	ГБОУ Школа № 2200 (11-я Парковая ул., д. 50)	1962	605	567	38	
40	ГБОУ Школа № 2200 (5-я Парковая ул., д. 58Б)	1960	СНОС	122	-122	
41	ГБОУ Школа № 2200 (Константина Федина ул., д. 14)	1964	132	213	-81	
42	ГБОУ Школа № 2200 (Щелковское ш., д. 58А)	1963	СНОС	512	-512	
43	ГБОУ Школа № 2033 (13-я Парковая ул., д. 33)	1963	605	734	-129	
44	ГБОУ Школа № 2033 (13-я Парковая ул., д. 29)	1963	303	340	-37	
Итого сохраняемые школы			2855	3492	-637	
Проектируемые объекты общего образования						
№ уч.	Наименование объекта	-	Проектная емкость, мест	Требуется на прирост, мест	Дефицит / Профицит	Примечание
Объекты на территории ППТ						
46	школа	-	600	1094	856	
47	школа	-	250			
24	школа	-	200			
48	школа	-	700			
26	школа	-	200			
Итого проектируемые школы			1950	1094	856	
Всего школьных мест на рассматриваемой территории 2			4805	4586	219	

Данные Департамента образования и науки города Москвы по фактической наполняемости в районе Северное Измайлово актуальны на сентябрь 2022 года.

УСЛОВНЫЕ ОБОЗНАЧЕНИЯ

ГРАНИЦЫ:

- района Северное Измайлово
- территорий кварталов градостроительного развития
- территории 2

ЗАСТРОЙКА:


- существующая сохраняемая
- проектируемая жилая
- проектируемая общественная

ОБЪЕКТЫ ДОО И СОШ:

- участки существующих дошкольных образовательных организаций
- участки существующих общеобразовательных организаций
- участки проектируемых дошкольных образовательных организаций
- участки проектируемых общеобразовательных организаций

- радиусы доступности от участков существующих дошкольных образовательных организаций
- радиусы доступности от участков существующих общеобразовательных организаций
- радиусы доступности от участков проектируемых детских садов
- радиусы доступности от участков проектируемых школ

ОБЕСПЕЧЕННОСТЬ ТЕРРИТОРИИ ОБЪЕКТАМИ ДОШКОЛЬНЫХ ОБРАЗОВАТЕЛЬНЫХ ОРГАНИЗАЦИЙ. ПРОЕКТНОЕ ПРЕДЛОЖЕНИЕ (ТЕРРИТОРИЯ 3)

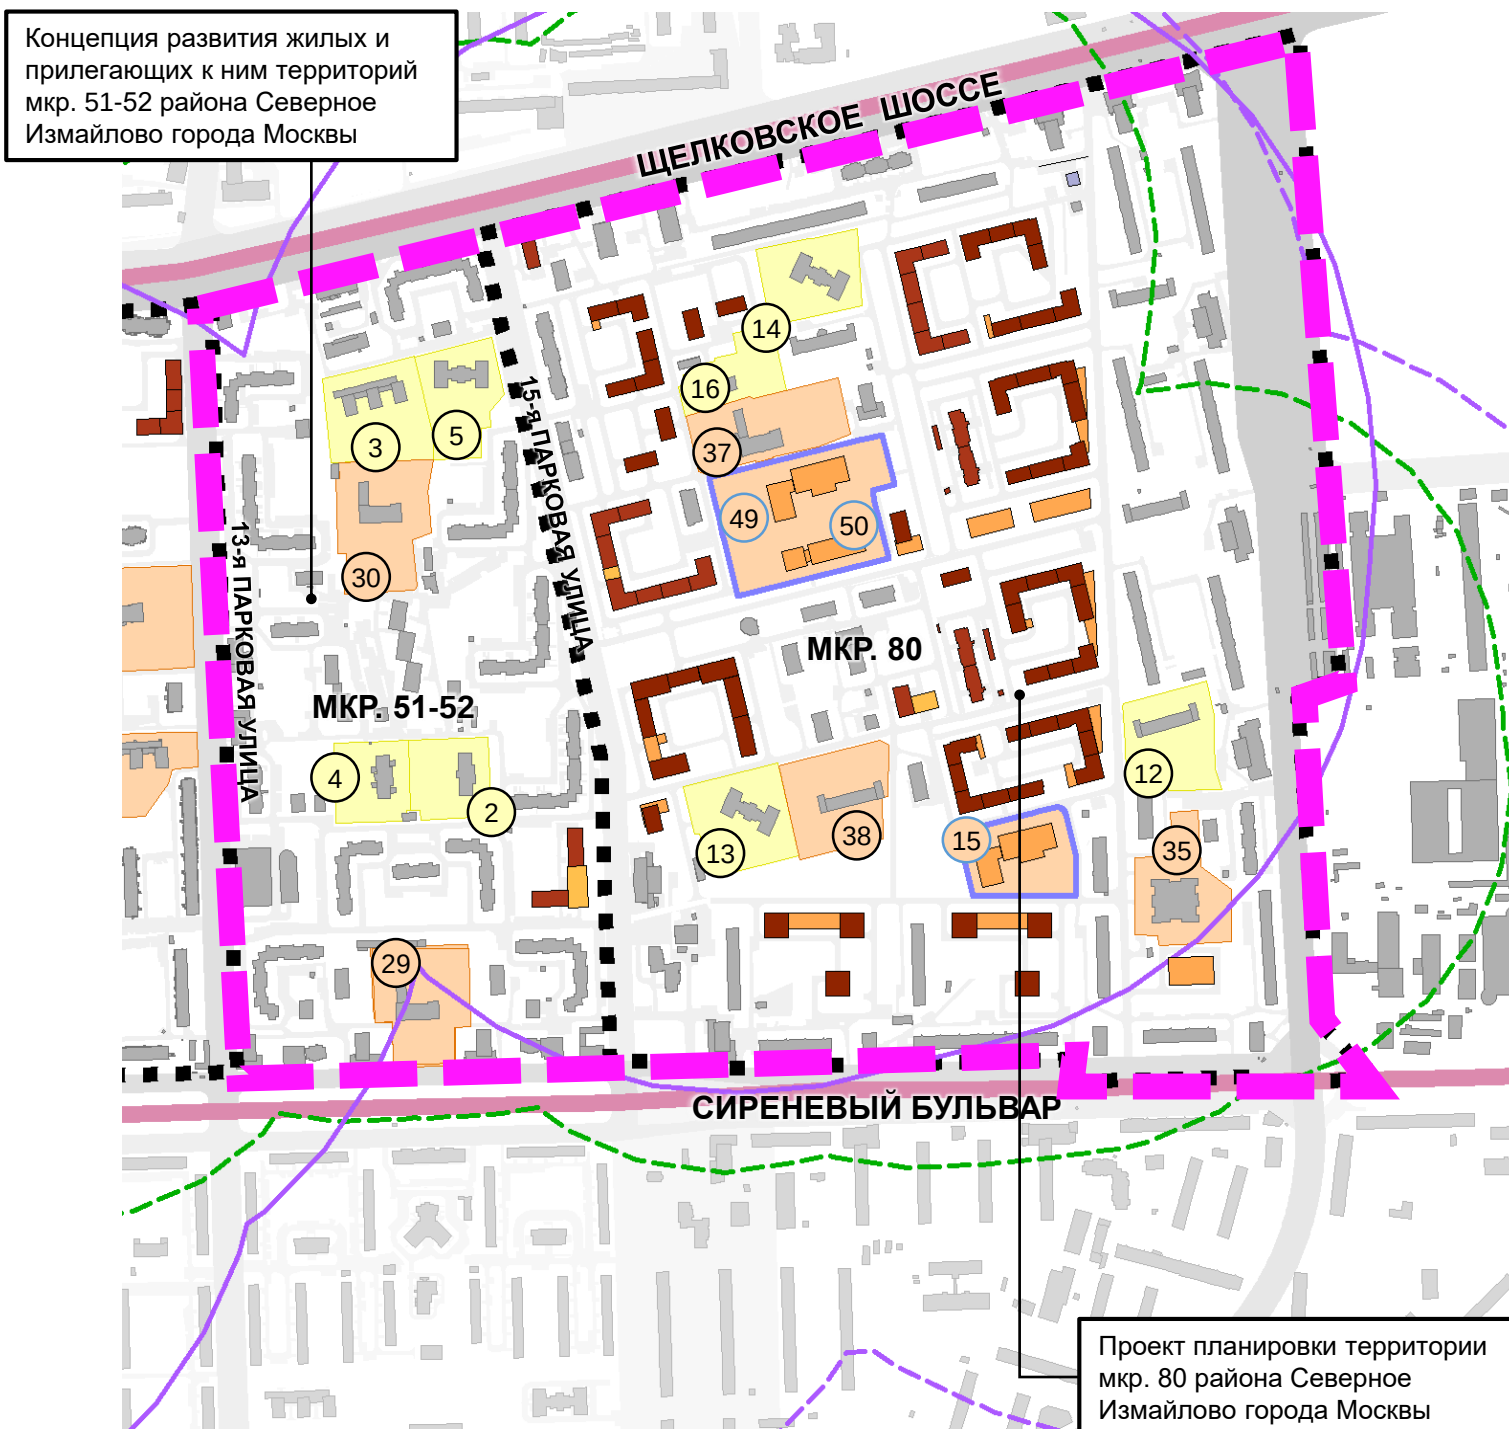

Объекты дошкольного образования в пешеходной доступности от территории 3 (расчетный прирост свободного фонда: 7197 чел., расчетный прирост свободного фонда в КРТ 16-я Парковая ул., вл.16, вл. 30: 1538 чел.)						
Существующие объекты ДОО						
№ уч.	Наименование объекта	Год постройки и	Существующая емкость (расчетная), мест	Фактическая наполняемость, мест	Дефицит / Профицит	Примечание
2	ГБОУ Школа № 2200 (15-я Парковая ул., д. 43)	2008	150	128	22	
3	ГБОУ Школа № 2200 (Щелковское ш., д. 82А)	1963	240	0	240	Только группы кратковременно го пребывания. Возможно использование для групп полного дня.
4	ГБОУ Школа № 2200 (13-я Парковая ул., д. 30)	2008	150	115	35	
5	ГБОУ Школа № 2200 (15-я Парковая ул., д. 51)	2007	264	200	64	
12	ГБОУ Школа № 1748 (16-я Парковая ул., д. 41)	1967	288	130	158	
13	ГБОУ Школа № 1748 (15-я Парковая ул., д. 40)	2013	264	256	8	
14	ГБОУ Школа № 1748 (Щелковское ш., д. 90Б)	2010	264	176	88	
15	ГБОУ Школа № 1748 (Сиреневый б-р, д. 69А)	1965	СНОС	0	-288	
16	ГБОУ Школа № 1748 (Щелковское ш., д. 88А)	2014	150	98	52	
Итого сохраняемые объекты ДОО		-	1770	1103	667	
Проектируемые объекты ДОО						
№ уч.	Наименование объекта	-	Проектная емкость, мест	Требуется на прирост, мест	Дефицит / Профицит	Примечание
Объекты на территории ППТ						
-	ДОО	-	-	373	-373	
Объекты на территории КРТ						
-	ДОО	-	-	85	-85	
Объекты на территории Концепции						
-	ДОО	-	-	23	-23	
Итого проектируемые объекты ДОО		-	-	481	-396	
Всего мест ДОО на рассматриваемой территории 3		-	1770	1584	186	

Данные Департамента образования и науки города Москвы по фактической наполняемости в районе Северное Измайлово актуальны на сентябрь 2022 года.

УСЛОВНЫЕ ОБОЗНАЧЕНИЯ

ГРАНИЦЫ:

- района Северное Измайлово
- территорий кварталов градостроительного развития
- территории 3

ЗАСТРОЙКА:

- существующая сохраняемая
- проектируемая жилая
- проектируемая общественная

ОБЪЕКТЫ ДОО И СОШ:

- участки существующих дошкольных образовательных организаций
- участки существующих общеобразовательных организаций
- участки проектируемых дошкольных образовательных организаций
- участки проектируемых общеобразовательных организаций
- радиусы доступности от участков существующих дошкольных образовательных организаций
- радиусы доступности от участков существующих общеобразовательных организаций
- радиусы доступности от участков проектируемых детских садов
- радиусы доступности от участков проектируемых школ

ОБЕСПЕЧЕННОСТЬ ТЕРРИТОРИИ ОБЪЕКТАМИ ОБЩЕОБРАЗОВАТЕЛЬНЫХ ОРГАНИЗАЦИЙ. ПРОЕКТНОЕ ПРЕДЛОЖЕНИЕ (ТЕРРИТОРИЯ 3)



Объекты общего образования в пешеходной доступности от территории 3 (расчетный прирост свободного фонда: 7197 чел., расчетный прирост свободного фонда в КРТ 16-я Парковая ул., вл.16, вл. 30: 1538 чел.)						
Существующие объекты общего образования						
№ уч.	Наименование объекта	Год постройк и	Существующая емкость (расчетная), мест	Фактическая наполняемость, мест	Дефицит / Профицит	Примечание
29	ГБОУ Школа № 2200 (Сиреневый б-р, д. 55)	1962	468	457	11	
30	ГБОУ Школа № 2200 (Щелковское ш., 82Б)	1963	605	633	-28	
35	ГБОУ Школа № 1748 (Сиреневый б-р, д. 73, корп. 3)	1993	605	637	-32	
36	ГБОУ Школа № 1748 (15-я Парковая ул., д. 46А)	1965	СНОС	465	-465	
37	ГБОУ Школа № 1748 (15-я Парковая ул., д. 52А)	1966	605	310	295	
38	ГБОУ Школа № 1748 (15-я Парковая ул., д. 40А)	1965	220	204	16	
Итого сохраняемые школы		-	2503	2706	-203	
Проектируемые объекты общего образования						
№ уч.	Наименование объекта	-	Проектная емкость, мест	Требуется на прирост, мест	Дефицит / Профицит	Примечание
Объекты на территории ППТ						
15	школа	-	400	760	565	предлагается строительство школы на месте сноса ДОО
49	школа	-	550			
50	школа	-	375			
Объекты на территории КРТ						
-	школа	-	-	172	-172	
Объекты на территории Концепции						
-	школа	-	-	46	-46	
Итого проектируемые школы		-	1325	978	347	
Всего школьных мест на рассматриваемой территории 3		-	3828	3684	144	

Данные Департамента образования и науки города Москвы по фактической наполняемости в районе Северное Измайлово актуальны на сентябрь 2022 года.

УСЛОВНЫЕ ОБОЗНАЧЕНИЯ					
ГРАНИЦЫ:		ОБЪЕКТЫ ДОО И СОШ:			
	района Северное Измайлово		участки существующих дошкольных образовательных организаций		радиусы доступности от участков существующих дошкольных образовательных организаций
	территорий кварталов градостроительного развития		участки существующих общеобразовательных организаций		радиусы доступности от участков существующих общеобразовательных организаций
	территории 3		участки проектируемых дошкольных образовательных организаций		радиусы доступности от участков проектируемых детских садов
ЗАСТРОЙКА:			участки проектируемых общеобразовательных организаций		радиусы доступности от участков проектируемых школ
	существующая сохраняемая				
	проектируемая жилая				
	проектируемая общественная				