

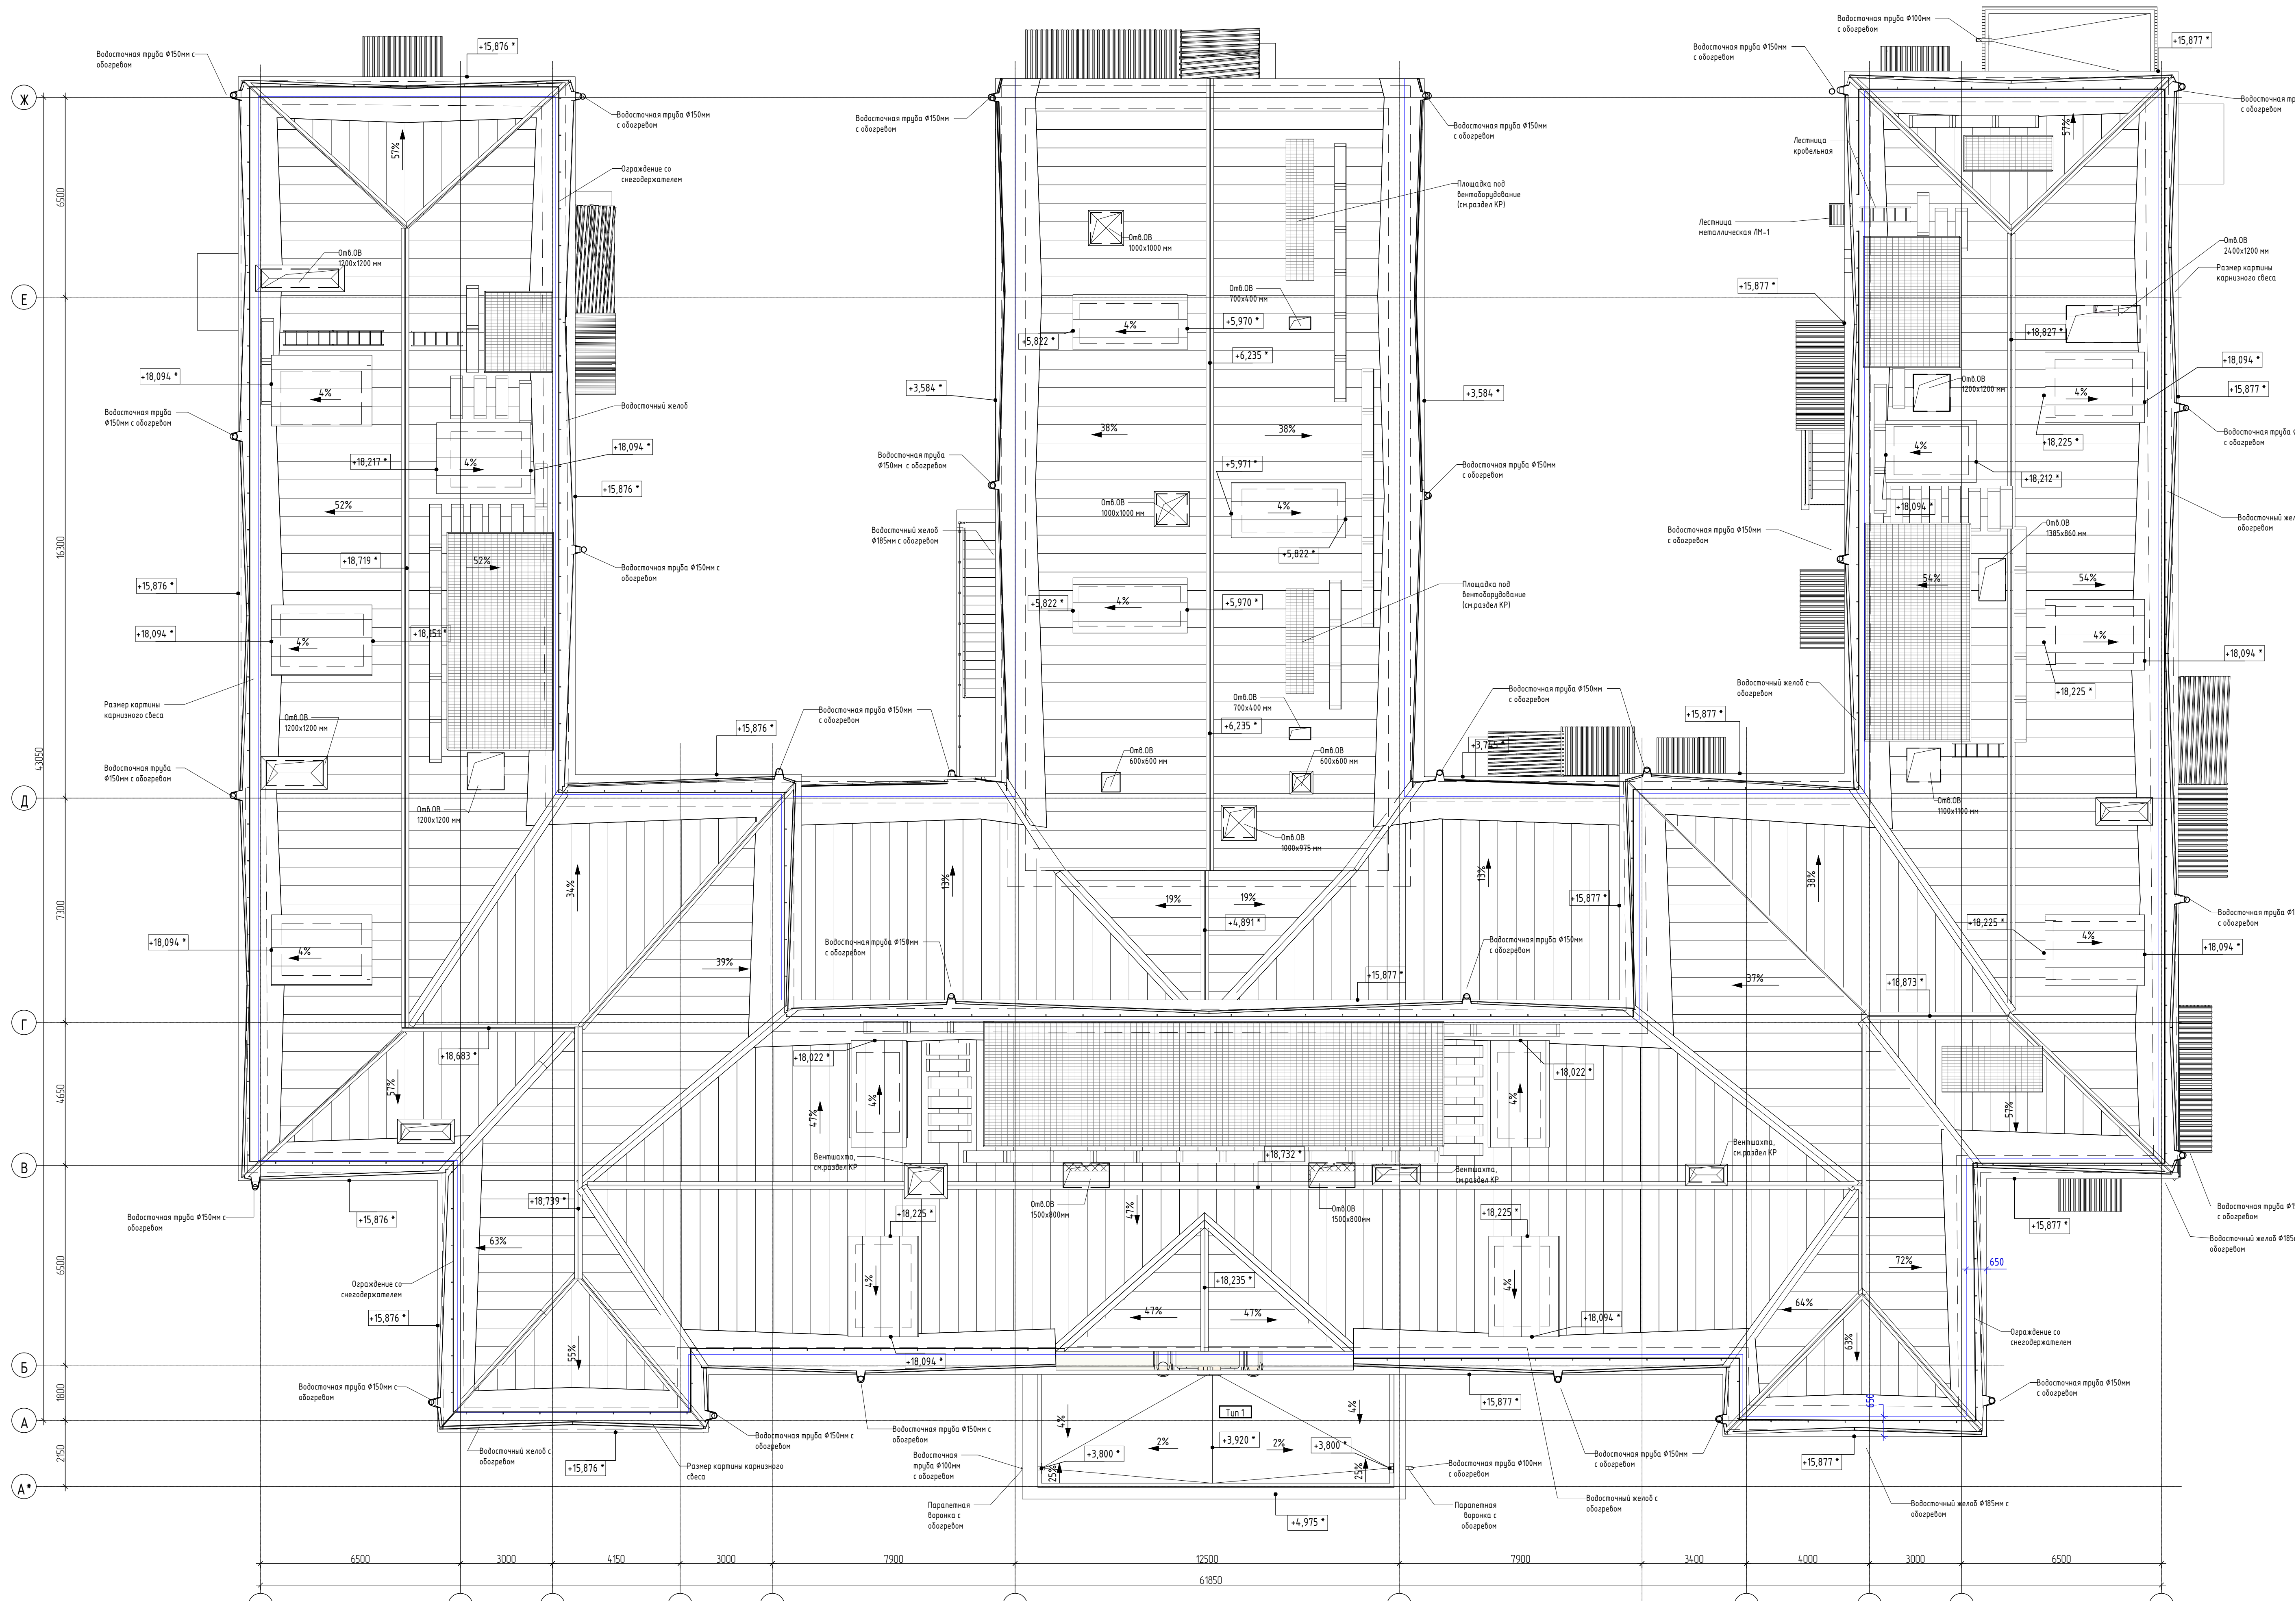


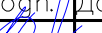


					696/П-24- АНО/ТЗК		
					Выполнение проектно-изыскательских работ на капитальный ремонт общеобразовательного учреждения (ГБОУ Школа №1282 "Сокольники"), по адресу: г. Москва, ул. Барболина, д.1, стр.1		
Изм.	Кол. уч.	Лист	2	док.	Подп.	Дата	
Разраб.	Выжигин	А.В.				10.24	
Проверил	Зеленцов	А.				10.24	
ГИП	Емельянов	А.А.				10.24	
					Обследование технического состояния строительных конструкций и инженерных систем здания		Статус
							Лист
							Листов
							7
					План чертёжа М1:100. Система отопления		ООО "Аркана"
Н. контр.	Циванков	А.А.				10.24	

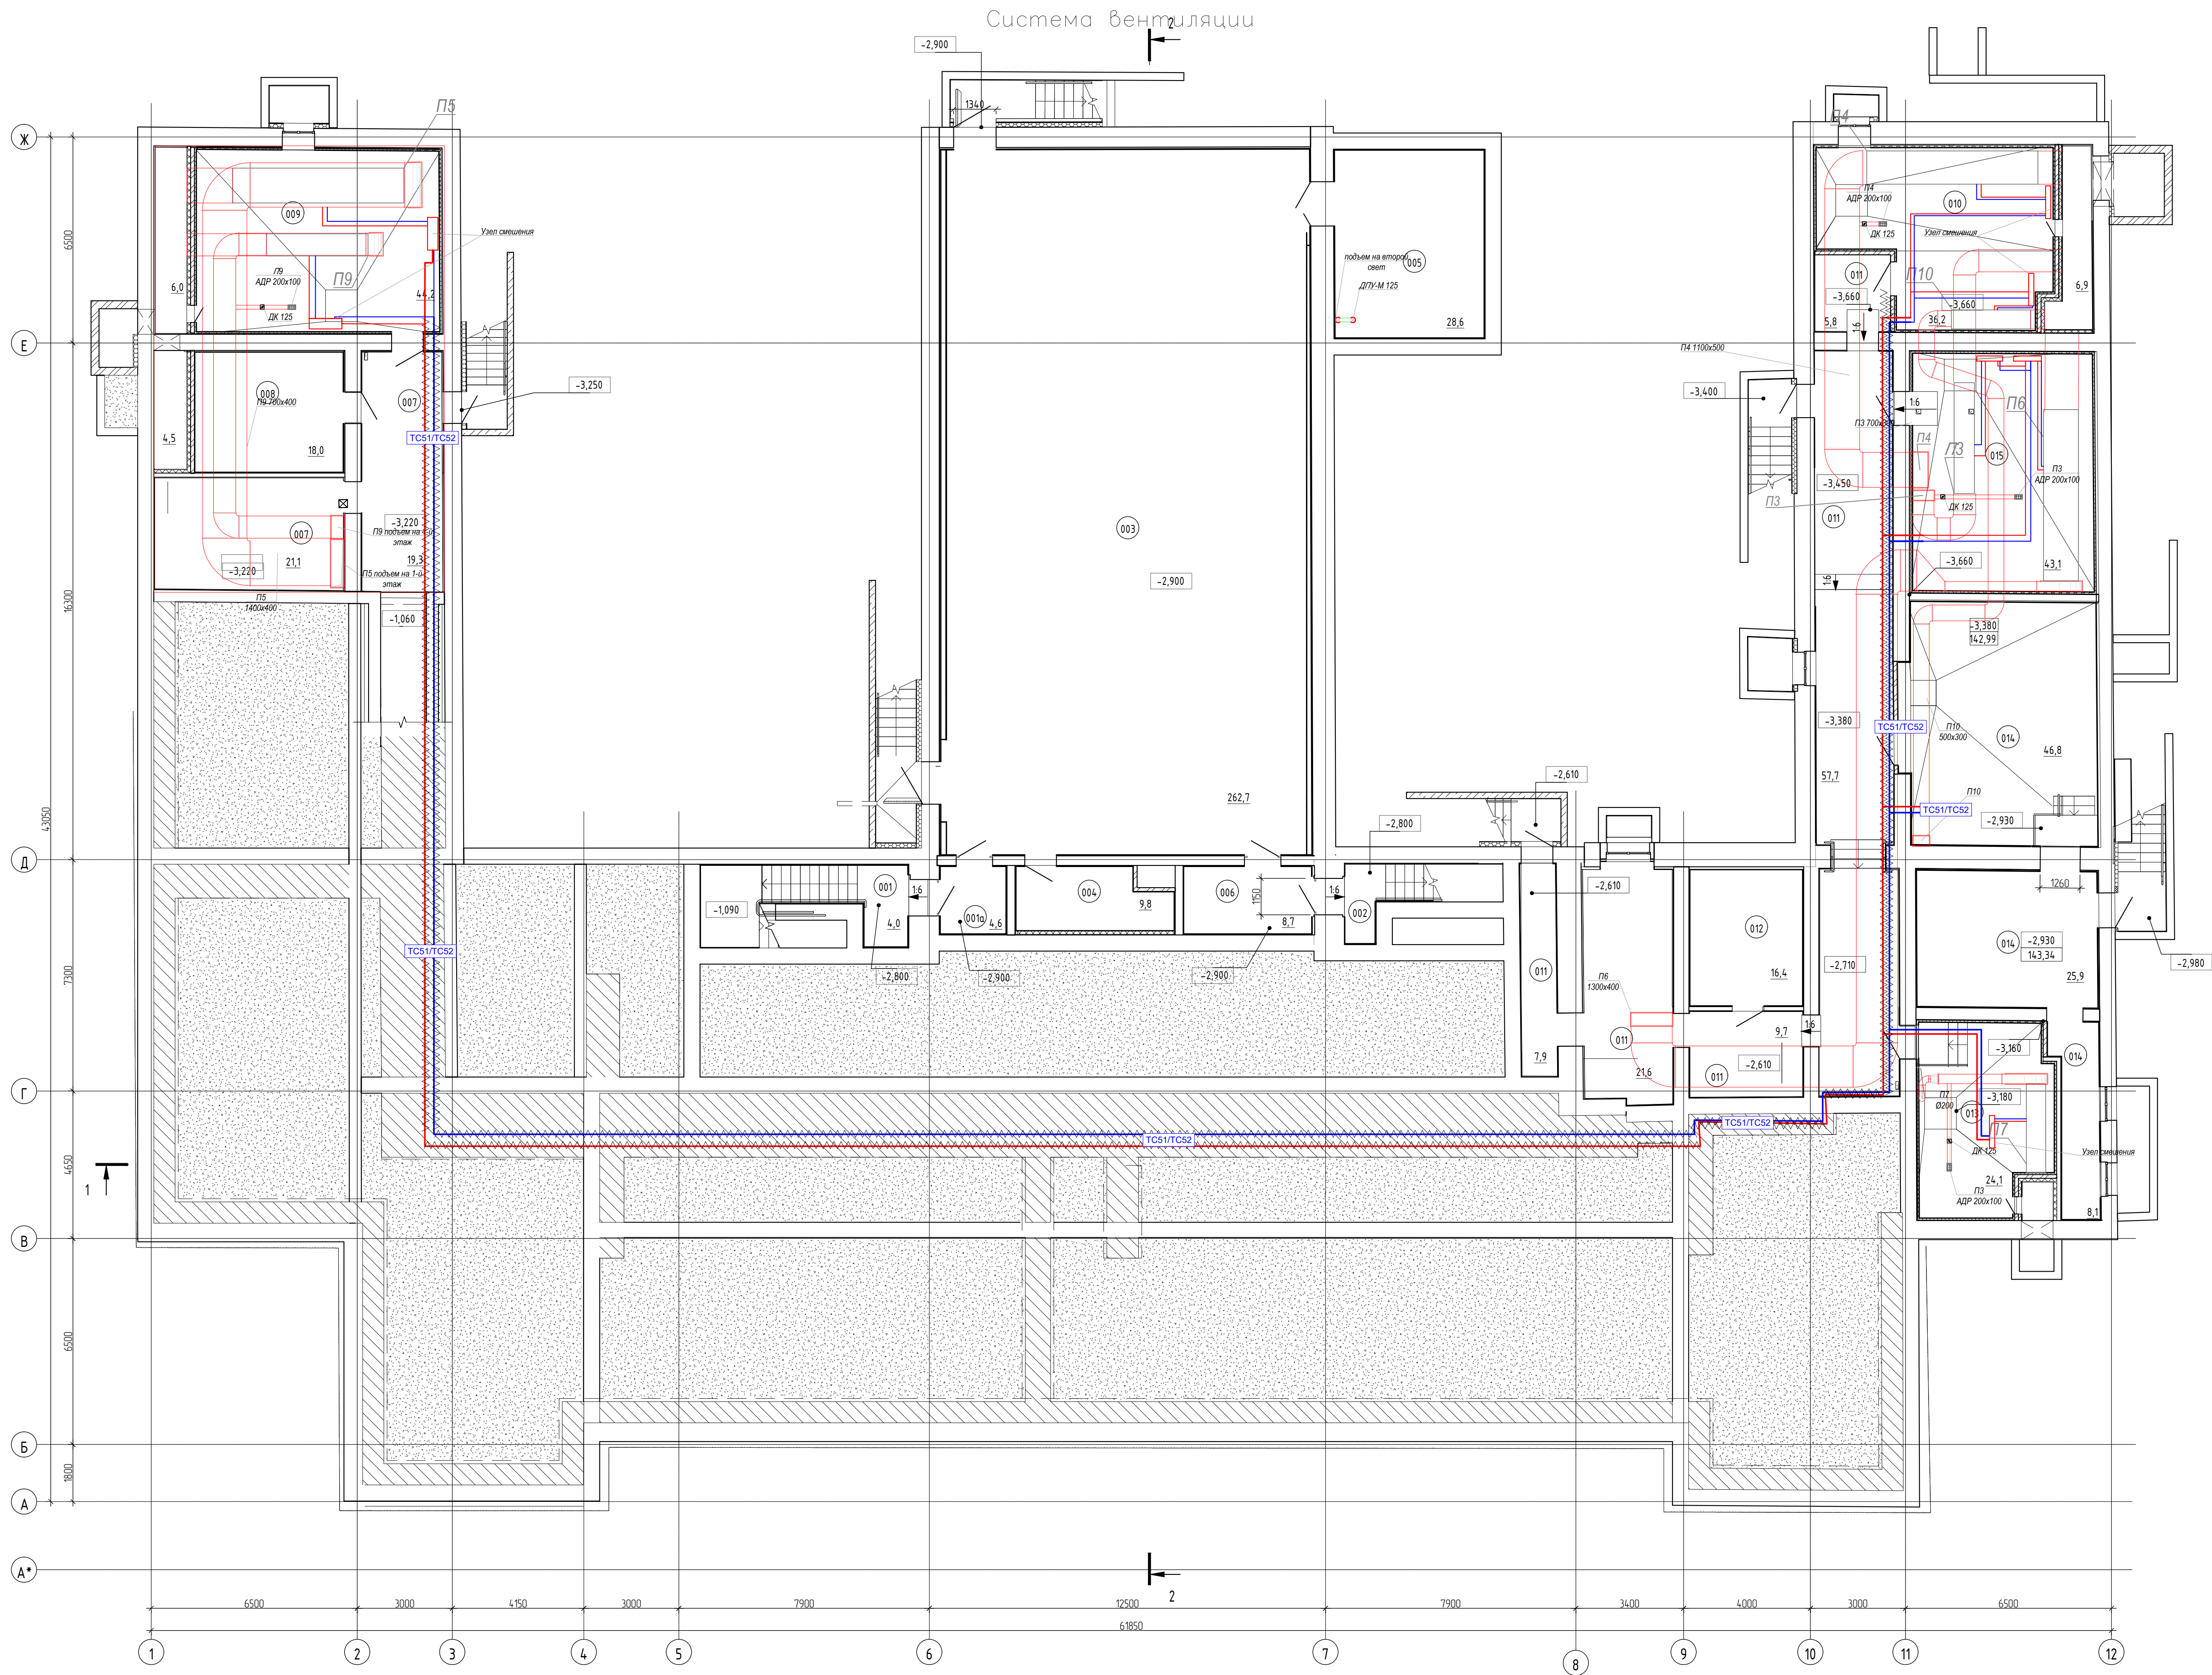

Экспликация помещений			
Номер помеще-ния	Наименование	Площадь, м²	Кат. помеще-ния
001	Технологическая лестница	10,1	
001а	Транз-шлюз 1-го типа	4,6	
002	Технологическая лестница	7,3	
003	Складской зал	262,7	
004	Складская	9,8	В3
005	Складская	28,6	В3
006	Транз-шлюз 1-го типа	8,7	
007	Коридор	40,4	
008	Кладовая	18,0	В3
009	Венткамера	44,2	В4
010	Венткамера	36,2	В4
011	Коридор	102,8	
012	Маслона	16,4	В4
013	Венткамера	24,1	В4
014	ИТП	80,8	Д
015	Венткамера	43,1	В4
		737,8	

- трубопровод ДУ32 дренажный конденсата кондиционеров
- трубопроводы Газ/жидкость фреоновые в изоляции
- трубопроводы теплоснабжения вентустановок

636/П-24-АНО/ТЗК			
Выполнение проектно-изыскательских работ на капитальный ремонт общеобразовательного учреждения (ГБОУ Школа №282 "Соколники"), по адресу: г. Москва, ул. Барбосова, д. 1, стр. 1			
Изм. Вкл. к листу	арк.	Лист	Дата
Разработ.	Землянов А.В.	10.24	10.24
Проверил	Землянов А.В.	10.24	10.24
ГИП	Землянов А.В.	10.24	10.24
осуществление технического сопровождения строительства и инженерных систем здания			
План подвала М1:100. Система вентиляции			
ООО "Аркана"			
Формат А0			

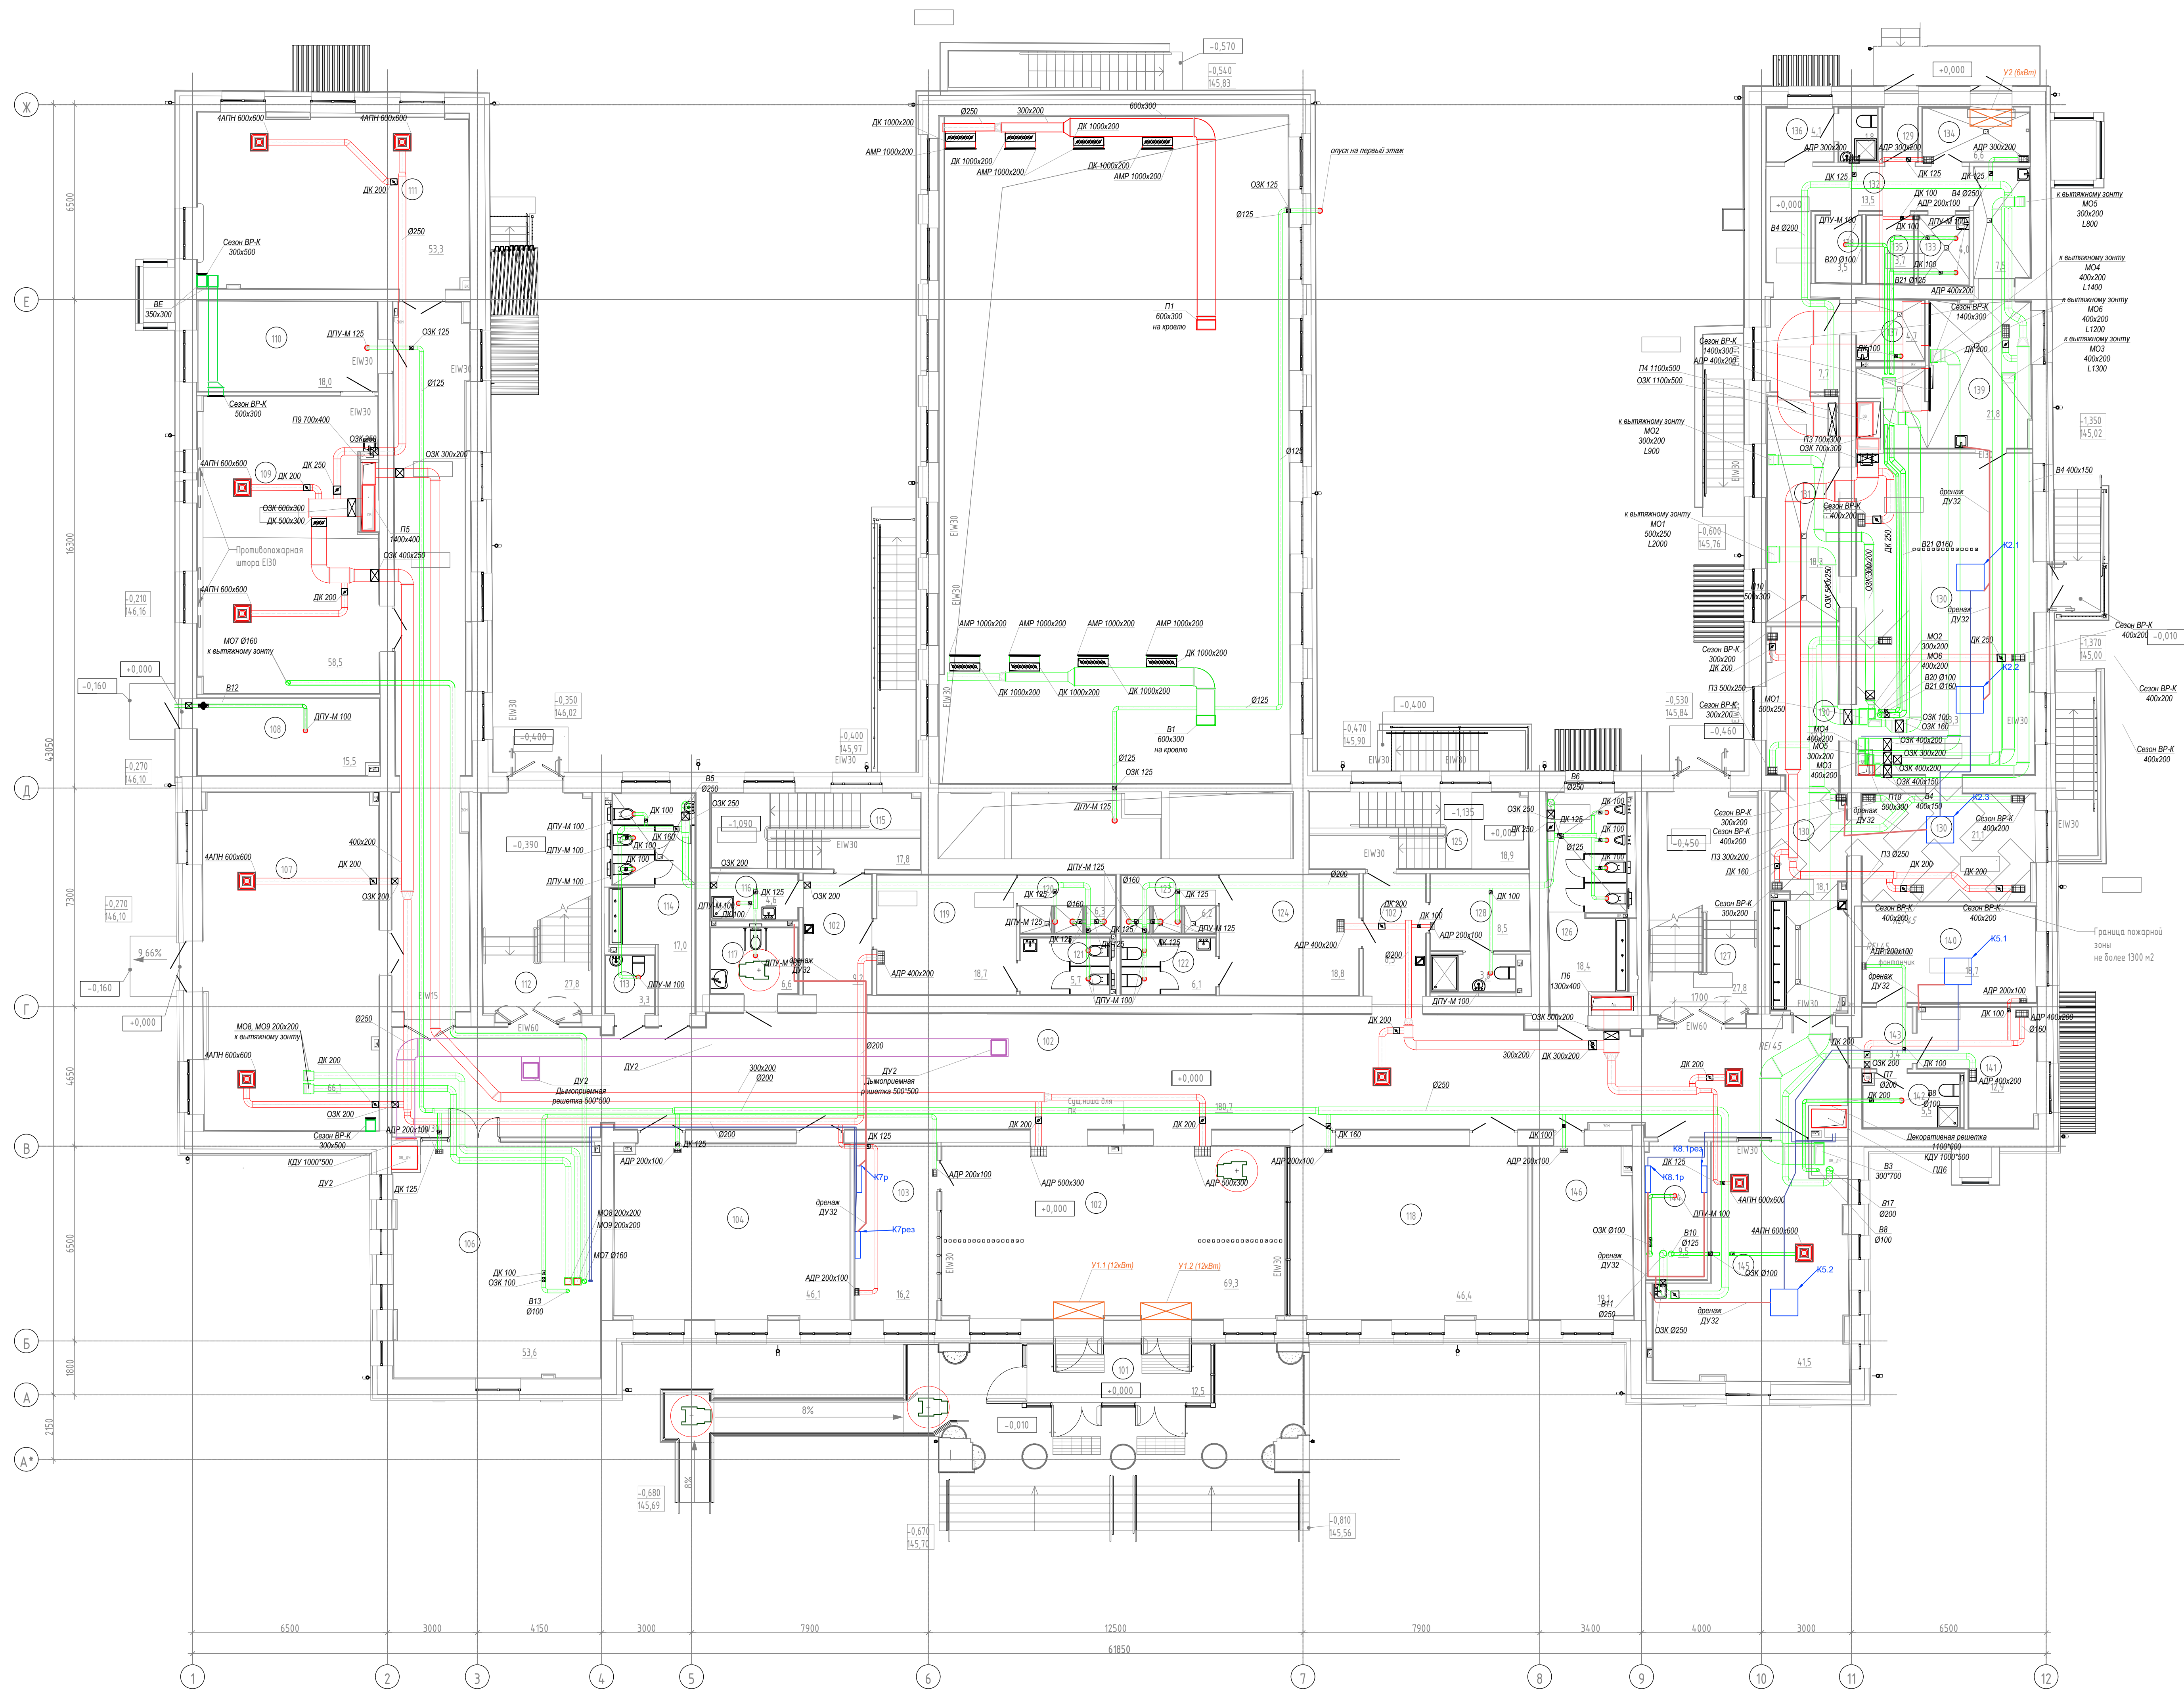


Экспликация помещений 1-го этажа			
Номер помеще-ния	Наименование	Площадь, м²	Кол. помеще-ния
131	Мечеть для столовой посуды	18,4	ВЛ
132	Коридор	21,2	
133	Кладовая и мясная оборотной тары	4,0	ВЛ
134	Загрузочный цех	6,6	ВЛ
135	Кладовая сухих продуктов	3,7	ВЛ
136	Помещение персонала с санузлом	6,0	
137	Помещение для временного хранения пищевых отходов	4,8	ВЛ
138	ПМ	3,5	ВЛ
139	Помещение подготовки для реализации с участием мусора посуды	29,2	ВЛ
140	Кабинет врача	18,7	
141	Процедурный (прибыльный) кабинет	12,9	
142	Помещение для хранения уборочного инвентаря, приготовления дезинфицирующих растворов	5,5	ВЛ
143	Жилая медока	3,4	
144	Помещение СС	9,5	ВЛ
145	Кабинет с рабочим пространством для учителей. Тип 1	41,5	
146	Гардероб для учителей	19,1	
		1254,5	

Экспликация помещений 1-го этажа			
Номер помеще-ния	Наименование	Площадь, м²	Кол. помеще-ния
101	Танбур	12,5	
102	Вестибиль	287,7	
103	Комната охраны (с диспетчерским пунктом)	16,2	
104	Гардероб для обучающихся	46,2	
105	Коридор	59,9	
106	Гардероб для обучающихся	53,7	
107	Эквальный кабинет (Тип 1)	66,1	
108	Электрощитовая	15,5	ВЛ
109	Эквальный кабинет (Тип 2)	58,5	
110	Кладовая	18,0	ВЛ
111	Эквальный кабинет (наполнитель)	53,3	
112	Лестничная клетка (Тип 1)	27,8	
113	Туалет для персонала	3,3	
114	Забора для дежурки	17,0	
115	Технологическая лестница	17,8	
116	ПМ	4,6	ВЛ
117	Универсальная уборная для МН	6,6	
118	Гардероб для обучающихся	44,4	
119	Раздевальня Тип 1	18,7	
120	Душевая	6,3	
121	Забора	5,7	
122	Забора	6,1	
123	Душевая	6,2	
124	Раздевальня Тип 1	18,8	
125	Технологическая лестница	18,9	
126	Забора для мальчиков	18,4	
127	Лестничная клетка (Тип 1)	27,8	
128	Тренерская с санузлом	12,1	
129	Танбур	2,2	
130	Общественный зал	114,5	

- трубопроводы ДВ/32 дренажных конденсата кондиционеров
- трубопроводы Газ/жидкости фреоновые в изоляции
- трубопроводы теплоснабжения вентустановок


636/П-24-АНО/ТЗК			
Выполнение проектно-изыскательских работ на капитальный ремонт общеобразовательного учреждения (ГБОУ Школа №282 "Соколники"), по адресу: г. Москва, ул. Барбаровская, 9, стр. 1			
Исполн. К.И.Шестерин	Дата	10.24	
Проект. В.В.Земсков	Дата	10.24	
Проверил. Зеленин А.В.	Дата	10.24	
ГИП	Емельянов А.В.	10.24	
Н. контр. Цивилев А.В.		10.24	
План 1 этажа М:100. Система вентиляции		000 "Аркона"	
		9	
		Формат А0	

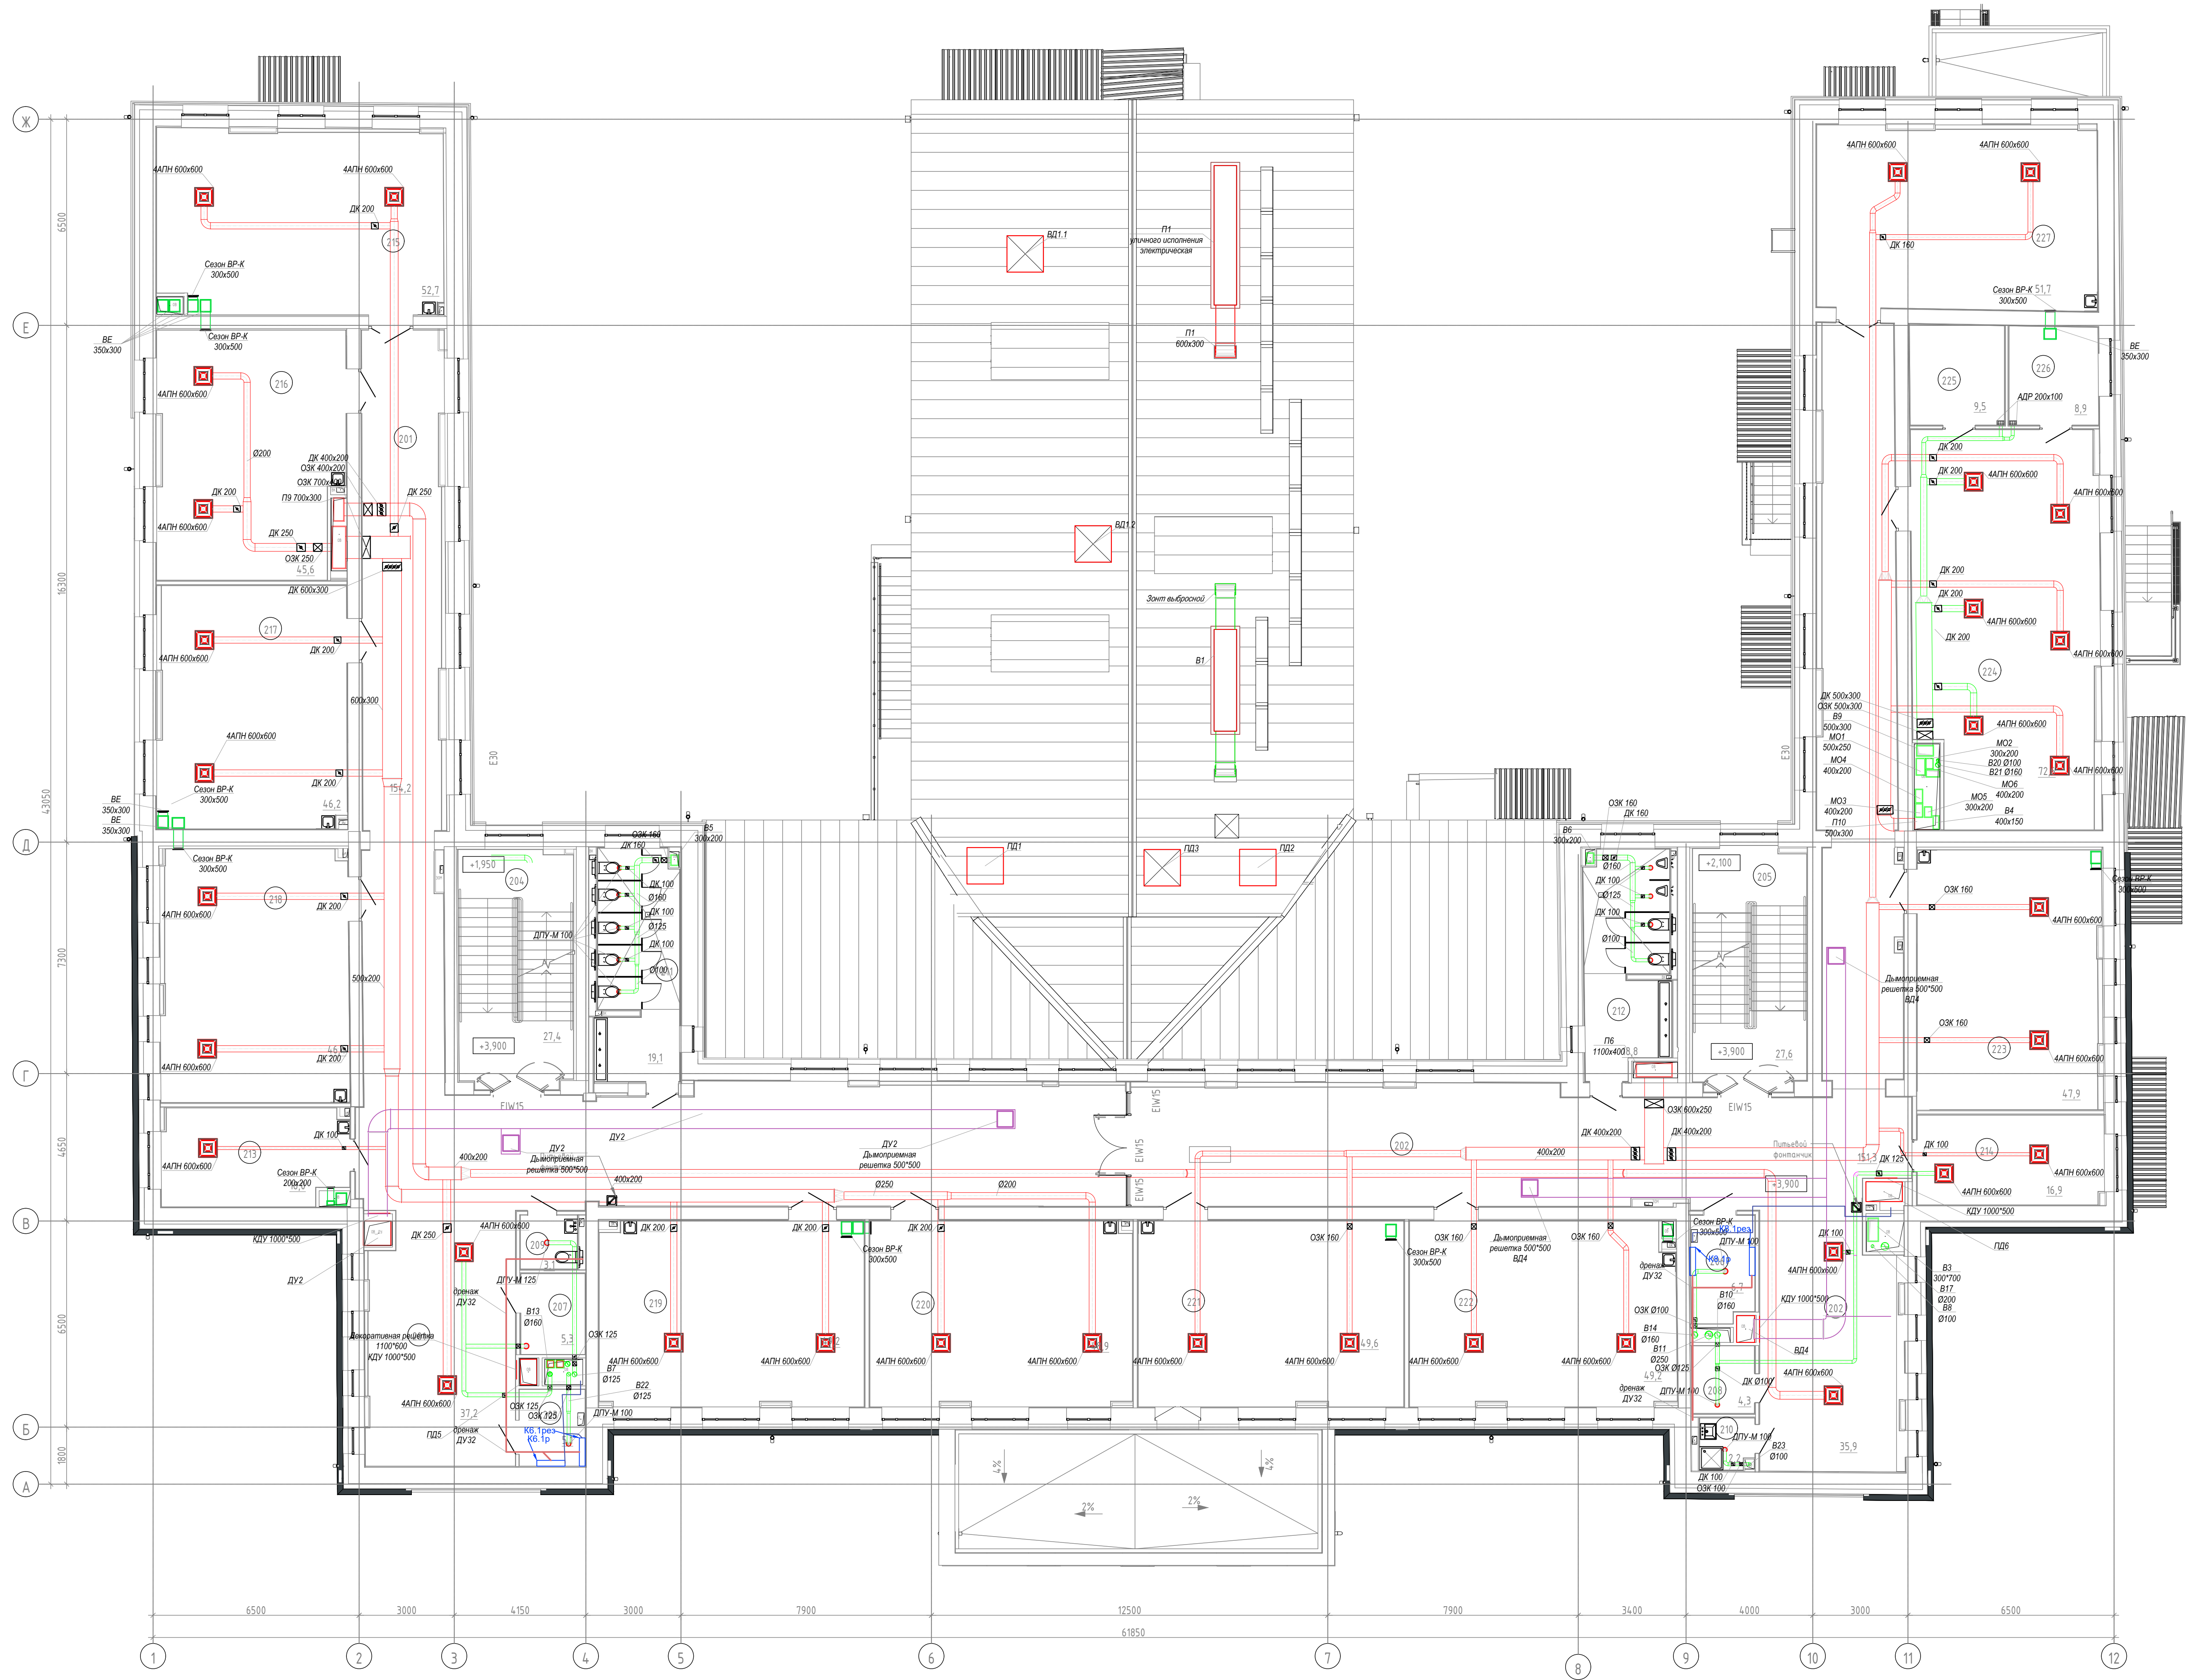


Экспликация помещений 2-го этажа			
Номер помещения	Наименование	Площадь, м²	Кат. помеще-ния
201	Коридор с рекреацией	191,5	
202	Коридор с рекреацией	187,2	
203	Помещение СС	5,1	ВА
204	Лестничная клетка (Тип И0)	27,4	
205	Лестничная клетка (Тип И0)	27,6	
206	Помещение СС	6,7	ВА
207	Подсобное помещение	5,3	ВА
208	Подсобное помещение	4,3	ВА
209	Туалет для персонала	3,1	
210	ПМ	2,2	ВА
211	Уборная для девочек	19,1	
212	Уборная для мальчиков	18,8	
213	Кабинет для индивидуальных занятий, в т.ч. с учителем-логопедом	18,1	
214	Административный кабинет. Тип 1	16,9	
215	Учебный кабинет	52,7	
216	Учебный кабинет	45,6	
217	Учебный кабинет	46,2	
218	Учебный кабинет	46,4	
219	Учебный кабинет	49,3	
220	Учебный кабинет	48,9	
221	Учебный кабинет	49,6	
222	Учебный кабинет	49,3	
223	Учебный кабинет	47,9	
224	Гимнастический зал	72,6	
225	Раздевальная Тип 1	9,5	
226	Раздевальная Тип 1	8,9	
227	Учебный кабинет	51,7	
		1111,7	

- трубопровода ДУ32 дренажная конденсата кондиционера
- трубопровода Газ/жидкость фреоновые в изоляции
- трубопровода теплоснабжения бентустанбокс

636/П-24-АНО/ТЗК					
Выполнение проектно-изыскательских работ на капитальный ремонт общеобразовательного учреждения (ГБОУ Школа №282 "Соколники"), по адресу: г. Москва, ул. Барбарисов, 9, эт. 1					
Изм. Кол. листы в экз.	Подп.	Дата			
Разработ. Замков А.В.	10.24				
Проверил Зеленцов А.В.	10.24				
ГИП Виноградов А.В.	10.24				
			Осуществление технического сопровождения строительства и инженерных систем здания	Этапия	Пусто
			План 2 этажа М1:100. Система вентиляции	10	Пусто
Н. контр. Циванов А.В.	10.24				
			ООО "Аркана"		
			Формат А0		

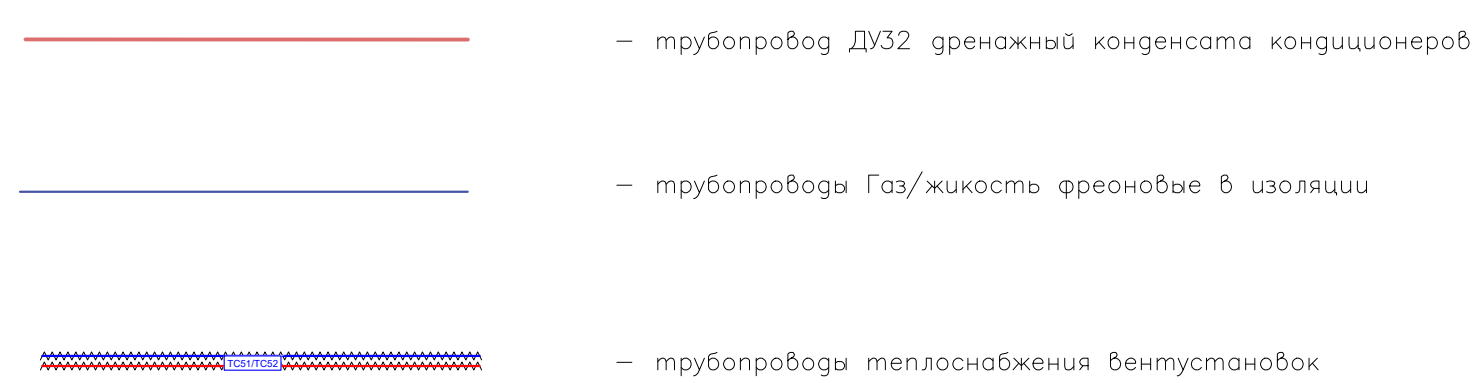

							6/96/П-24-АНО/ТЭК
Выполнение проектно-изыскательских работ на капитальный ремонт общепромышленного оборудования (БОО Школа №1282 "Соколинки"), по адресу: с. Москва, ул. Барыкина, д. 1, стр. 1							
ММ	ММ	ИЗ	ИЗ	ИЗ	ПОС	ПОС	10.24
Рублев	Венский	А					10.24
Проверил	Беленко	А					10.24
ГИП	Емельянов	А					10.24
обследование технического состояния строительных и инженерных систем здания							
План 3 этажа ММ:100, Система вентилиции							
И.контр.	Завинов	А					10.24
Фомат							А0

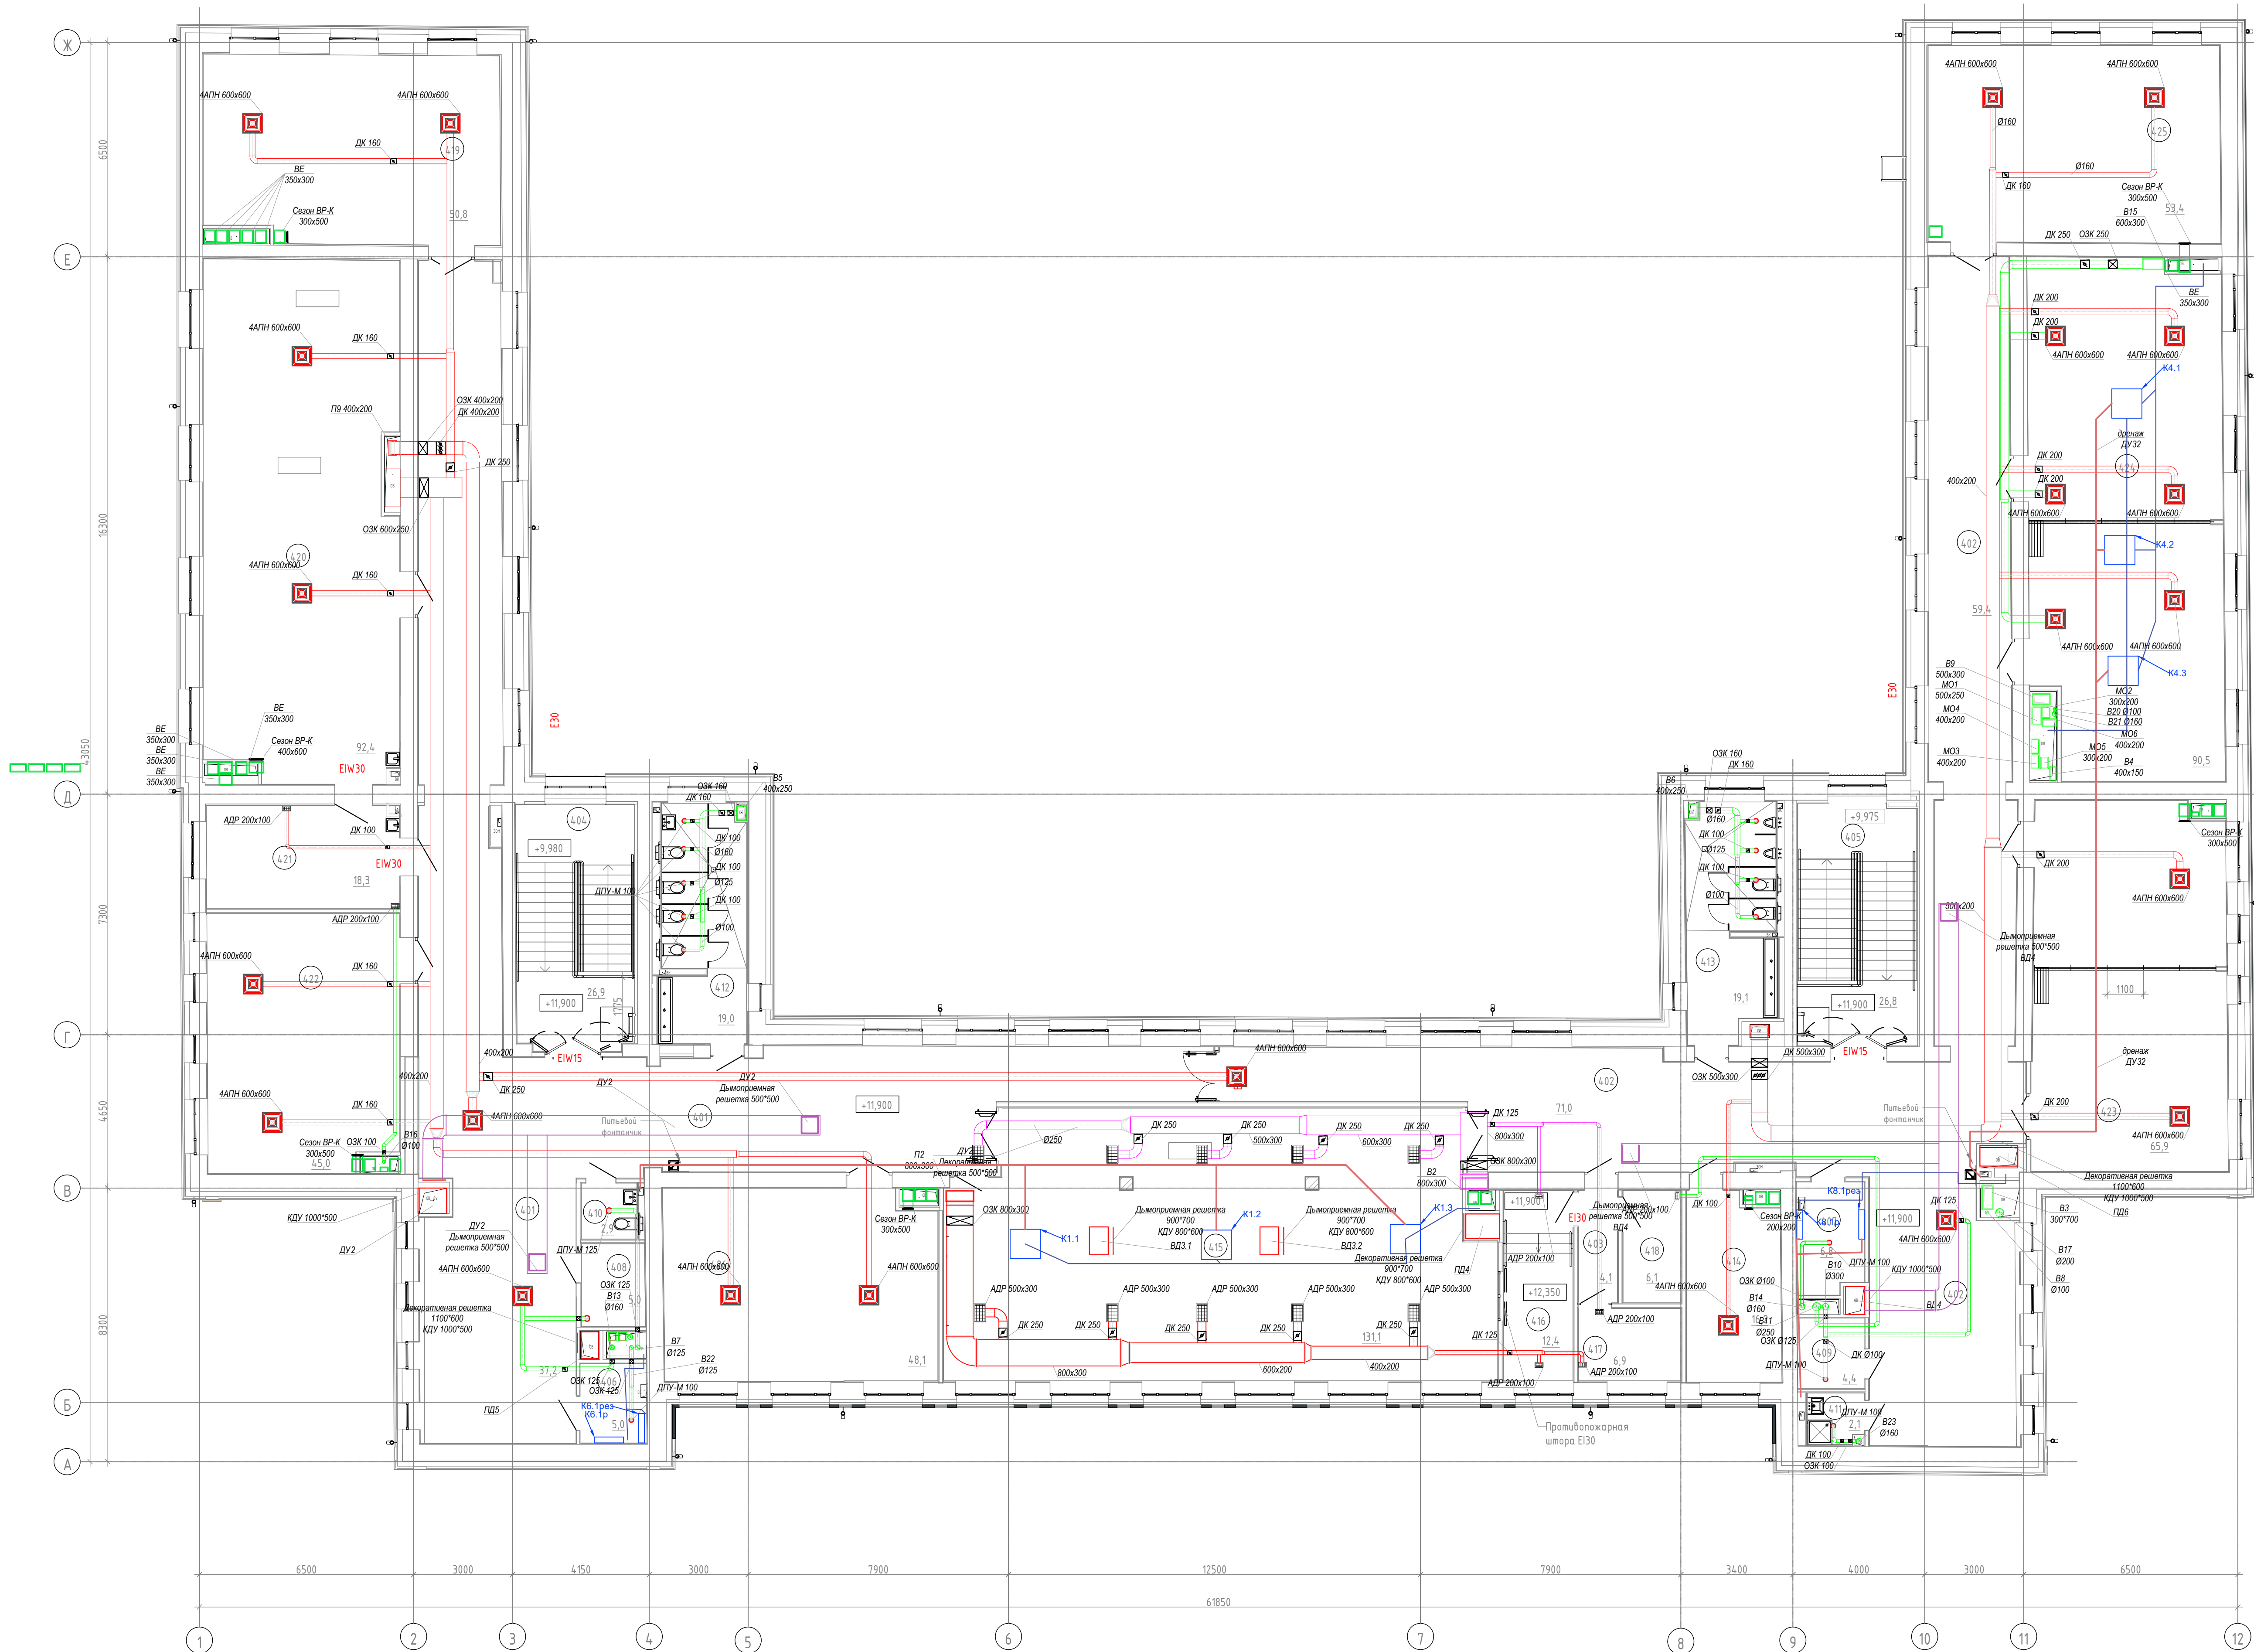


Экспликация помещений 4-го этажа			
Номер помещения	Наименование	Площадь, м²	Кат. помеще-ния
401	Коридор с рекреацией	173,6	
402	Коридор с рекреацией	166,2	
403	Танцев	4,1	
404	Лестничная клетка (Тип Л0)	26,9	
405	Лестничная клетка (Тип Л0)	26,8	
406	Помещение СС	5,0	Б4
407	Помещение СС	6,8	Б4
408	Подсобное помещение	5,0	Б4
409	Подсобное помещение	4,4	Б4
410	Туалет для персонала	2,9	
411	ЛТМ	2,1	Б4
412	Уборная для девочек	19,0	
413	Уборная для мальчиков	19,1	
414	Кабинет для индивидуальных занятий, в т.ч. индивидуаль-но-групповые	16,2	
415	Актовый зал (с эстрадой в уровне пола)	131,1	
416	Технический центр	12,4	Б3
417	Арт-студия	6,9	
418	Кабинет для хранения	6,1	Б4
419	Кабинет информатики	50,8	
420	Учебный кабинет (для изучения естественных биологических/географических)	92,4	
421	Лабораторная биологии	18,3	Б3
422	Учебный кабинет (история)	45,0	
423	Кабинет иностранного языка с возможностью деления/трансформированной перегородкой на два помещения	65,9	
424	Учебный кабинет информатики с возможностью деления/трансформированной перегородкой на два помещения	90,5	
425	Кабинет русского языка и литературы	53,4	
426	Кабинет русского языка и литературы	48,1	
		1938,9	

- трубопровода ДУ32 дренажный конденсата кондиционеров
- трубопровода Газ/жидкость фреоновые в изоляции
- трубопровода теплоснабжения Вентустановок

636/П-24-АНО/ТЭК					
Выполнение проектно-изыскательских работ на капитальный ремонт общеобразовательного учреждения (ГБОУ Школа №282 "Соколники"), по адресу: г. Москва, ул. Барбосова, д. 1, стр. 1					
Исполн.	Климентьев А.В.	Подп.	Дата	Этап	Пусто
Разработ.	Земсков А.В.	Подп.	10.24	12	Пусто
Проверил	Земсков А.В.	Подп.	10.24		
ГИП	Бельянов А.А.	Подп.	10.24		
План 4 этажа М1:100. Система вентиляции				ООО "Аркона"	
Н. контр.	Цыганов А.В.	Подп.	10.24	Формат А0	

Обозначение систем	Кол-во систем	Наименование обслуживаемого помещения (технологического оборудования)	Тип установок агрегата	Тип	Вентилятор			Электропривод			Воздухонагреватель				Фильтр				Воздухоохладитель				Примечание								
					N, кВт	Схема исполн.	Положение	L, м3/ч +10%	Р **, Па	п, об/мин	Кол-во, шт	N, кВт	п, об/мин	Т-ра нагретв, °С	Расход тепла, кВт	Δ Р, Па	Тип	N	Кол.	Δ Р, Па	концентрация мг/м3			Тип	N	Кол.	Т-ра охладж-я, °С		Расход холода, кВт	Δ Р, Па	
																					от	до					начальная	конечная			от
П1	1	Спортивный зал	наруж. Исполнения	-	-	-	-	2 520	350		1.10	0	эл.	-	1	-26 -2	-2 20	2198 18.64		G4 F7	-	-	-	-	-	-	-	-	-	-	Штроспиль со стороны помещения, Д/Ш/В 4250/710520, 258 кг
П2	1	Актовый зал	наруж. Исполнения	-	-	-	-	3 520	300		1.10	0	эл.	-	1	-26 -3	-3 20	2953 27.21		G4 F7	-	-	-	-	-	-	-	-	-	-	Штроспиль со стороны помещения, Д/Ш/В 4510/10570, 300.2 кг
П3	1	Обеденный зал	Напольная	-	-	-	-	3 600	400		150	0	вода 95/70	-	1	-26	20	55,73		G4 F7	-	-	-	-	-	-	-	-	-	-	Штроспиль со стороны помещения, Д/Ш/В 3020/10570, 210.3 кг
П4	1	Пещеблок. (Производ. Пом.)	Напольная	-	-	-	-	8 590	500		4.00	0	вода 95/70	-	1	-26	18	128.07		G4 F7	-	-	-	-	-	-	-	-	-	-	Штроспиль со старыми помещения, Д/Ш/В 4275/1100/1100, 584.4 кг
П5	1	Учебные кабинеты	Напольная	-	-	-	-	8 730	650		5.5	0	вода 95/70	-	1	-26	20	135,15		Укороченны е G4 F7	-	-	-	-	-	-	-	-	-	-	Штроспиль со стороны помещения, Д/Ш/В 4275/1100/1100, 614.4 кг
П6	1	Учебные кабинеты	Напольная					8740	650		4	0	вода 95/70	-	1	-26	20	135,3		Укороченны е G4 F7	-	-	-	-	-	-	-	-	-	-	Штроспиль со стороны помещения, Д/Ш/В 4275/1100/1100, 584.4 кг
П7	1	Мед блок	подвесная					370	400		0.37	0	эл.	-	1	-26	20	6.000		G4 F7 F9	-	-	-	-	-	-	-	-	-	-	Штроспиль со стороны помещени, Д/Ш/В 3000/610/420, 160.8 кг
П9	2	Рекреация	Напольная					5350	400		2.20	0	вода 95/70	-	1	-26	20	72,14		G4 F7	-	-	-	-	-	-	-	-	-	-	Штроспиль со стороны помещени, Д/Ш/В 3020/710/520, 181.2 кг
П10	3	Гимнастический зал	подвесная					1480	350		0.75	0	вода 95/70	-	1	-26	20	22.910		G4 F7	-	-	-	-	-	-	-	-	-	-	Штроспиль со стороны помещени, Д/Ш/В 3022/640/340, 122.9 кг
В1	1	Спортивный зал	наруж. Исполнения					2410	350		1.10	-	-	-	-	-	-	-	-	-	-	-	-	-	-	-	-	-	-	-	2 штроспиль, Д/Ш/В 366/710/520, 162.2 кг
В2	1	Актовый зал	наруж. Исполнения					3520	300		1.10	-	-	-	-	-	-	-	-	-	-	-	-	-	-	-	-	-	-	-	2 штроспиль, Д/Ш/В 366/610/520, 174.1 кг
В3	1	Обеденный зал	наруж. Исполнения					2360	400		1.10	0	-	-	-	-	-	-	-	-	-	-	-	-	-	-	-	-	-	-	2 штроспиль, Д/Ш/В 366/710/520, 162.2 кг
В4	1	Пещеблок. (Производ. Пом.)	наруж. Исполнения	-	-	-	-	1130	380		0.37	0	-	-	-	-	-	-	-	-	-	-	-	-	-	-	-	-	-	-	2 штроспиль, Д/Ш/В 266/610/420, 131.1 кг
В5	1	Санузлы	наруж. Исполнения	-	-	-	-	1550	380		0.55	0	-	-	-	-	-	-	-	-	-	-	-	-	-	-	-	-	-	-	2 штроспиль, Д/Ш/В 266/710/470, 145.5 кг
В6	1	Санузлы	наруж. Исполнения	-	-	-	-	1280	380		0.37	0	-	-	-	-	-	-	-	-	-	-	-	-	-	-	-	-	-	-	2 штроспиль, Д/Ш/В 266/610/420, 131.1 кг
В7	1	Санузлы	наруж. Исполнения	-	-	-	-	280	300		0.37	0	-	-	-	-	-	-	-	-	-	-	-	-	-	-	-	-	-	-	2 штроспиль, Д/Ш/В 266/610/420, 131.1 кг
В8	1	Туалет медблока	наруж. Исполнения	-	-	-	-	90	250		0.07	0	-	-	-	-	-	-	-	-	-	-	-	-	-	-	-	-	-	-	2 штроспиль, Д/Ш/В 266/610/420, 131.1 кг
В9	1	Гимнастический зал	наруж. Исполнения	-	-	-	-	1480	350		0.37	0	-	-	-	-	-	-	-	-	-	-	-	-	-	-	-	-	-	-	2 штроспиль, Д/Ш/В 266/710/470, 145.5 кг
В10	1	административные каб., рекреация	наруж. Исполнения	-	-	-	-	220	350		0.37	0	-	-	-	-	-	-	-	-	-	-	-	-	-	-	-	-	-	-	2 штроспиль, Д/Ш/В 266/610/420, 131.1 кг
В11	1	Гардеробные	наруж. Исполнения	-	-	-	-	760	380		0.37	0	-	-	-	-	-	-	-	-	-	-	-	-	-	-	-	-	-	-	2 штроспиль, Д/Ш/В 266/610/420, 131.1 кг
В12раз/В12 рез	2	Электрощитовая	канальный	-	-	-	-	70	200		0.06	0	-	-	-	-	-	-	-	-	-	-	-	-	-	-	-	-	-	-	2 штроспиль, Д/Ш/В 1875/102/251, 59.8 кг
В13	1	Комната охраны, рекреация	наруж. Исполнения	-	-	-	-	730	350		0.37	0	-	-	-	-	-	-	-	-	-	-	-	-	-	-	-	-	-	-	2 штроспиль, Д/Ш/В 266/610/420, 131.1 кг
В14	1	Помещение СС	наруж. Исполнения	-	-	-	-	170	300		0.37	0	-	-	-	-	-	-	-	-	-	-	-	-	-	-	-	-	-	-	2 штроспиль, Д/Ш/В 266/610/420, 131.1 кг
В15	1	Многофункциональный информационный видеоблечный центр. Учебный кабинет информатики	наруж. Исполнения	-	-	-	-	2040	350		0.55	0	-	-	-	-	-	-	-	-	-	-	-	-	-	-	-	-	-	-	2 штроспиль, Д/Ш/В 266/710/470, 145.5 кг
В16	1	Лаборанская	наруж. Исполнения	-	-	-	-	70	250		0.06	0	-	-	-	-	-	-	-	-	-	-	-	-	-	-	-	-	-	-	2 штроспиль, Д/Ш/В 266/610/420, 131.1 кг
В17	1	Медблок	наруж. Исполнения	-	-	-	-	470	300		0.37	0	-	-	-	-	-	-	-	-	-	-	-	-	-	-	-	-	-	-	2 штроспиль, Д/Ш/В 266/610/420, 131.1 кг
В19	1	Тех помещения подвала	наруж. Исполнения	-	-	-	-	60	350		0.37	0	-	-	-	-	-	-	-	-	-	-	-	-	-	-	-	-	-	-	2 штроспиль, Д/Ш/В 266/610/420, 131.1 кг
В20	1	Помещение для временного хранения пищевых отходов	наруж. Исполнения	-	-	-	-	100	250		0.06	0	-	-	-	-	-	-	-	-	-	-	-	-	-	-	-	-	-	-	2 штроспиль, Д/Ш/В 266/610/420, 131.1 кг
В21	1	Санузлы пещеблока	наруж. Исполнения	-	-	-	-	220	300		0.37	0	-	-	-	-	-	-	-	-	-	-	-	-	-	-	-	-	-	-	2 штроспиль, Д/Ш/В 266/610/420, 131.1 кг
В22	1	Помещение СС	наруж. Исполнения					250	300		0.37																				Д/Ш/В 766/610/420, 57.1 кг
В23		Туалет	наруж. Исполнения					150	250		0.06																				Д/Ш/В 766/610/420, 57.1 кг
М01	1	Пещеблок. (Производ. Пом.)	наруж. Исполнения	-	-	-	-	2200	600		1.10	0	-	-	-	-	-	-	-	-	-	-	-	-	-	-	-	-	-	-	2 штроспиль, Д/Ш/В 366/710/520, 162.2 кг
М02	1	Пещеблок. (Производ. Пом.)	наруж. Исполнения	-	-	-	-	990	500		0.37	0	-	-	-	-	-	-	-	-	-	-	-	-	-	-	-	-	-	-	2 штроспиль, Д/Ш/В 266/610/420, 131.1 кг
М03	1	Пещеблок. (Производ. Пом.)	наруж. Исполнения	-	-	-	-	1430	500		0.55	0	-	-	-	-	-	-	-	-	-	-	-	-	-	-	-	-	-	-	2 штроспиль, Д/Ш/В 266/710/470, 145.5 кг
М04	1	Пещеблок. (Производ. Пом.)	наруж. Исполнения					1540	500		0.55	0	-	-	-	-	-	-	-	-	-	-	-	-							

План подвала
Системы водоснабжения

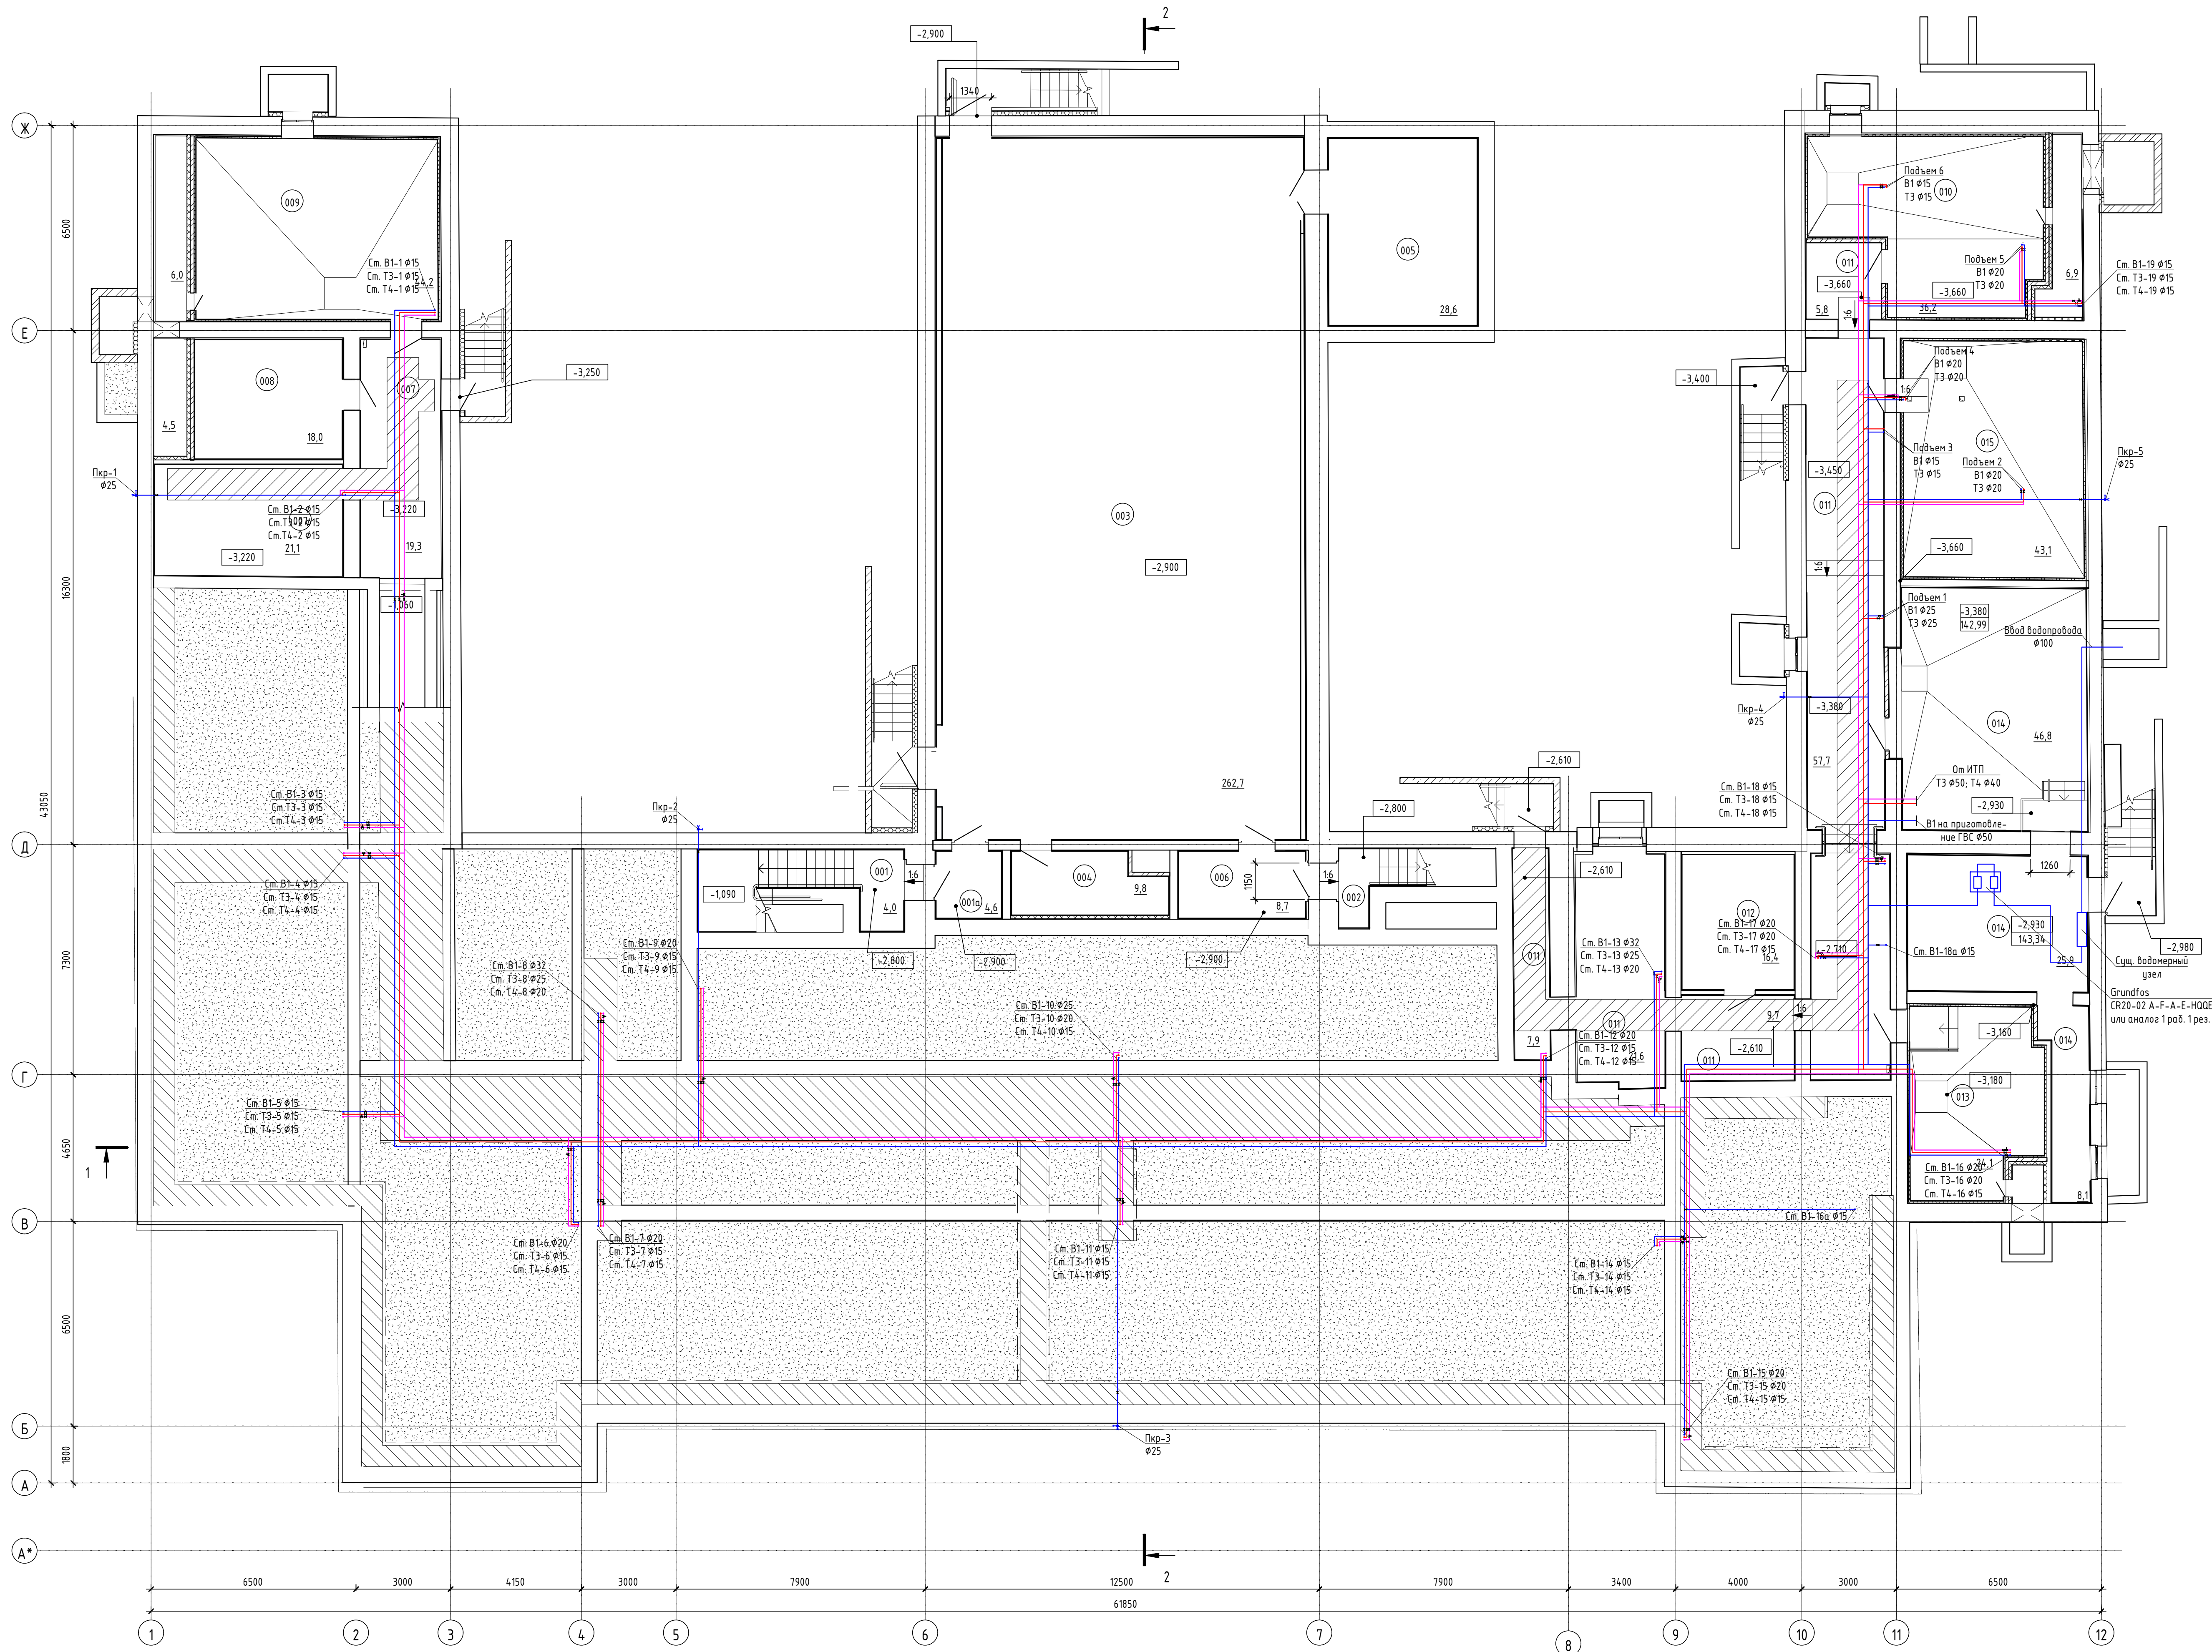


Экспликация помещений			
Номер помеще-ния	Наименование	Площадь, м²	Кол-во помеще-ния
Помещения общего пользования			
001	Лестница	8.6	
002	Лестница	7.8	
007	Коридор	21.1	
008	Коридор	19.3	
014	Коридор	63.5	
015	Коридор	9.7	
016	Коридор	21.6	
017	Коридор	7.9	
		159.5	
Специальные помещения			
005	Тум	3.6	В4
		3.6	
Спортивно-оздоровительная группа помещений			
003	Спортивный зал	262.7	
004	Складная	10.9	В3
006	Складная	28.6	В3
		302.2	
Технические помещения			
009	Кладовая	18.0	В4
010	Венткамера	44.2	Д
011	Формкамера	10.5	
012	Формкамера	6.9	
013	Венткамера	36.1	В4
018	Насосная	15.9	Д
019	Венткамера	24.1	В4
020	Формкамера	1.6	
021	ИТП	80.8	Д
022	Венткамера	43.1	Д
		281.2	
		746.5	

Условные обозначения

- трубопровод В1
- трубопровод Т3, Т4
- трубопроводы проложенные скрыто. Показания условно
- стояк В1
- стояк Т3, Т4

636/П-24-АНО/ТЗК			
Выполнение проектно-изыскательских работ на капитальный ремонт общеобразовательного учреждения (ГБОУ школа №282 "Сколково"), по адресу: г. Москва, ул. Барбариса, д. 1, стр. 1			
Изм. Кол. листы	Исполн.	Дата	
Разработ.	Венгелов А.А.	10.24	
Проектировщик	Венгелов А.А.	10.24	
ГИП	Венгелов Д.А.	10.24	
Н. контр.	Венгелов А.А.	10.24	
План подвала. М:100. Система водоснабжения			000 "Аркона"
Формат			A0

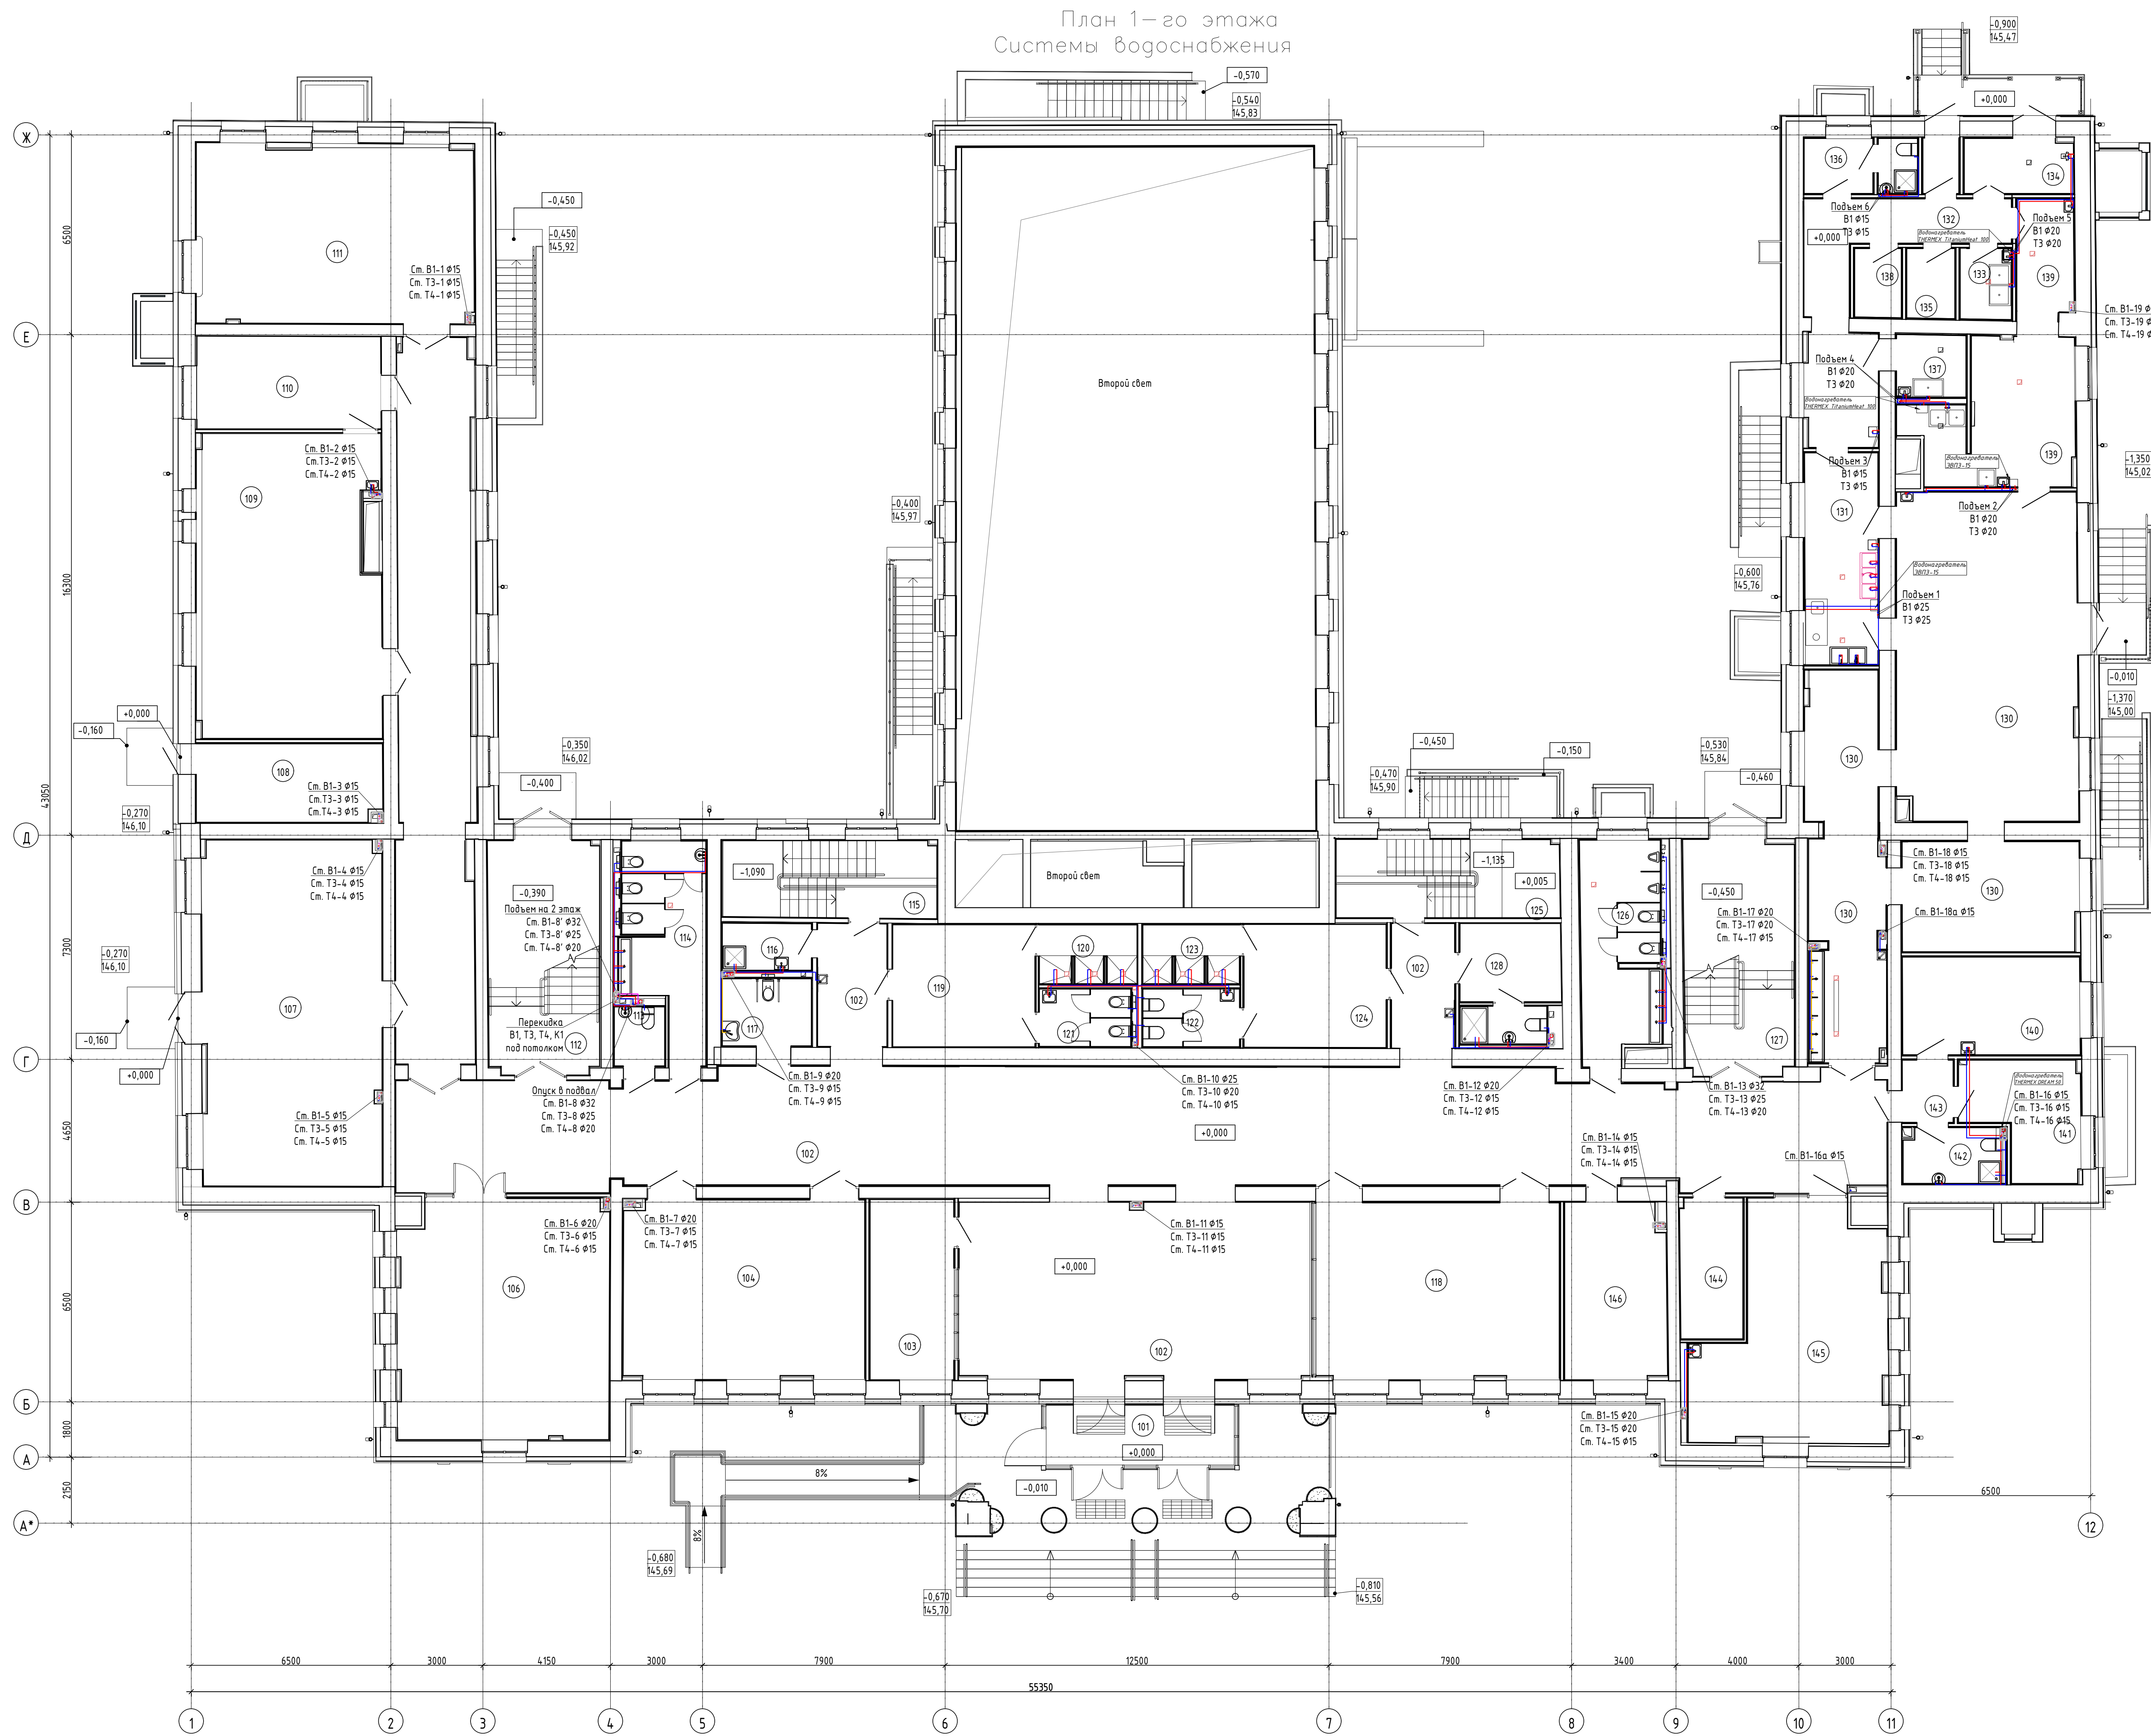


Условные обозначения

- трубопровод В1 — стояк В1
— трубопровод Т3, Т4 — стояк Т3, Т4
----- трубопровода проложения скрыта. Показаны условно

Экспликация помещений 1-го этажа			
Номер помеще-ния	Наименование	Площадь, м²	Кат. поме-щени-я
Помещения общего пользования			
101	Танбур	12,5	
102	Вестибюль (с зоной ожидания для посетителей)	69,3	
105	Коридор	60,3	
112	Лестничная клетка	27,8	
115	Лестничная клетка	17,8	
118	Коридор	199,2	
125	Лестничная клетка	18,9	
127	Лестничная клетка	27,8	
		423,5	
Сантехнические помещения			
113	Туалет для персонала	3,3	
114	Уборная для девочек	17,0	
116	ПМ	4,6	В4
117	Универсальная уборная для МГН	6,6	
126	Уборная для мальчиков	18,4	
		49,9	
Специализированные помещения			
107	Кабинет материальной технологии Тип 1	66,1	В3
109	Кабинет материальной технологии Тип 2	58,7	В3
110	Кабинет материальной технологии	18,0	В3
		142,9	
Спортивно-оздоровительная группа помещений			
119	Раздевальня Тип 1	18,7	
120	Душевая	6,3	
121	Уборная	5,7	
122	Уборная	6,1	
123	Душевая	6,2	
124	Раздевальня Тип 1	18,8	
128	Тренировочная с санузлом	12,1	
		73,9	
Технические помещения			
108	Электрощитовая	15,5	В4
144	Помещение СС	9,5	В4
		25,0	
		1257,8	

Экспликация помещений 1-го этажа			
Номер помеще-ния	Наименование	Площадь, м²	Кат. поме-щени-я
Административные помещения			
103	Кабинет охраны (с диспетчерским пунктом)	16,2	
145	Кабинет с рабочим пространством для инженерно-технической и охранных работ Тип 1	41,8	
		58,0	
Гардеробная			
104	Гардероб для обучающихся (основная школа)	46,2	
106	Гардероб для обучающихся (начальная школа)	53,7	
146	Гардероб для учителей	19,1	
147	Гардероб для обучающихся (начальная школа)	46,4	
		165,4	
Медицинский блок			
140	Кабинет врача	18,7	
141	Процедурный (прибыльнич) кабинет	12,9	
142	Туалет медблока с местом для приготовления дезинфицирующих растворов и хранения уборочного инвентаря, предназначенных для помещений школьного назначения	6,1	В4
143	Коридор медблока	3,4	
		41,1	
Основная школа. Учебные кабинеты			
111	Учебный кабинет (математика)	53,3	
		53,3	
Посудоблок			
129	Умывальная	10,2	
130	Обеденный зал	104,7	
131	Моечная для столовой посуды	16,9	
132	Коридор	22,7	
133	Кладовая и моечная оборотной тары	4,0	
134	Застольный цех	6,6	
135	Кладовая сухих продуктов	3,7	
136	Помещение персонала с санузлом	6,5	
137	Помещение для временного хранения посуды отхода	4,8	
138	ПМ	3,5	В4
139	Помещение подготовки блюд к реализации с участком хранения посуды	29,3	В4
148	Танбур	22,2	
		214,9	

Системы водоснабжения

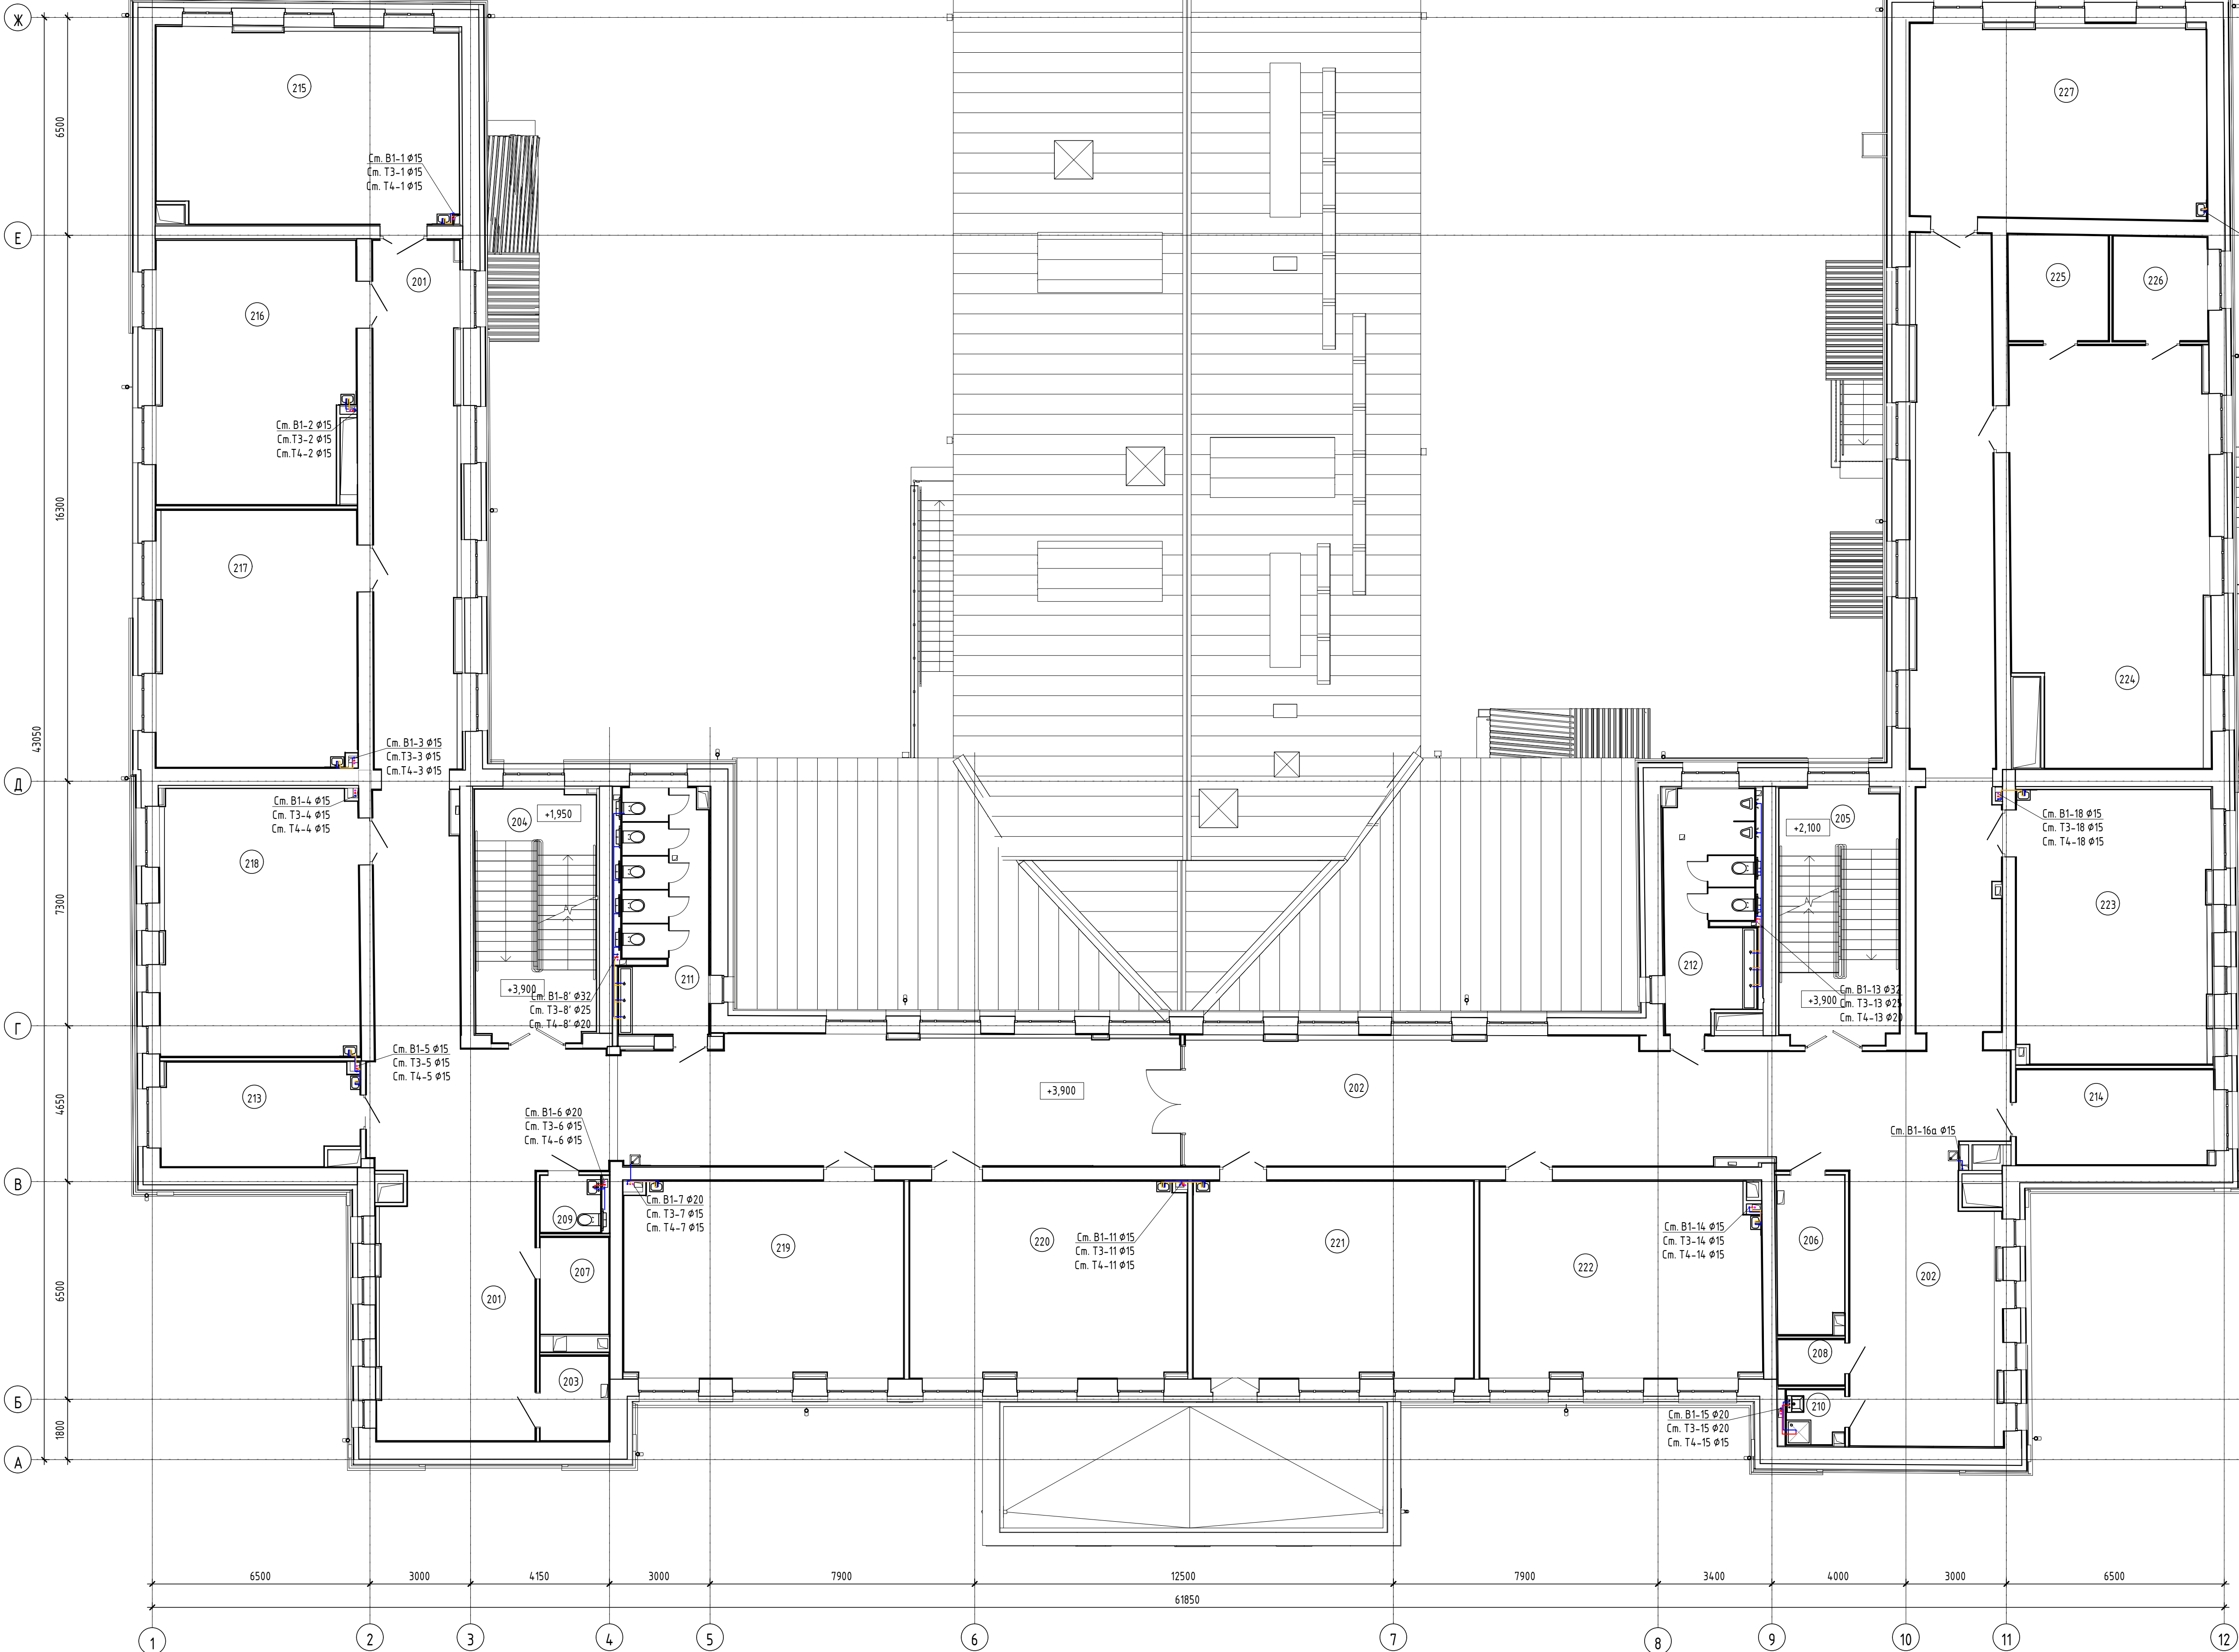


Экспликация помещений 2-го этажа			
Номер помеще- ний	Наименование	Площадь, м²	Класс помеще- ния
Административные помещения			
214	Кабинет для индивидуальных занятий, в т.ч. слушатель-логопедом	18,2	
215	Административный кабинет (начальная школа) Тип 0	16,9	
		35,1	
Начальная школа. Учебные кабинеты			
216	Учебный кабинет (1 класс)	52,8	
217	Учебный кабинет (1 класс)	45,8	
218	Учебный кабинет (1 класс)	46,2	
219	Учебный кабинет (1 класс)	44,7	
220	Учебный кабинет (2-4 классы)	49,2	
221	Учебный кабинет (2-4 классы)	49,6	
222	Учебный кабинет (2-4 классы)	48,9	
223	Учебный кабинет (2-4 классы)	49,3	
224	Учебный кабинет (2-4 классы)	47,9	
225	Учебный кабинет (2-4 классы)	49,9	
226	Учебный кабинет (2-4 классы)	51,7	
		489,1	
Помещения общего пользования			
201	Коридор	14,4	
202	Рекреация	37,5	
203	Рекреация	36,2	
204	Лестничная клетка (Тип П0)	27,4	
205	Лестничная клетка (Тип П0)	27,6	
209	Коридор	162,2	
		435,2	
Сантехнические помещения			
210	Туалет для персонала	3,2	
211	Рем.	2,8	
212	Уборная для девочек (начальная школа)	19,4	
213	Уборная для мальчиков (начальная школа)	18,8	
		44,2	
Спортивно-оздоровительная группа помещений			
225	Гимнастический зал	72,8	
226	Раздевальня зал	9,5	
227	Раздевальня Тип 1	8,9	
		91,3	
Технические помещения			
206	Помещение СС	5,3	Б4
207	Помещение СС	9,6	Б4
208	Подсобное помещение	6,1	
209	Подсобное помещение	2,8	Б4
		23,7	
		1119,5	

Условные обозначения

- – трубопровод В1 – стояк В1
 – трубопровод Т3, Т4  – стояк Т3
 – трубопроводы проложенные скрыто. Показ

[illegible]

План 3-го этажа
Системы водоснабжения

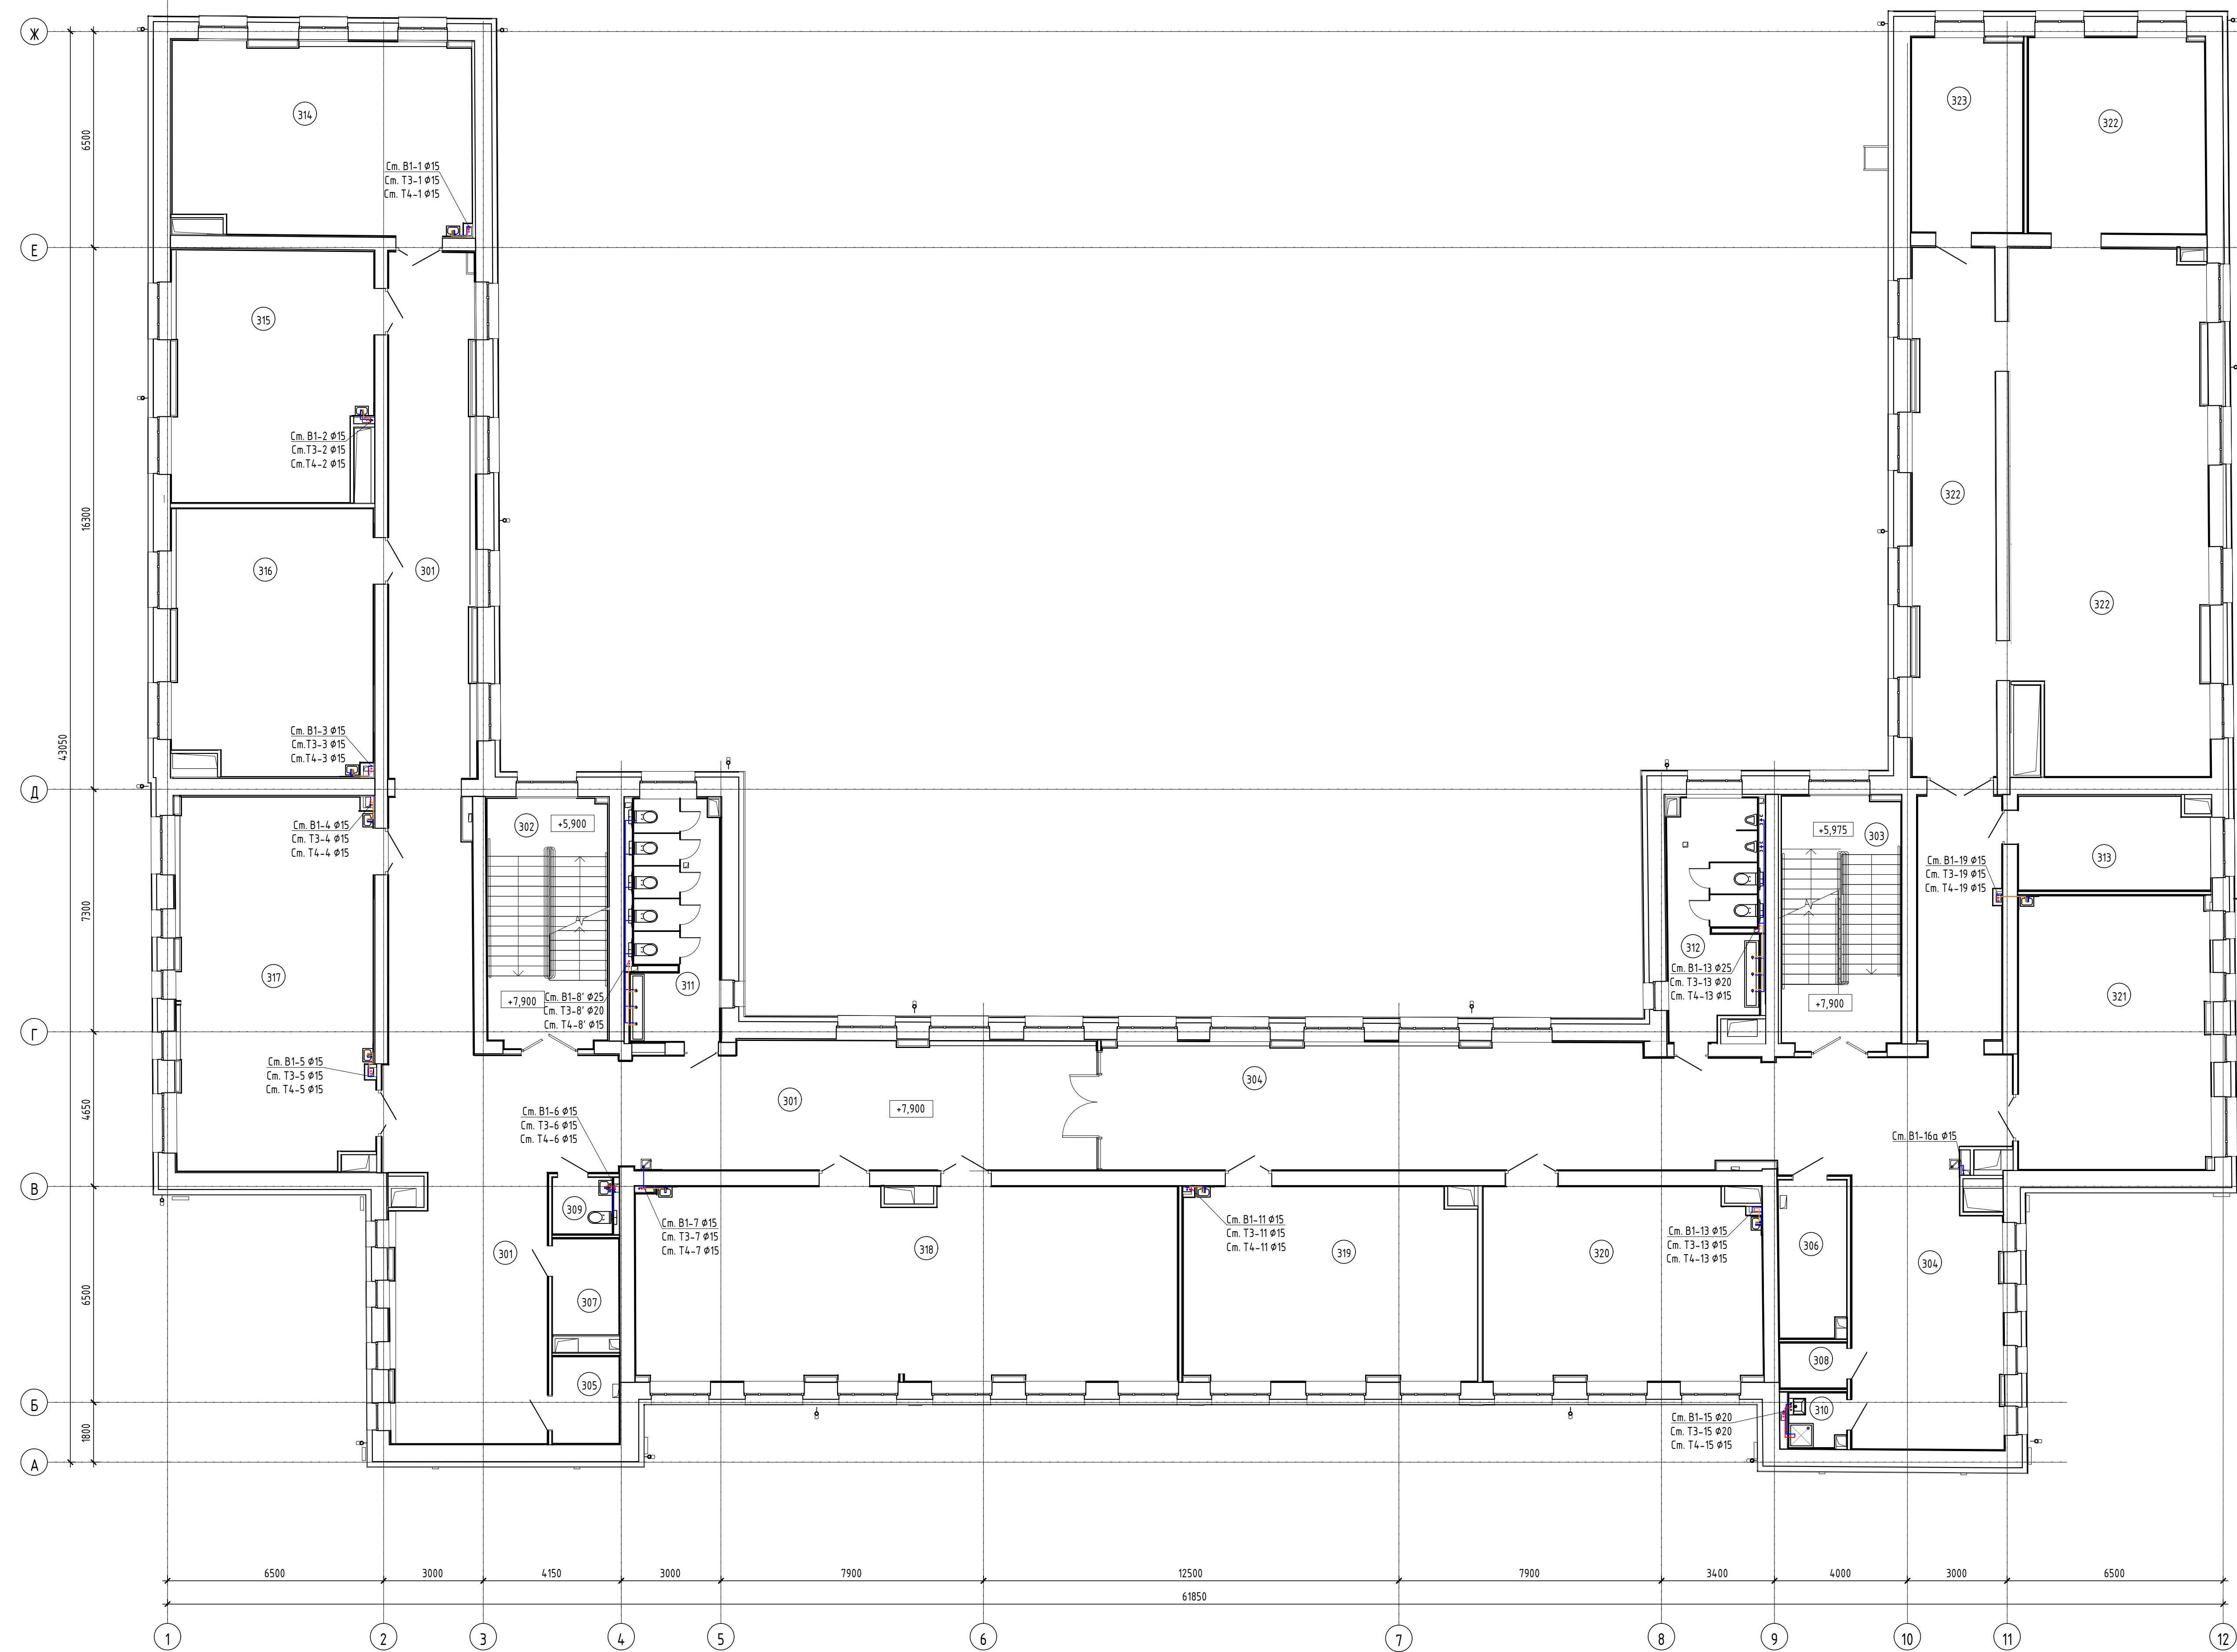


Условные обозначения

- трубопровод В1
- трубопровод Т3, Т4
- трубопроводы проложенные скрыто. Показания условно
- стояк В1
- стояк Т3, Т4

Экспликация помещений 3-го этажа			
Номер помеще-ния	Наименование	Площадь, м²	Кол-во помеще-ния
Административные помещения			
314	Кабинет для индивидуальных занятий, 8 кв.м. с коридором и туалетом	16,0	
		16,0	
Библиотечно-методика			
323	Информационный информационный библиотечный центр с зонами для индивидуальных и групповых занятий, методички, 163,7	163,7	
324	Информационный информационный библиотечный центр. Хранилище (скрытый фонд) и выдачи книг	19,8	83
		183,6	
Начальная школа. Учебные кабинеты			
315	Учебный кабинет (2-4 классы)	52,0	
316	Учебный кабинет (2-4 классы)	45,0	
317	Учебный кабинет (2-4 классы)	48,1	
318	Кабинет иностранного языка с возможностью деления трансформированной перегородкой на два помещения (начальная школа)	66,8	
320	Учебный кабинет (2-4 классы)	51,4	
321	Учебный кабинет (2-4 классы)	48,9	
322	Учебный кабинет (2-4 классы)	47,9	
		360,0	
Помещения общего пользования			
301	Коридор	14,4	
302	Лестничная клетка (Тип Л1)	27,3	
303	Лестничная клетка (Тип Л1)	27,7	
304	Рекреация	37,8	
305	Рекреация	36,2	
306	Коридор	100,2	
		391,6	
Специальные помещения			
310	Туалет для персонала	3,2	
311	ПМ	2,8	
312	Зубная для девочек (начальная школа)	19,0	
313	Зубная для мальчиков (начальная школа)	18,9	
		43,9	
Технические помещения			
308	Помещение СС	5,4	84
307	Помещение СС	9,7	84
309	Подсобное помещение	5,9	
309	Подсобное помещение	2,8	84
		23,8	
Универсальная студия			
319	Творческая мастерская с возможностью деления трансформированной перегородкой на два помещения	94,8	
		94,8	
		113,6	

				636/П-24-АНО/ТЗК			
				Выполнение проектно-изыскательских работ на капитальный ремонт общеобразовательного учреждения (ГБОУ школа №282 "Солнечный"), по адресу: г. Москва, ул. Барбарисов, д. 1, стр. 1			
Изм. Вкл. к проекту	М.П. Исполн.	Дата	М.П. Исполн.	М.П. Исполн.	Дата	М.П. Исполн.	Дата
Разработ.	В.И.И.И.И.	10.24	В.И.И.И.И.	В.И.И.И.И.	10.24	В.И.И.И.И.	10.24
Проектиров.	В.И.И.И.И.	10.24	В.И.И.И.И.	В.И.И.И.И.	10.24	В.И.И.И.И.	10.24
Г.И.П.	В.И.И.И.И.	10.24	В.И.И.И.И.	В.И.И.И.И.	10.24	В.И.И.И.И.	10.24
Н. контр.	В.И.И.И.И.	10.24	В.И.И.И.И.	В.И.И.И.И.	10.24	В.И.И.И.И.	10.24
				План 3 этажа, М:100, Система водоснабжения			
				ООО "Аркан"			
				Формат А0			

План 4-го этажа
Системы водоснабжения

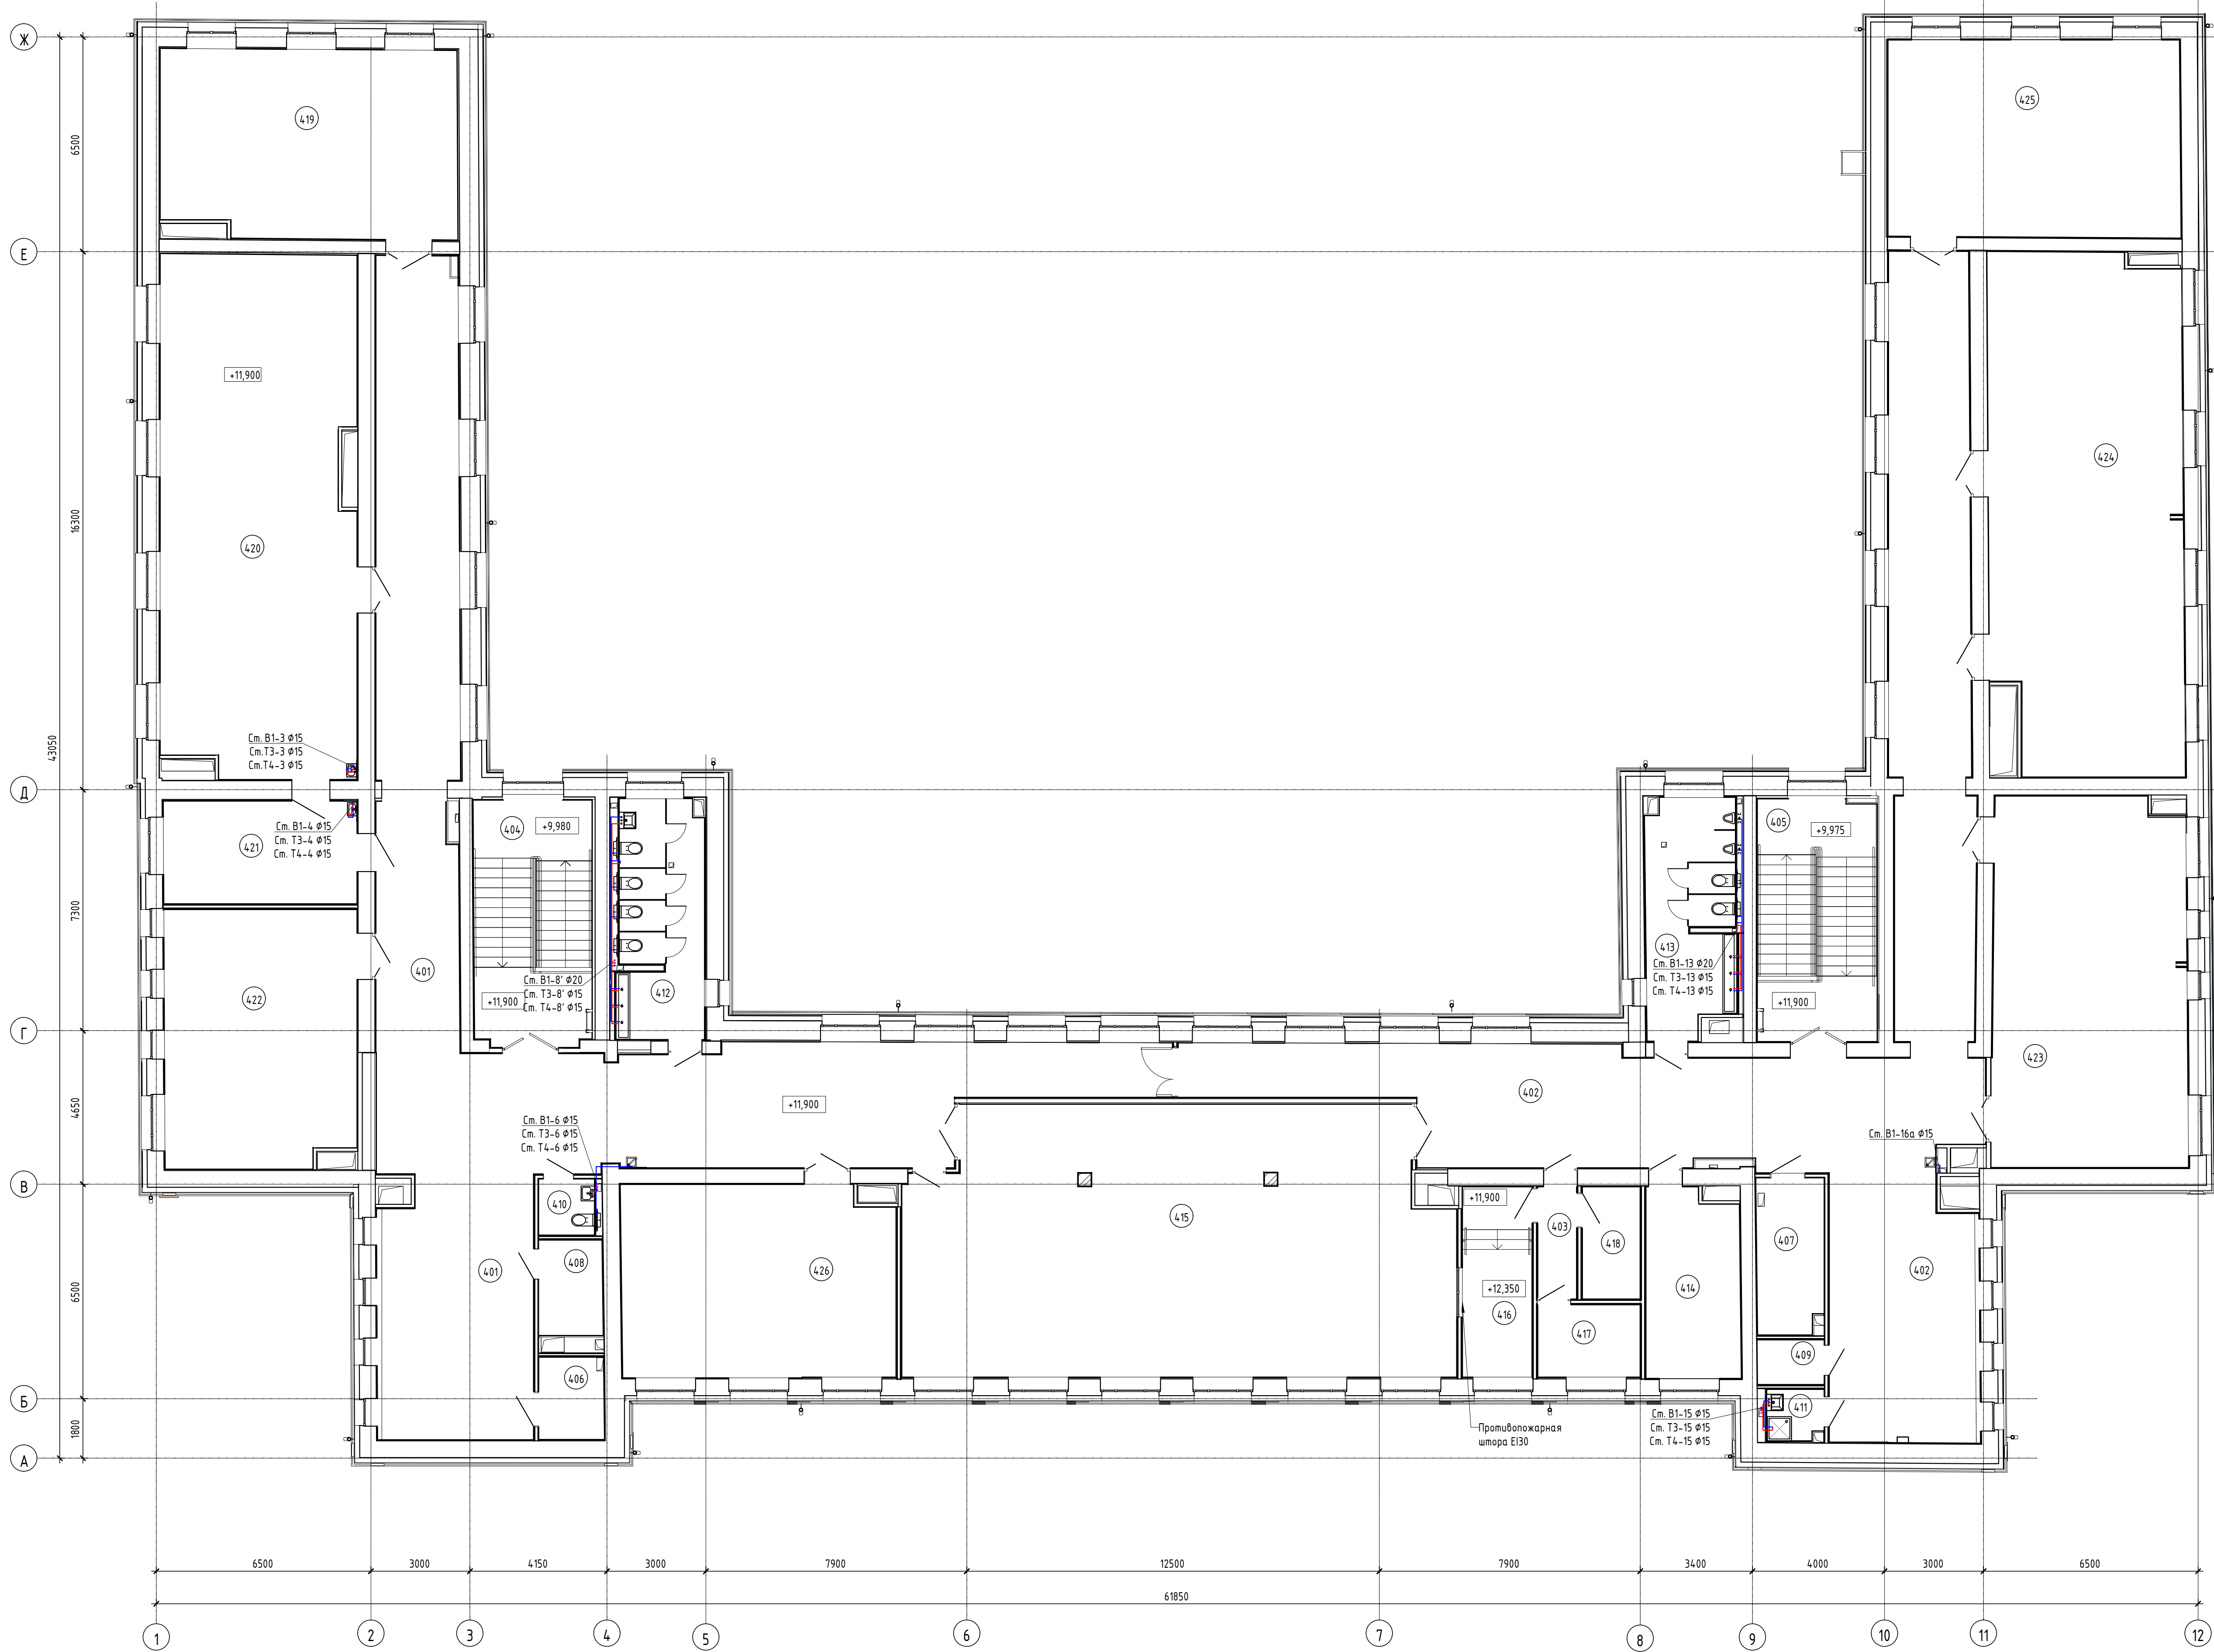


Экспликация помещений 4-го этажа			
Номер помещения	Назначение	Площадь, м²	Кат. помеще-ния
Административные помещения			
416	Кабинет для индивидуальных занятий, 6 п.ч. (стабилизатор-циклограмм)	16,2	
		16,2	
Зрительный зал			
417	Многофункциональное пространство, с функцией зрительного зала (с эстрадой в крайнем поле)	131,3	
418	Технический центр	12,4	B3
419	Артистическая	6,9	
420	Кладовая инвентаря	6,1	
		156,6	
Основная школа. Учебные кабинеты			
421	Кабинет математики	51,0	
422	Учебный кабинет (для изучения естественных наук/биологии/географии Тип 2)	93,0	
423	Лаборантская биологии	18,5	B3
424	Учебный кабинет (история)	45,5	
425	Кабинет иностранного языка с возможностью деления/трансформированной перегородкой на два помещения	66,0	
426	Учебный кабинет информатики с возможностью деления/трансформированной перегородкой на два помещения	90,8	
427	Кабинет русского языка и литературы	53,4	
428	Кабинет русского языка и литературы	48,2	
		466,3	
Помещения общего пользования			
401	Коридор	137,0	
402	Коридор	131,8	
403	Рекреация	35,9	
404	Рекреация	37,2	
405	Коридор	4,1	
406	Астматическая клетка (Тип II)	26,9	
407	Астматическая клетка (Тип II)	26,8	
		399,7	
Санитарно-технические помещения			
412	Туалет для персонала	2,9	
413	ПМ	2,7	
414	Зубная для девочек (основная школа)	19,2	
415	Зубная для мальчиков (основная школа)	19,2	
		44,1	
Технические помещения			
408	Помещение СС	5,1	B4
409	Помещение СС	9,7	B4
410	Подсобное помещение	5,7	
411	Подсобное помещение	2,8	B4
		23,3	
		1106,1	

Условные обозначения

- трубопровод В1 — стояк В1
— трубопровод Т3, Т4 — стояк Т3, Т4
----- — трубопроводы проложенные скрыто. Показаны условно

636/П-24—АНО/ТЗК			
Выполнение проектно-изыскательских работ на капитальный ремонт общеобразовательного учреждения (ГБОУ Школа №282 "Сокольники"), по адресу: г. Москва, ул. Барбариса, д. 1, стр. 1			
Изм. Вкл. к проекту	Исполн.	Дата	
Разработ.	Внедрен А.А.	10.24	
Проверен	Внедрен А.А.	10.24	
ГИП	Внедрен Д.А.	10.24	
Н. контр.	Внедрен А.А.	10.24	
План 4 этажа, М:100, Система водоснабжения		000 "Аркан"	19
Формат		A0	

План чердака
Системы водоснабжения

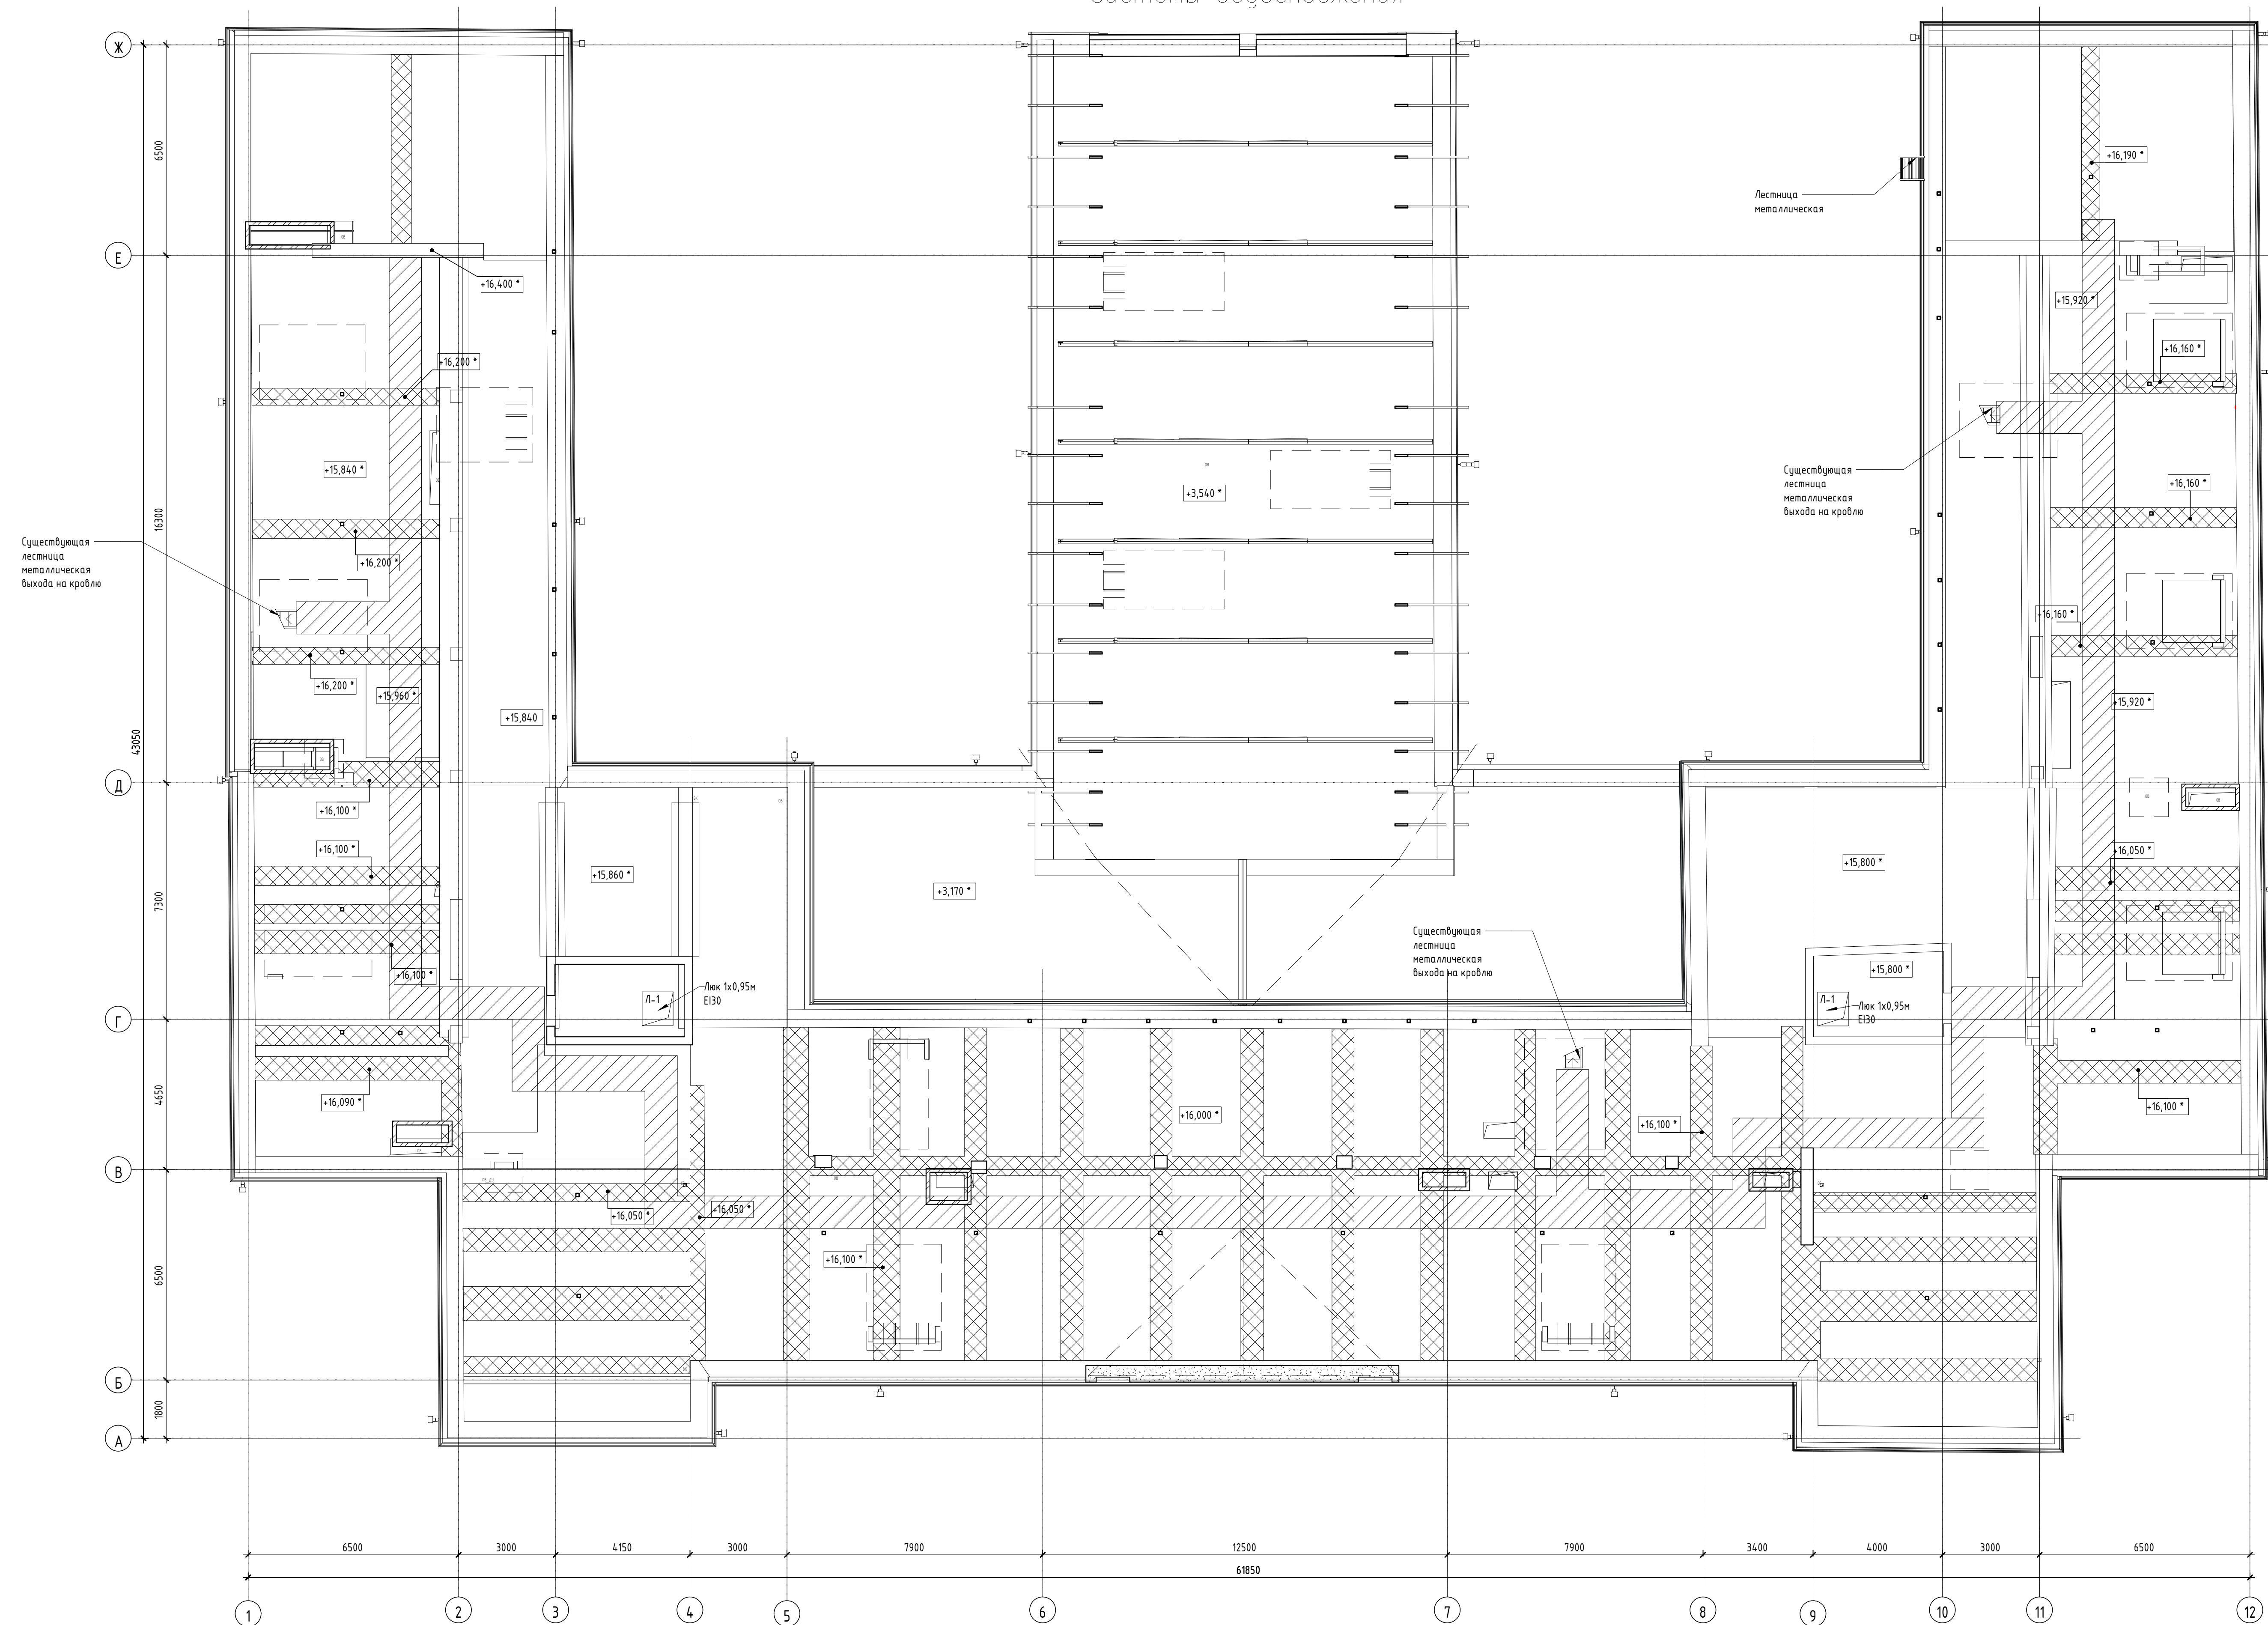


Условные обозначения

-  — трубопровод В1  — стояк В1
 — трубопровод Т3, Т4  — стояк Т3, Т4
 — трубопроводы проложенные скрыто. Показаны условно

						696/П-24- АНО/ТЭК	
						Выполнение проектно-изыскательских работ на капитальный ремонт общеобразовательного учреждения (ГБОУ Школа №1282 "Соколиный"), по адресу: г. Москва, ул. Барбарина, д.1, стр.1	
Изм.	Кол. уч.	Лист	№ док.	Подп.	Дата		
Разраб.			Вихаркин А.В.		10.24	Обследование технического состояния строительных конструкций и инженерных систем здания	
Проверил			Веленцов А.А.		10.24		Стация
ГИП			Емельянов Д.А.		10.24		Лист
						20	
Н. контр.			Циванов А.А.		10.24	План чертэка. М1:100. Система водоснабжения	
						ООО "Аркана"	

План подвала
Система водоотведения

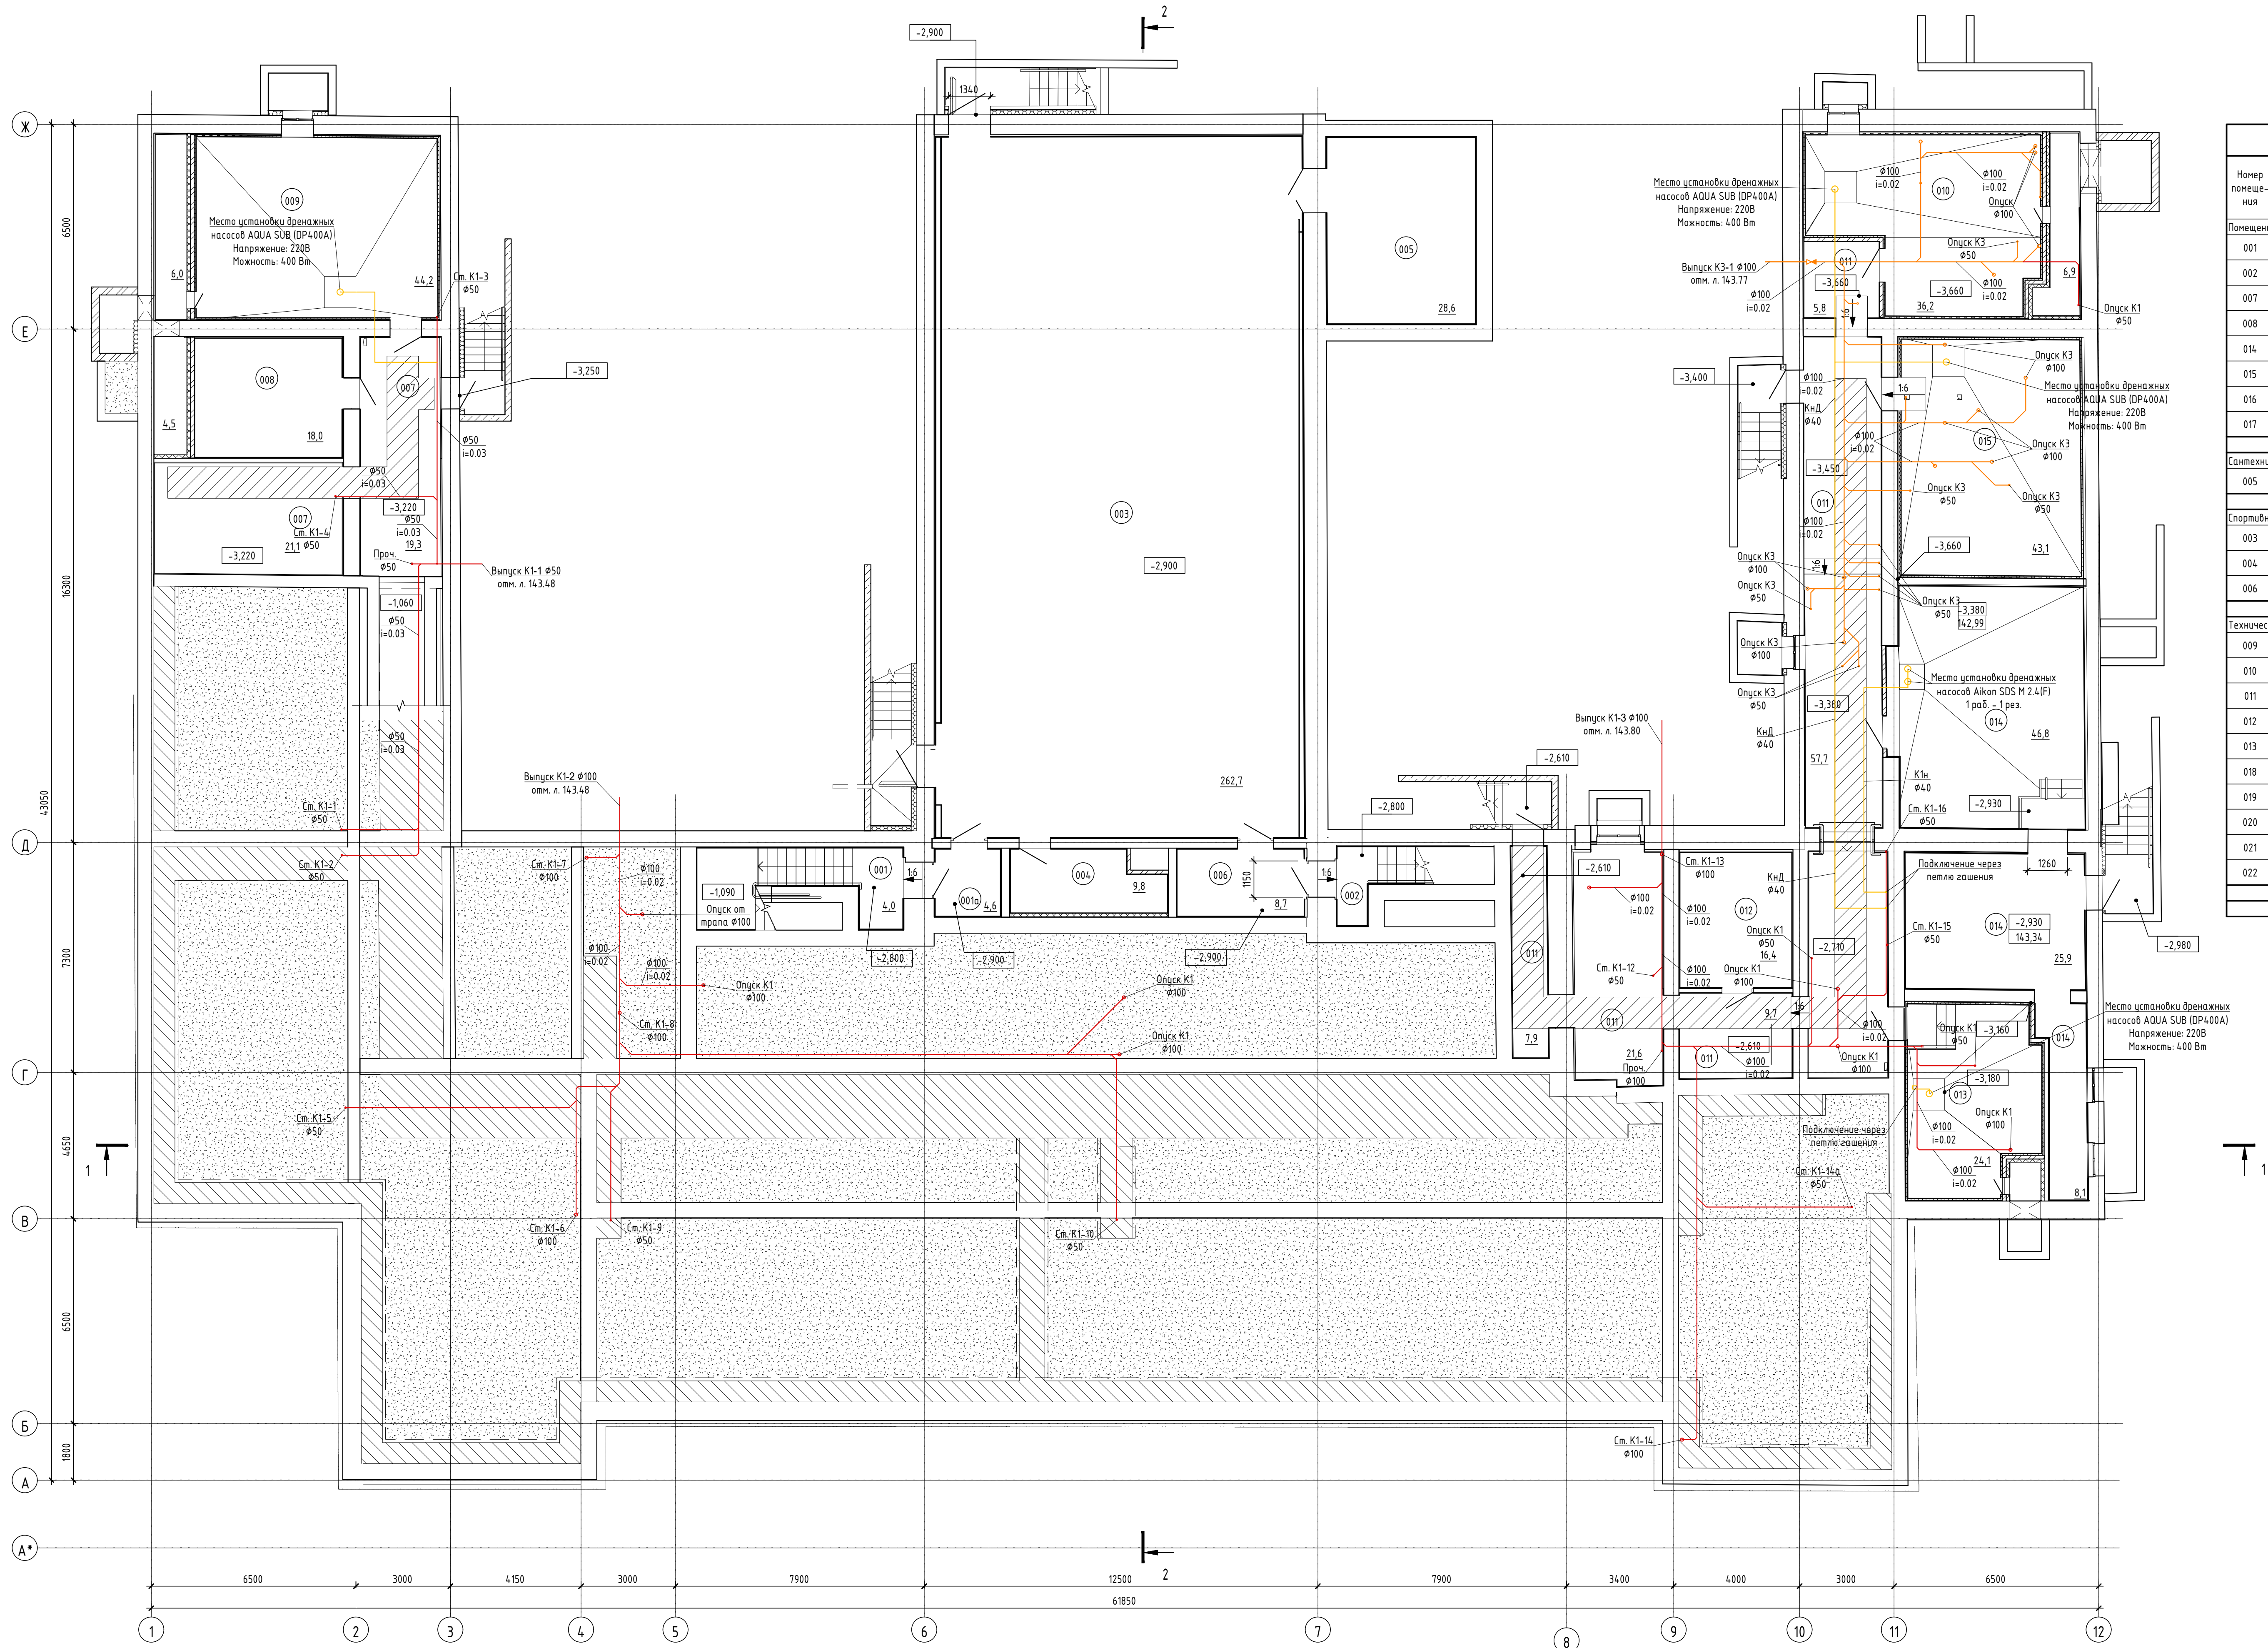

Экспликация помещений			
Номер помеще-ния	Назначение	Площадь, м²	Кат. помеще-ния
Помещения общего пользования			
001	Лестница	8,6	
002	Лестница	7,8	
007	Коридор	21,1	
008	Коридор	19,3	
014	Коридор	63,5	
015	Коридор	9,7	
016	Коридор	21,6	
017	Коридор	7,9	
		159,5	
Специальные помещения			
005	ТМ	3,6	Б4
		3,6	
Спортивно-образовательная группа помещений			
003	Спортивный зал	262,7	
004	Складная	10,9	Б3
006	Складная	28,6	Б3
		302,2	
Технические помещения			
009	Кладовая	18,0	Б4
010	Вентилятора	44,2	Д
011	Фармацевта	10,5	
012	Фармацевта	6,9	
013	Вентилятора	36,1	Б4
018	Насосная	15,9	Д
019	Вентилятора	24,1	Б4
020	Фармацевта	1,6	
021	ИТП	80,8	Д
022	Вентилятора	43,1	Д
		281,2	
		746,5	

- Условные обозначения
- трубопроводы бытовых канализаций (K1)
 - трубопроводы производственной канализации (K2)
 - стояки бытовых канализаций (K1)
 - стояки производственной канализации (K2)
 - трубопроводы проложенные скрыто. Показаны условно


636/П-24-АНО/ТЗК			
Выполнение проектно-изыскательских работ на капитальный ремонт общеобразовательного учреждения (ГБОУ школа №282 "Солнечный"), по адресу: г. Москва, ул. Барбарисов, д. 1, стр. 1			
Изм. Кол. лист. Исполн. Подп. Дата			
Разработ. Введен. А.А. 10.24			
Проверен. Введен. А.А. 10.24			
ГИП Введен. Д.А. 10.24			
Н. контр. Введен. А.А. 10.24		Этадия	Пост. Постов
		21	
План подвала. М:100. Система водоотведения		ООО "Аркона"	
		Формат А0	

— трубопроводы бытовой канализации (К1)
 — трубопроводы производственной канализации (К3)
 + стояки бытовой канализации (К1)
 + стояки производственной канализации (К3)
 - - - - - трубопроводы проложенные скрыто. Показаны условно

Экспликация помещений 1-20 этажа				
Номер помещения	Назначение	Площадь, м²	Кол. помещений	
Административные помещения				
103	Комната охраны (с диспетчерским пунктом)	9,2		
105	Кабинет с рабочим пространством для учителя-начальника и основы школы) Тип 1	41,8		
		58,0		
Гардеробы				
104	Гардероб для обучающихся (начальная школа)	46,2		
106	Гардероб для обучающихся (начальная школа)	53,7		
146	Гардероб для учителей	19,1		
147	Гардероб для обучающихся (начальная школа)	46,6		
		95,6		
Медицинский блок				
140	Кабинет врача	18,7		
141	Приемный (прибыльный) кабинет	12,9		
142	Туалет男/женского с местами для размещения идентифицирующих расборов и хранения оборудования/инструмента, при этом значении для размещения/идентификации назначения	6,1		84
143	Коридор男/женского	34,1		
		41,4		
Основная школа. Учебные кабинеты				
111	Учебный кабинет (математика)	53,3		
		53,3		
Пешеход				
129	Учебный зал	90,2		
130	Общественный зал	104,7		
131	Мечеть для столовой посуды	96,9		
132	Коридор	22,7		
133	Кладовая с мочальной оборотной тары	4,0		
134	Застарелый щит	6,6		
135	Кладовая сухих продуктов	3,7		
136	Помещение персонала с санузлом	6,9		
137	Помещение для временного хранения пешеходных оттоков	4,8		
138	ПМ	3,5		84
139	Помещение подсобных/вещей в реализации с участием/мочальной посуды	29,3		84
148	Таймер	2,2		
		214,9		

Формат А0

Системы водоотведения

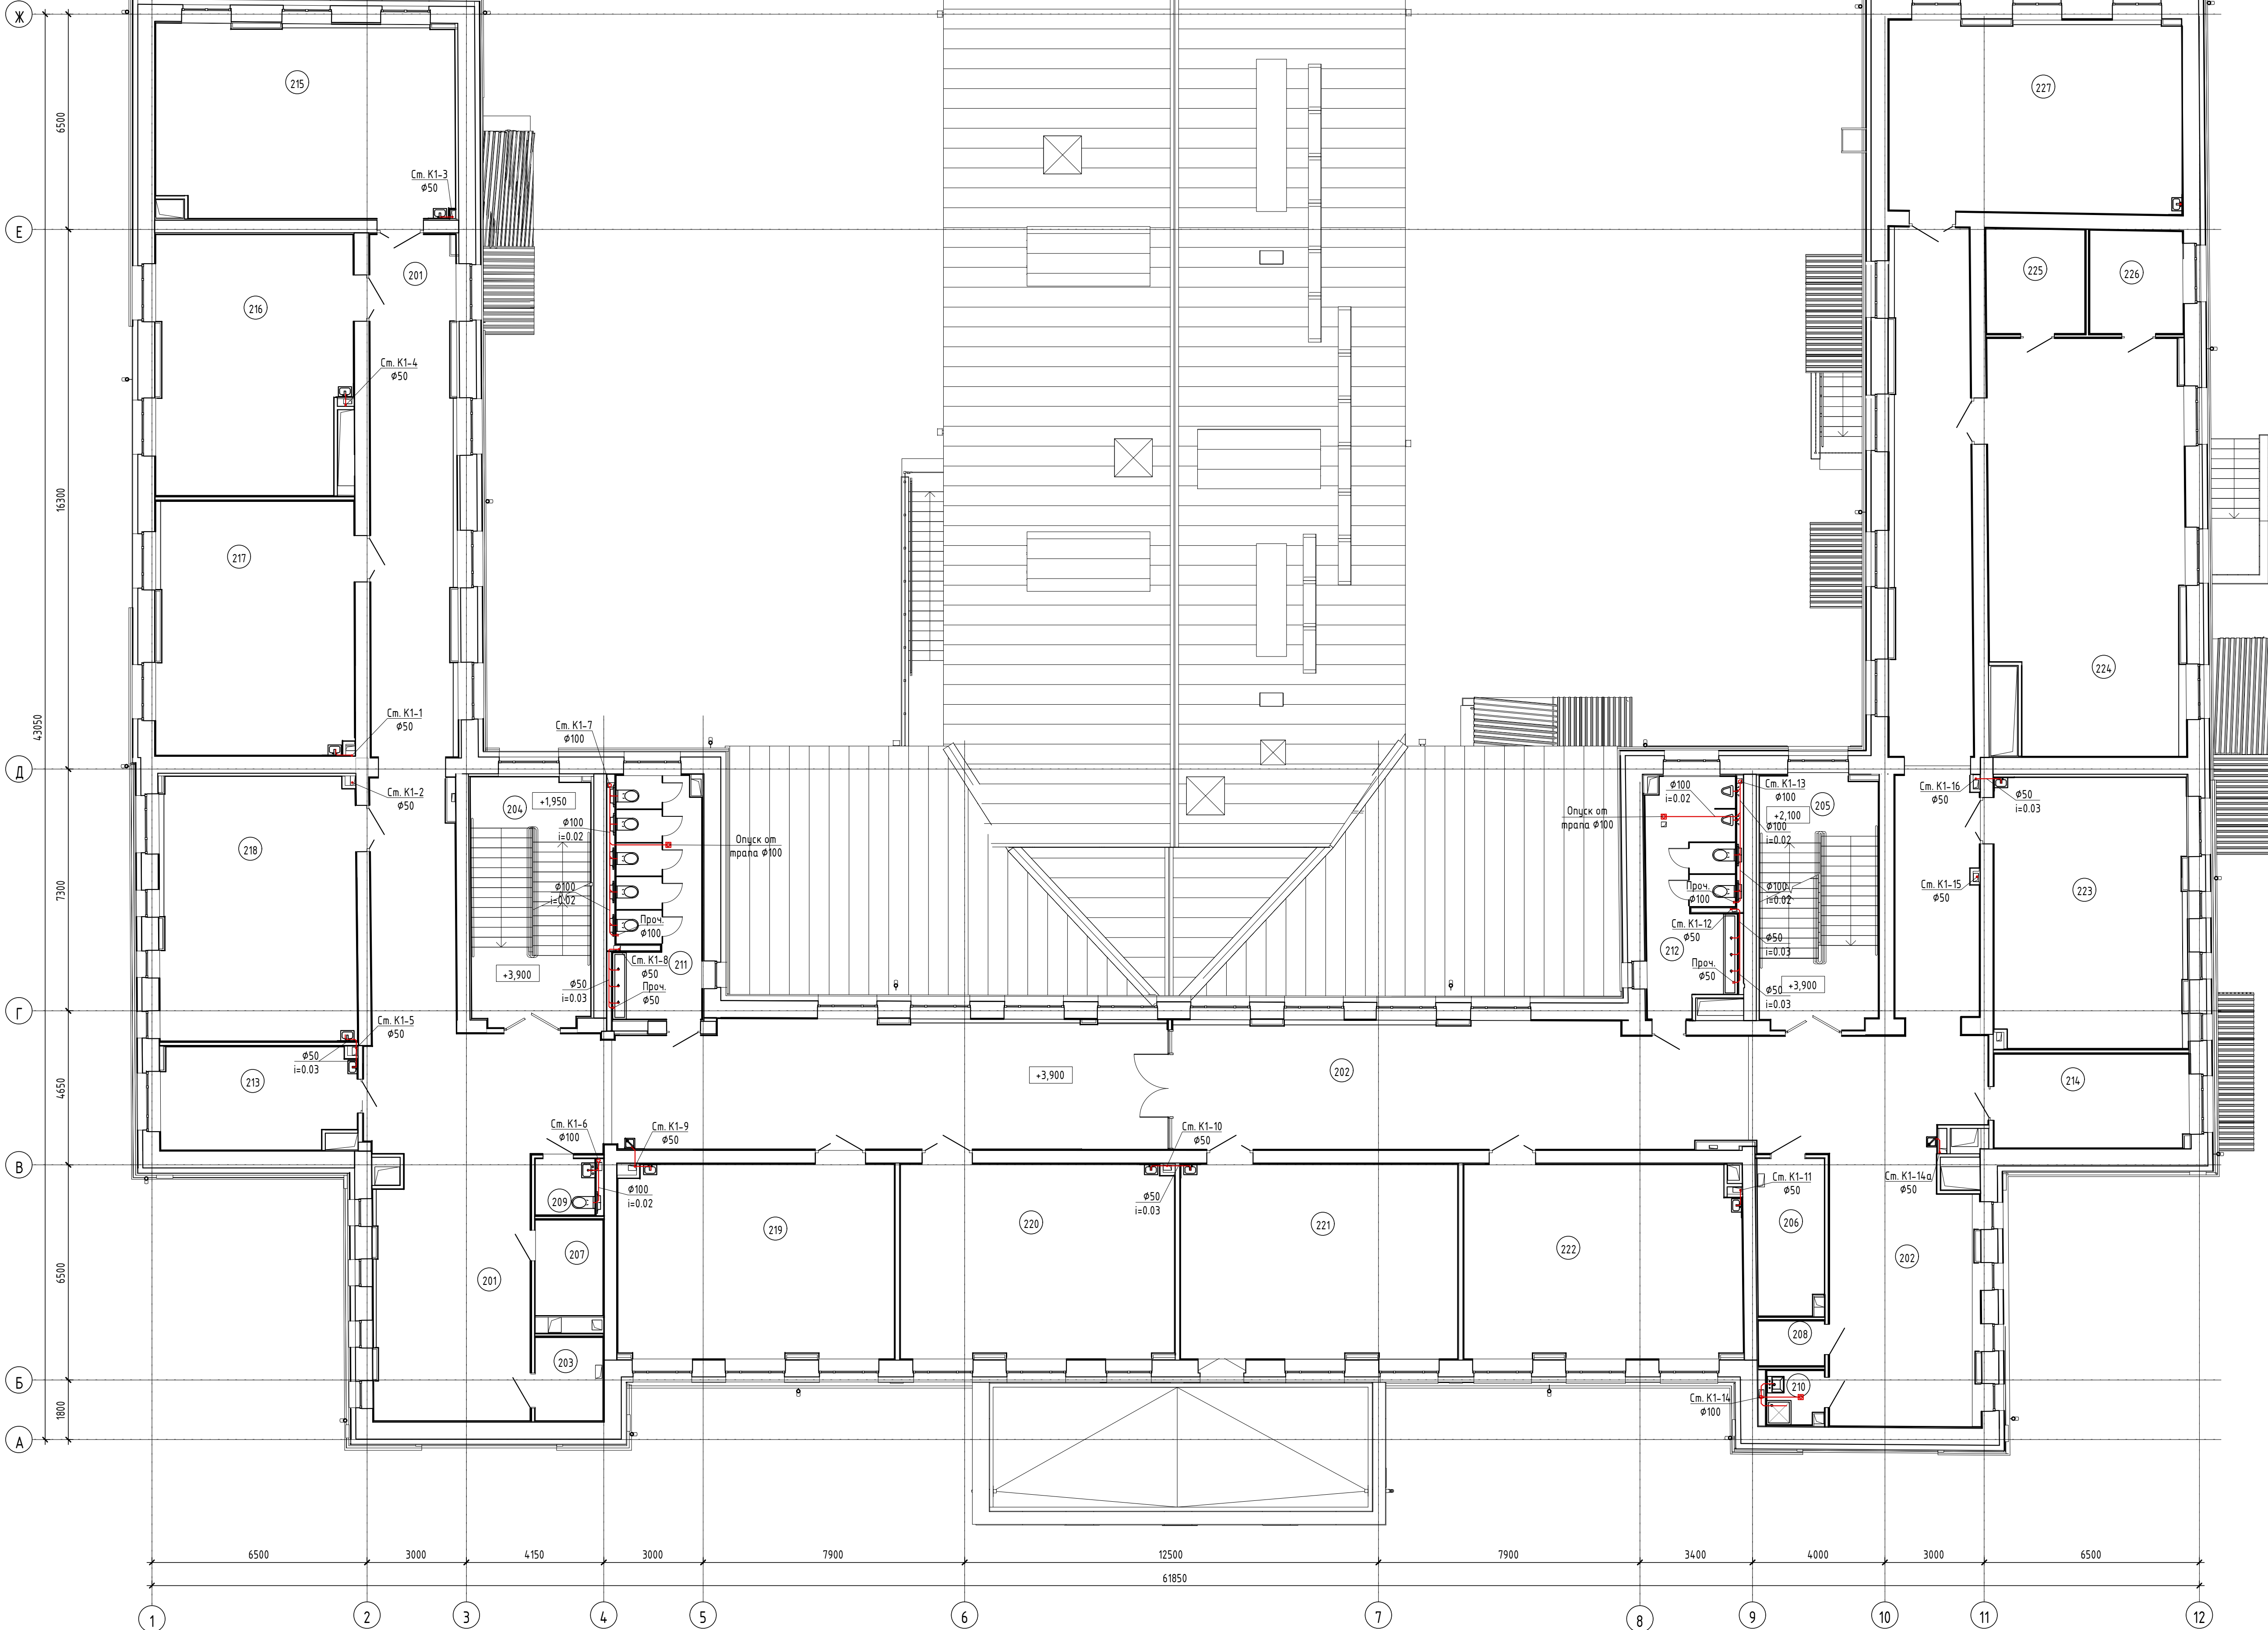


Экспликация помещений 2-го этажа			
Номер помеще- ния	Наименование	Площадь, кв. м	Кат. помеще- ния
Административные помещения			
215	Коридор для индивидуальных занятий, в т.ч. сучумен-мен, логопедов	18,2	
216	Административный кабинет (начальная школа) Тип 1	16,9	
		35,1	
Начальная школа. Учебные кабинеты			
217	Учебный кабинет (1 класс)	52,8	
217	Учебный кабинет (1 класс)	52,8	
218	Учебный кабинет (1 класс)	46,2	
219	Учебный кабинет (1 класс)	47,7	
220	Учебный кабинет (2-4 классы)	49,2	
221	Учебный кабинет (2-4 классы)	48,9	
222	Учебный кабинет (2-4 классы)	49,6	
223	Учебный кабинет (2-4 классы)	49,3	
224	Учебный кабинет (2-4 классы)	47,9	
228	Учебный кабинет (2-4 классы)	51,7	
		489,1	
Помещения общего пользования			
201	Коридор	164,4	
202	Рекреация	37,5	
203	Рекреация	36,2	
204	Рекреация клетка (Тип Л1)	27,4	
205	Ассиминная клетка (Тип Л1)	27,6	
229	Коридор	162,2	
		435,2	
Специальные помещения			
210	Туалет для персонала	3,2	
211	Туалет	2,8	
212	Уборная для девочек (начальная школа)	19,4	
213	Уборная для мальчиков (начальная школа)	18,8	
		44,2	
Спортивно-оздоровительная группа помещений			
225	Гимнастический зал	72,8	
226	Раздевальня Тип 1	9,5	
227	Раздевальня Тип 1	9,5	
		91,3	
Технические помещения			
206	Помещение СС	5,3	Б4
207	Помещение СС	9,6	Б4
208	Подсобное помещение	2,1	
209	Подсобное помещение	6,8	Б4
		223	
		118,5	

Условные обозначения

- трубопроводы бытовой канализации (К1)
- трубопроводы производственной канализации (К3)
- ⊕ — стояки бытовой канализации (К1)
- ⊕ — стояки производственной канализации (К3)
- трубопроводы, продолженные скотом. Показаны условно

									696/П-24-АНО/ТЭК
									Выполнение проектно-изыскательских работ на капитальный ремонт общеобразовательных учреждений ("Школа №82 "Соколиный"). по адресу г. Москва ул. Боровицкая д. 4, стр. 1.
Иван Ю.А.	Улицин М.В.	Малин П.С.	Давидов Д.А.						
Григорьев А.В.	Киселева А.А.	Борисов В.В.	10.24						Обследование технического состояния строительных конструкций
Павлов С.В.	Земцова Е.А.	Белый Д.О.	10.24						и инженерных систем здания
ГИП								23	
									План 2 этажа. М1-100. Система водоотведения
									000 "Арктика"
Н. Контарь	Цаповой А.А.		10.24						

План 3-го этажа
Системы водоотведения

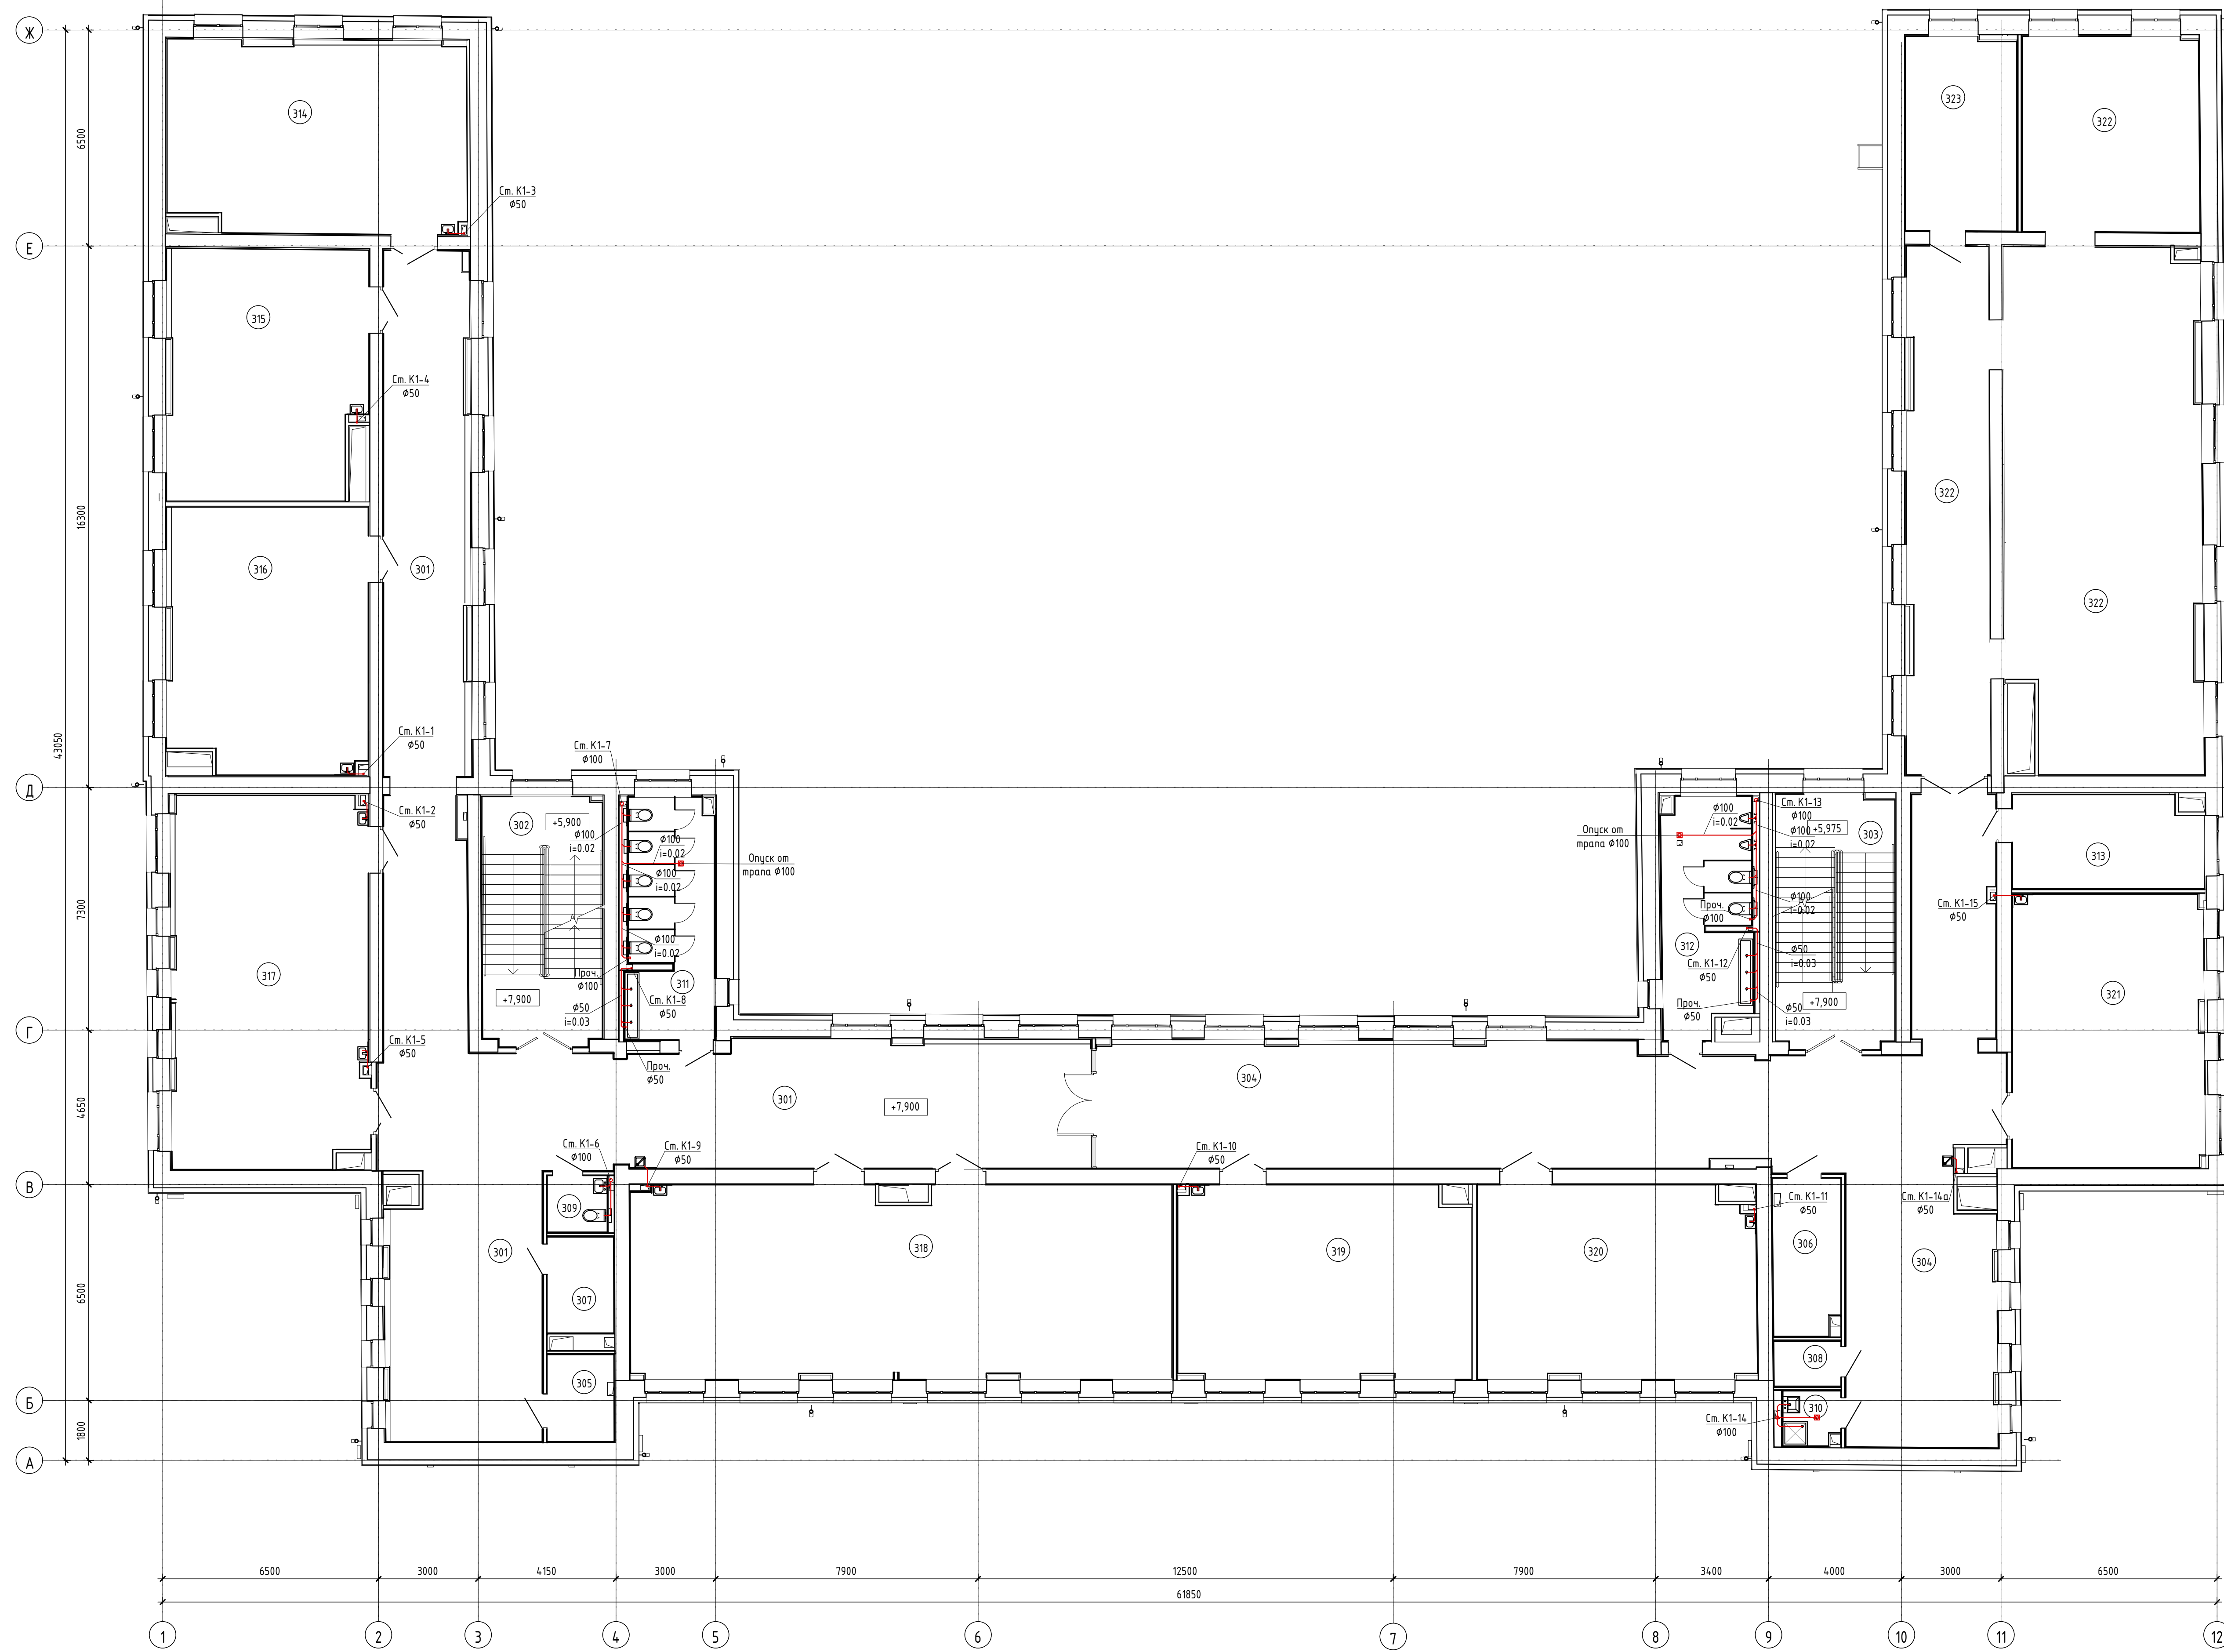


Условные обозначения

- трубопроводы бытовой канализации (К1)
- трубопроводы производственной канализации (К3)
- ⊕ стояки бытовой канализации (К1)
- ⊕ стояки производственной канализации (К3)
- трубопроводы проложенные скрито. Показаны условно

Экспликация помещений 3-го этажа				
Номер помеще-ния	Наименование	Площадь, кв.м	Кол. помеще-ния	
Административные помещения				
314	Кабинет для индивидуальных занятий, 6 рабочих компьютерных мест	16,0		
		16,0		
Библиотека-медиатека				
323	Медиаинформационный информационный библиотечный центр с залом для индивидуальных и групповых занятий, медиацентр, 163,7 центра чтения учащихся	163,7		
324	Медиаинформационный информационный библиотечный центр хранения (закрытый фонд) учебные книги	19,8	83	
		183,6		
Начальная школа. Учебные кабинеты				
315	Учебный кабинет (2-4 классы)	52,0		
316	Учебный кабинет (2-4 классы)	45,0		
317	Учебный кабинет (2-4 классы)	48,1		
318	Учебный кабинет (2-4 классы) с возможностью делегитимизированной перерывной на фва поменяющаяся школа	66,8		
320	Учебный кабинет (2-4 классы)	51,4		
321	Учебный кабинет (2-4 классы)	48,9		
322	Учебный кабинет (2-4 классы)	47,9		
		366,0		
Помещения общего пользования				
301	Коридор	142,4		
302	Лестничная клетка (Тип ЛП)	27,3		
303	Лестничная клетка (Тип ЛП)	27,3		
304	Рекреация	37,8		
305	Рекреация	36,2		
325	Коридор	100,2		
		391,6		
Санитарно-технические помещения				
310	Туалет для персонала	3,2		
311	ПМ	2,8		
312	Уборная для девочек (начальная школа)	19,0		
313	Уборная для мальчиков (начальная школа)	18,9		
		43,8		
Технические помещения				
306	Помещение СС	5,4	84	
307	Помещение СС	5,7	84	
308	Подсобное помещение	9,9		
309	Подсобное помещение	2,8	84	
		23,8		
Учебно-спортивная студия				
319	Творческая мастерская с возможностью делегитимизированной перерывной на фва помещения	94,8		
		94,8		

						696 /П-24- АНО/ТЭК					
						Выполнение протектно-экологических работ на капитальный ремонт общеобразовательного учреждения (ГБОУ Школа №282 "Соколники"), по адресу г. Москва ул. Барбарина д. 1, стр. 1.					
Изм.	Код изм.	Листов	Экз.	Подп.	Дата				Этапы	Лист	Листов
Разроб.		Вилькин А. В.			10.24	Обследование технического состояния отслуживших конструкций					
Проектиров.		Мельников Д. А.			10.24					24	
ГИП		Резнилов Д. С.			10.24	и инженерные системы зданий					
План 3 этажа М:100. Система водоснабжения:						ООО "Арикан"					
Н. контрлг.		Заванова А. А.			10.24						

План 4-го этажа
Системы водоотведения

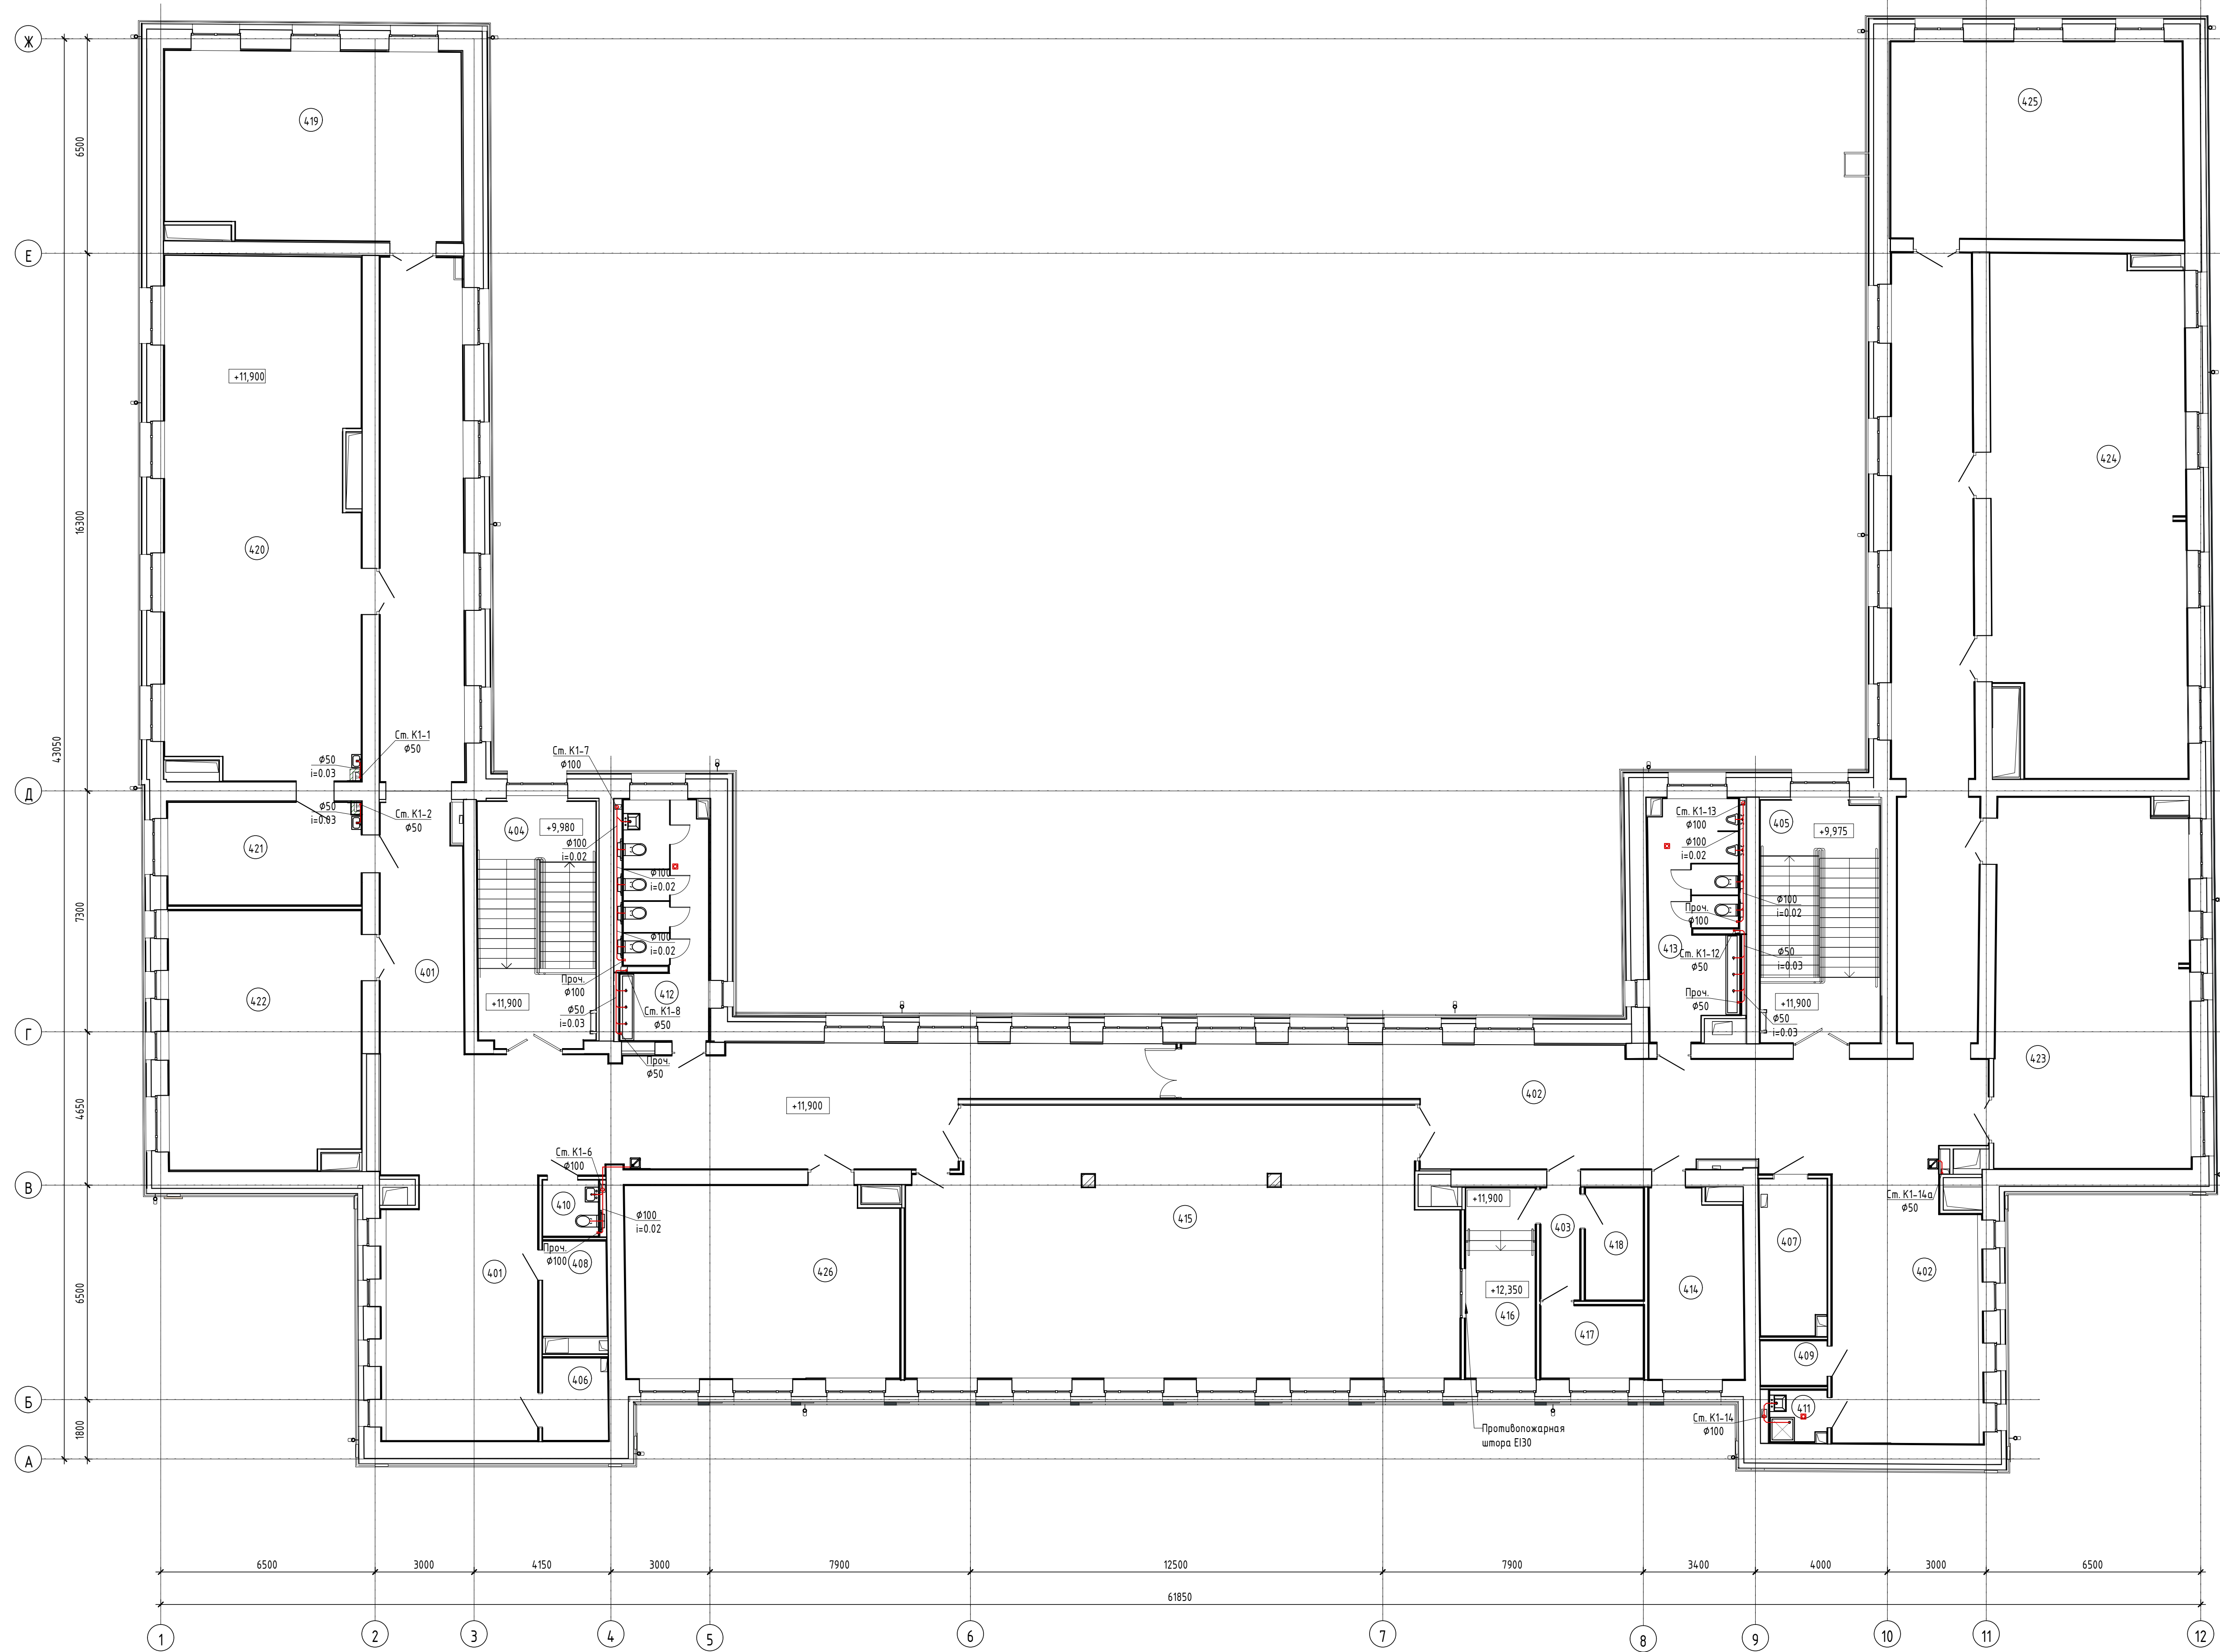


Условные обозначения

- трубопроводы бытовой канализации (К1)
- трубопроводы производственной канализации (К3)
- + стояки бытовой канализации (К1)
- + стояки производственной канализации (К3)
- трубопроводы проложенные скрыто. Показаны условно

Экспликация помещений 4–20 этажа				
Номер помещения	Наименование	Площадь, м²	Кол. помещений	
Административные помещения				
416	Кабинет для сбора/разбора занятий, 8 в.ч. info@egzon.ru	16,2		
		16,2		
Экспертный зал				
417	Информационный пространств., с видеосъемочным залом (с экраном в рабочем плане)	131,3		
418	Технический центр	12,4	83	
419	Архитектурная	6,9		
420	Клавиатура интерактора	6,1		
		156,6		
Основная школа. Учебные кабинеты				
421	Кабинет математики	51,0		
422	Учебный кабинет (для изучения естественных биологич./географич. Tut 2	93,0		
423	Лабораторная биологии	18,5	83	
424	Учебный кабинет (история)	45,3		
425	Кабинет иностранного языка с возможностью видеотрансляционной переборкой на два помещения	66,0		
426	Учебный кабинет информатики с возможностью видеотрансляционной переборкой на два помещения	93,4		
427	Кабинет русского языка и литературы	50,8		
428	Кабинет русского языка и литературы	48,2		
		466,3		
Помещения общего пользования				
401	Коридор	137,0		
402	Коридор	137,8		
403	Рекреация	35,9		
404	Рекреация	37,2		
405	Коридор	4,1		
406	Лестничная клетка (Tut 1П)	26,9		
407	Лестничная клетка (Tut 1П)	26,8		
		399,7		
Санитарно-технические помещения				
412	Гулет для персонала	2,9		
413	РМ	2,7		
414	Уборная для девочек (основная школа)	19,2		
415	Уборная для мальчиков (основная школа)	19,2		
		44,1		
Технические помещения				
408	Помещение СС	9,1	84	
409	Помещение СС	9,7	84	
410	Подсобное помещение	5,7		
411	Подсобное помещение	2,8	84	
		23,3		
		1195,1		

						696/П-24-АНО/ТЗК
						Выполнение претренинговых работ на капитальный ремонт образовательного учреждения (ГБОУ Школа №282 "Соколиники"), по адресу: Москва ул. Борзоев д. 1, стр. 1
Изм.	Вкл	Испол	Прогн	Дата		
Разработчик	Филиппов А.Б.			10.24		10.24
Проверенный	Руднев В.С.			10.24		10.24
ГИП	Роговой Д.С.			10.24		10.24
					Обследование технического состояния строительных конструкций и инженерных систем здания	Строгий Пуст
					План 4 этажа М1-100 Система водоснабжения	25
Ит. континг	Шарова А.А.			10.24		ООО "Аркона"

План чердака
Системы водоотведения

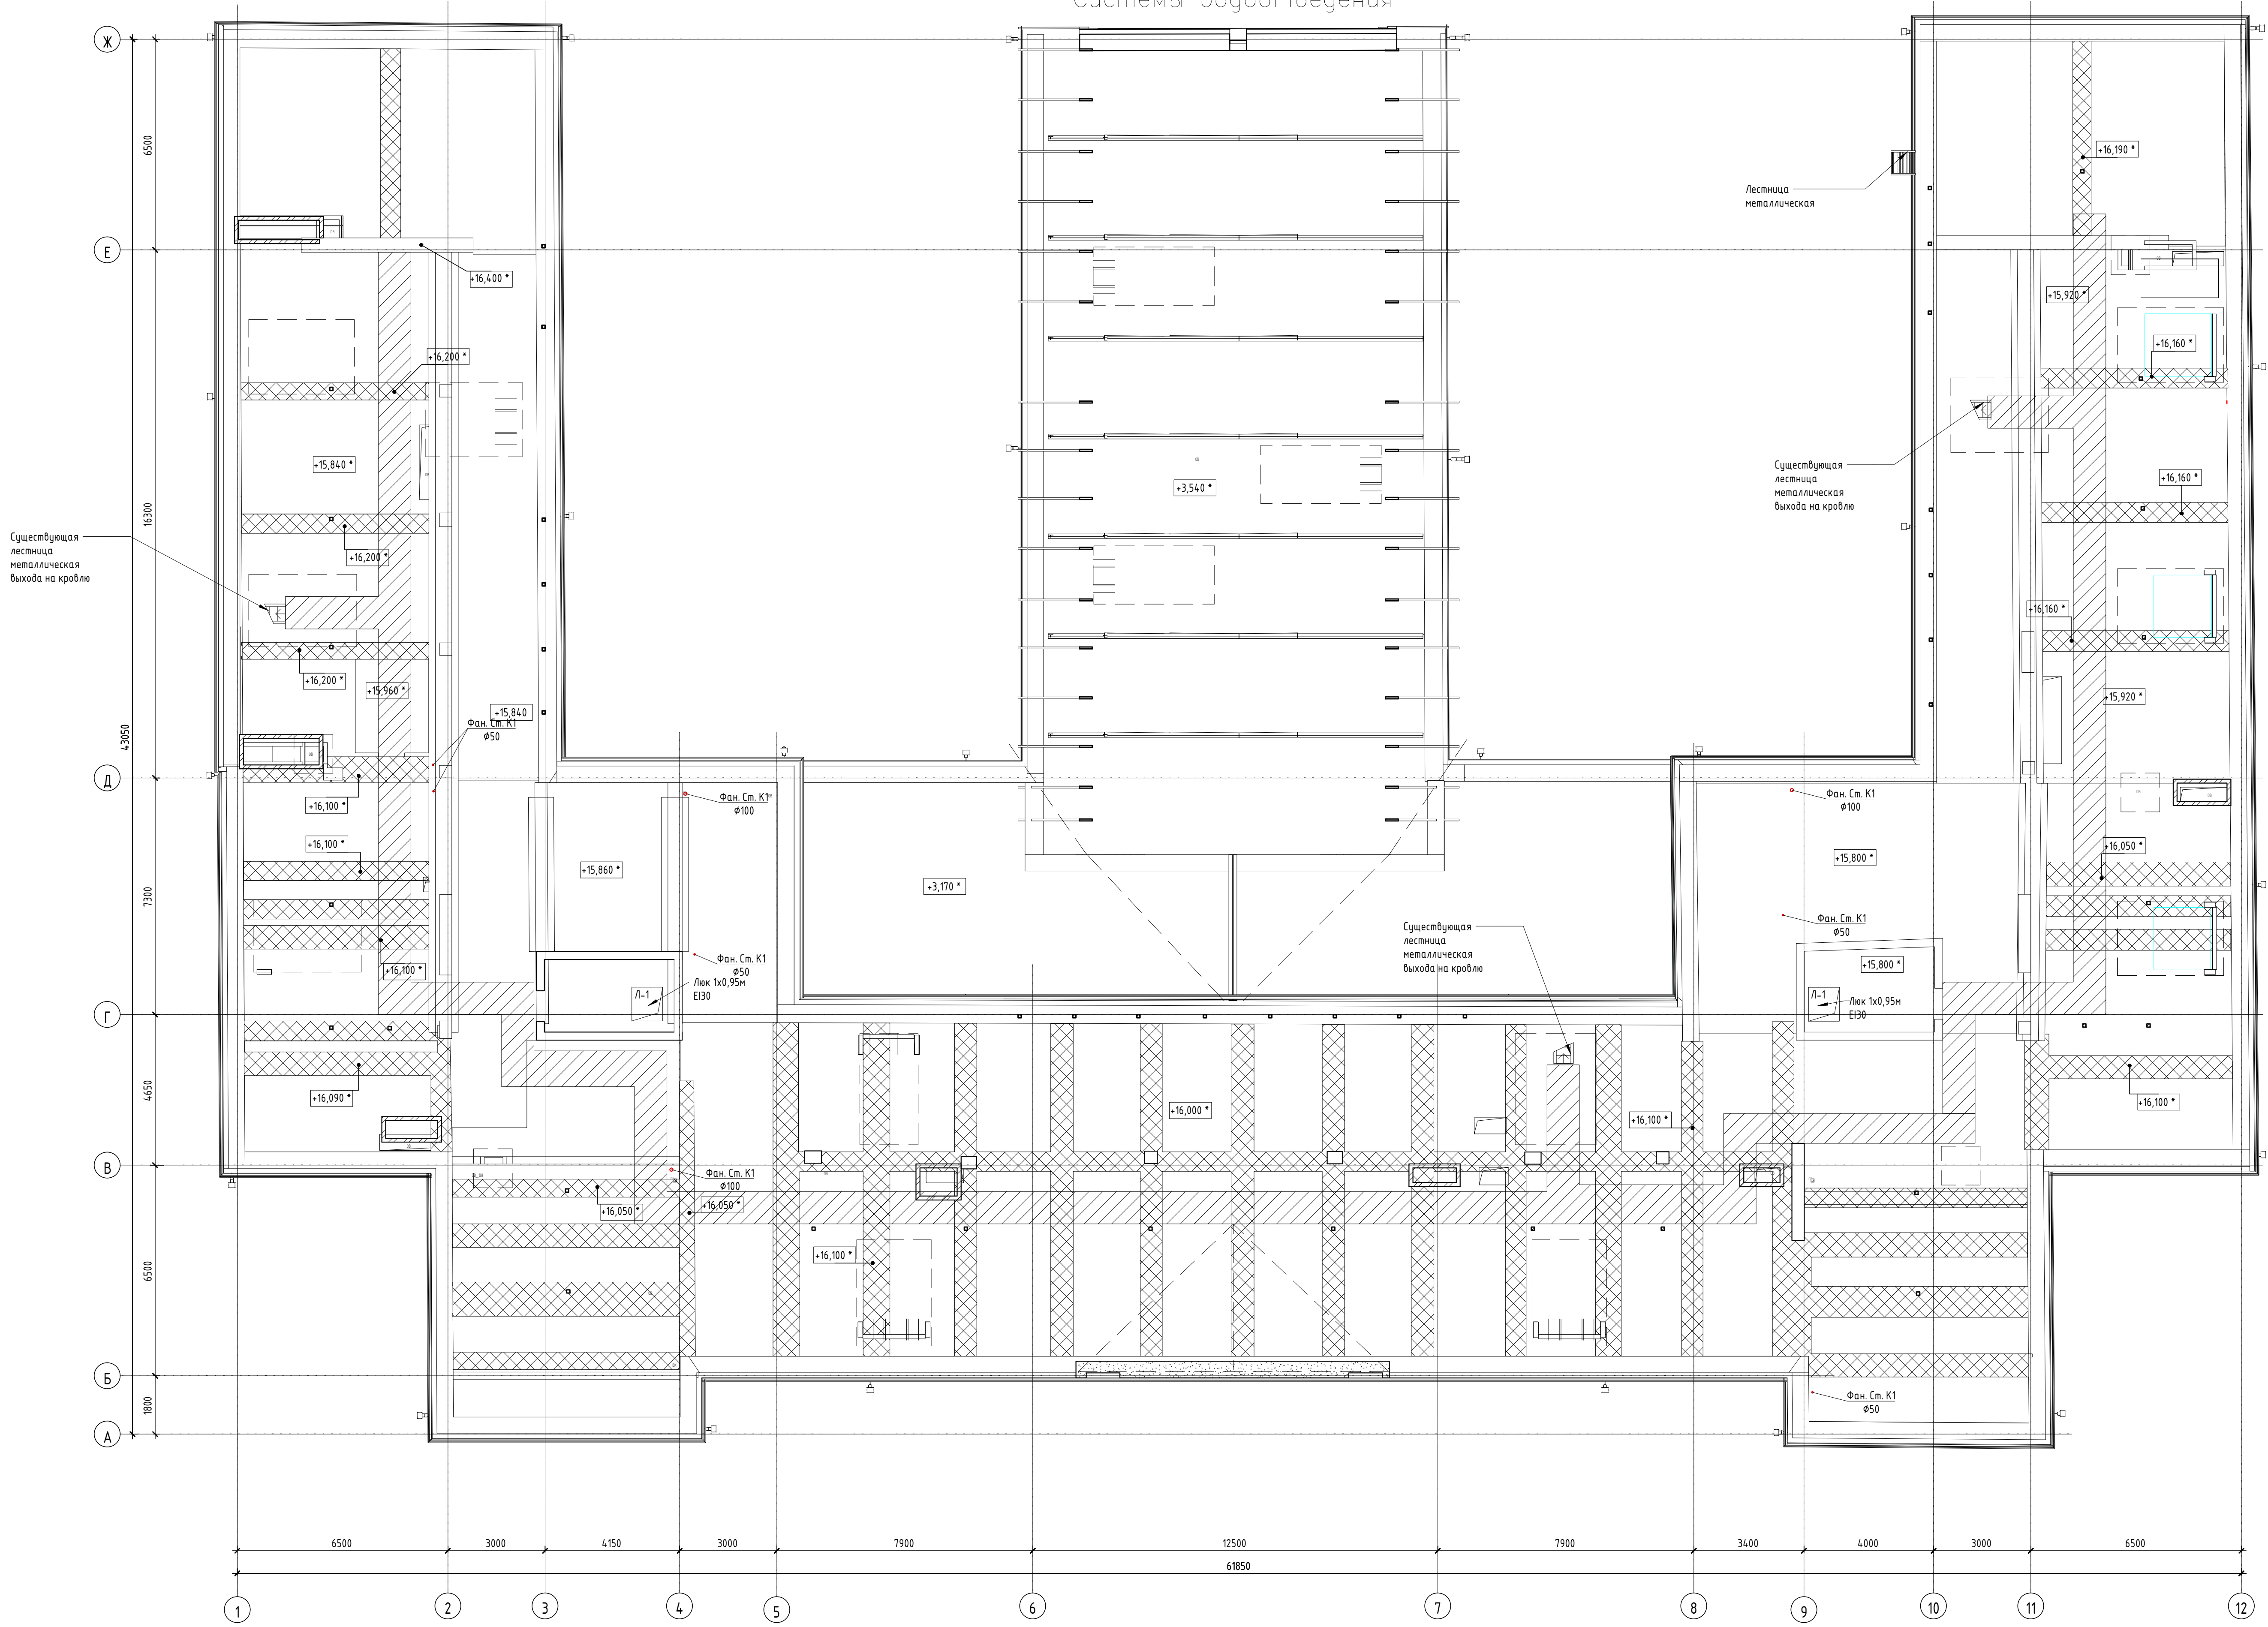


Условные обозначения

- трубопроводы бытовой канализации (К1)
- трубопроводы производственной канализации (К3)
- стояки бытовой канализации (К1)
- стояки производственной канализации (К3)
- трубопроводы проложенные скрыто. Показаны условно


					696/П-24- АНО/ТЗК				
					Выполнение проектно-изыскательских работ на капитальный ремонт общеобразовательного учреждения (ГБОУ Школа №1282 "Сокольники"), по адресу: г. Москва, ул. Барбюльна, д. 1, стр. 1				
Изм.	Кол. в листе	Исполн.	Дата				Статус	Лист	Листов
Разраб.	Вязинин А.В.	10.24	10.24		Обследование технического состояния строительных конструкций и инженерных систем здания			26	
Проберил	Велецков А.А.	10.24	10.24						
ГИП	Емельянов Д.А.	10.24	10.24		План чердака. М1:100. Система водоотведения				
Н. контр.	Цыганков А.А.	10.24	10.24				ООО "Аркана"		

План подвала
Системы электроснабжения и слабых токов

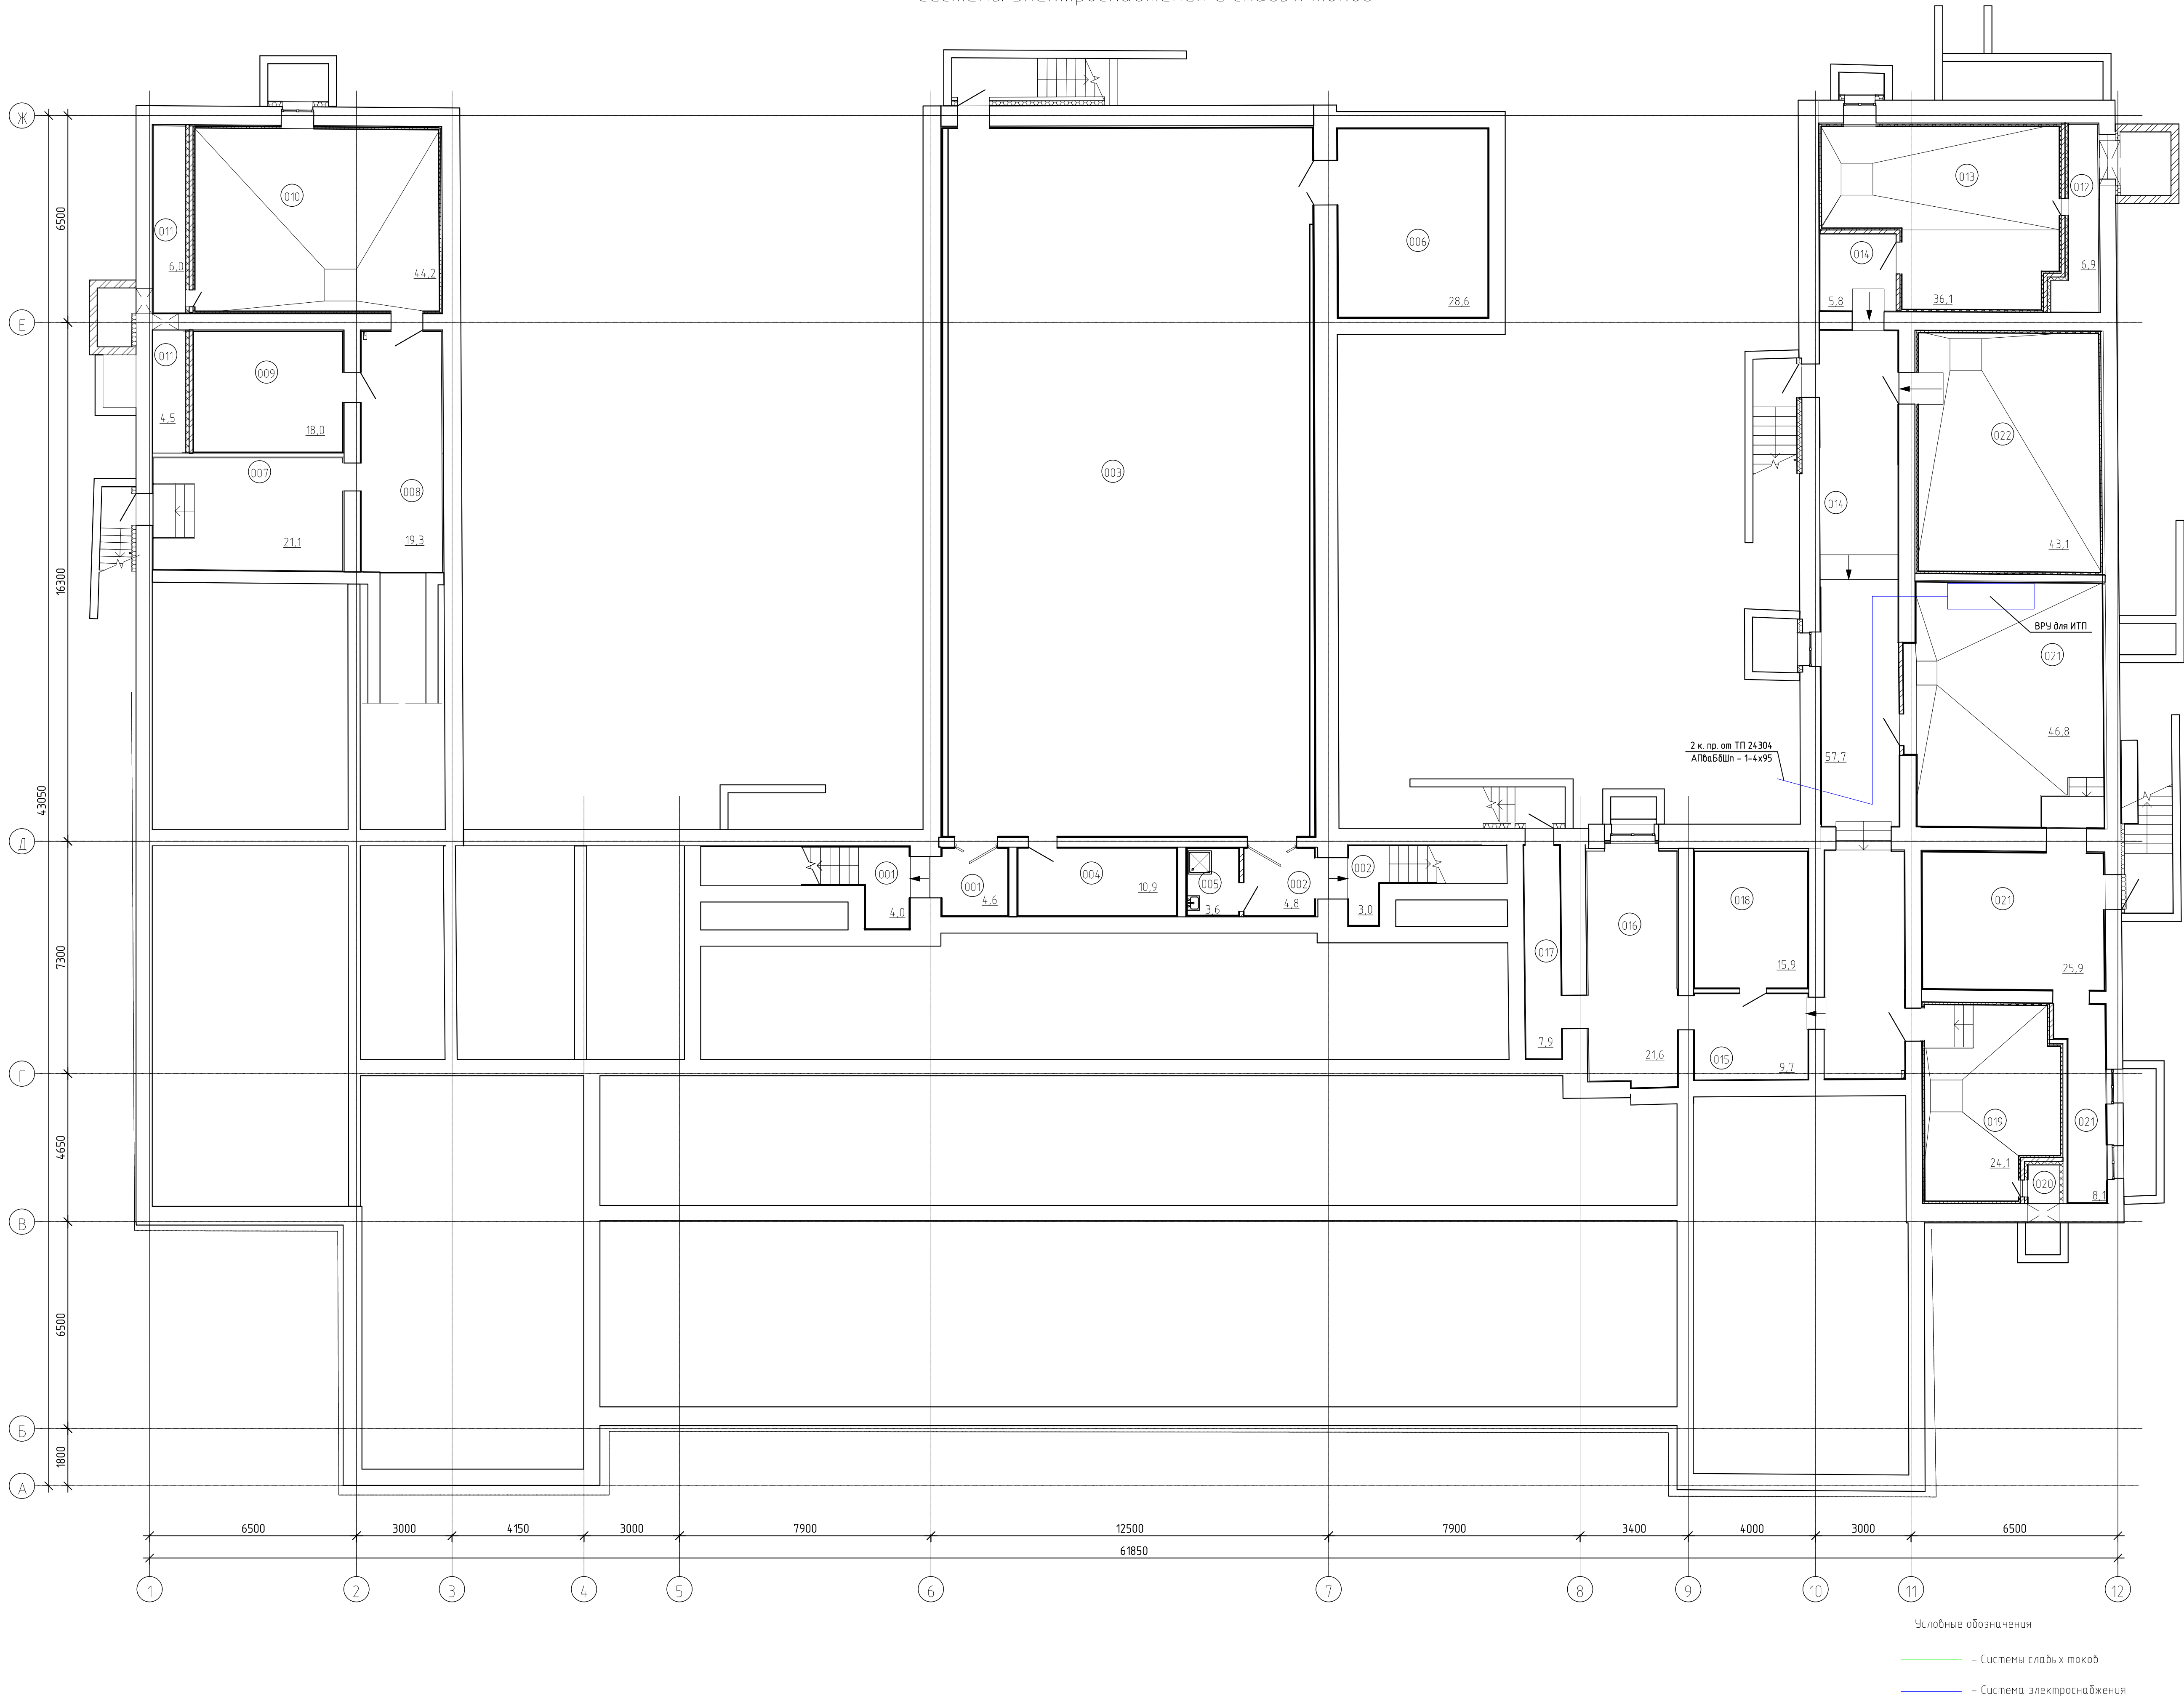

Экспликация помещений			
Номер помеще-ния	Наименование	Площадь, м²	Кат. помеще-ния
Помещения общего пользования			
001	Лестница	8,6	
002	Лестница	7,8	
007	Коридор	21,1	
008	Коридор	19,3	
014	Коридор	63,5	
015	Коридор	9,7	
016	Коридор	21,6	
017	Коридор	7,9	
		155,5	
Специальные помещения			
005	ЛТД	3,6	В4
		3,6	
Спортивно-оздоровительная группа помещений			
003	Спортивный зал	262,7	
004	Снарядная	10,9	В3
006	Снарядная	20,6	В3
		392,2	
Технические помещения			
009	Кладовая	18,0	В4
010	Вентилятора	44,2	Д
011	Фармака	10,5	
012	Фармака	6,9	
013	Вентилятора	36,1	В4
018	Насосная	15,9	Д
019	Вентилятора	24,1	В4
020	Фармака	1,6	
021	ИТП	80,8	Д
022	Вентилятора	43,1	Д
		281,2	
		746,5	

План 1-го этажа
Системы электроснабжения и слабых токов

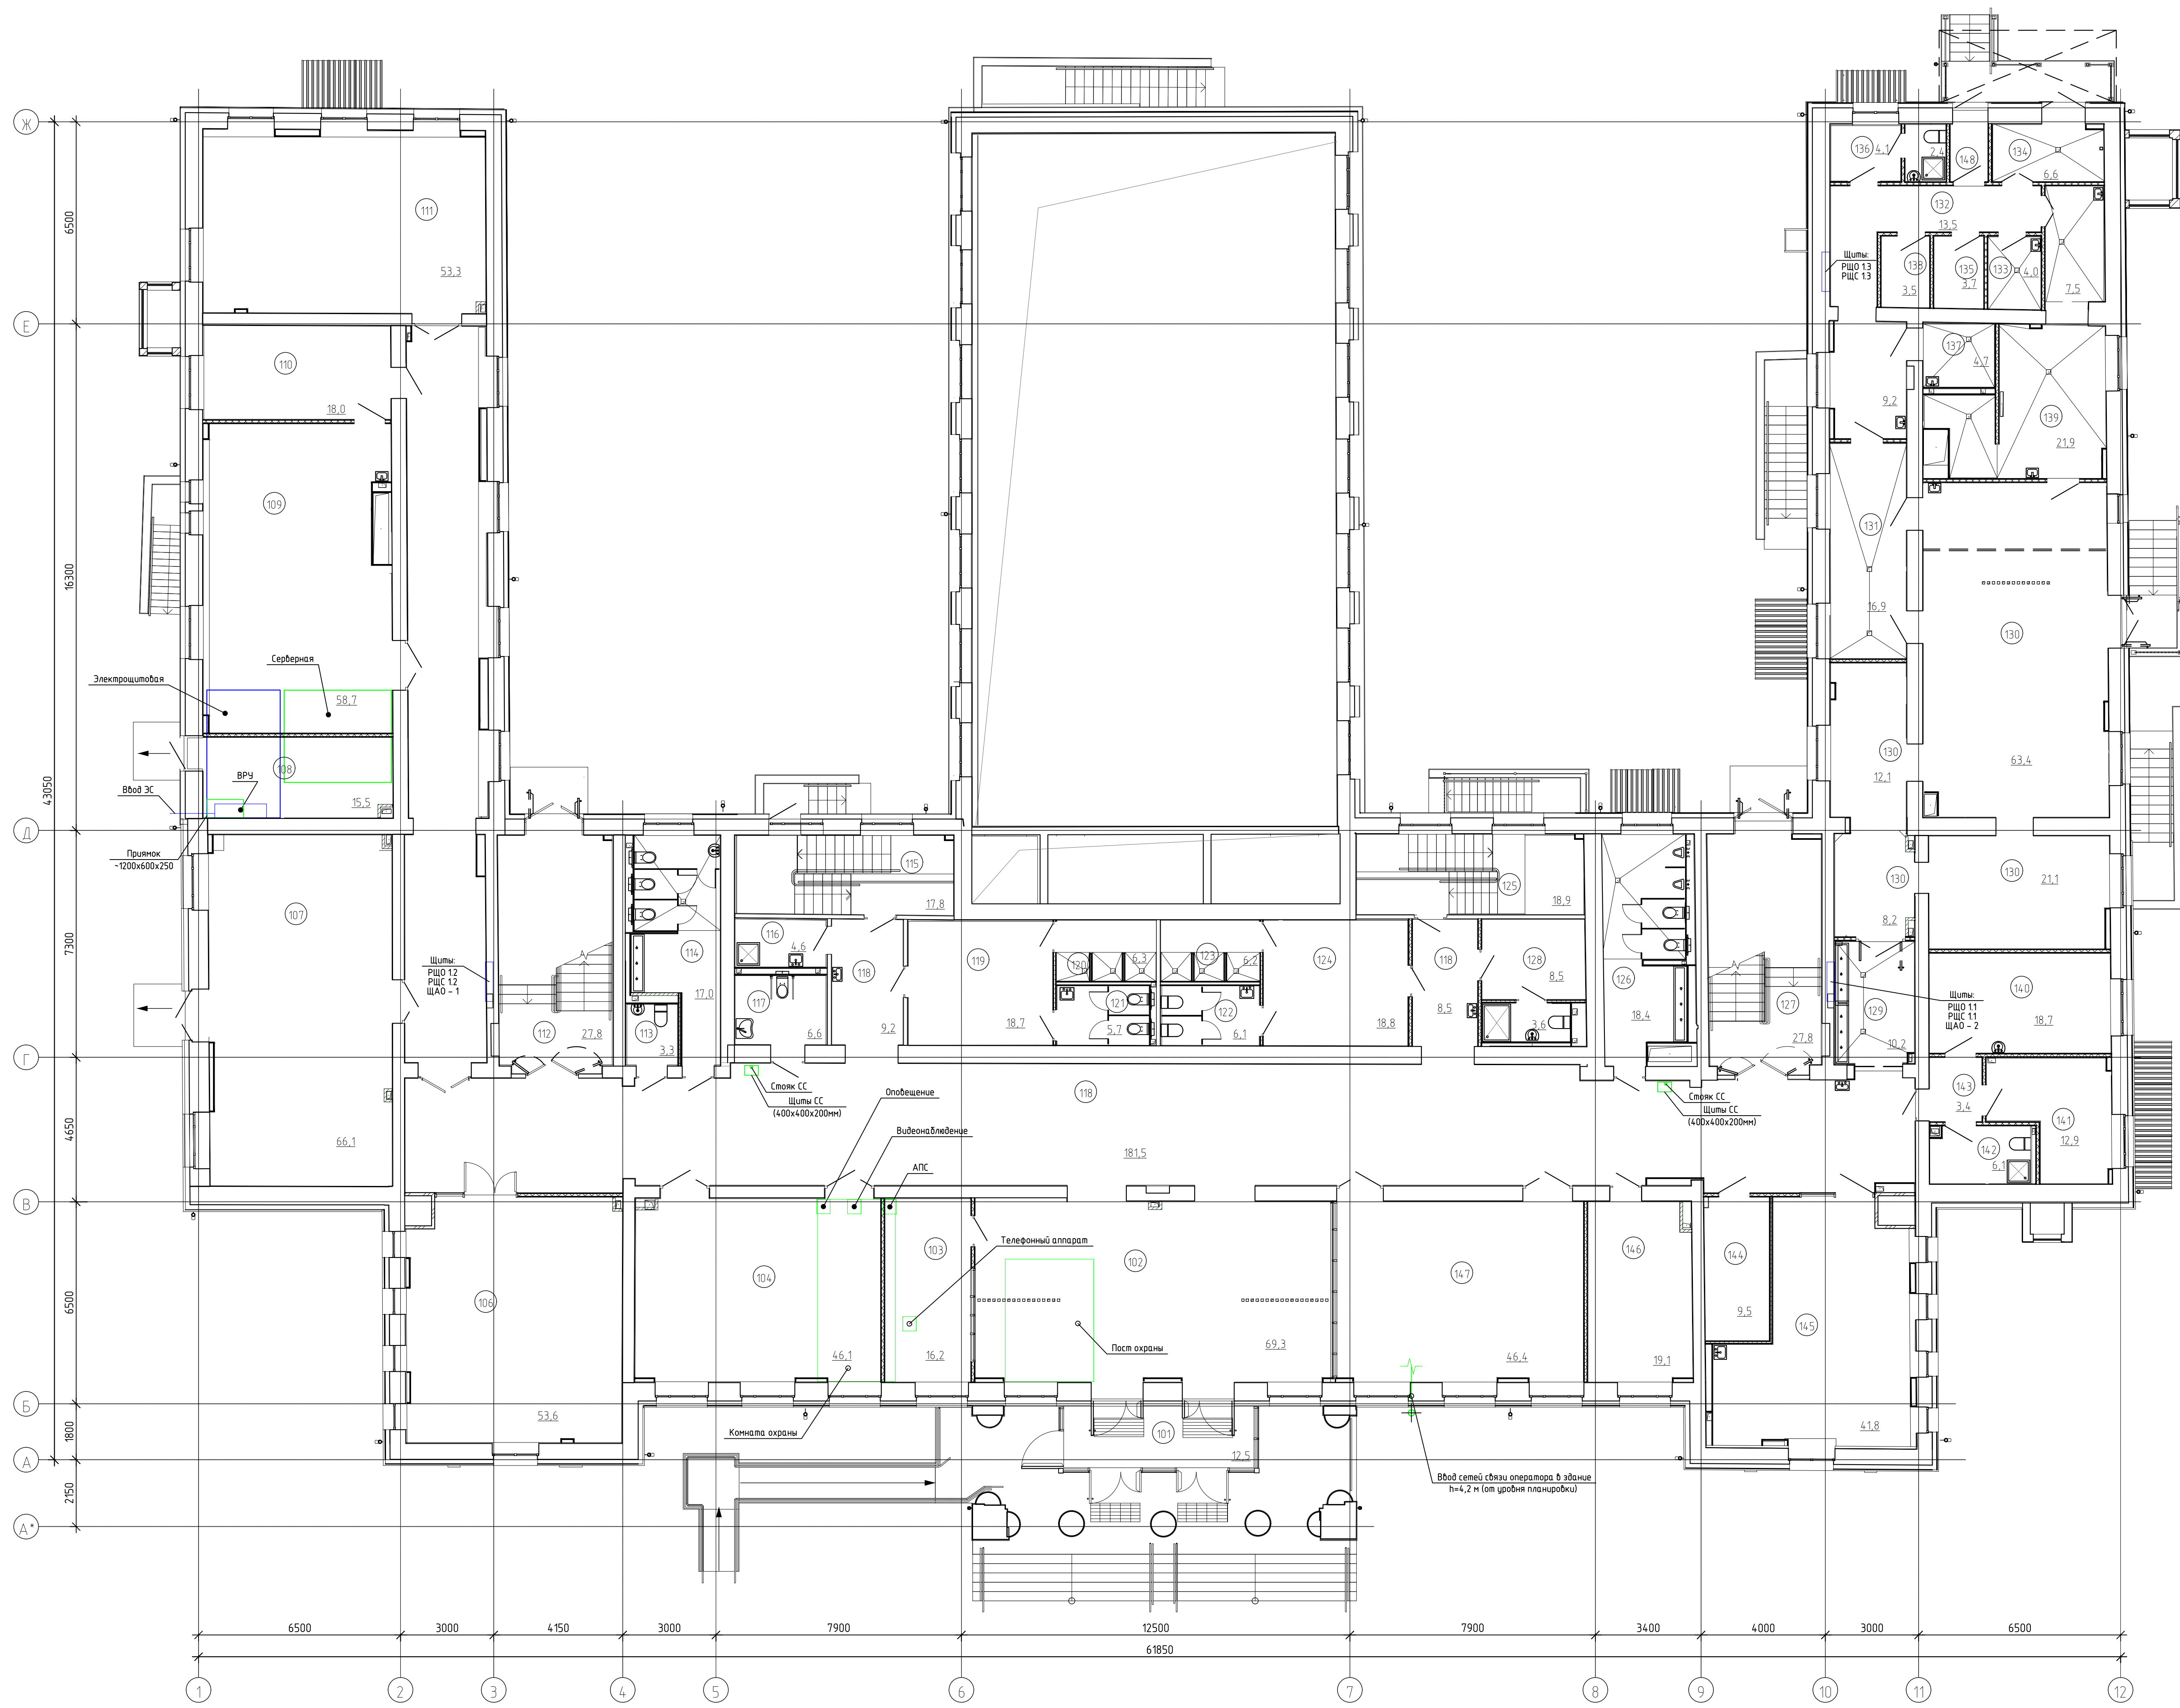

Экспликация помещений 1-го этажа			
Номер помеще-ния	Наименование	Площадь, м²	Кат. помеще-ния
Помещения общего пользования			
101	Танбур	12,5	
102	Вестибюль (с зоной ожидания для посетителей)	69,3	
105	Коридор	60,3	
112	Лестничная клетка	27,8	
115	Лестничная клетка	17,8	
118	Коридор	99,2	
125	Лестничная клетка	18,9	
127	Лестничная клетка	27,8	
		433,5	
Сантехнические помещения			
113	Туалет для персонала	3,3	
114	Уборная для девочек	17,0	
116	ПМ	4,6	В4
117	Универсальная уборная для МГН	6,6	
126	Уборная для мальчиков	18,4	
		69,9	
Специализированные помещения			
107	Кабинет материальной технологии Тип 1	66,1	В3
109	Кабинет материальной технологии Тип 2	58,7	В3
110	Кладовая канцелярии материальной технологии	18,0	В3
		142,9	
Спортивно-оздоровительная группа помещений			
119	Раздевальня Тип 1	18,7	
120	Душевая	6,3	
121	Уборная	5,7	
122	Уборная	6,1	
123	Душевая	6,2	
124	Раздевальня Тип 1	18,8	
128	Тренерская с санузлом	12,1	
		78,9	
Технические помещения			
108	Электрощитовая	15,5	В4
144	Помещение СС	9,5	В4
		25,0	
		103,8	

Экспликация помещений 1-го этажа			
Номер помеще-ния	Наименование	Площадь, м²	Кат. помеще-ния
Административные помещения			
103	Комната охраны (с диспетчерским пунктом)	16,2	
145	Кабинет с рабочим пространством для учителей (начальная и основная школа) Тип 1	41,8	
		58,0	
Гардеробная			
104	Гардероб для обучающихся (основная школа)	46,2	
106	Гардероб для обучающихся (начальная школа)	53,7	
146	Гардероб для учителей	19,1	
147	Гардероб для обучающихся (начальная школа)	46,4	
		165,4	
Медицинский блок			
140	Кабинет врача	18,7	
141	Процедурный (прибыльный) кабинет	12,9	
142	Туалет медблока с местом для приготовления/дезинфицирования растворов и хранения уборочного инвентаря, предназначенных для помещений медицинского назначения	6,1	В4
143	Коридор медблока	3,4	
		41,1	
Основная школа. Учебные кабинеты			
111	Учебный кабинет (математика)	53,3	
		53,3	
Питание			
129	Универсальная	10,2	
130	Обеденный зал	104,7	
131	Моечная для столовой посуды	16,9	
132	Коридор	22,7	
133	Кладовая и моечная оборотной тары	4,0	
134	Заслужечный цех	6,6	
135	Кладовая сухих продуктов	3,7	
136	Помещение персонала с санузлом	6,5	
137	Помещение для временного хранения пищевых отходов	4,8	
138	ПМ	3,5	В4
139	Помещение подготовки блюд к реализации с участием кухонной посуды	29,3	В4
148	Танбур	2,2	
		216,9	